



COUPE TYPE SUR VIDANGE DE FOND

(1:200)

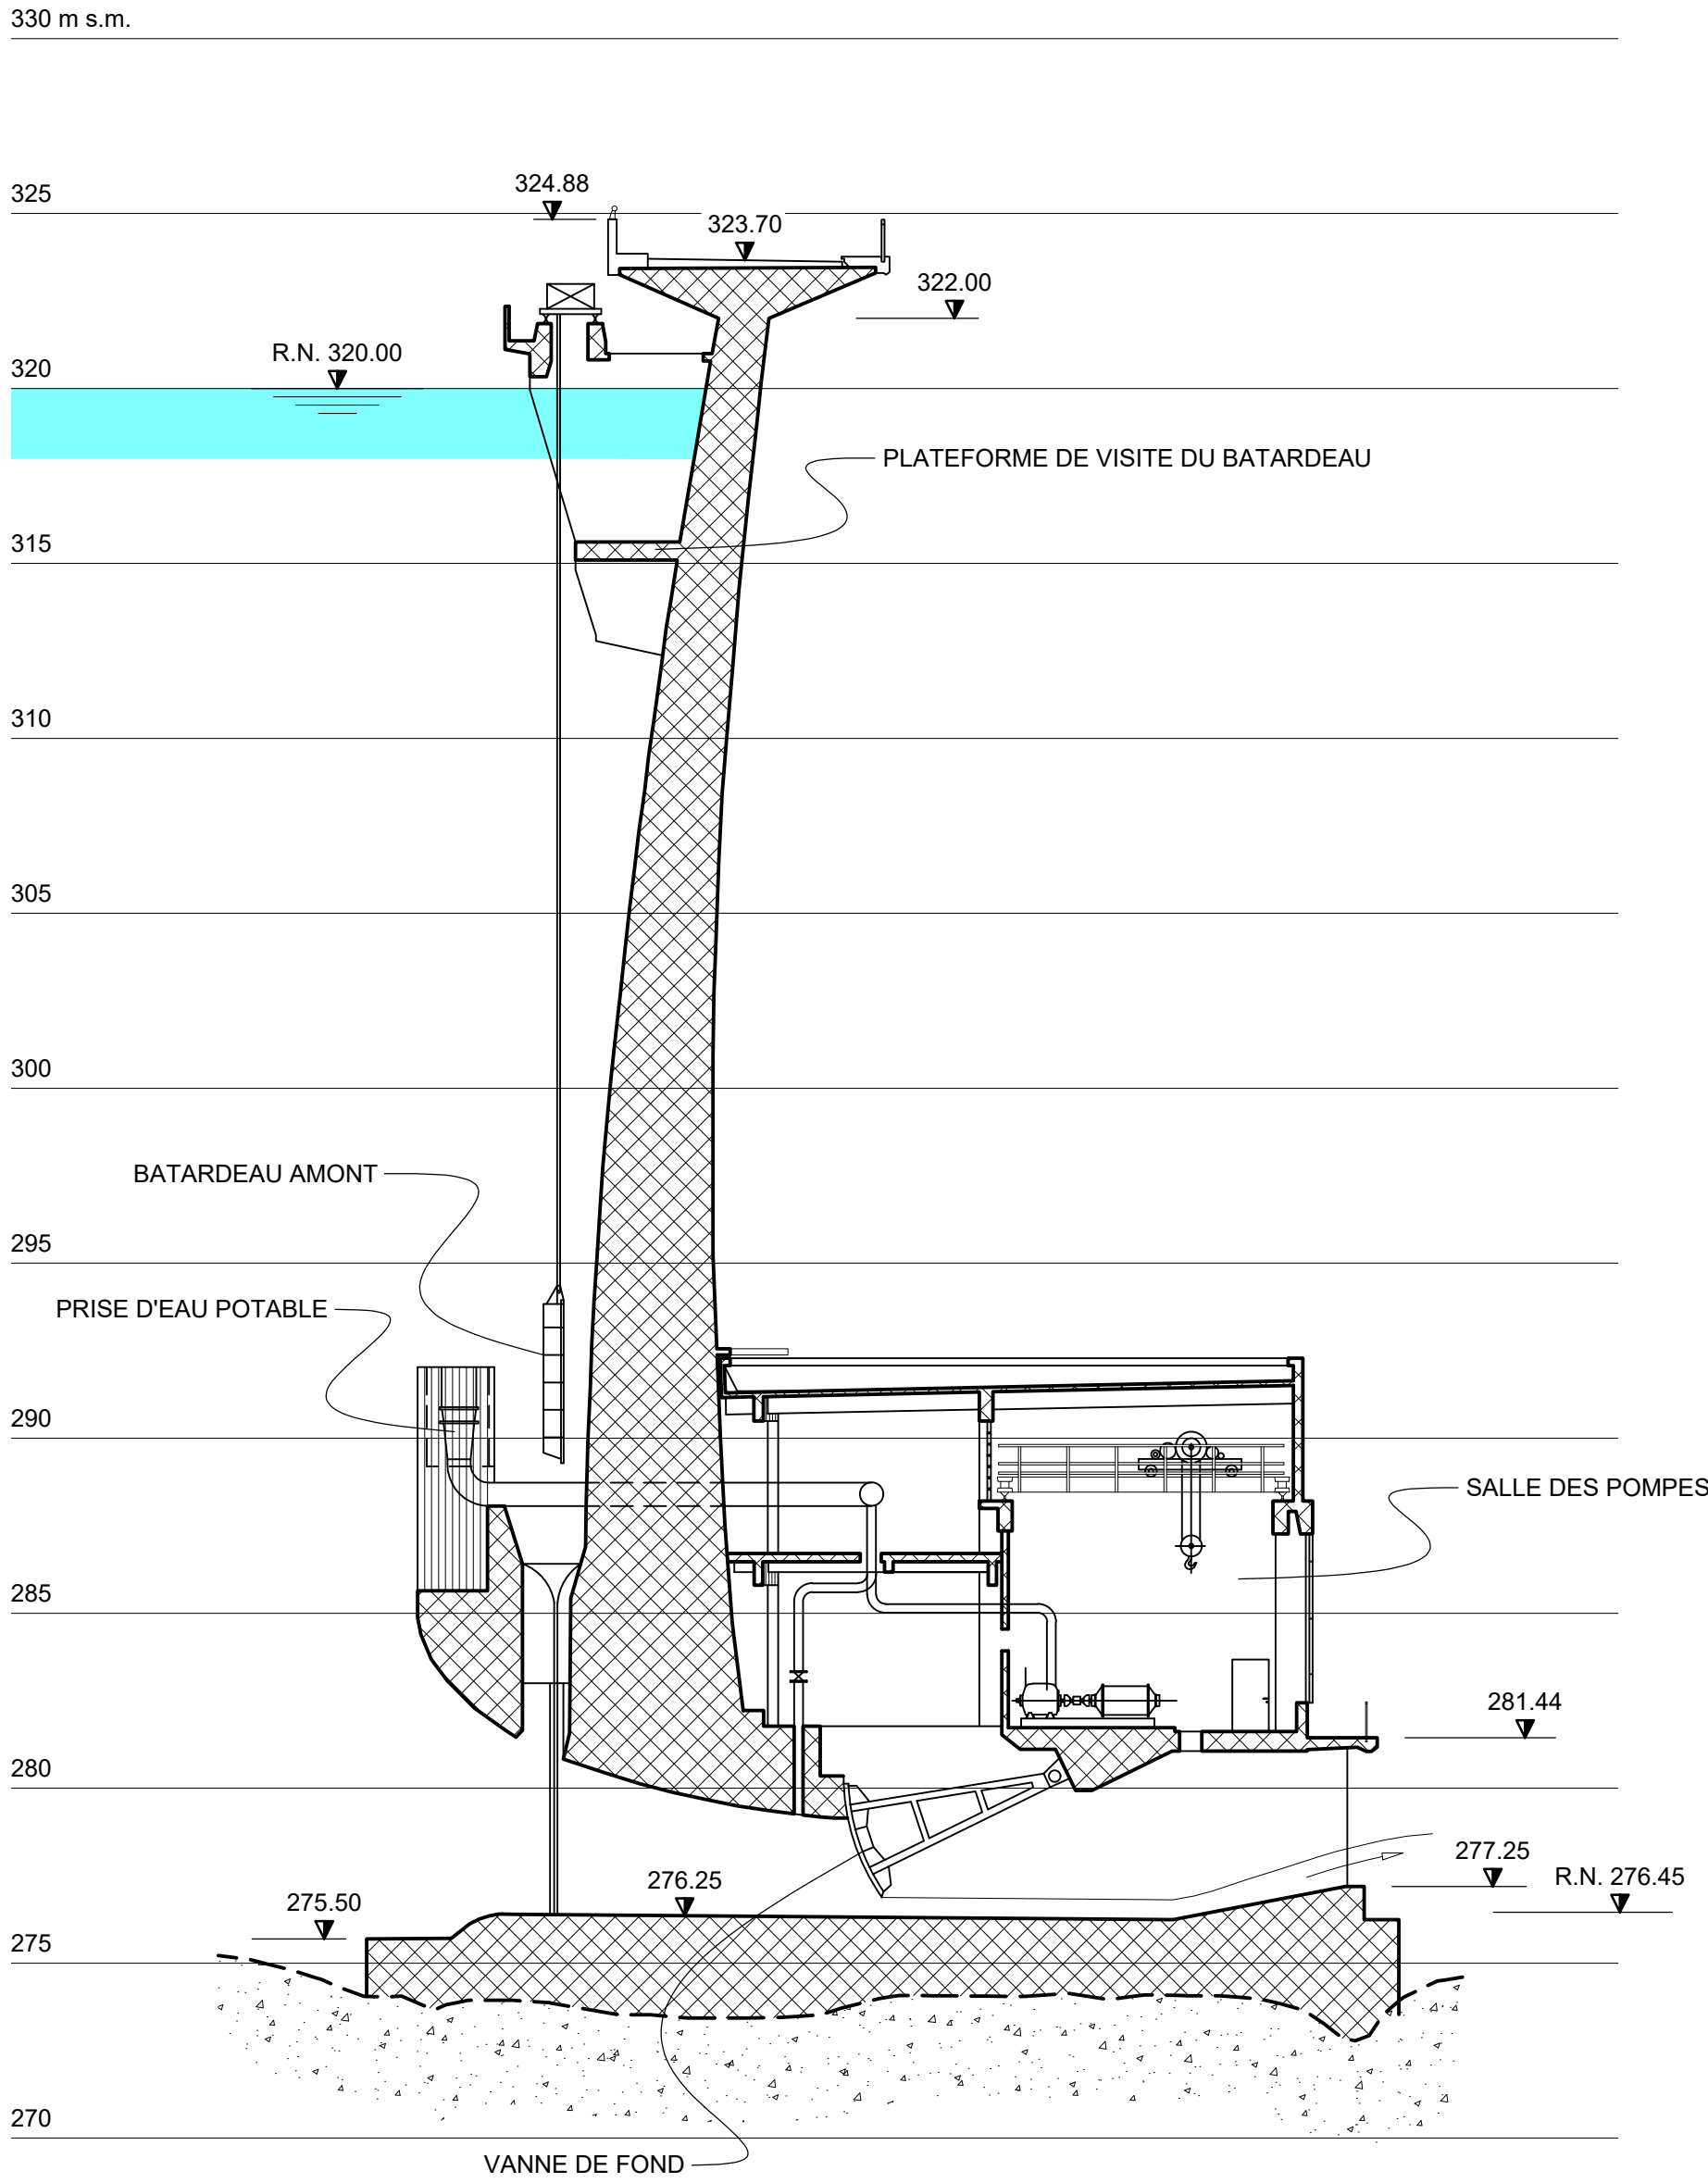

VOLUME UTILE DE LA RETENUE

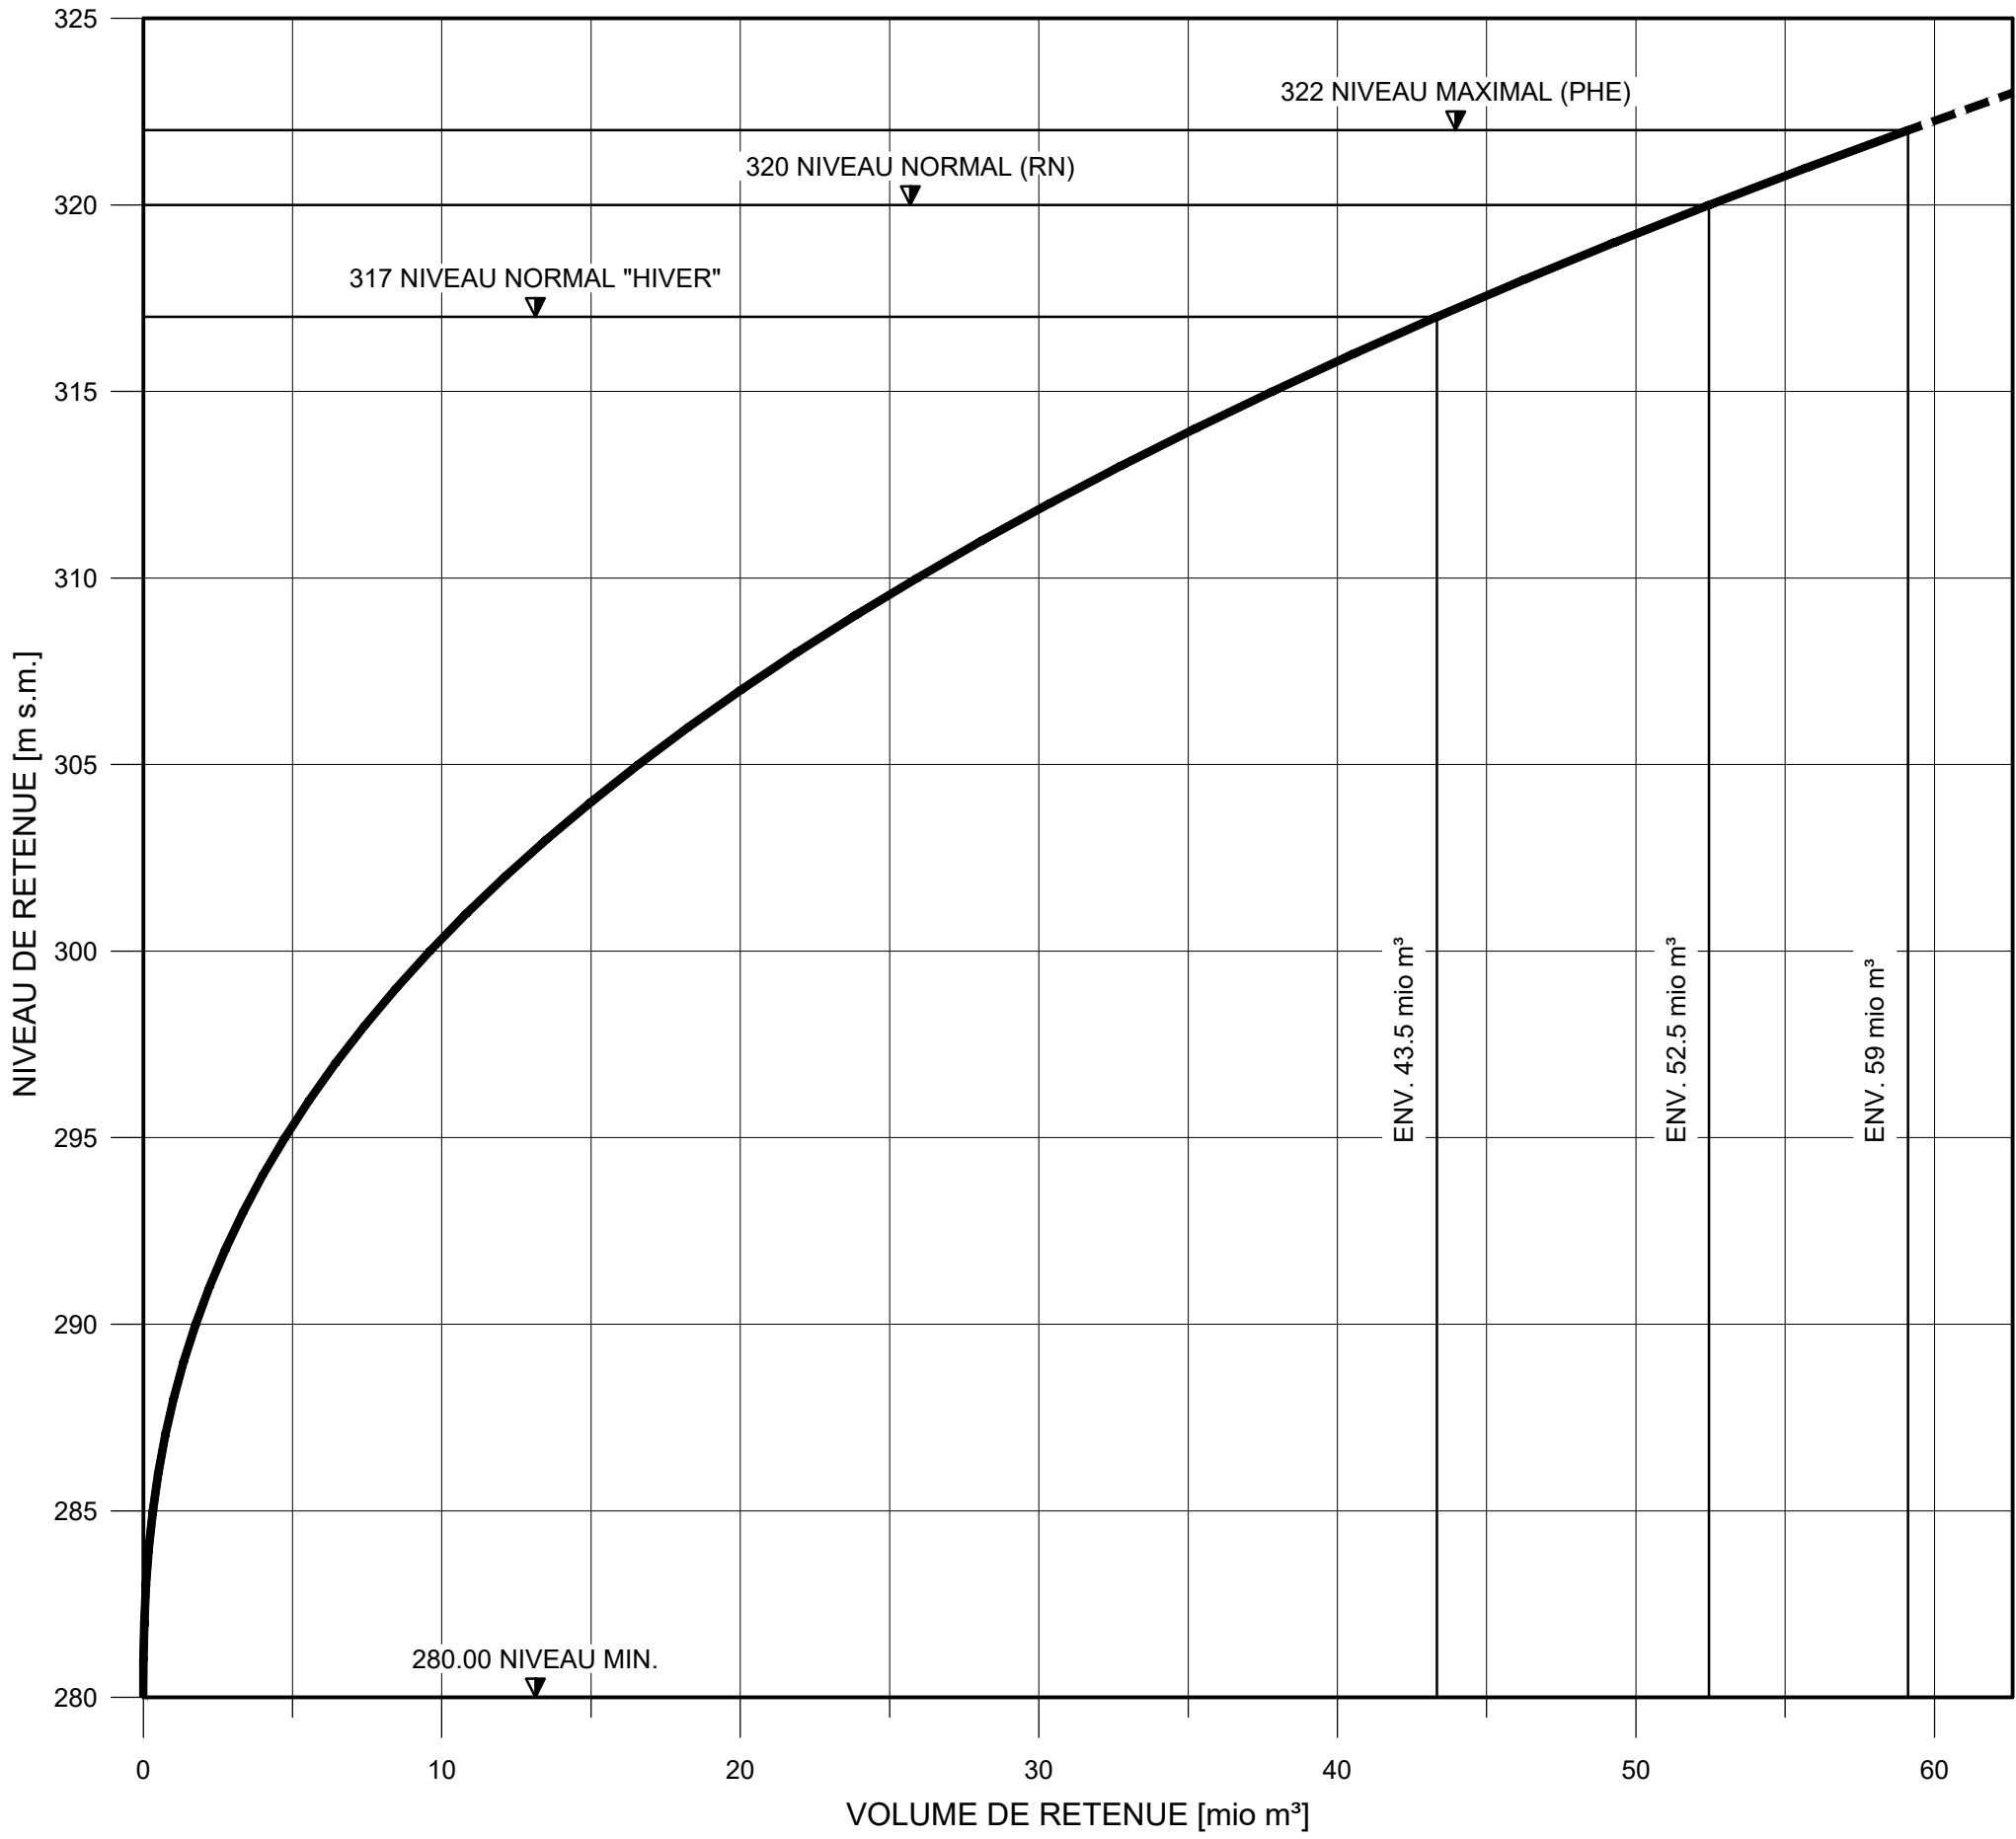


REFERENCE:

-SITUATION GENERALE, VOIR PLAN N.° 48925

ECHELLE GRAPHIQUE :

(1:200)

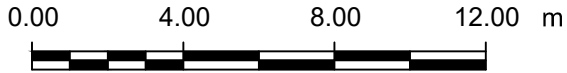

	LE GOUVERNEMENT DU GRAND-DUCHÉ DE LUXEMBOURG MINISTÈRE DE LA MOBILITÉ ET DES TRAVAUX PUBLICS ADMINISTRATION DES PONTS ET CHAUSSEES				
BARRAGE D'ESCH-SUR-SURE Evacuateur de crue complémentaire OA1158					
SOUSSION					
AMENAGEMENT EXISTANT COUPE TYPE DU BARRAGE					
Date:	Dess.	Verif.	Appr.	Description modification	C
					B
					A
05.06.2015	UP	Fel	BF	A1 (84 x 60)	7500.4-P-302
Date:	Dess.	Verif.	Appr.	Dim. :	Nom fichier
Echelle :	1:200	No. Lo :	7500.4-P-302	No.	48926