


PROFIL LONGITUDINAL

(1:500)

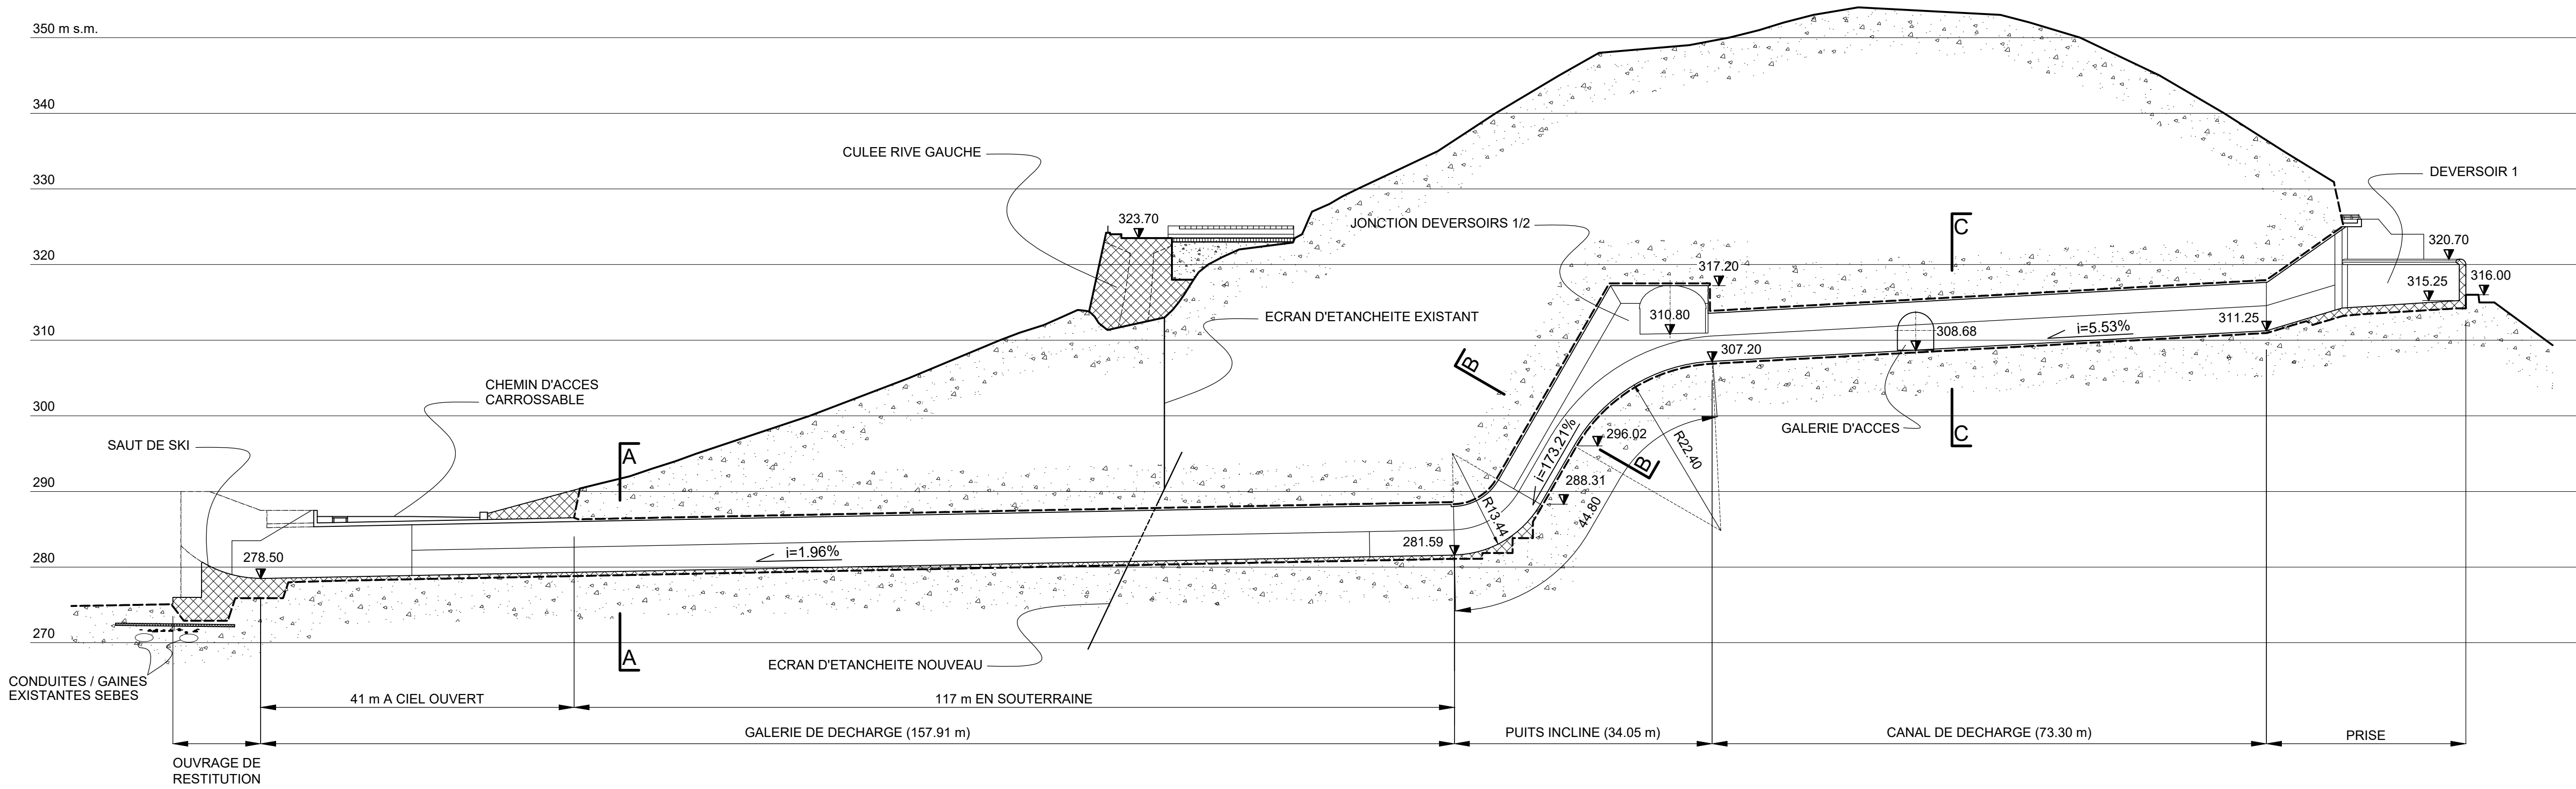

REFERENCES:


- AMENAGEMENT REHABILITE SITUATION GENERALE, VOIR PLAN N.° 48927
- TYPES SOUTÈNEMENT ET REVÈTEMENT DÉFINITIF, VOIR PLANS N.° 48936 ET 48944

NOTE:

- LES DIMENSIONS SUR LES COUPES SONT RÉFÉRÉES AU REVÈTEMENT (SOUTÈNEMENT VARIABLE EN FONCTION DE LA QUALITÉ DE LA ROCHE)
- BETON ARMÉ: C30/37
- BETON PROJETÉ: C25/30
- DRAINS: TUBE CREPINE
- ANCRAGES: CT BOLT 168 KN OU SWELLEX PM16 130 KN
- ECRAN D'ETANCHEITE RÉALISÉ SOUS FORME D'INJECTIONS RADIALES DEPUIS LA GALÉRIE


COUPE A-A - GALÉRIE DE DÉCHARGE

(1:100)

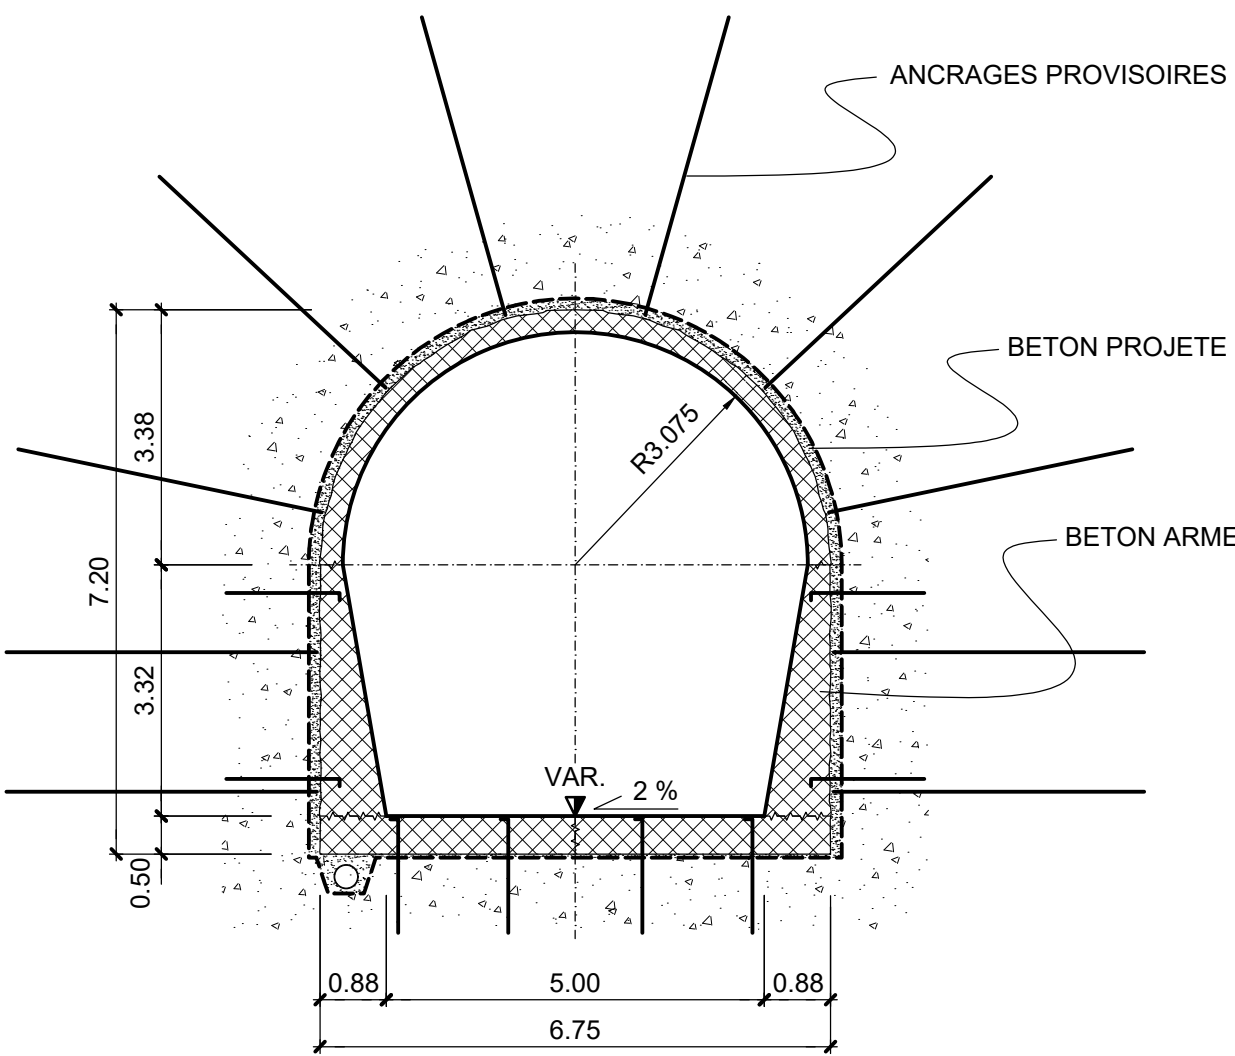


COUPE B-B - PUITS INCLINÉ

(1:100)

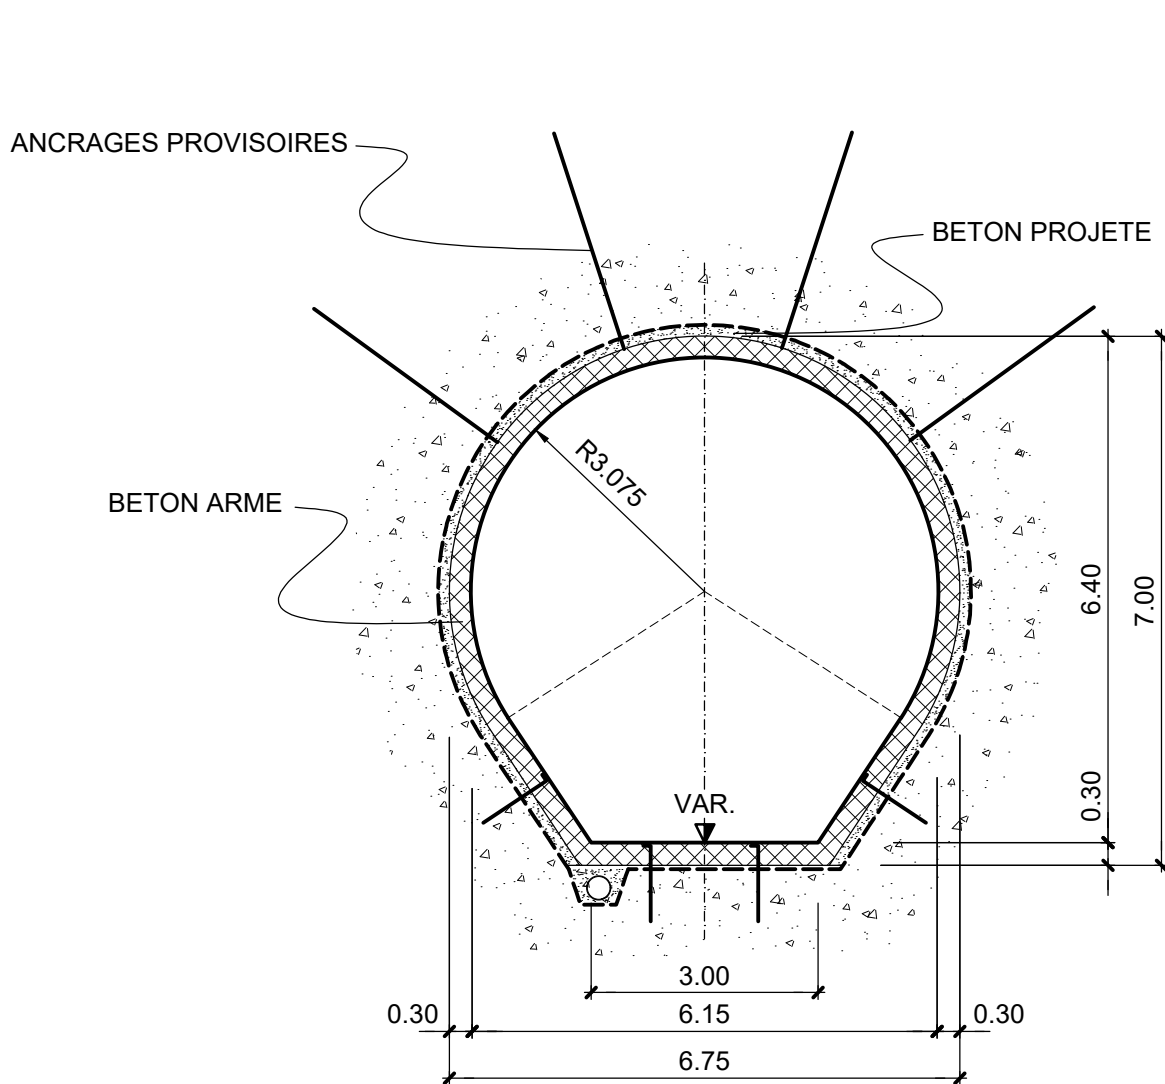

COUPE C-C - CANAL DE DÉCHARGE

(1:100)

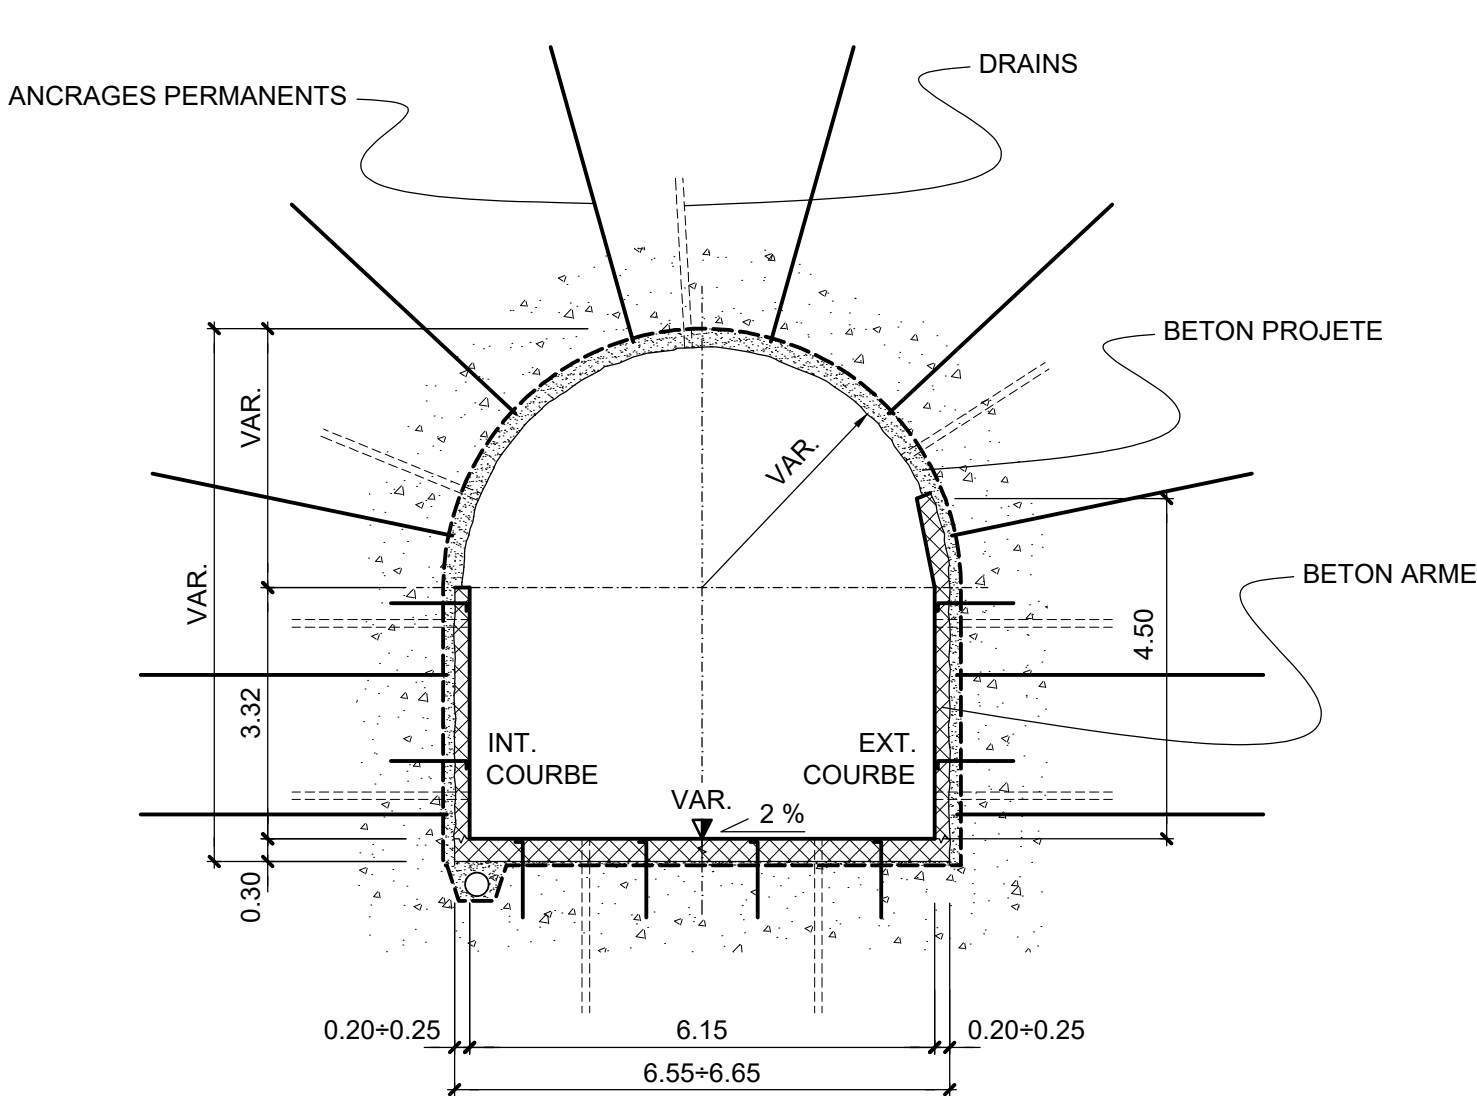

		LE GOUVERNEMENT DU GRAND-DUCHÉ DE LUXEMBOURG MINISTÈRE DE LA MOBILITÉ ET DES TRAVAUX PUBLICS ADMINISTRATION DES PONTS ET CHAUSSEES		 Lombardi	
BARRAGE D'ESCH-SUR-SURE Evacuateur de crue complémentaire OA1158					
SOUSSION					
AMENAGEMENT REHABILITE PROFIL LONGITUDINAL ET COUPES GENERALES					
					C
19.08.2019	LME	MID	MID	Actualisation SEBES	B
23.05.18	MID	Fel	La	Modifications mineures	A
Date:	Dess.	Verif.	Appr.	Description modification	
05.06.2015	UP	Fel	BF	A1 (84 x 60)	7500.4-P-306B
Date:	Dess.	Verif.	Appr.	Dim. :	Nom fichier
Echelle : 1:500, 1:100			No. Lo : 7500.4-P-306B	No.	48928
					B