



PROFIL LONGITUDINAL

(1:250)

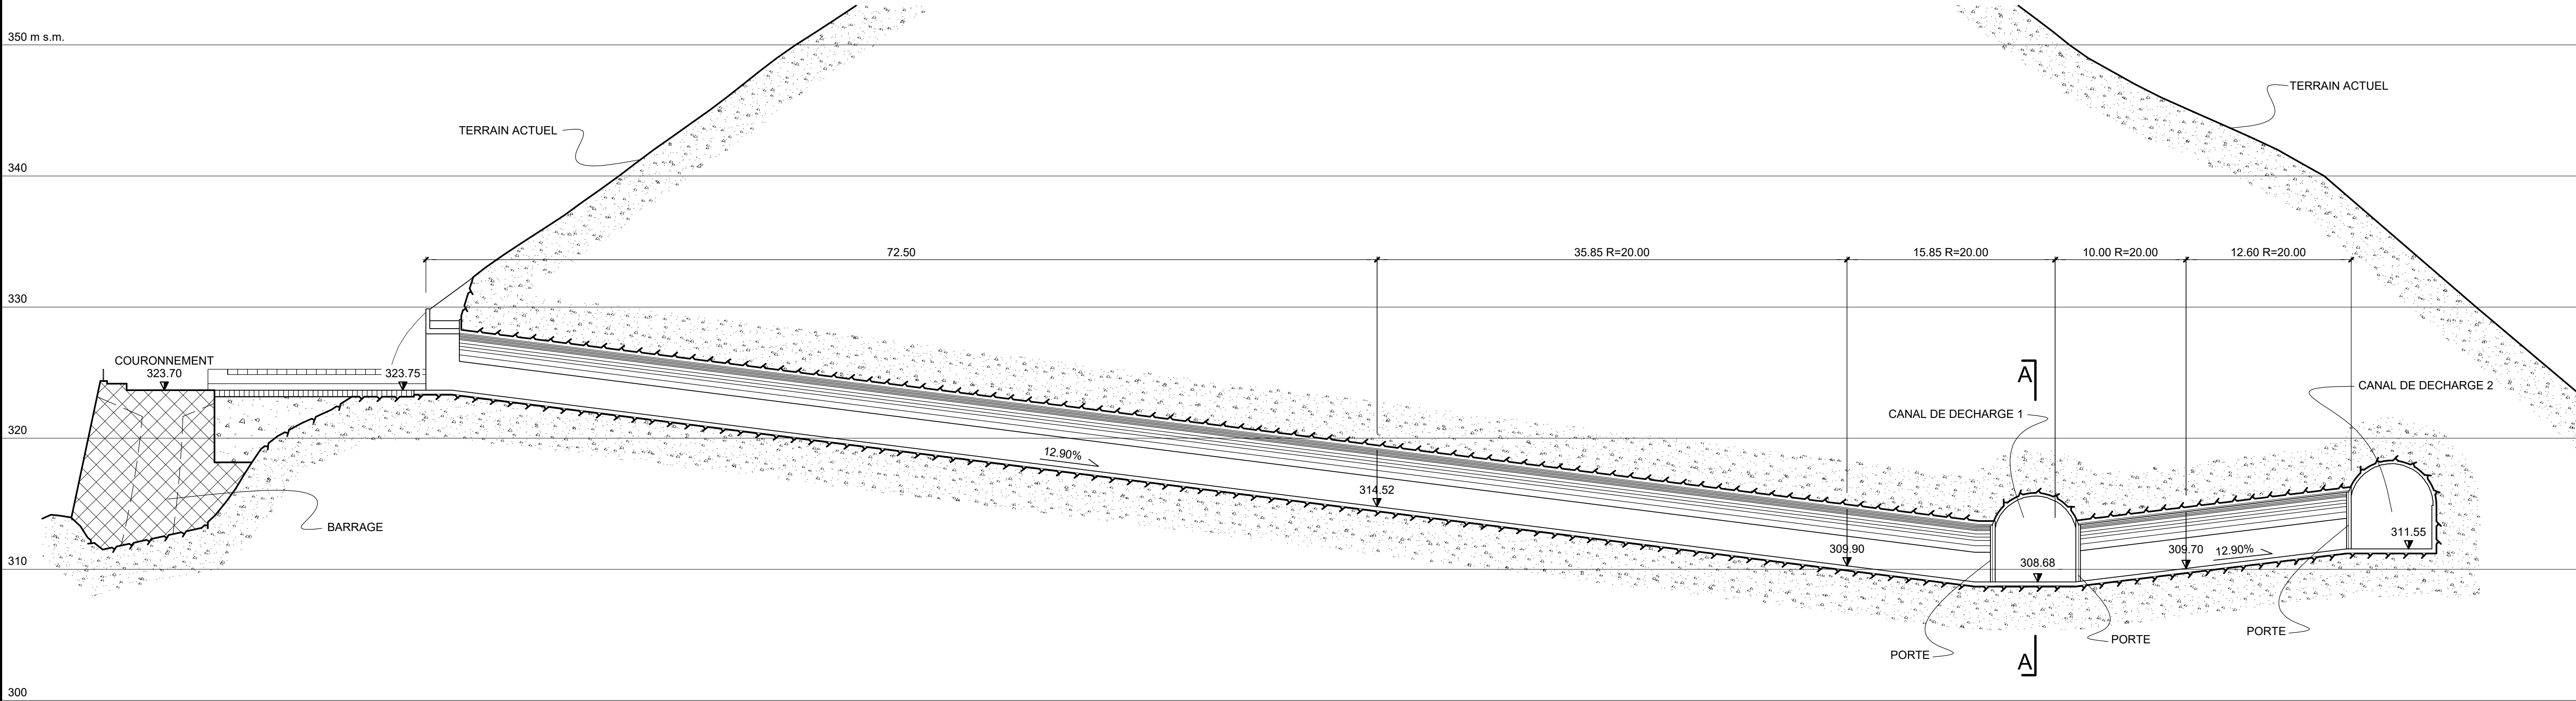


COUPE A-A

(1:100)

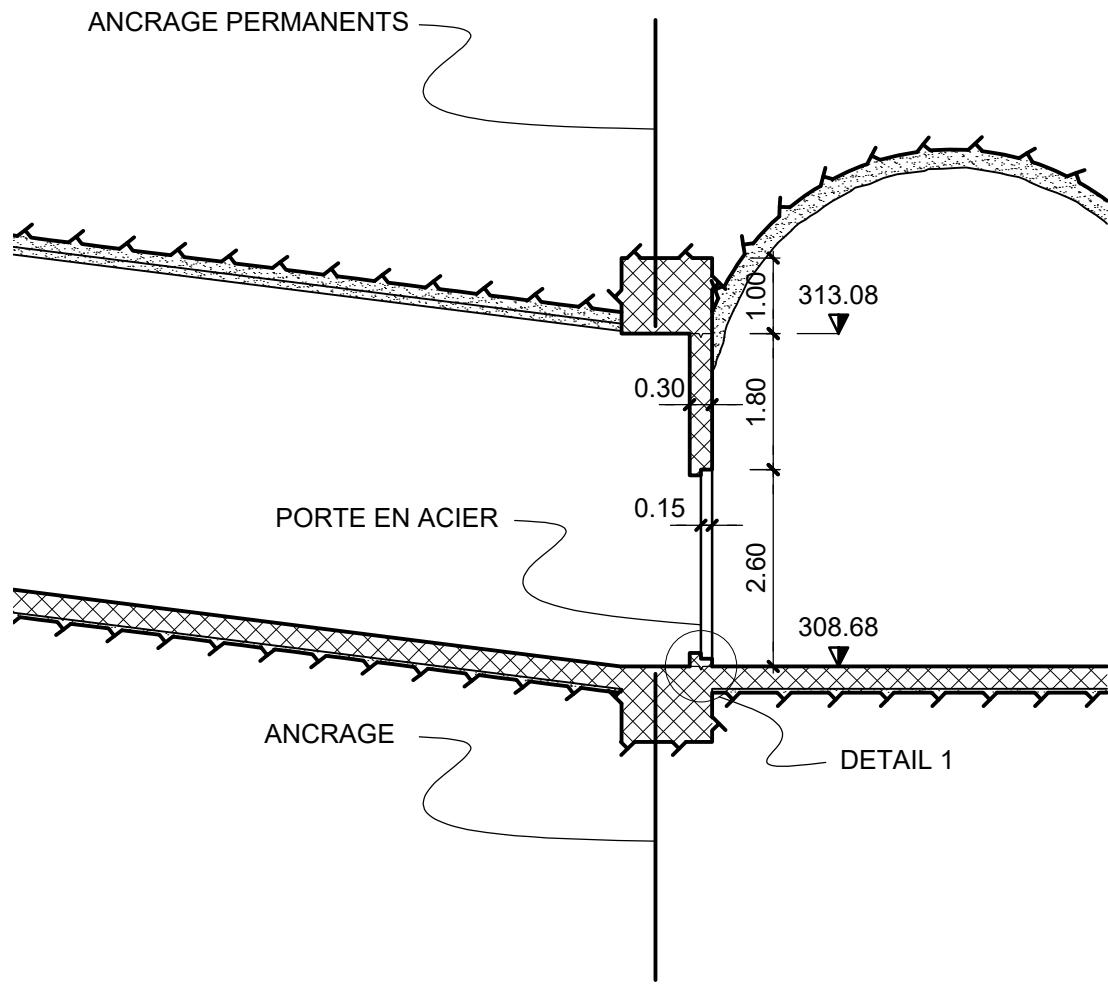


COUPE TYPE GALERIE D'ACCES

(1:50)

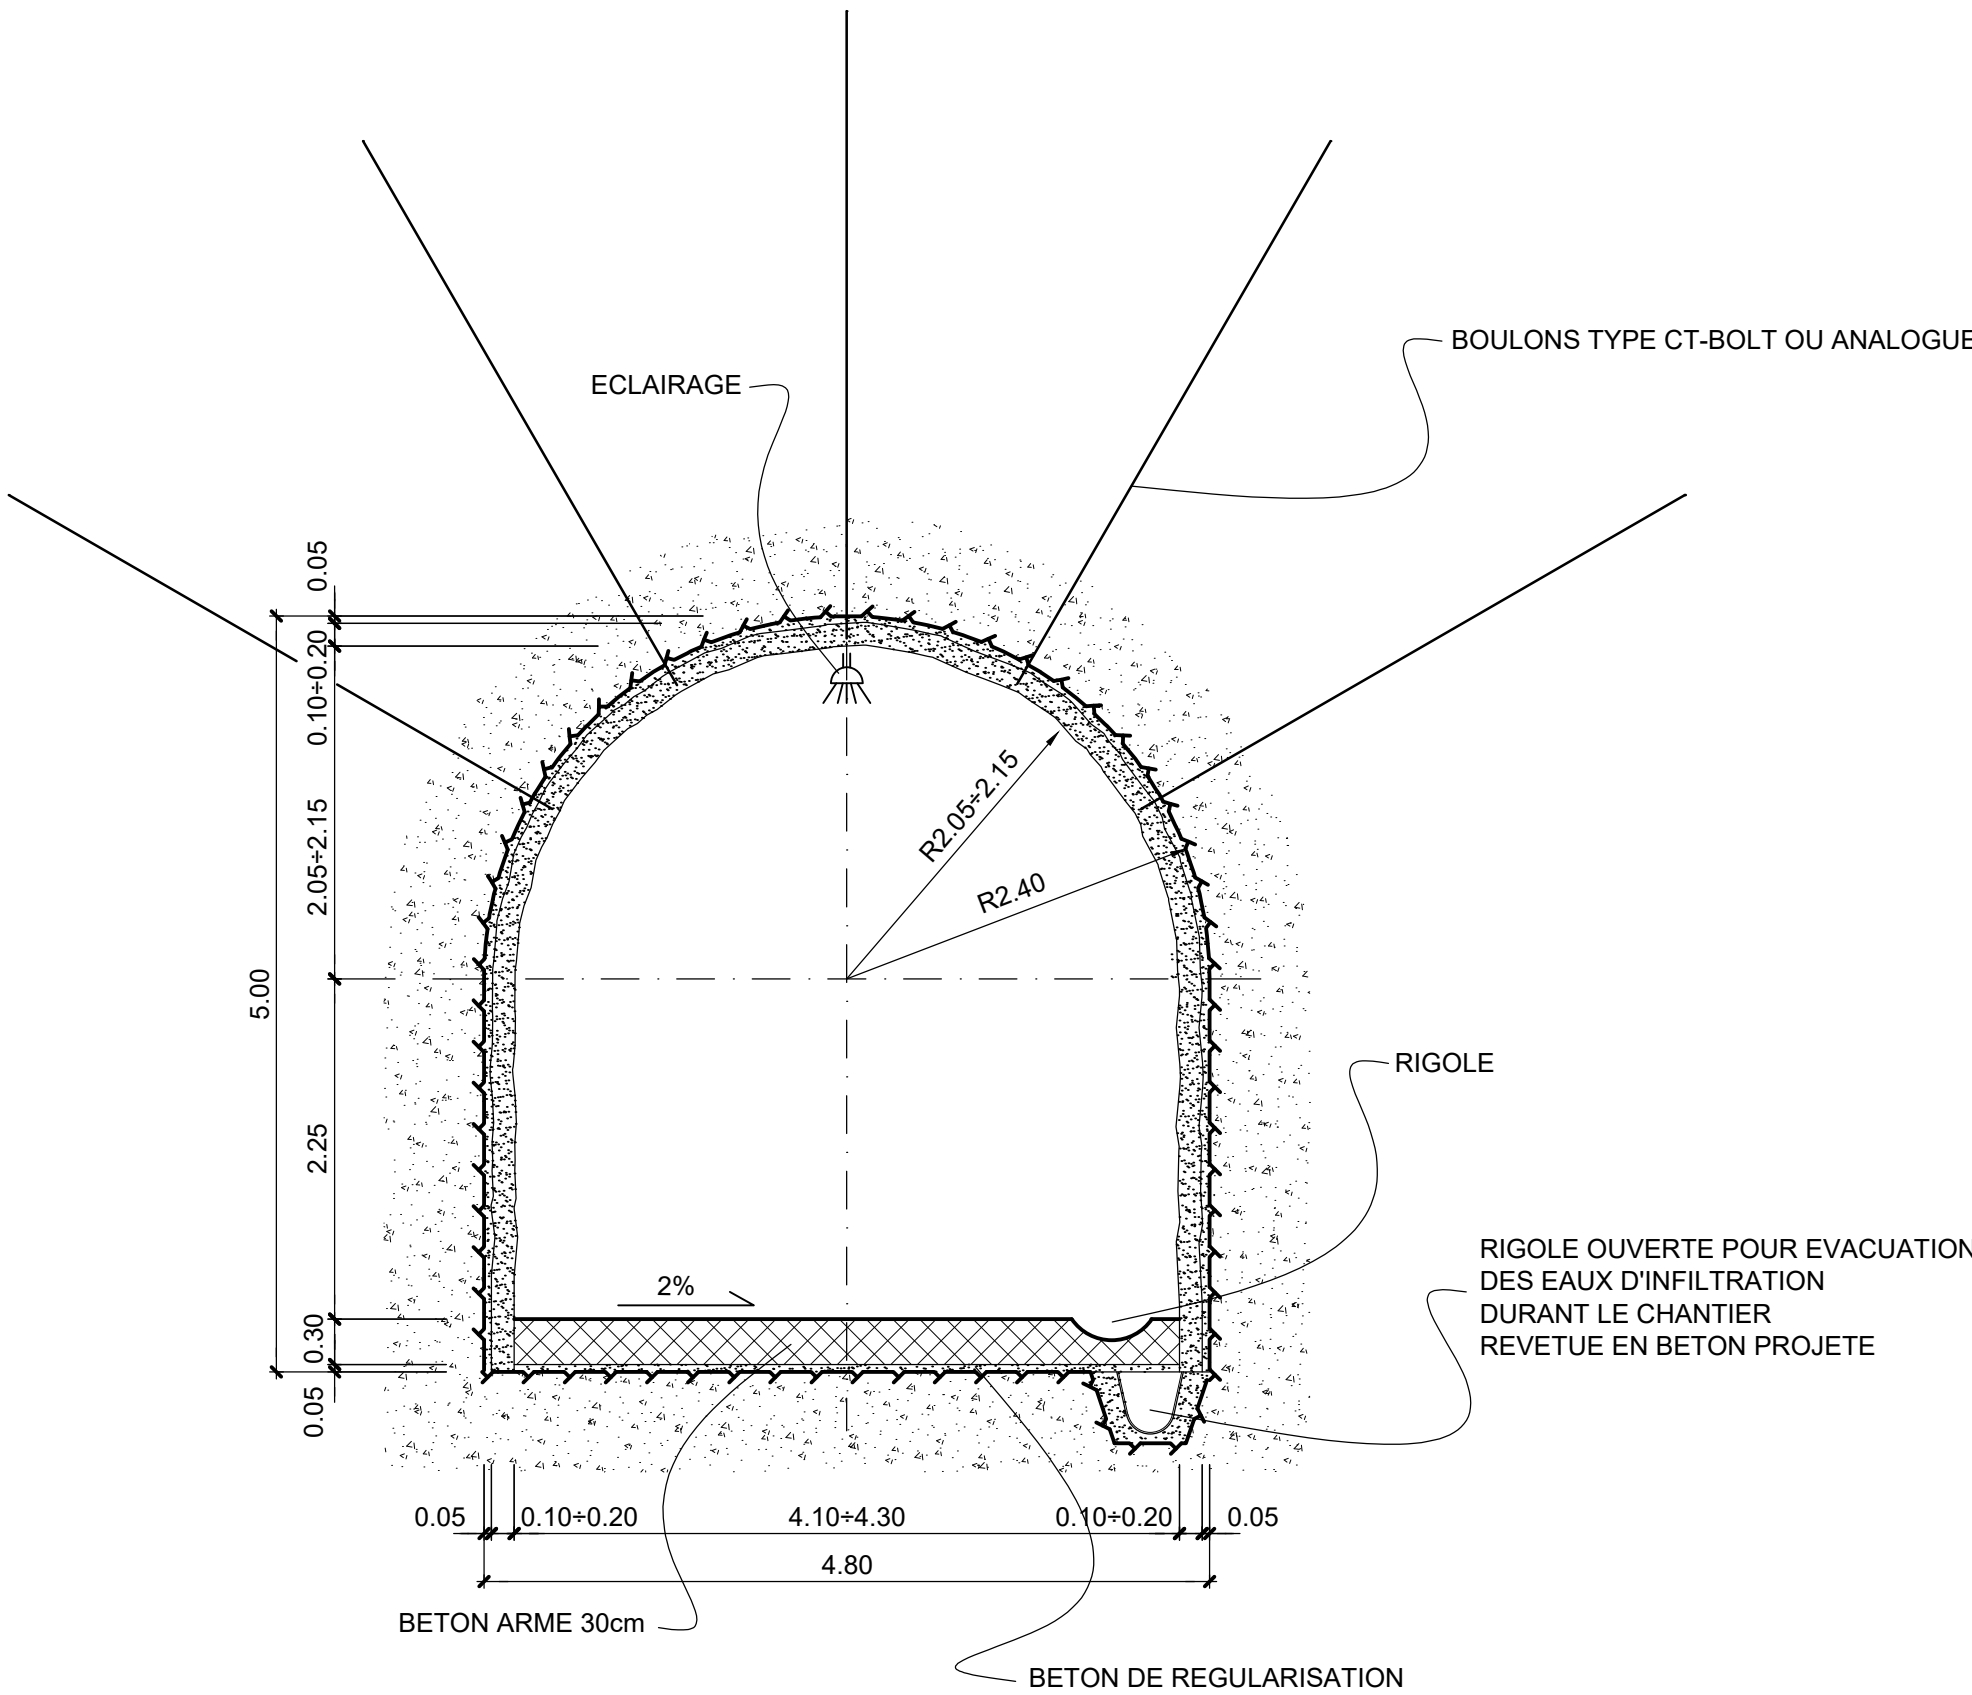


DETAIL 1

(1:10)

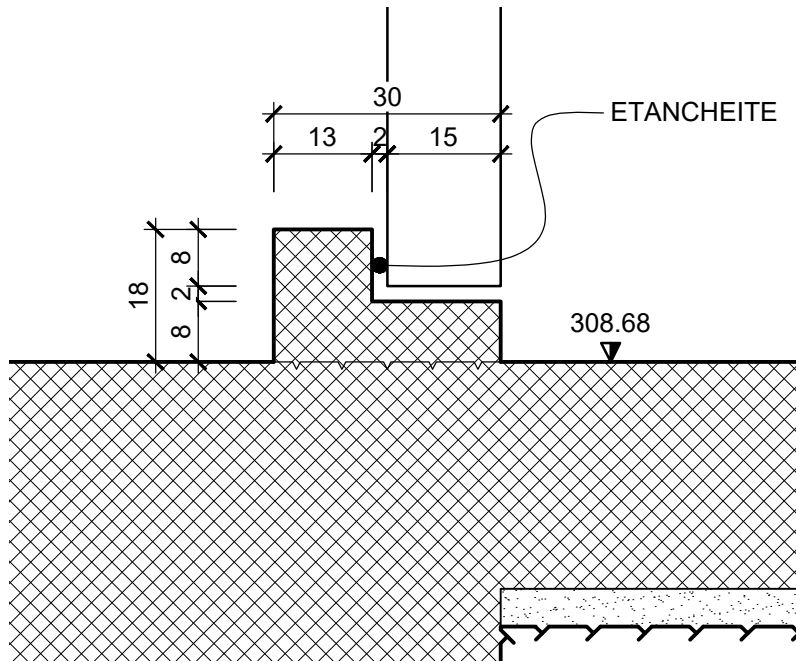


SITUATION DETAIL 1

(1:10)

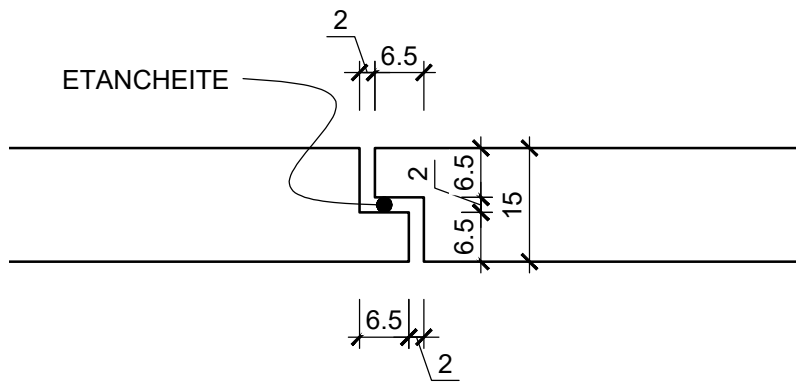

SITUATION

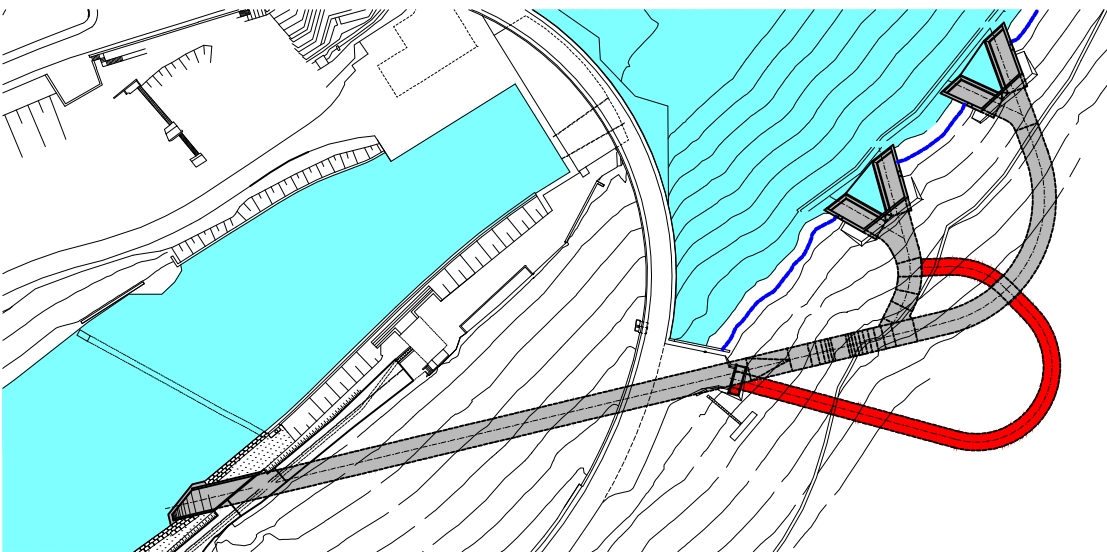


REFERENCE:

-TRONCON AMONT - SITUATION GENERALE, VOIR PLAN N.° 48930

NOTE:

- BETON DE REGULARISATION:
- BETON ARME: C30/37
- BOULONS: CT BOLT 168 KN
- LA RIGOLE SERA COMBLEE A LA FIN DES TRAVAUX
- LE BOULONNAGE POURRA ETRE ADAPTE AU FUR ET A MESURE DU COMPORTEMENT DU ROCHER

ECHELLES GRAPHIQUES :

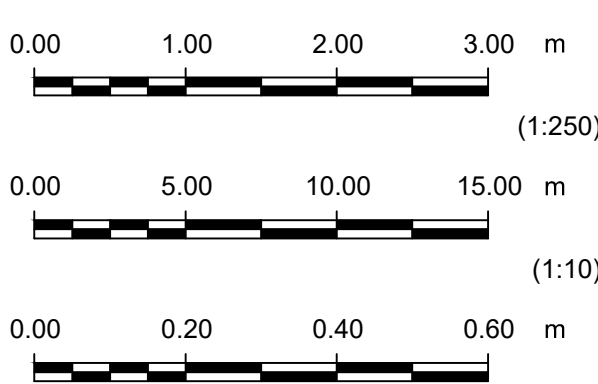

		LE GOUVERNEMENT DU GRAND-DUCHÉ DE LUXEMBOURG MINISTÈRE DE LA MOBILITÉ ET DES TRAVAUX PUBLICS ADMINISTRATION DES PONTS ET CHAUSSEES			
BARRAGE D'ESCH-SUR-SURE Evacuateur de crue complémentaire OA1158					
SOUSSION					
GALERIE D'ACCES PROFIL LONGITUDINAL ET COUPE TYPE					
Date:	Dess.	Verif.	Appr.	Description modification	
05.06.2015	UP	Fel	BF	A1 (84 x 60)	7500.4-P-311
Date:	Dess.	Verif.	Appr.	Dim. :	Nom fichier
Echelle :	1:250, 1:50, 1:10	No. Lo :	7500.4-P-311	No.	48931