




COUPE TYPE GALERIE DE DECHARGE (A-A)

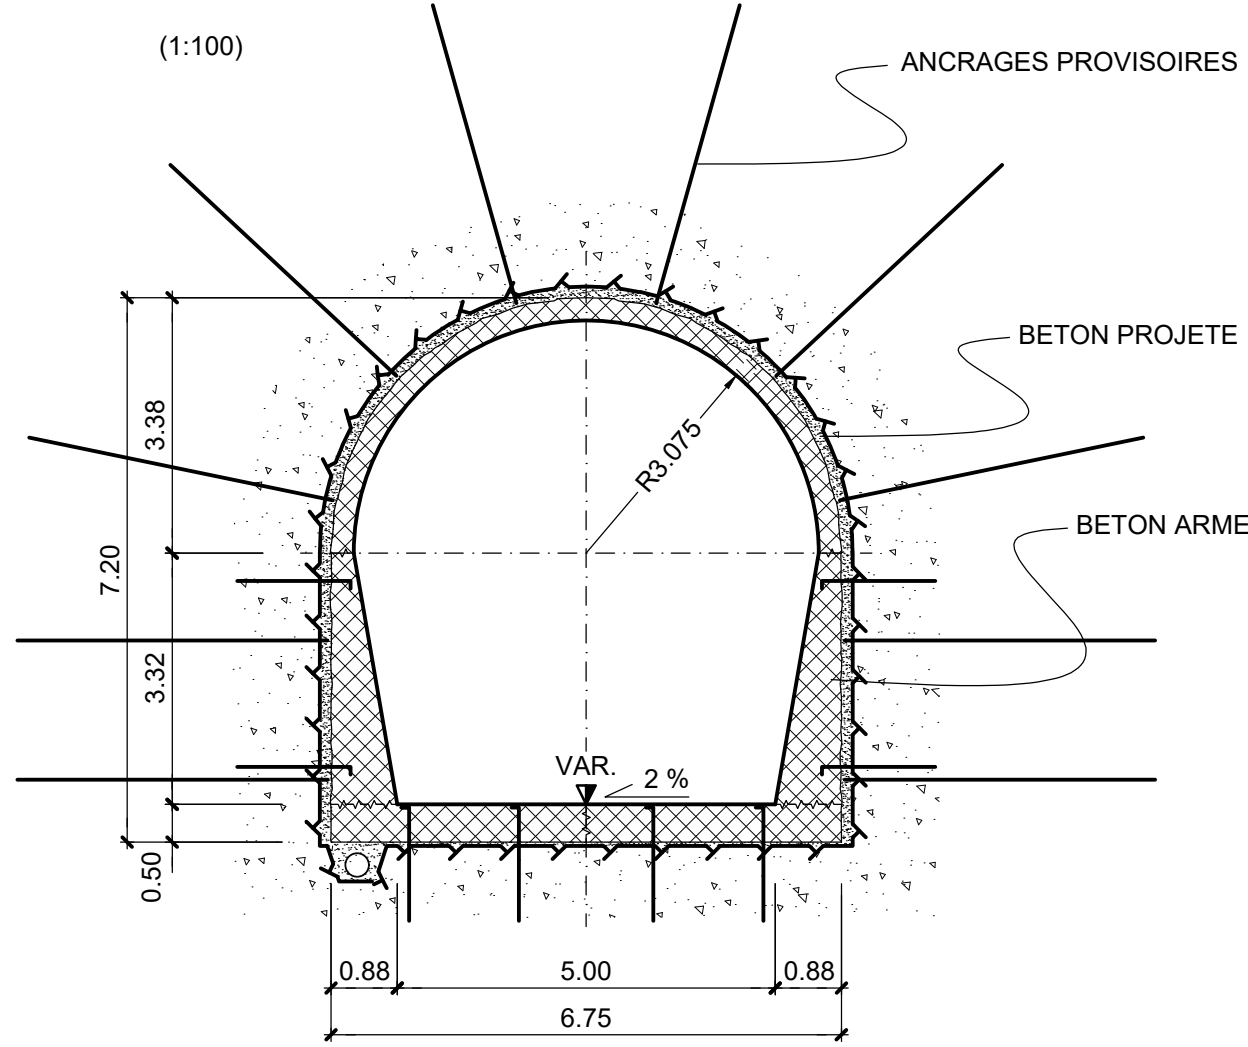


COUPE TYPE PUIITS INCLINE (B-B)

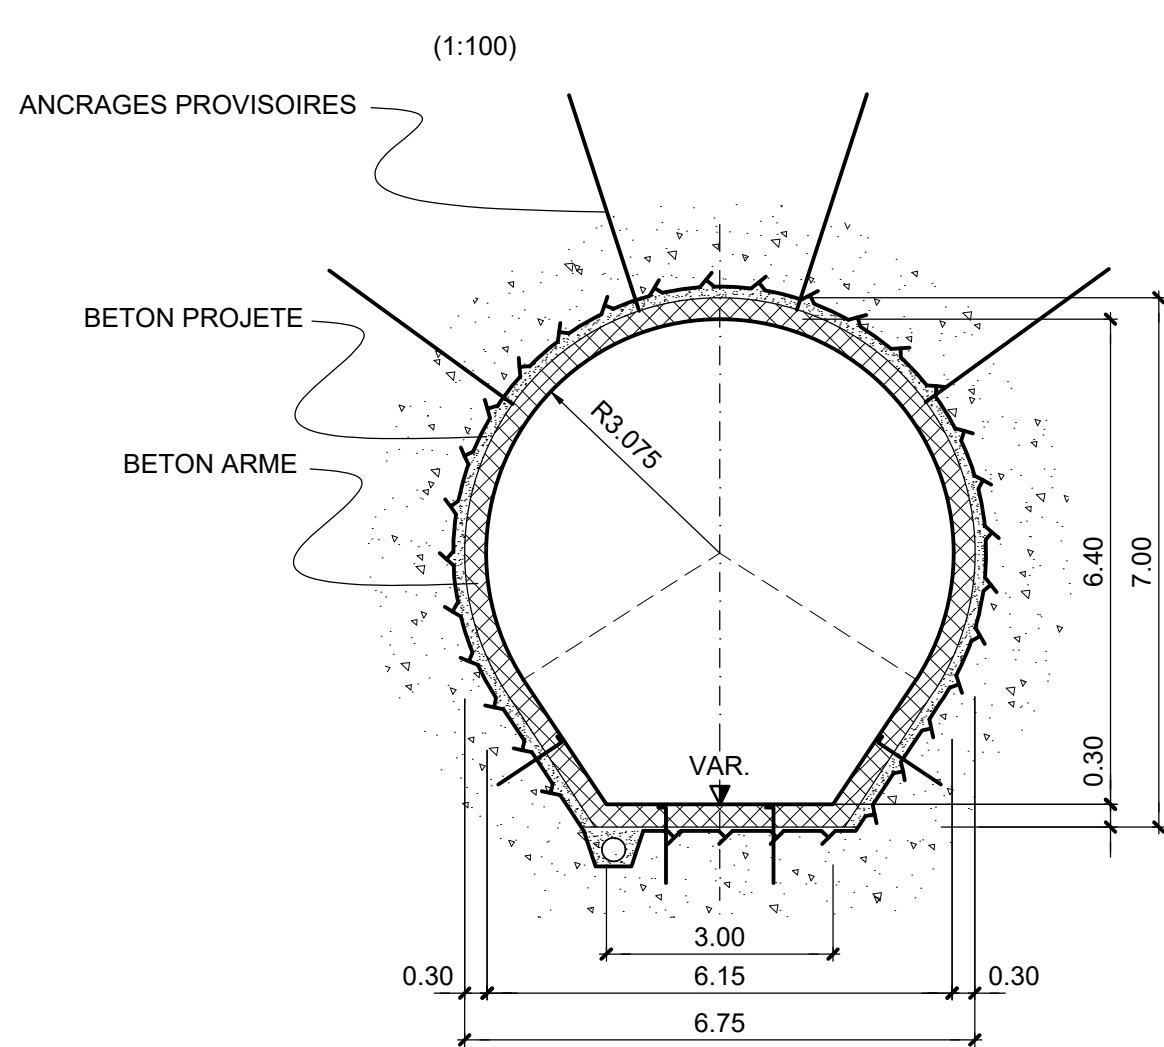

COUPE TYPE INTERSECTION
CANAL DE DECHARGE ET PUIITS INCLINE (C-C)

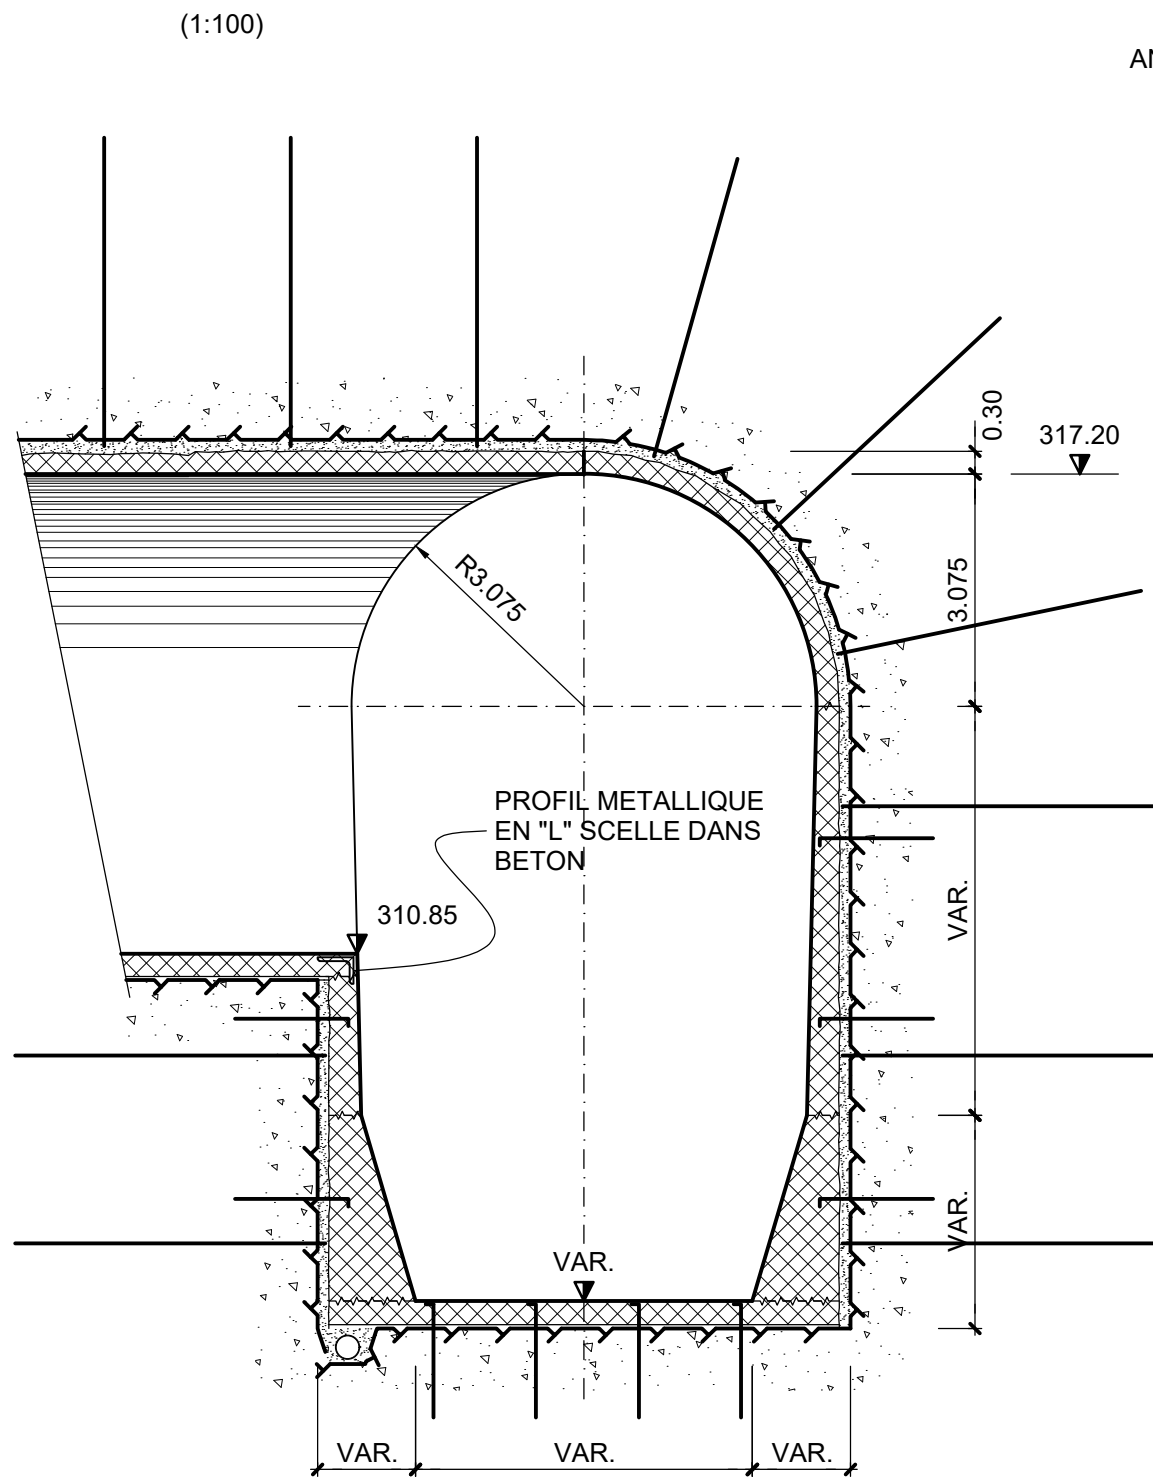



COUPE TYPE CANAL DE DECHARGE (D-D)

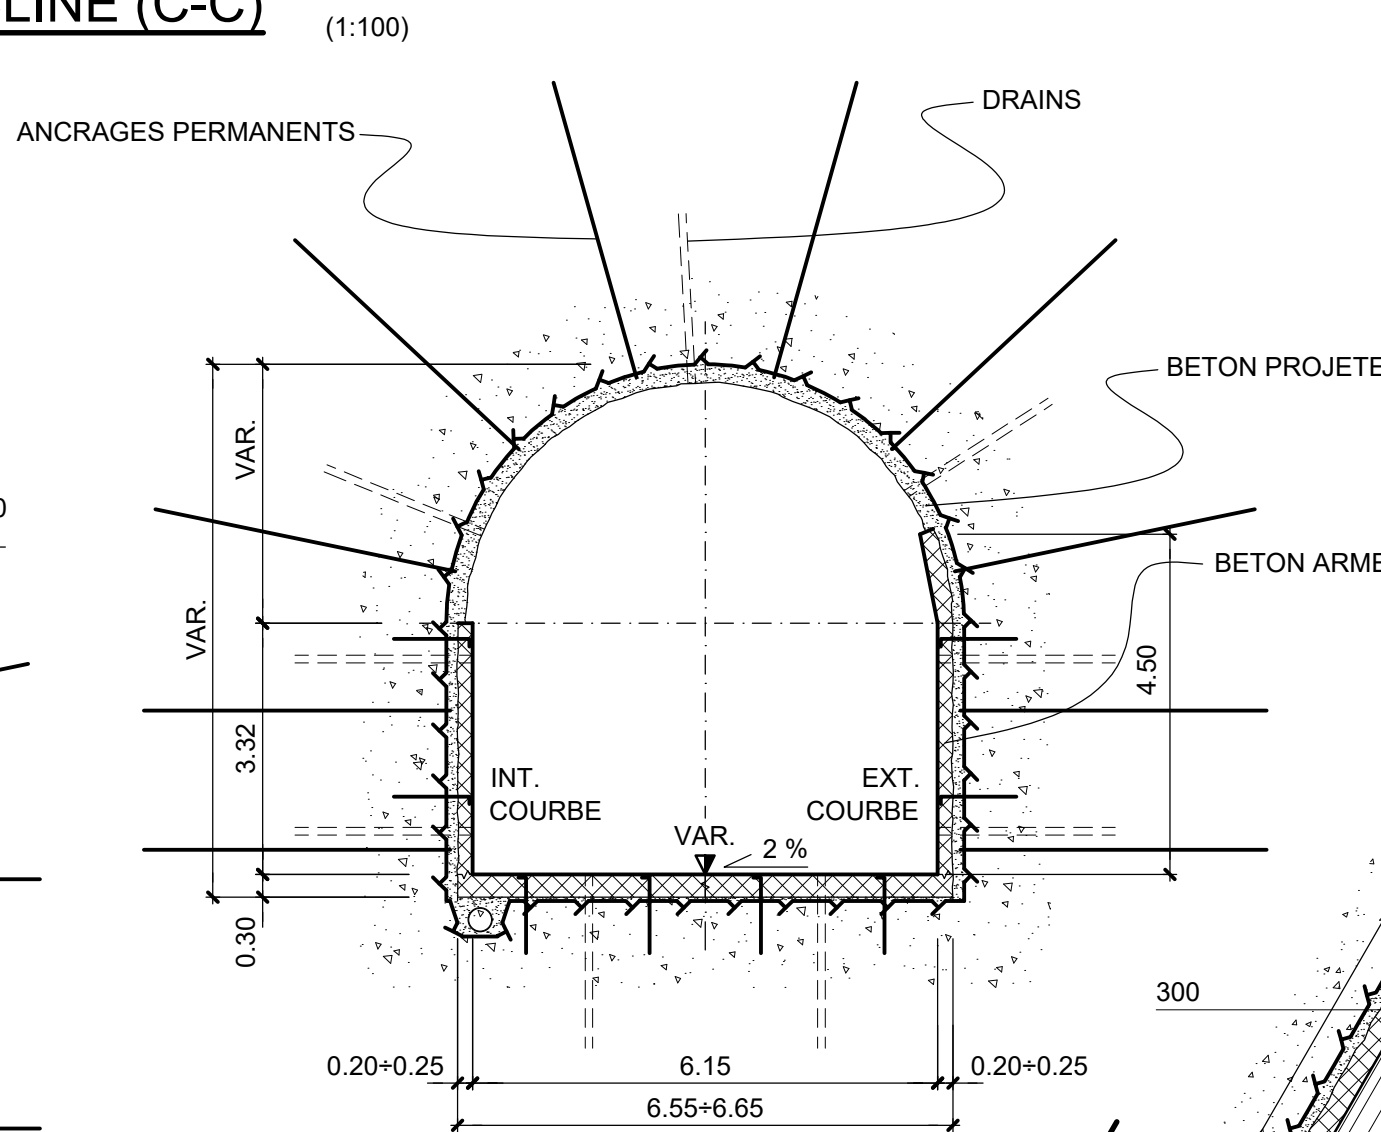

PUITS INCLINE PROFIL LONGITUDINAL

(1:100)

SITUATION

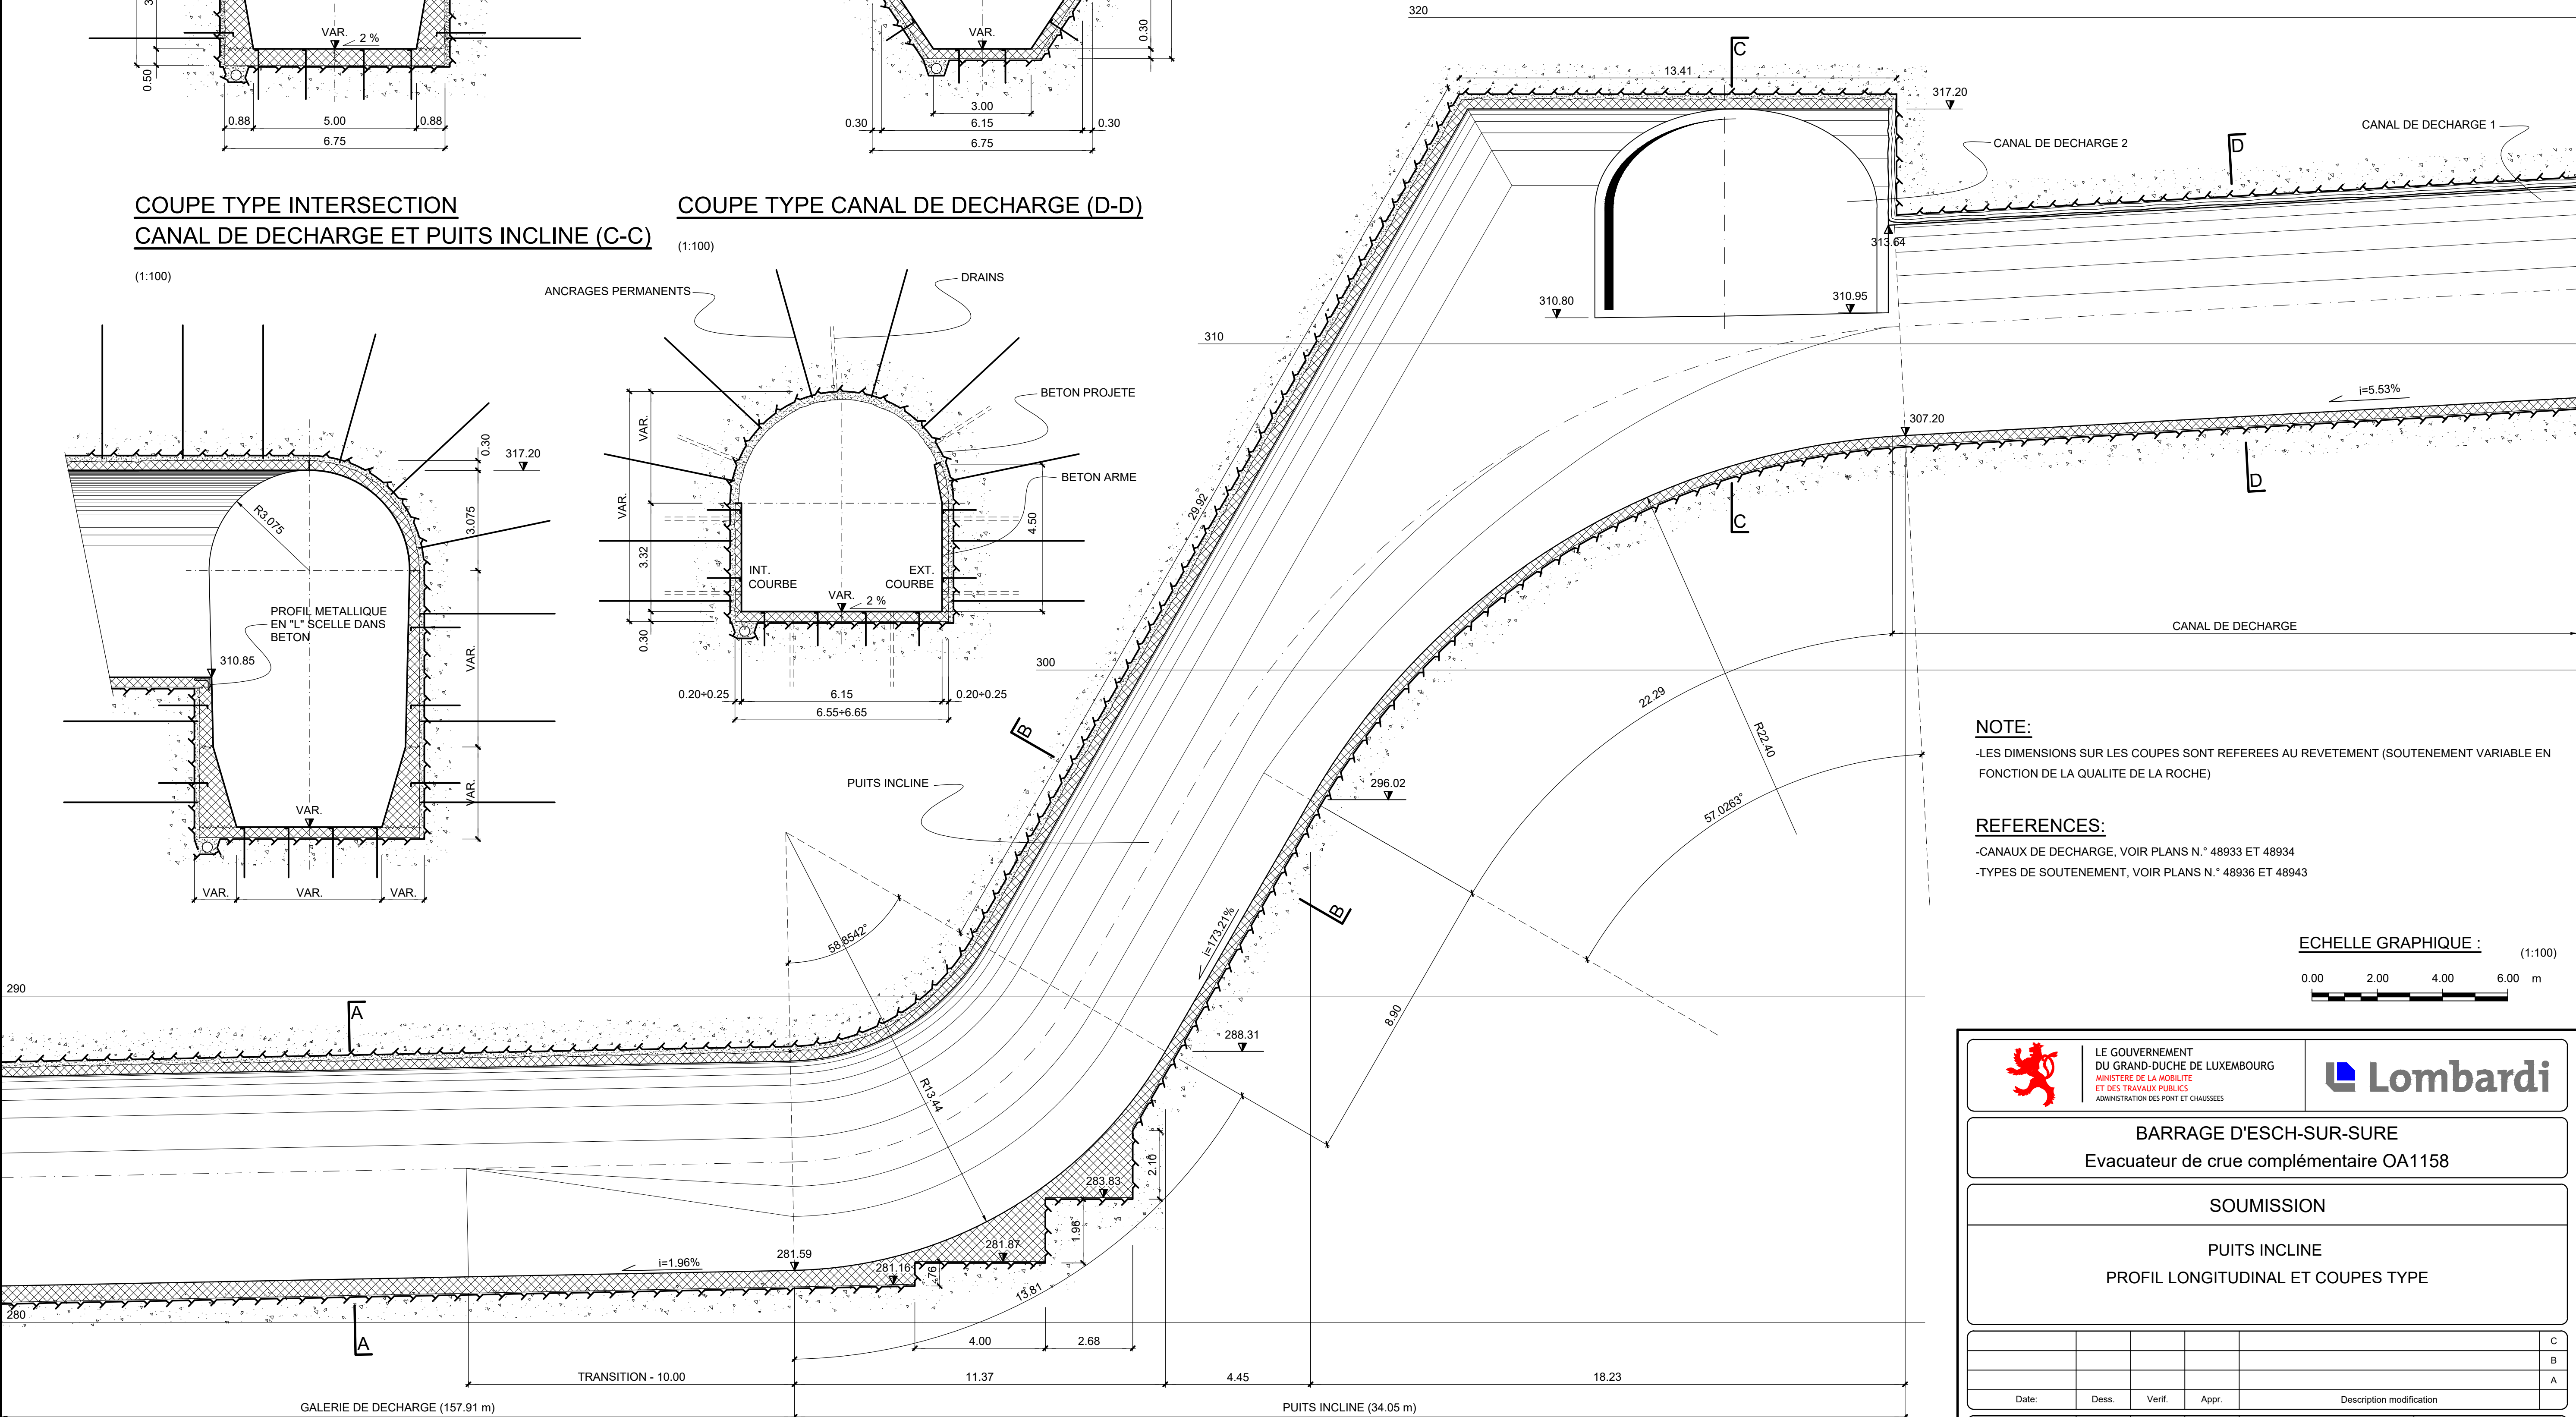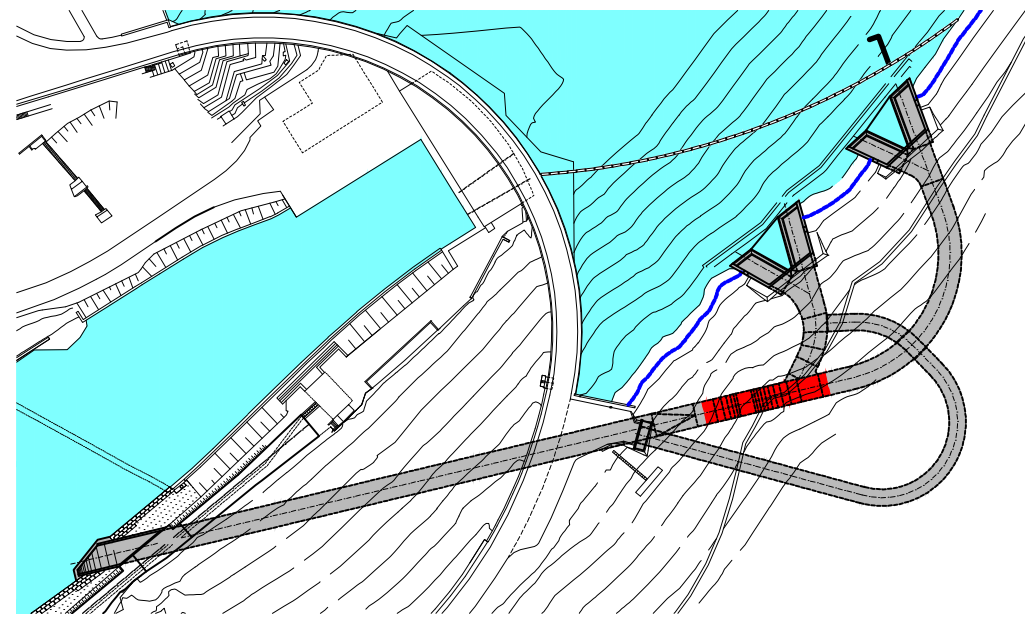

NOTE:

-LES DIMENSIONS SUR LES COUPES SONT REFEREES AU REVETEMENT (SOUTENEMENT VARIABLE EN FONCTION DE LA QUALITE DE LA ROCHE)

REFERENCES:

-CANAUX DE DECHARGE, VOIR PLANS N.° 48933 ET 48934
-TYPES DE SOUTENEMENT, VOIR PLANS N.° 48936 ET 48943

ECHELLE GRAPHIQUE :



	LE GOUVERNEMENT DU GRAND-DUCHÉ DE LUXEMBOURG MINISTÈRE DE LA MOBILITÉ ET DES TRAVAUX PUBLICS ADMINISTRATION DES PONTS ET CHAUSSEES	
BARRAGE D'ESCH-SUR-SURE Evacuateur de crue complémentaire OA1158		
SOUSSION		
PUITS INCLINE PROFIL LONGITUDINAL ET COUPES TYPE		
Date:	Dess.	Verif.
Date:	Dess.	Verif.
UP		BF
Dim. :		7500.4-314
No. Lo :		7500.4-314
No.		48935