


ROCHE BONNE

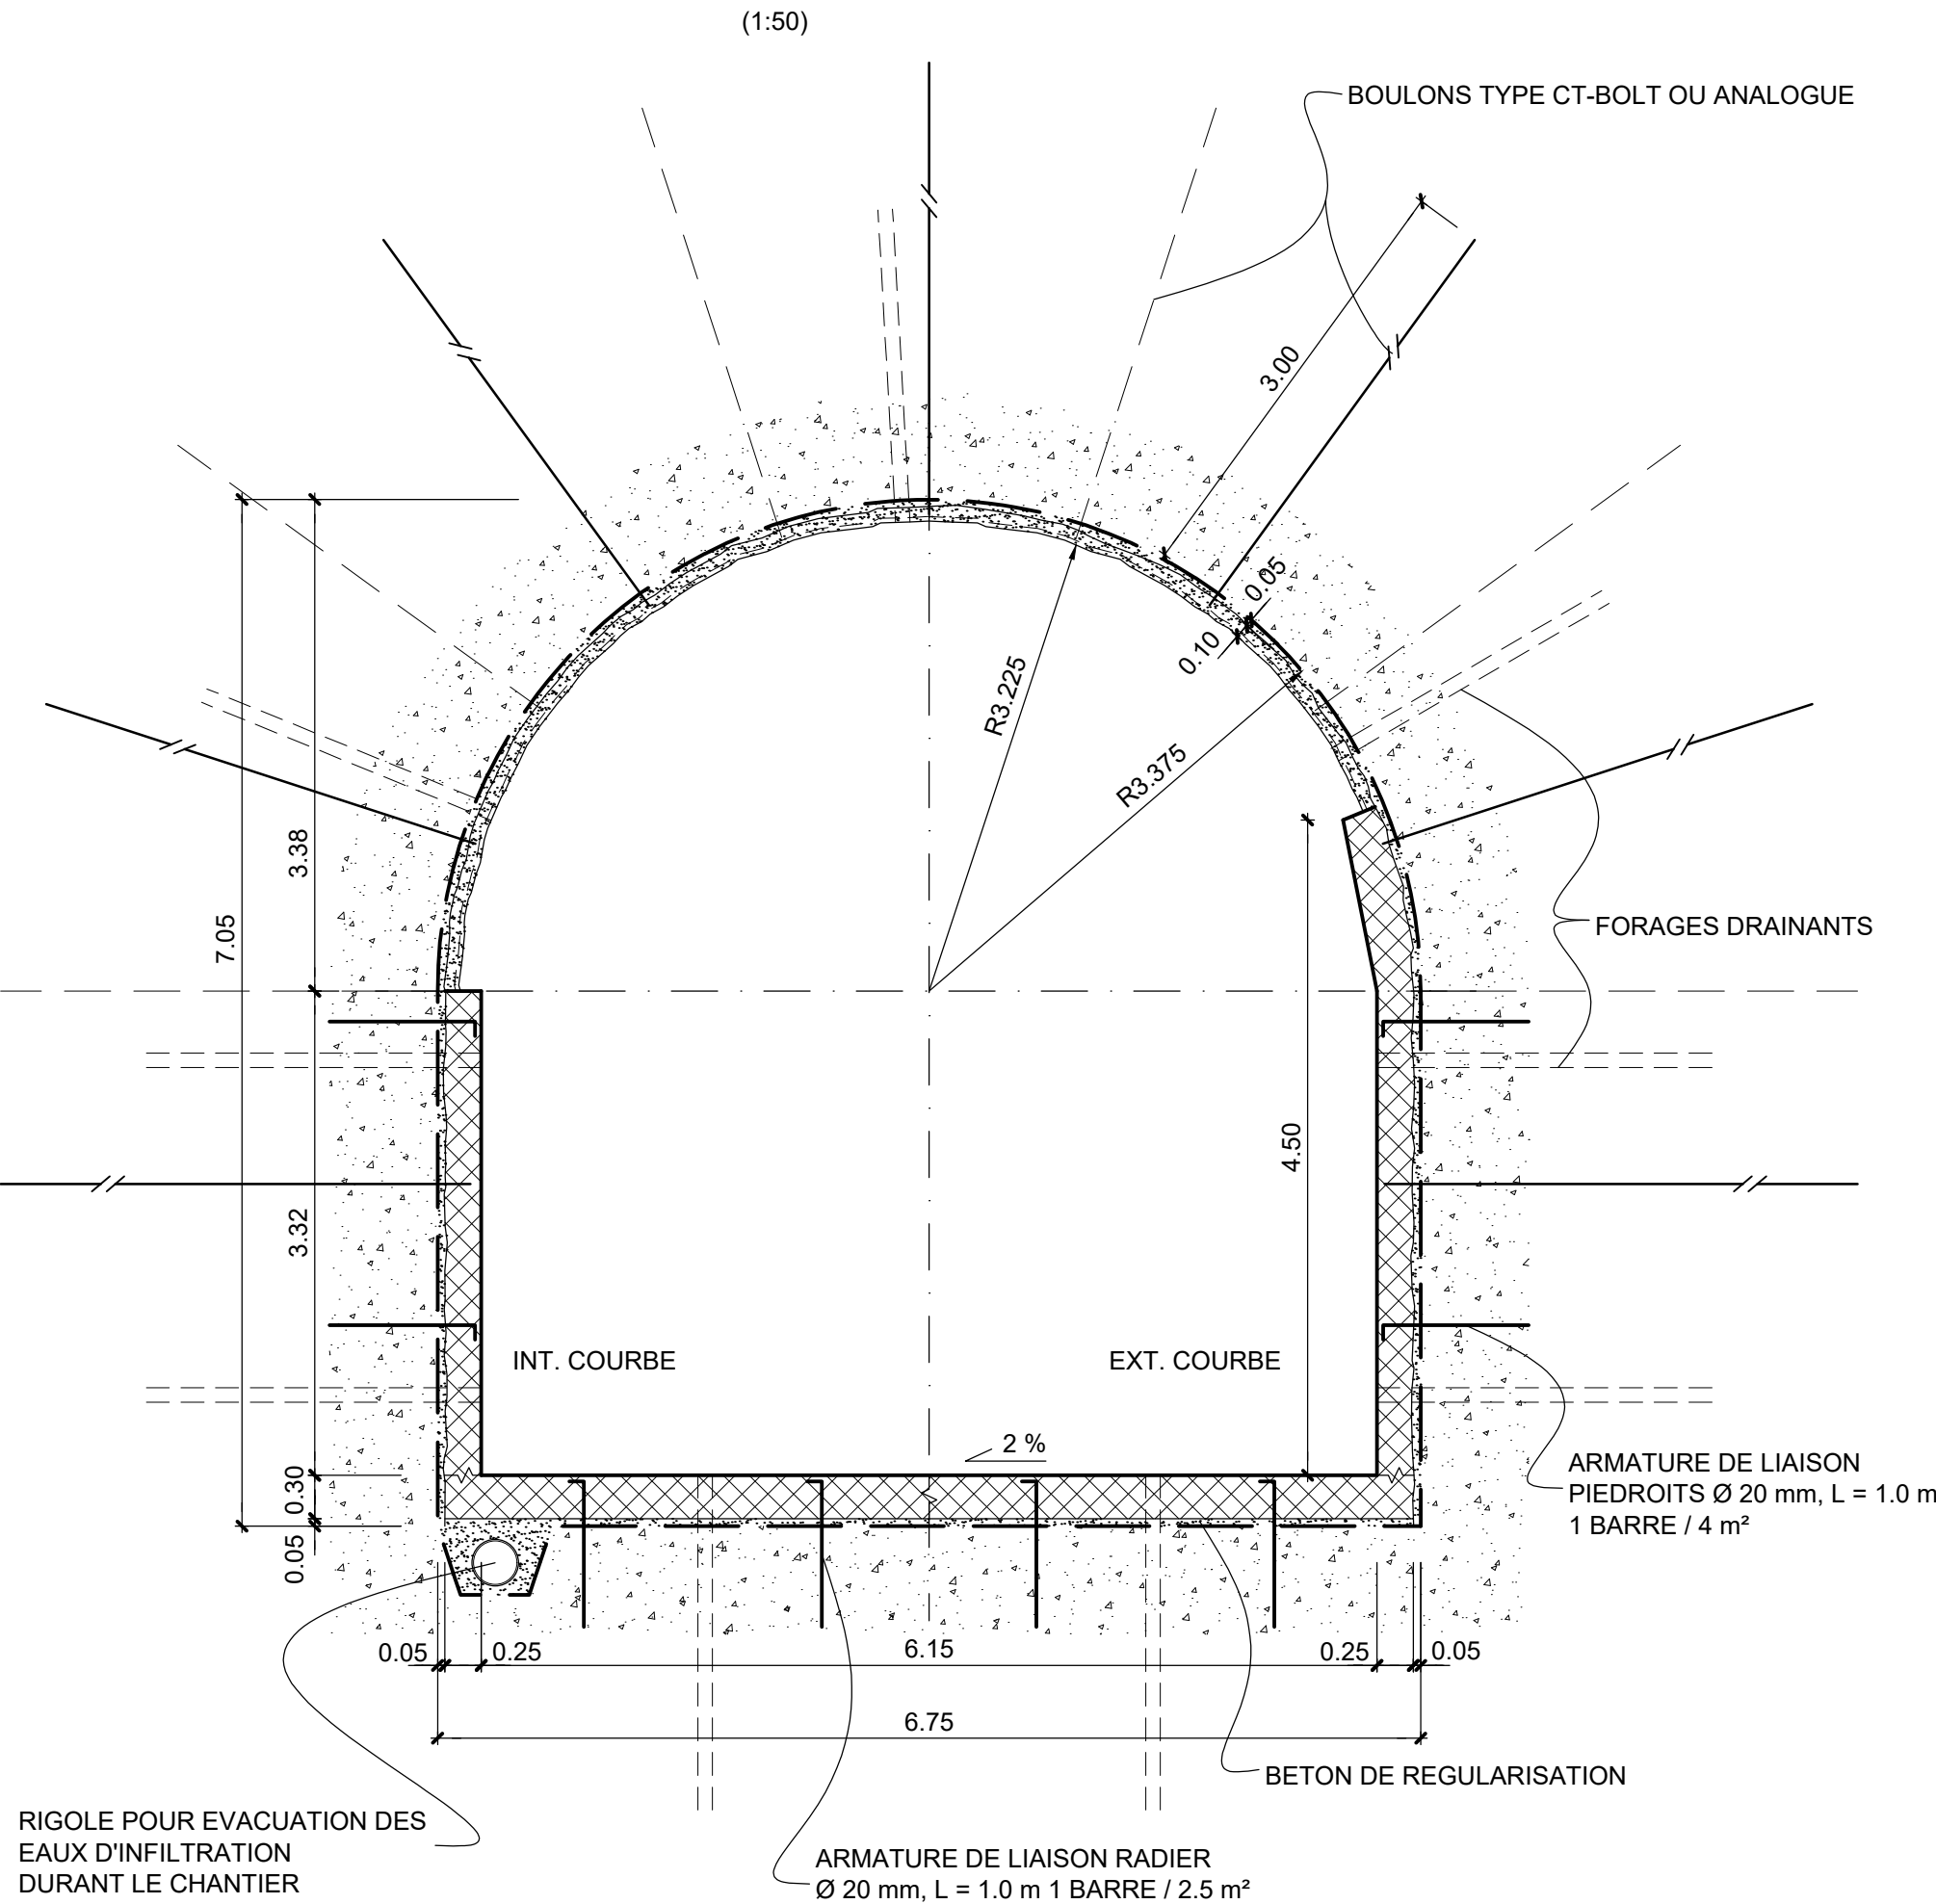


SOUTENEMENT (PAR METRE LINEAIRE)

- 5cm BETON PROJETE AVEC FIBRES D'ACIER [Kg/m3]
- 6/7 BOULONS TYPE CT-BOLT OU ANALOGUE, L= 3m

REVETEMENT DEFINITIF ANCRE AU ROCHER

- 30cm BETON ARME (RADIER) AVEC TRELLIS D'ARMATURE
- 25cm BETON ARME (PAROI) AVEC TRELLIS D'ARMATURE
- 10cm BETON PROJETE : (CALOTTE)
 - 7cm AVEC FIBRES
 - 3cm SANS FIBRES
- FORAGES DRAINANTS Ø80mm, L=2m MUNIS DE TUBE CREPINE Ø 50mm

ROCHE MOYENNE

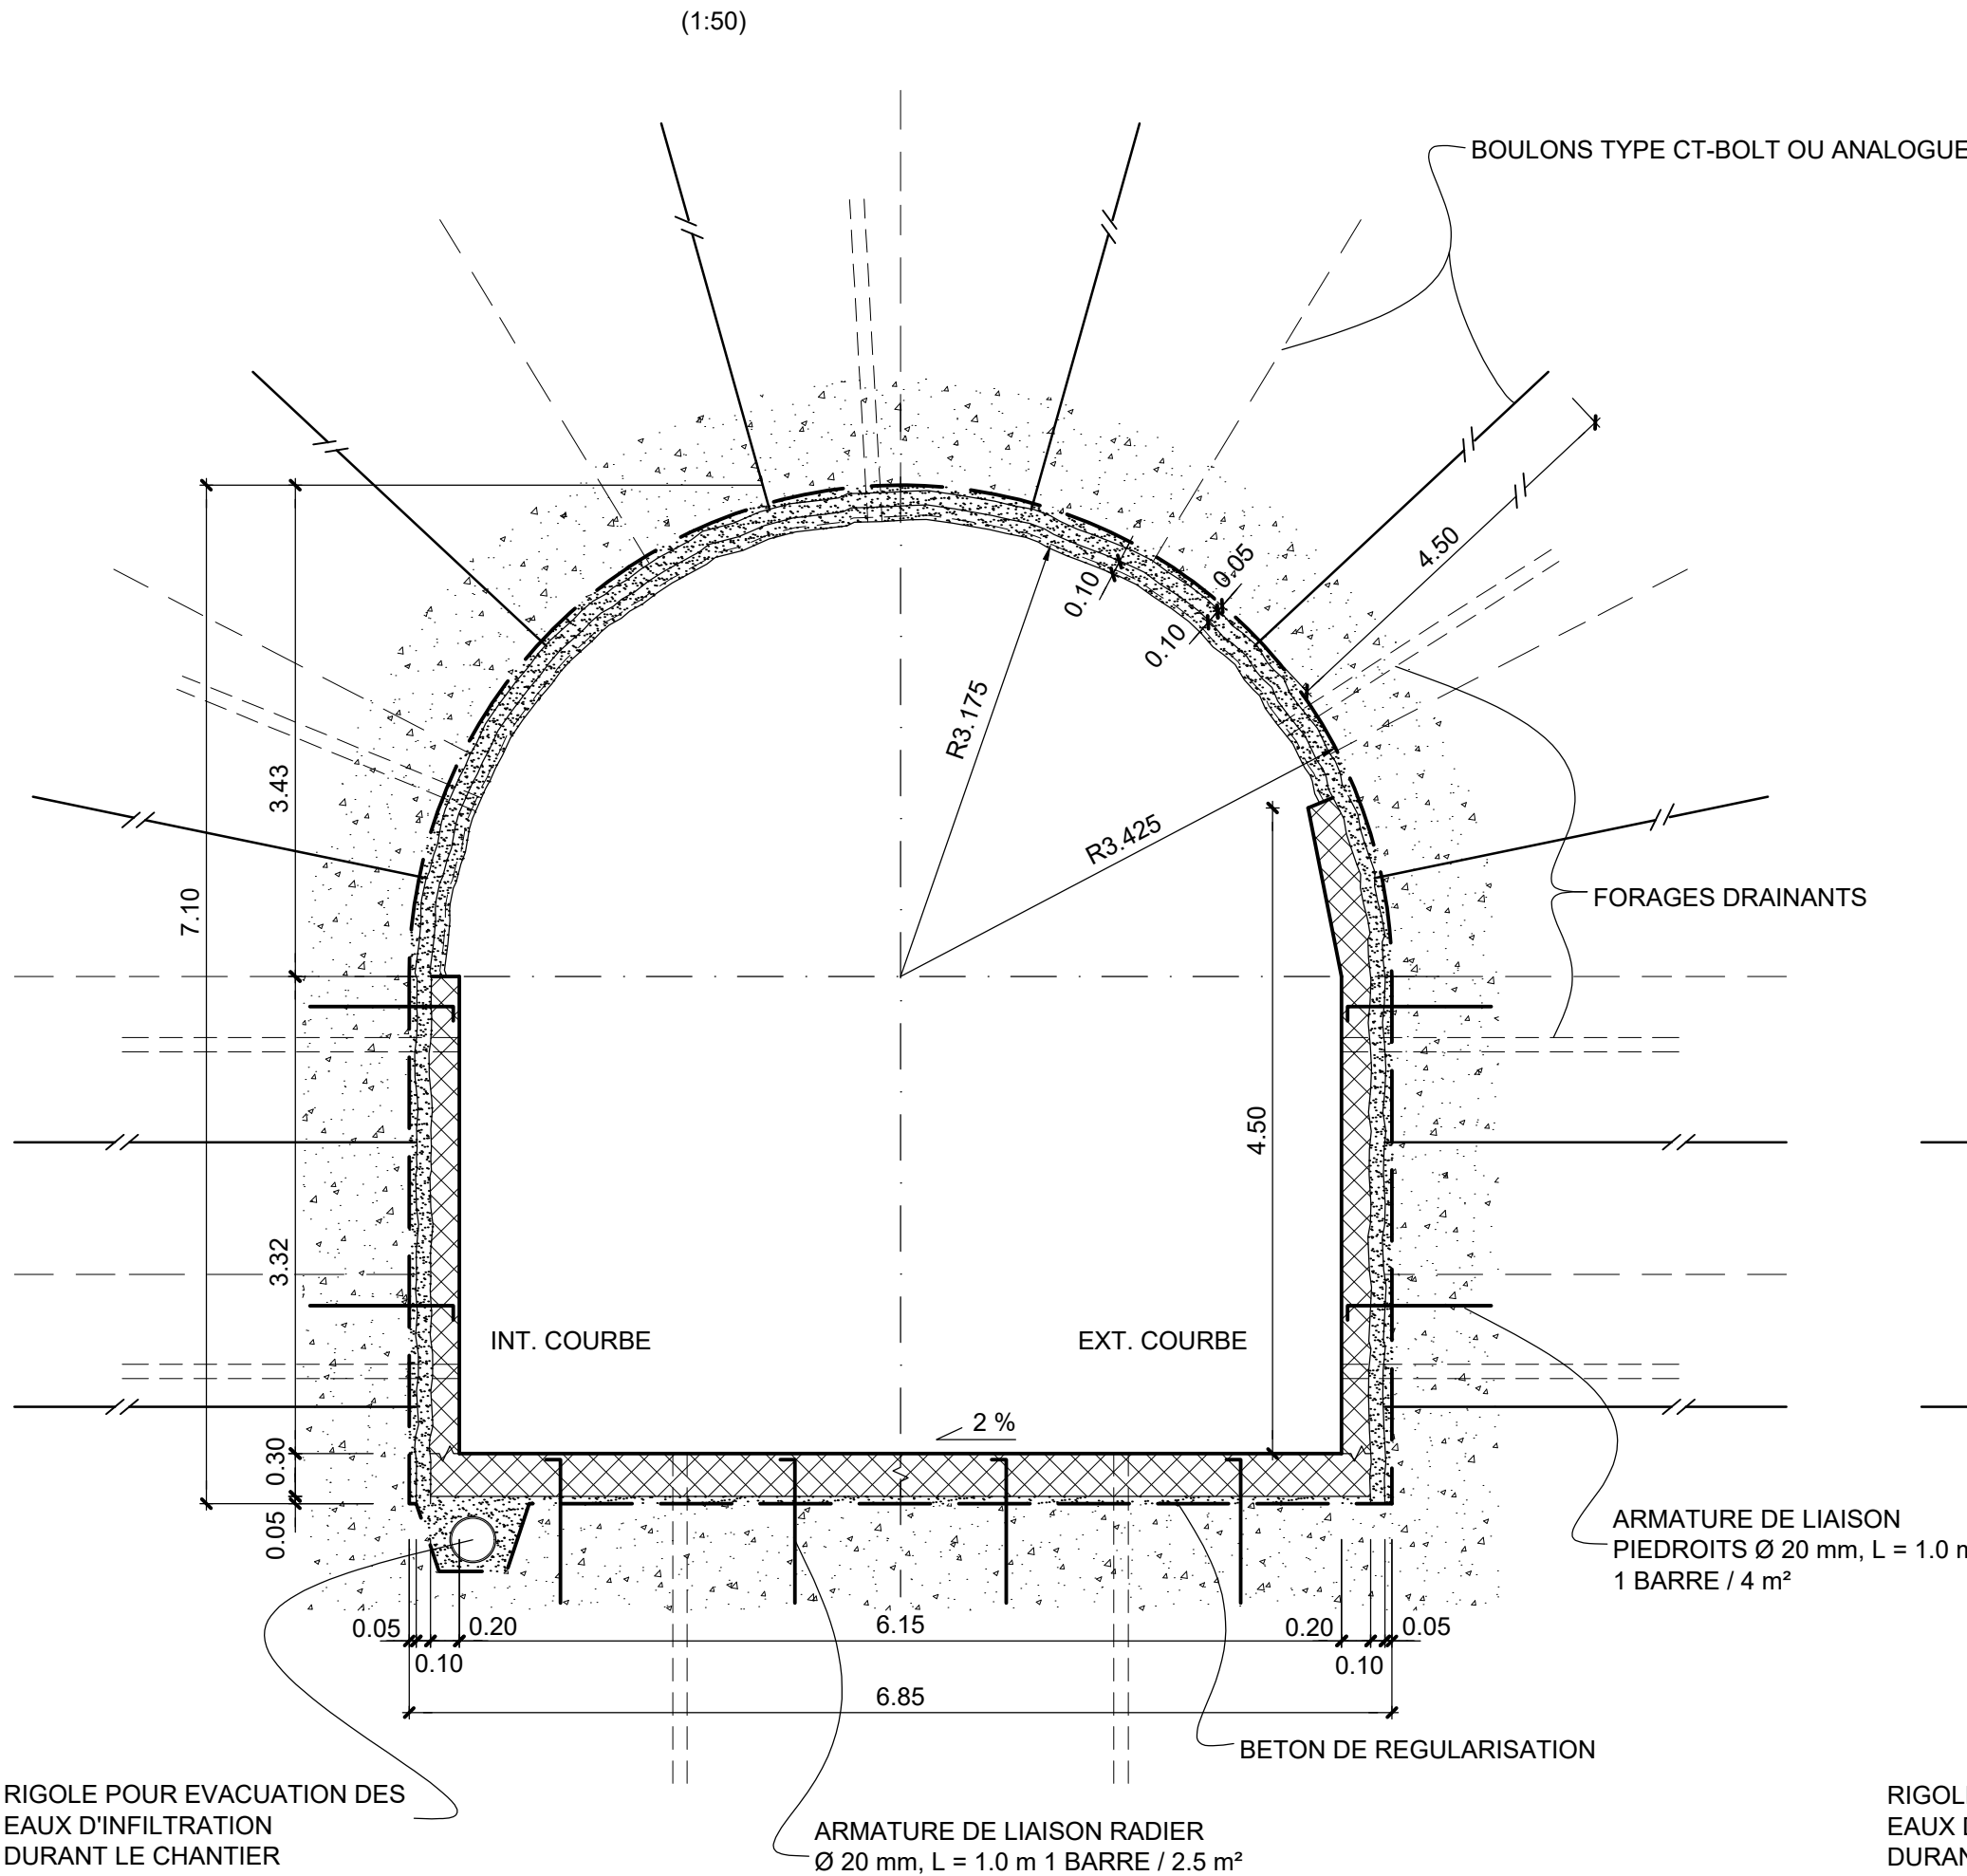


SOUTENEMENT (PAR METRE LINEAIRE)

- 5cm BETON PROJETE AVEC FIBRES D'ACIER
- 9/10 BOULONS TYPE CT-BOLT OU ANALOGUE, L= 4.5m
- 10cm BETON PROJETE AVEC FIBRES

REVETEMENT DEFINITIF ANCRE AU ROCHER

- 30cm BETON ARME (RADIER) AVEC TRELLIS D'ARMATURE
- 20cm BETON (ARME PAROI) AVEC TRELLIS D'ARMATURE
- 10cm BETON PROJETE : (CALOTTE)
 - 7cm AVEC FIBRES
 - 3cm SANS FIBRES
- FORAGES DRAINANTS Ø80mm, L=2m MUNIS DE TUBE CREPINE Ø 50mm

ROCHE BROYEE

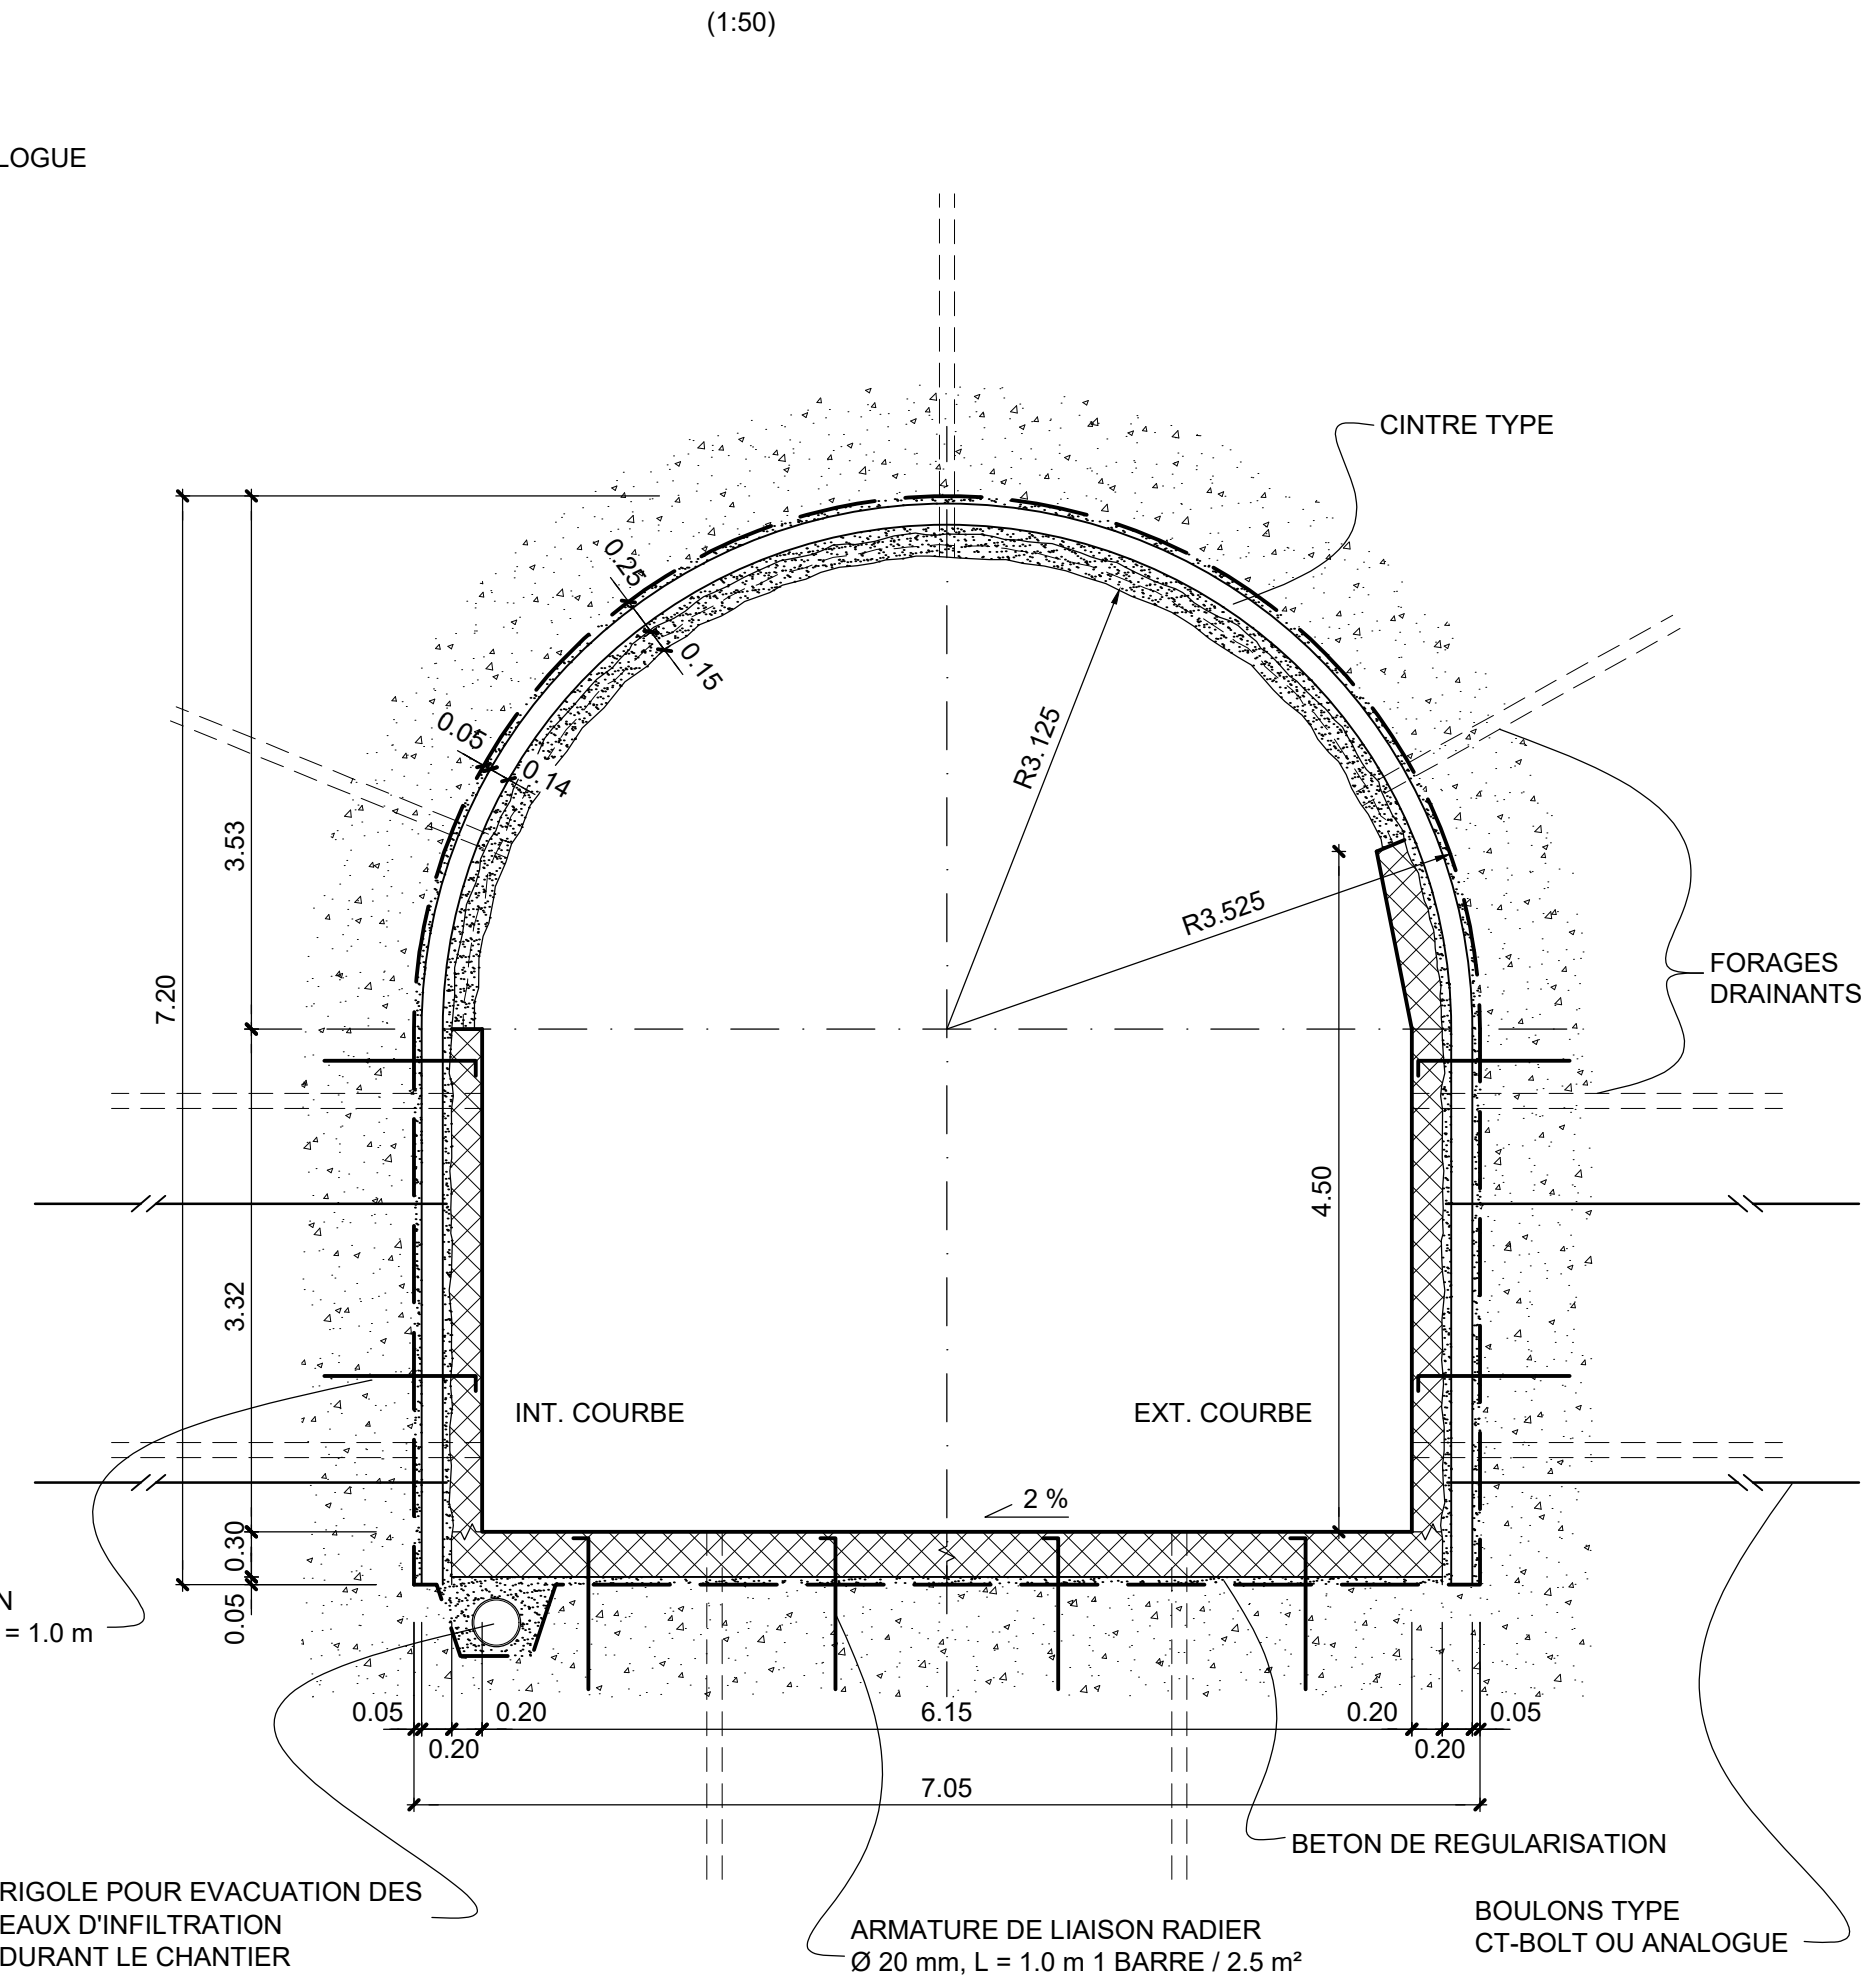

SOUTENEMENT (PAR METRE LINEAIRE)

- 5cm BETON PROJETE AVEC FIBRES D'ACIER
- CINTRE TYPE JB-4G-140/22 OU ANALOGUE
- 2+2 BOULONS TYPE CT-BOLT OU ANALOGUE, L= 4.5m
- 20cm BETON PROJETE AVEC FIBRES


REVETEMENT DEFINITIF ANCRE AU ROCHER

- 30cm BETON ARME (RADIER) AVEC TRELLIS D'ARMATURE
- 20cm BETON (PAROI) AVEC TRELLIS D'ARMATURE
- 15cm BETON PROJETE : (CALOTTE)
 - 12cm AVEC FIBRES
 - 3cm SANS FIBRES
- FORAGES DRAINANTS Ø80mm, L=2m MUNIS DE TUBE CREPINE Ø 50mm

ECHELLE GRAPHIQUE :



SITUATION

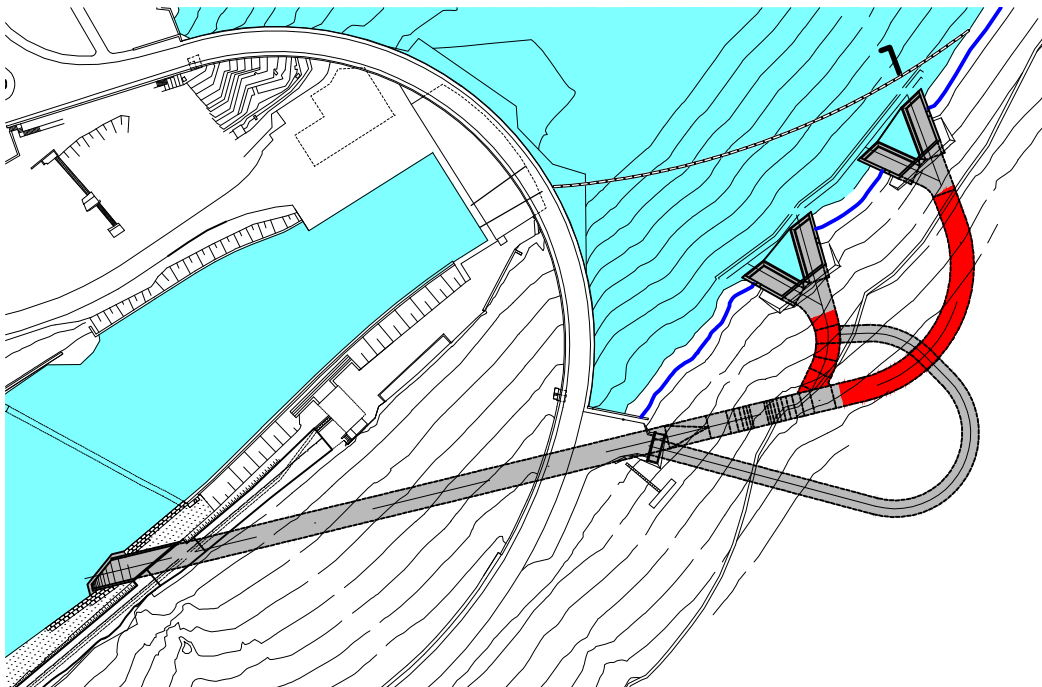

NOTE:

- LE TYPE DE SOUTENEMENT SERA DEFINI EN FONCTION DE LA QUALITE DE LA ROCHE
- DISTRIBUTION ADMISE: 35% ROCHE BONNE / 50% ROCHE MOYENNE / 15% ROCHE BROYEE

		LE GOUVERNEMENT DU GRAND-DUCHÉ DE LUXEMBOURG MINISTÈRE DE LA MOBILITÉ ET DES TRAVAUX PUBLICS ADMINISTRATION DES PONTS ET CHAUSSEES			
BARRAGE D'ESCH-SUR-SURE Evacuateur de crue complémentaire OA1158					
SOUSSION					
CANAL DE DECHARGE TYPES DE SOUTENEMENT ET REVETEMENT DEFINITIF					
				C	
				B	
				A	
Date:	Dess.	Verif.	Appr.	Description modification	
08.06.2015	UP	Fel	BF	A1 (84 x 60)	7500.4-P-315
Date:	Dess.	Verif.	Appr.	Dim. :	Nom fichier
Echelle : 1:50		No. Lo : 7500.4-P-315		No. 48936	