


COUPE C-C AU NIVEAU 317.00



DETAIL ANCRAGE

(1:20)

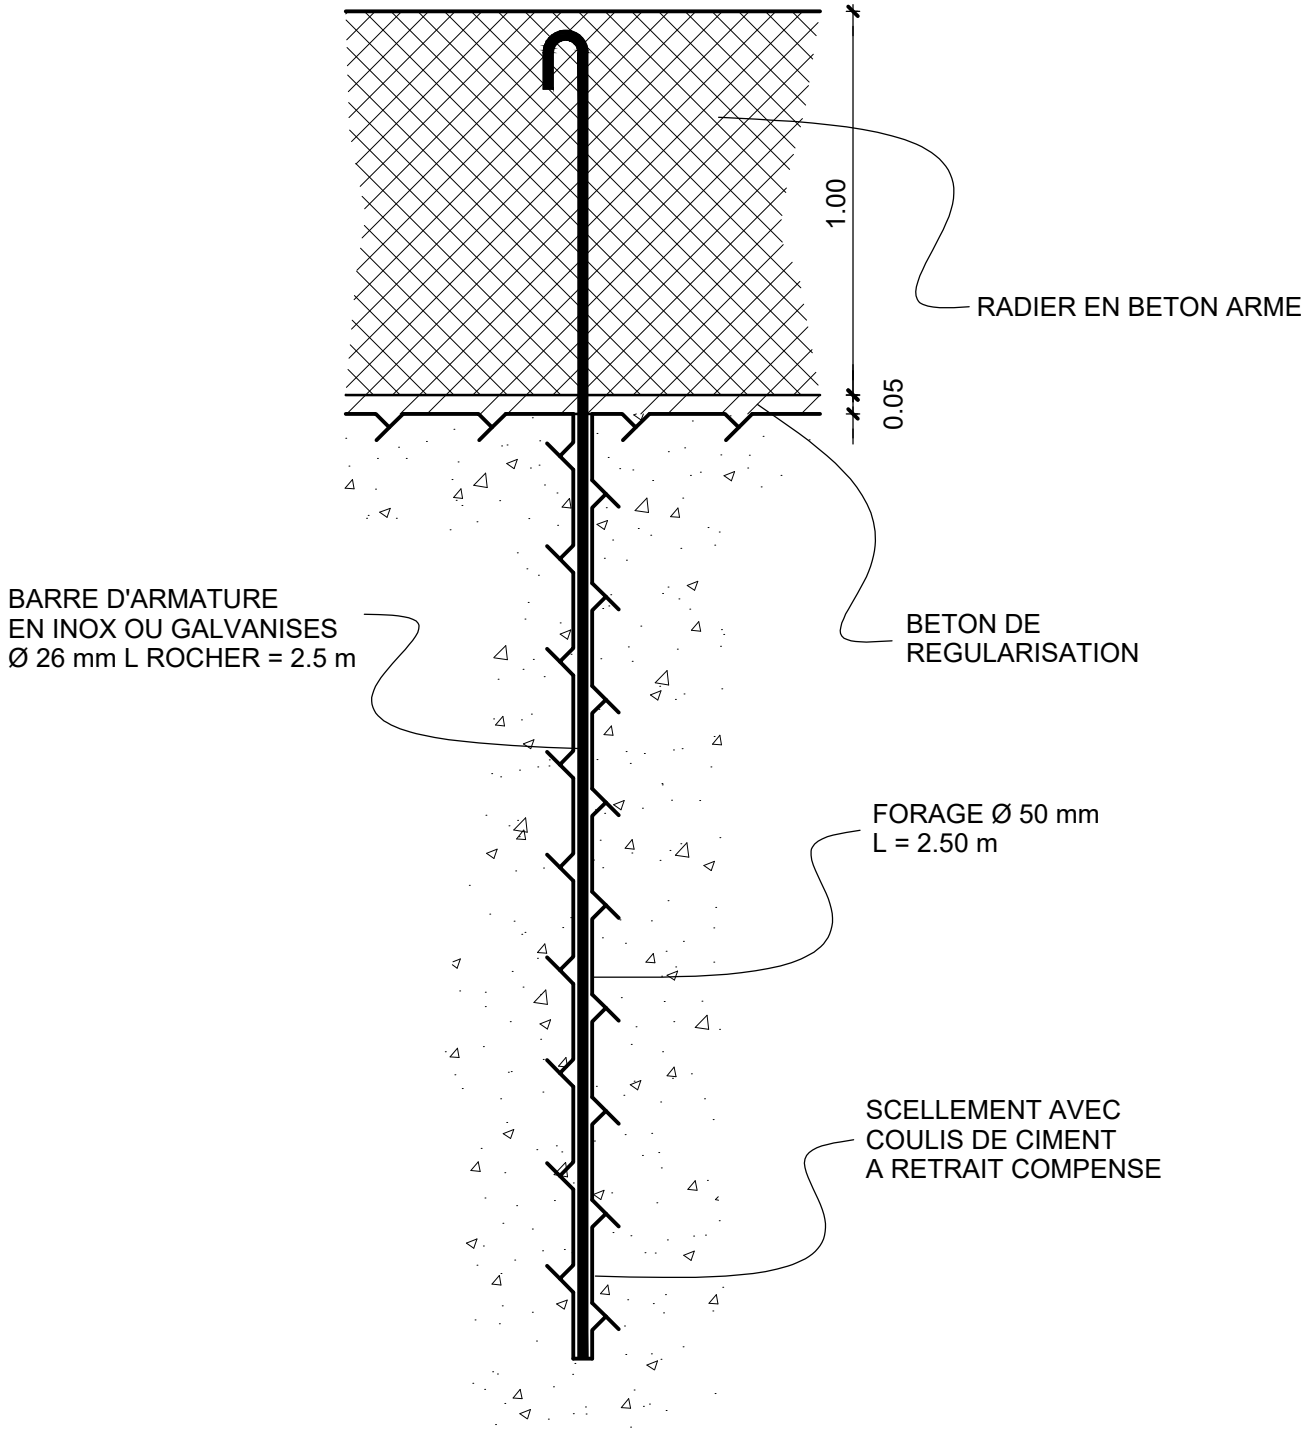

DETAIL DRAINAGE

(1:20)

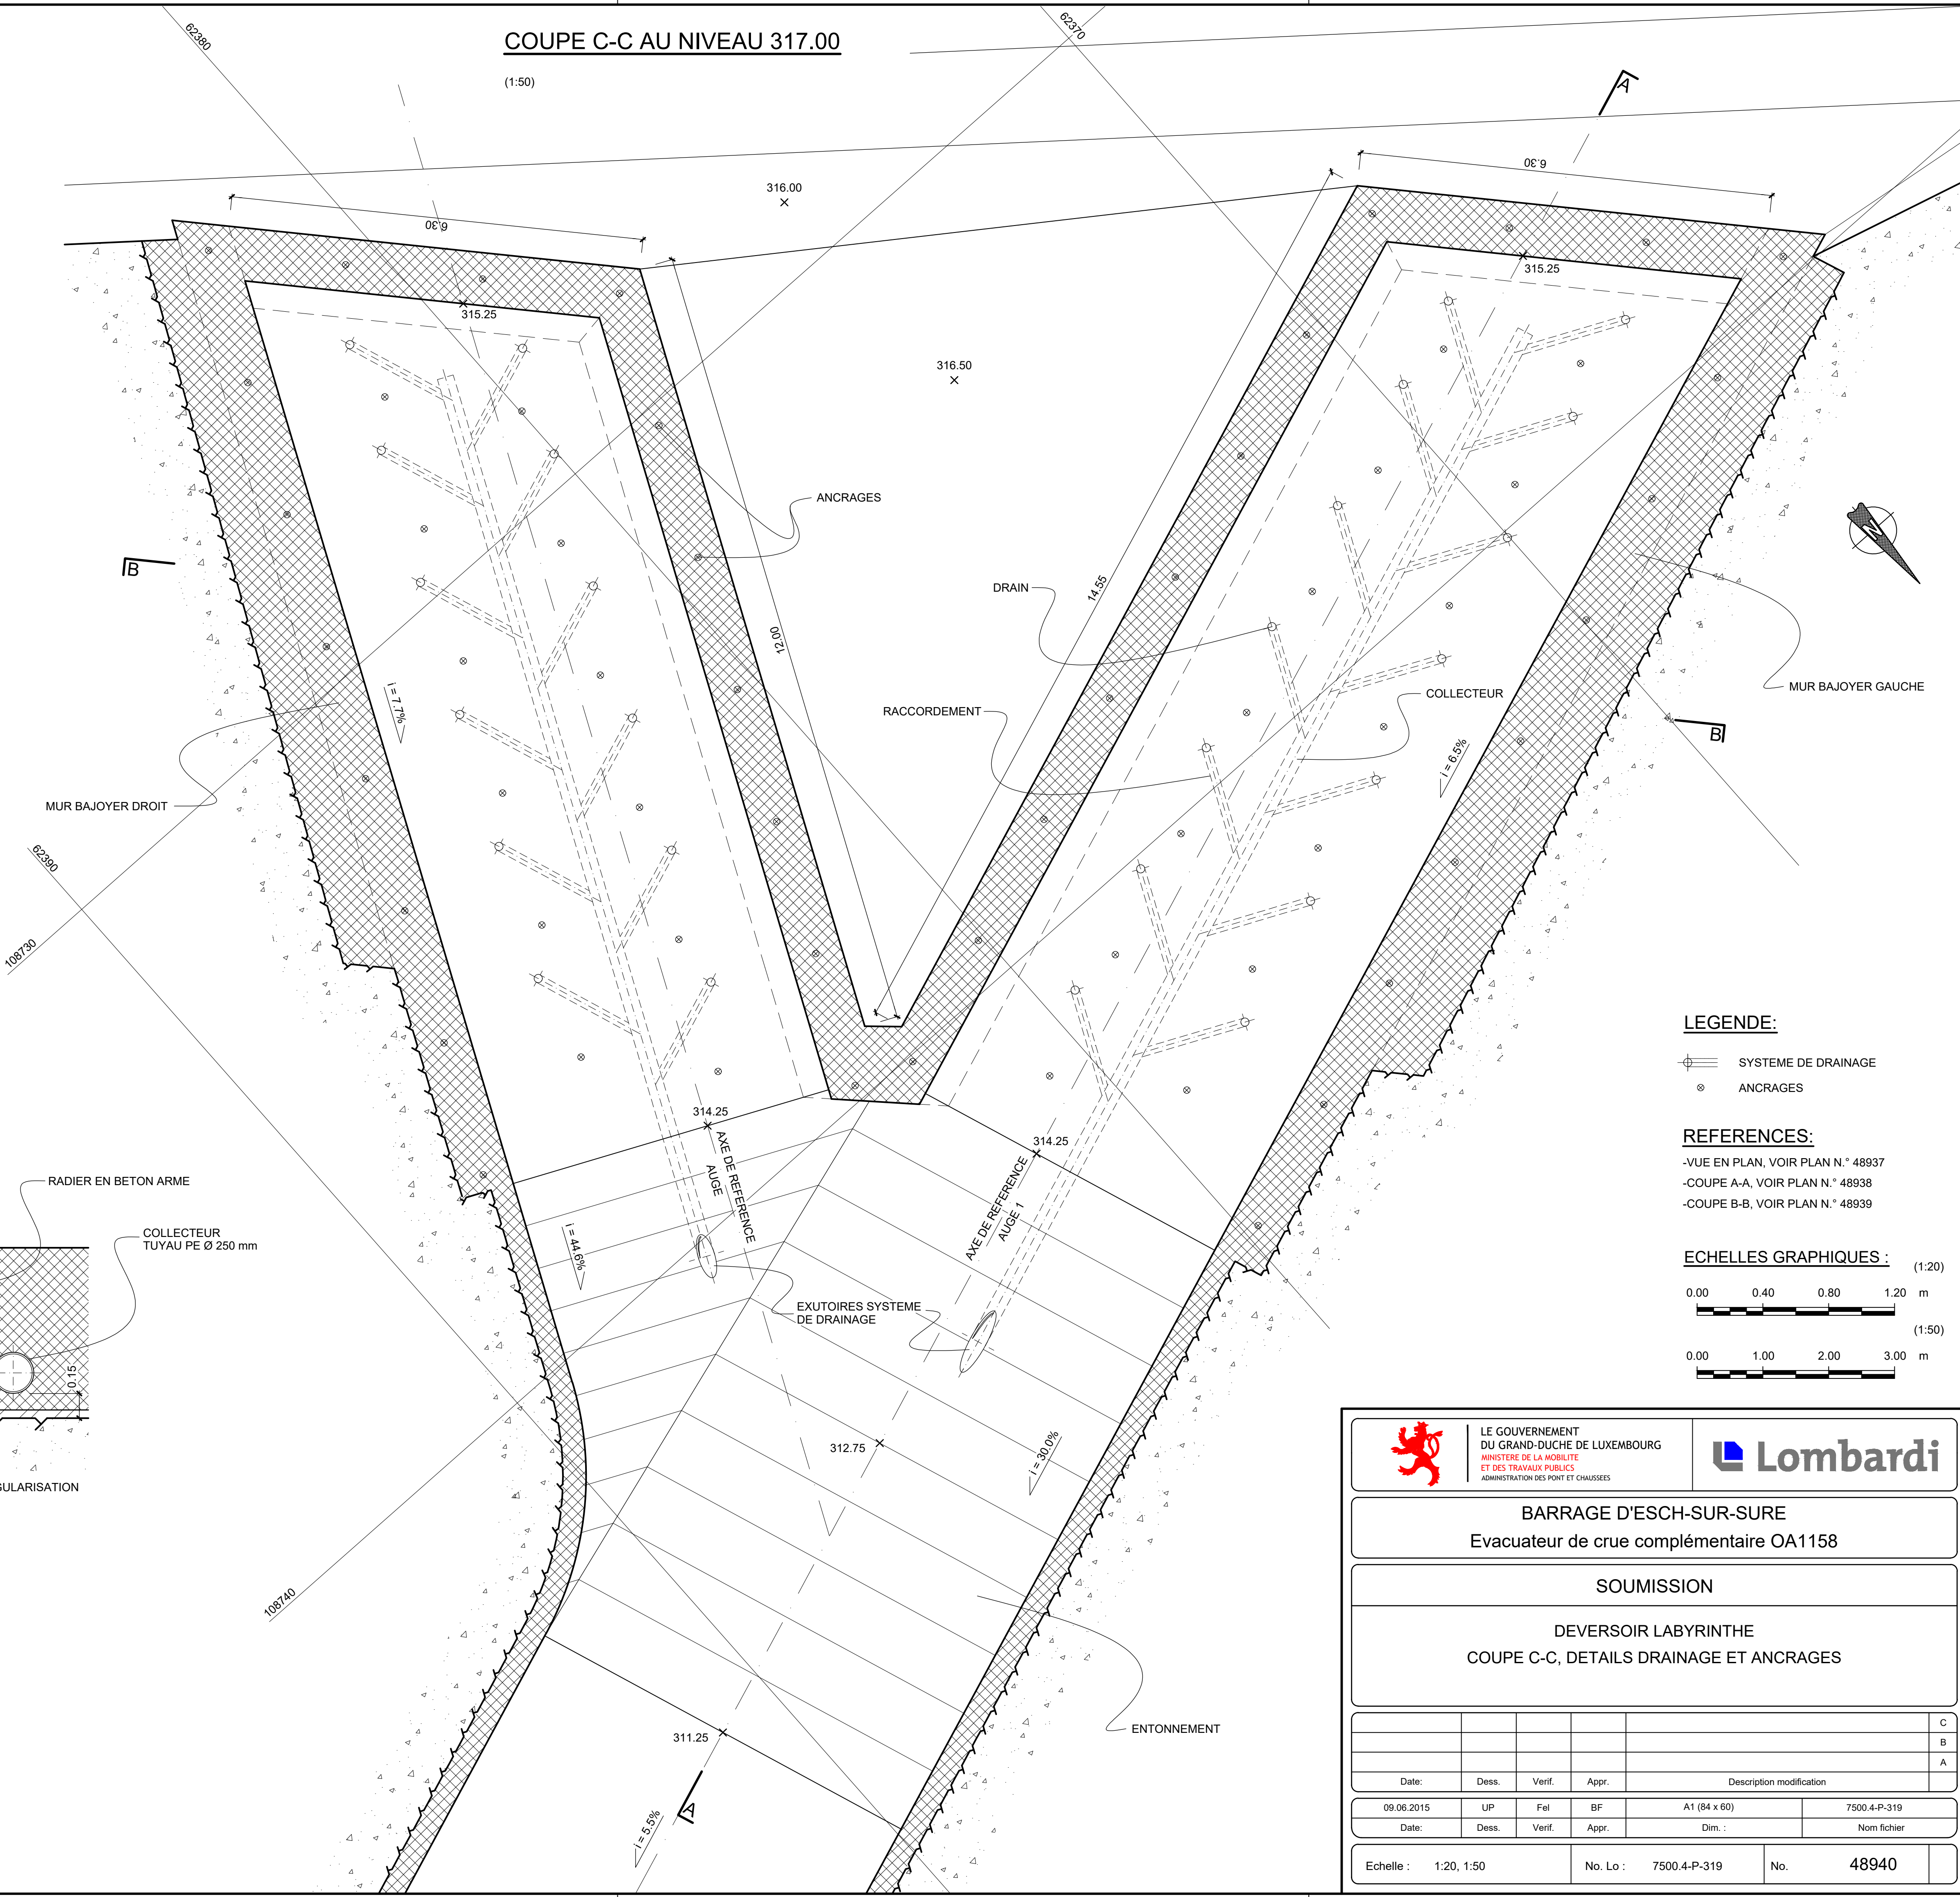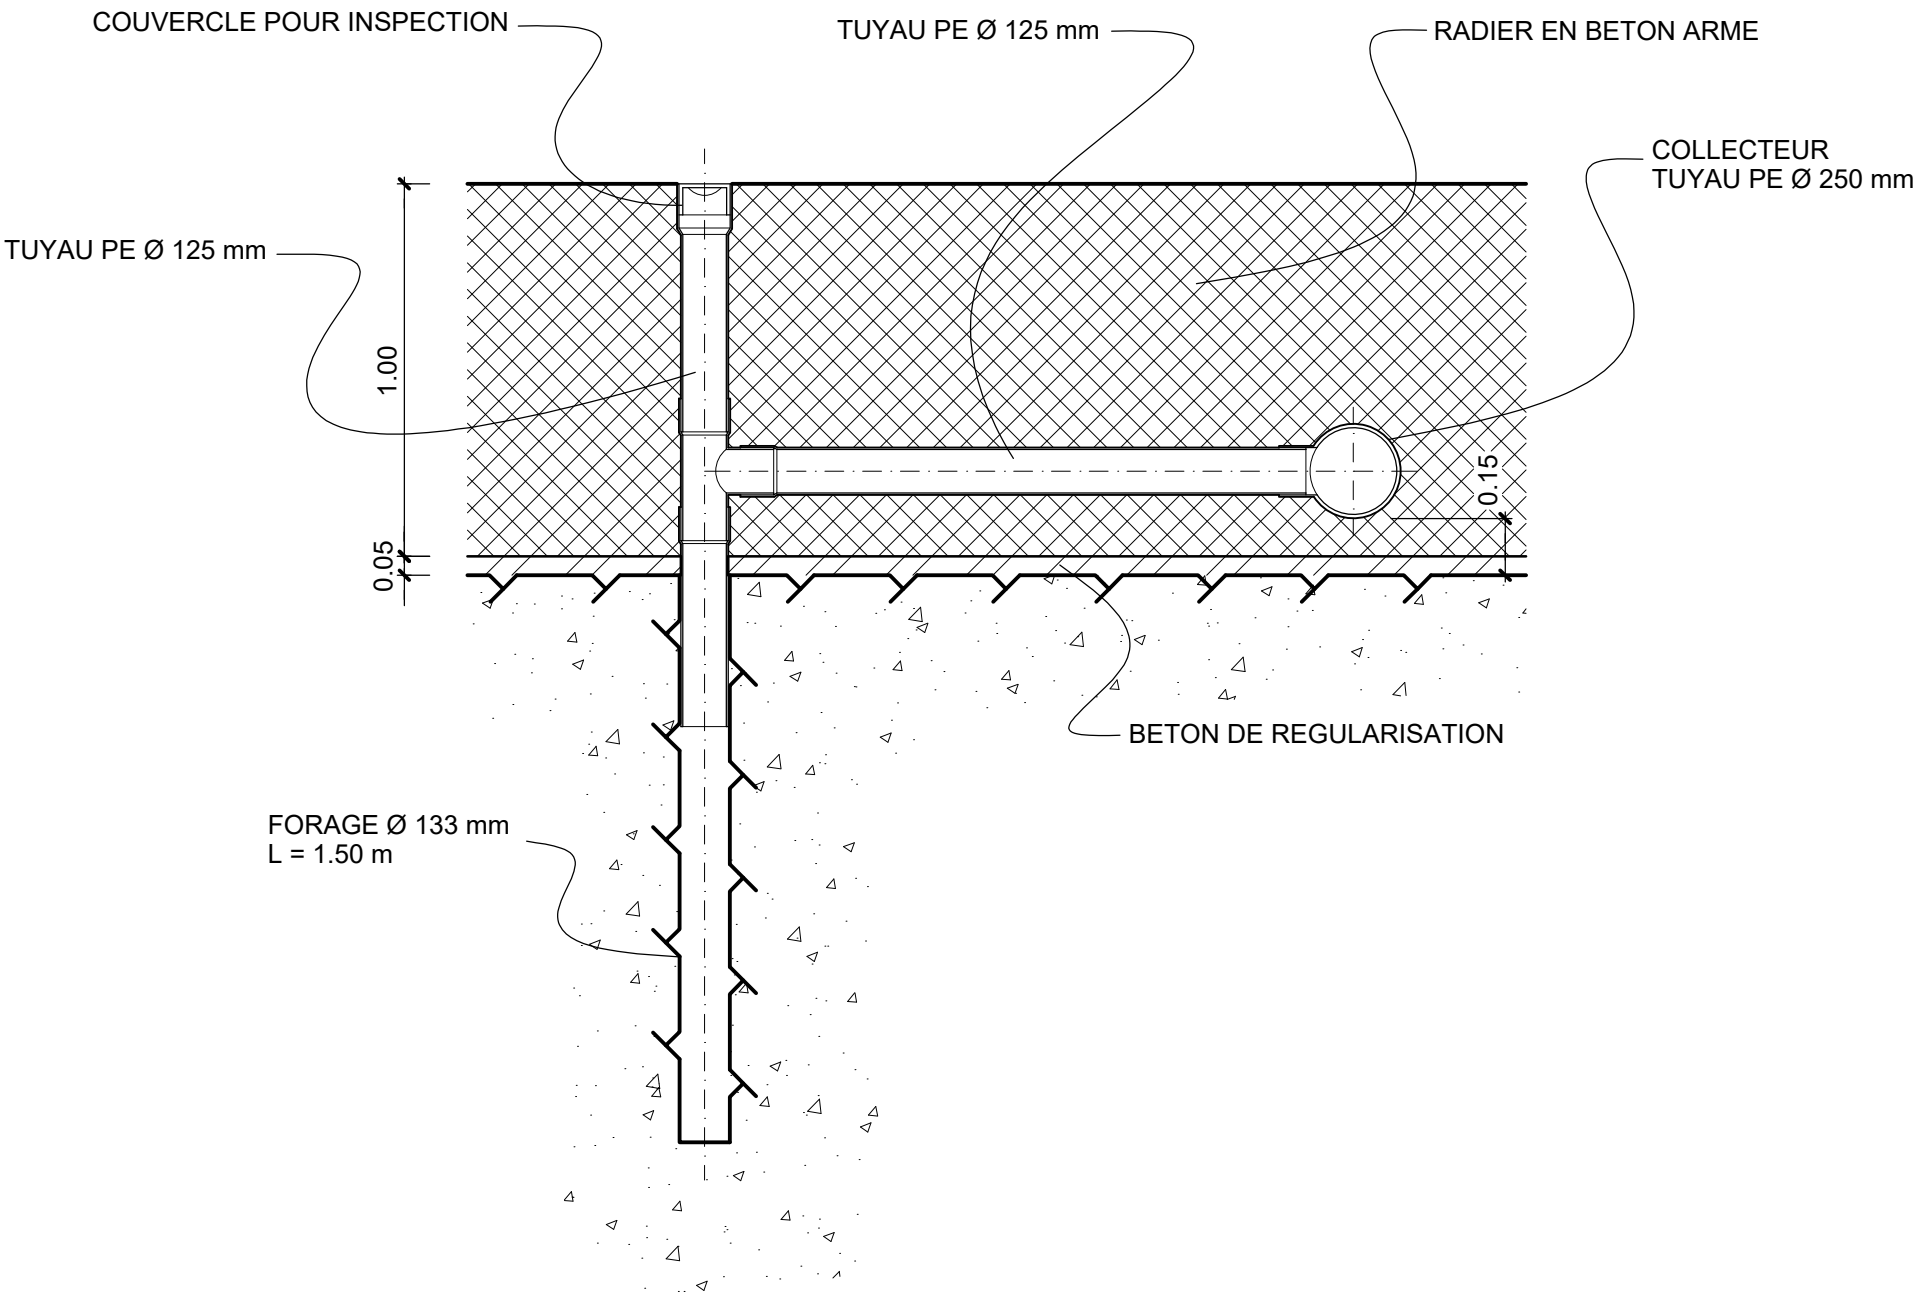


LEGENDE:

- SYSTEME DE DRAINAGE
- ANCRAGES

REFERENCES:

- VUE EN PLAN, VOIR PLAN N.° 48937
- COUPE A-A, VOIR PLAN N.° 48938
- COUPE B-B, VOIR PLAN N.° 48939

ECHELLES GRAPHIQUES :

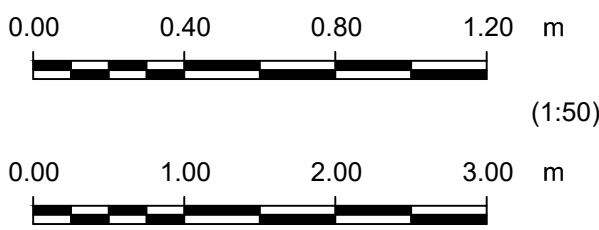

		LE GOUVERNEMENT DU GRAND-DUCHÉ DE LUXEMBOURG MINISTÈRE DE LA MOBILITÉ ET DES TRAVAUX PUBLICS ADMINISTRATION DES PONTS ET CHAUSSEES			
BARRAGE D'ESCH-SUR-SURE Evacuateur de crue complémentaire OA1158					
SOUSSION					
DEVERSOIR LABYRINTHE COUPE C-C, DETAILS DRAINAGE ET ANCRAGES					
Date:	Dess.	Verif.	Appr.	Description modification	C
09.06.2015	UP	Fel	BF	A1 (84 x 60)	B
Date:	Dess.	Verif.	Appr.	Dim. :	A
Echelle :	1:20, 1:50	No. Lo :	7500.4-P-319	No.	48940