




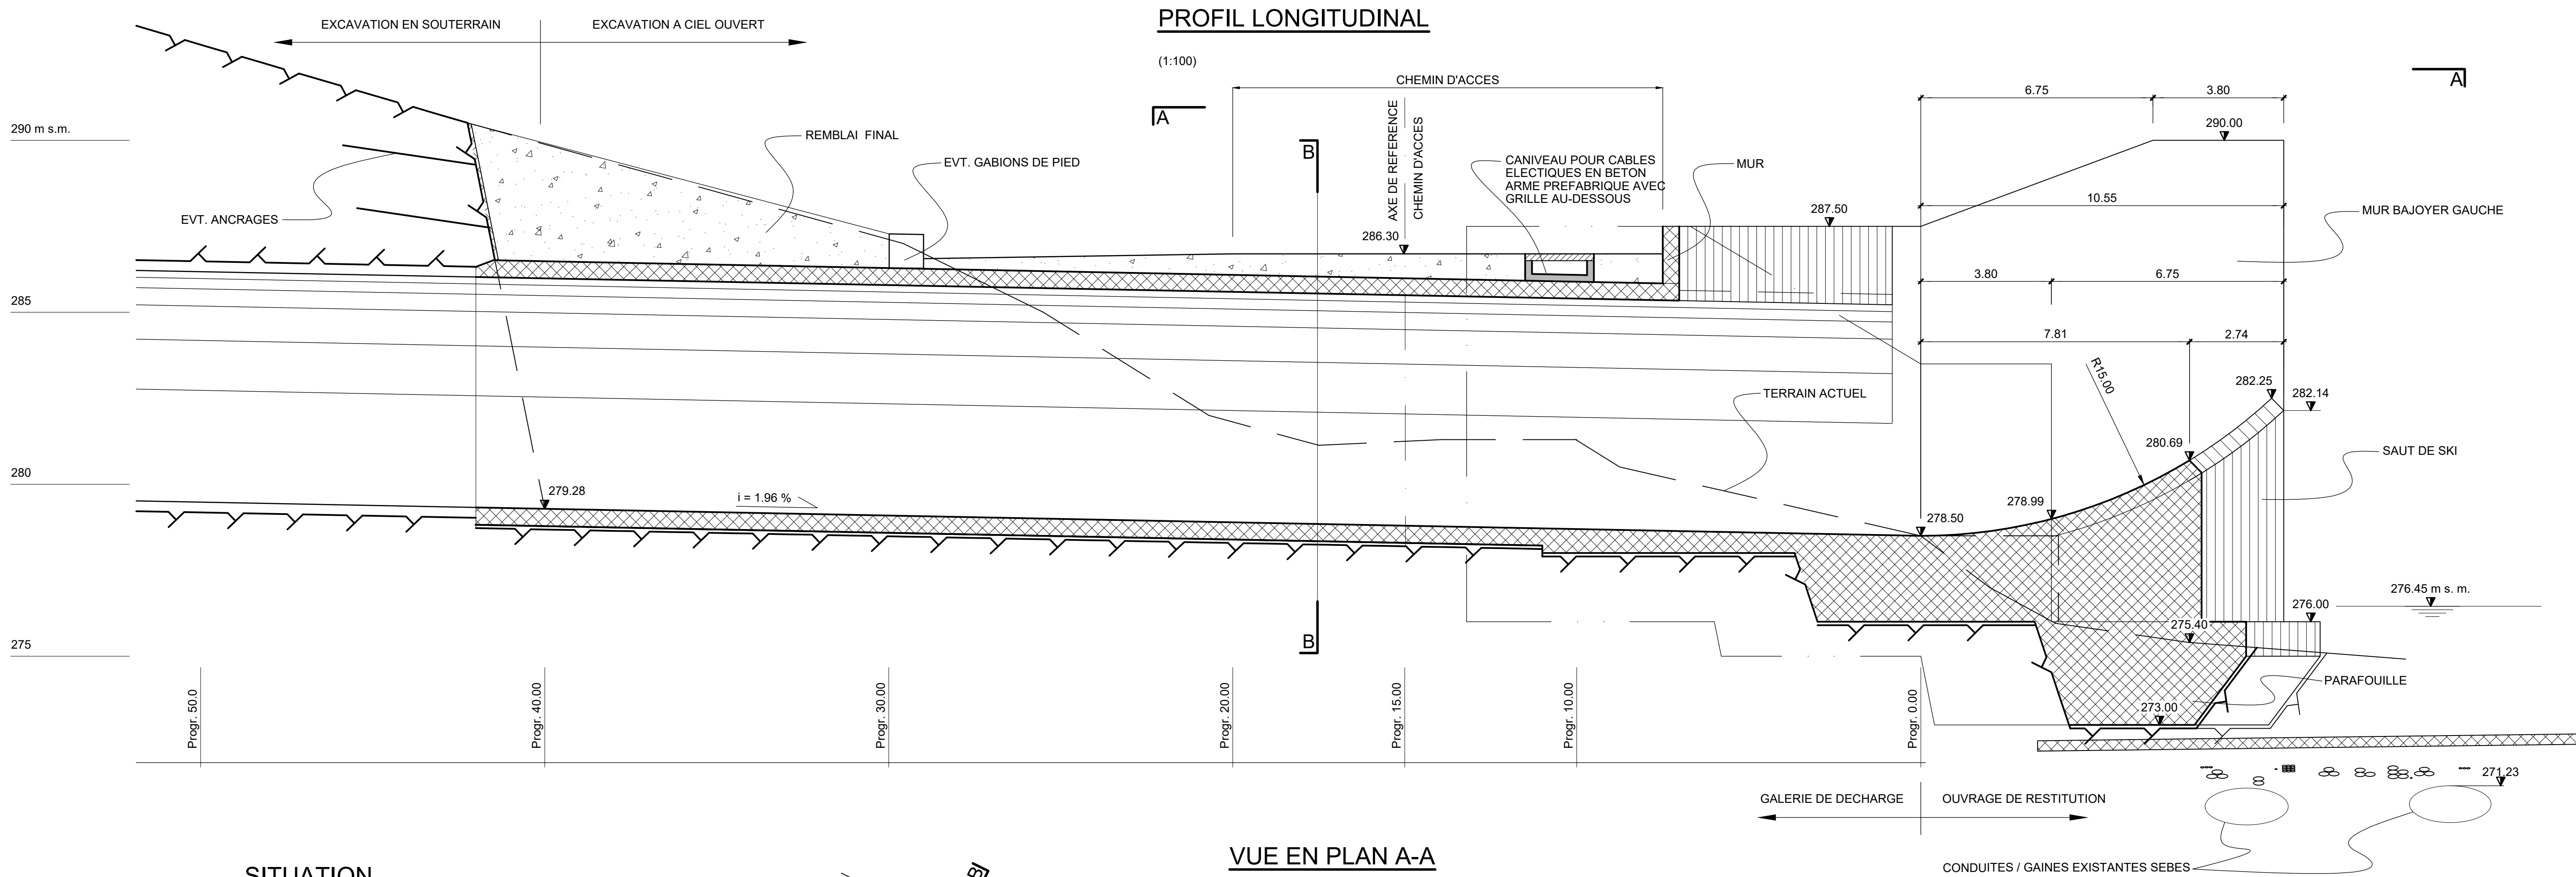


SITUATION

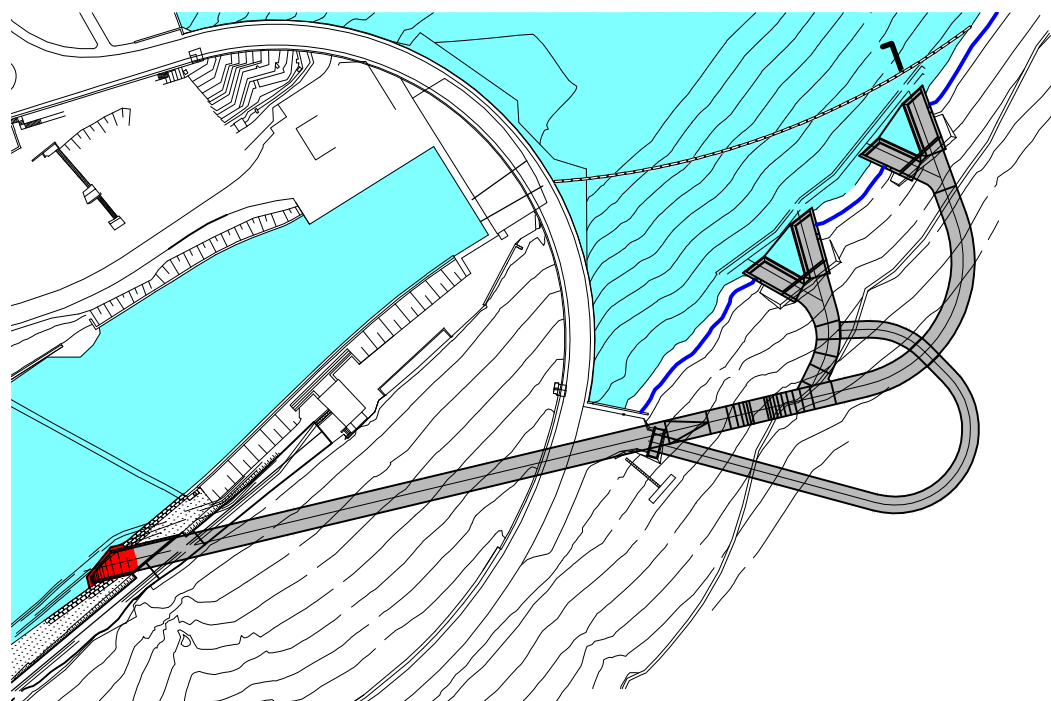

VUE EN PLAN A-A
(1:100)

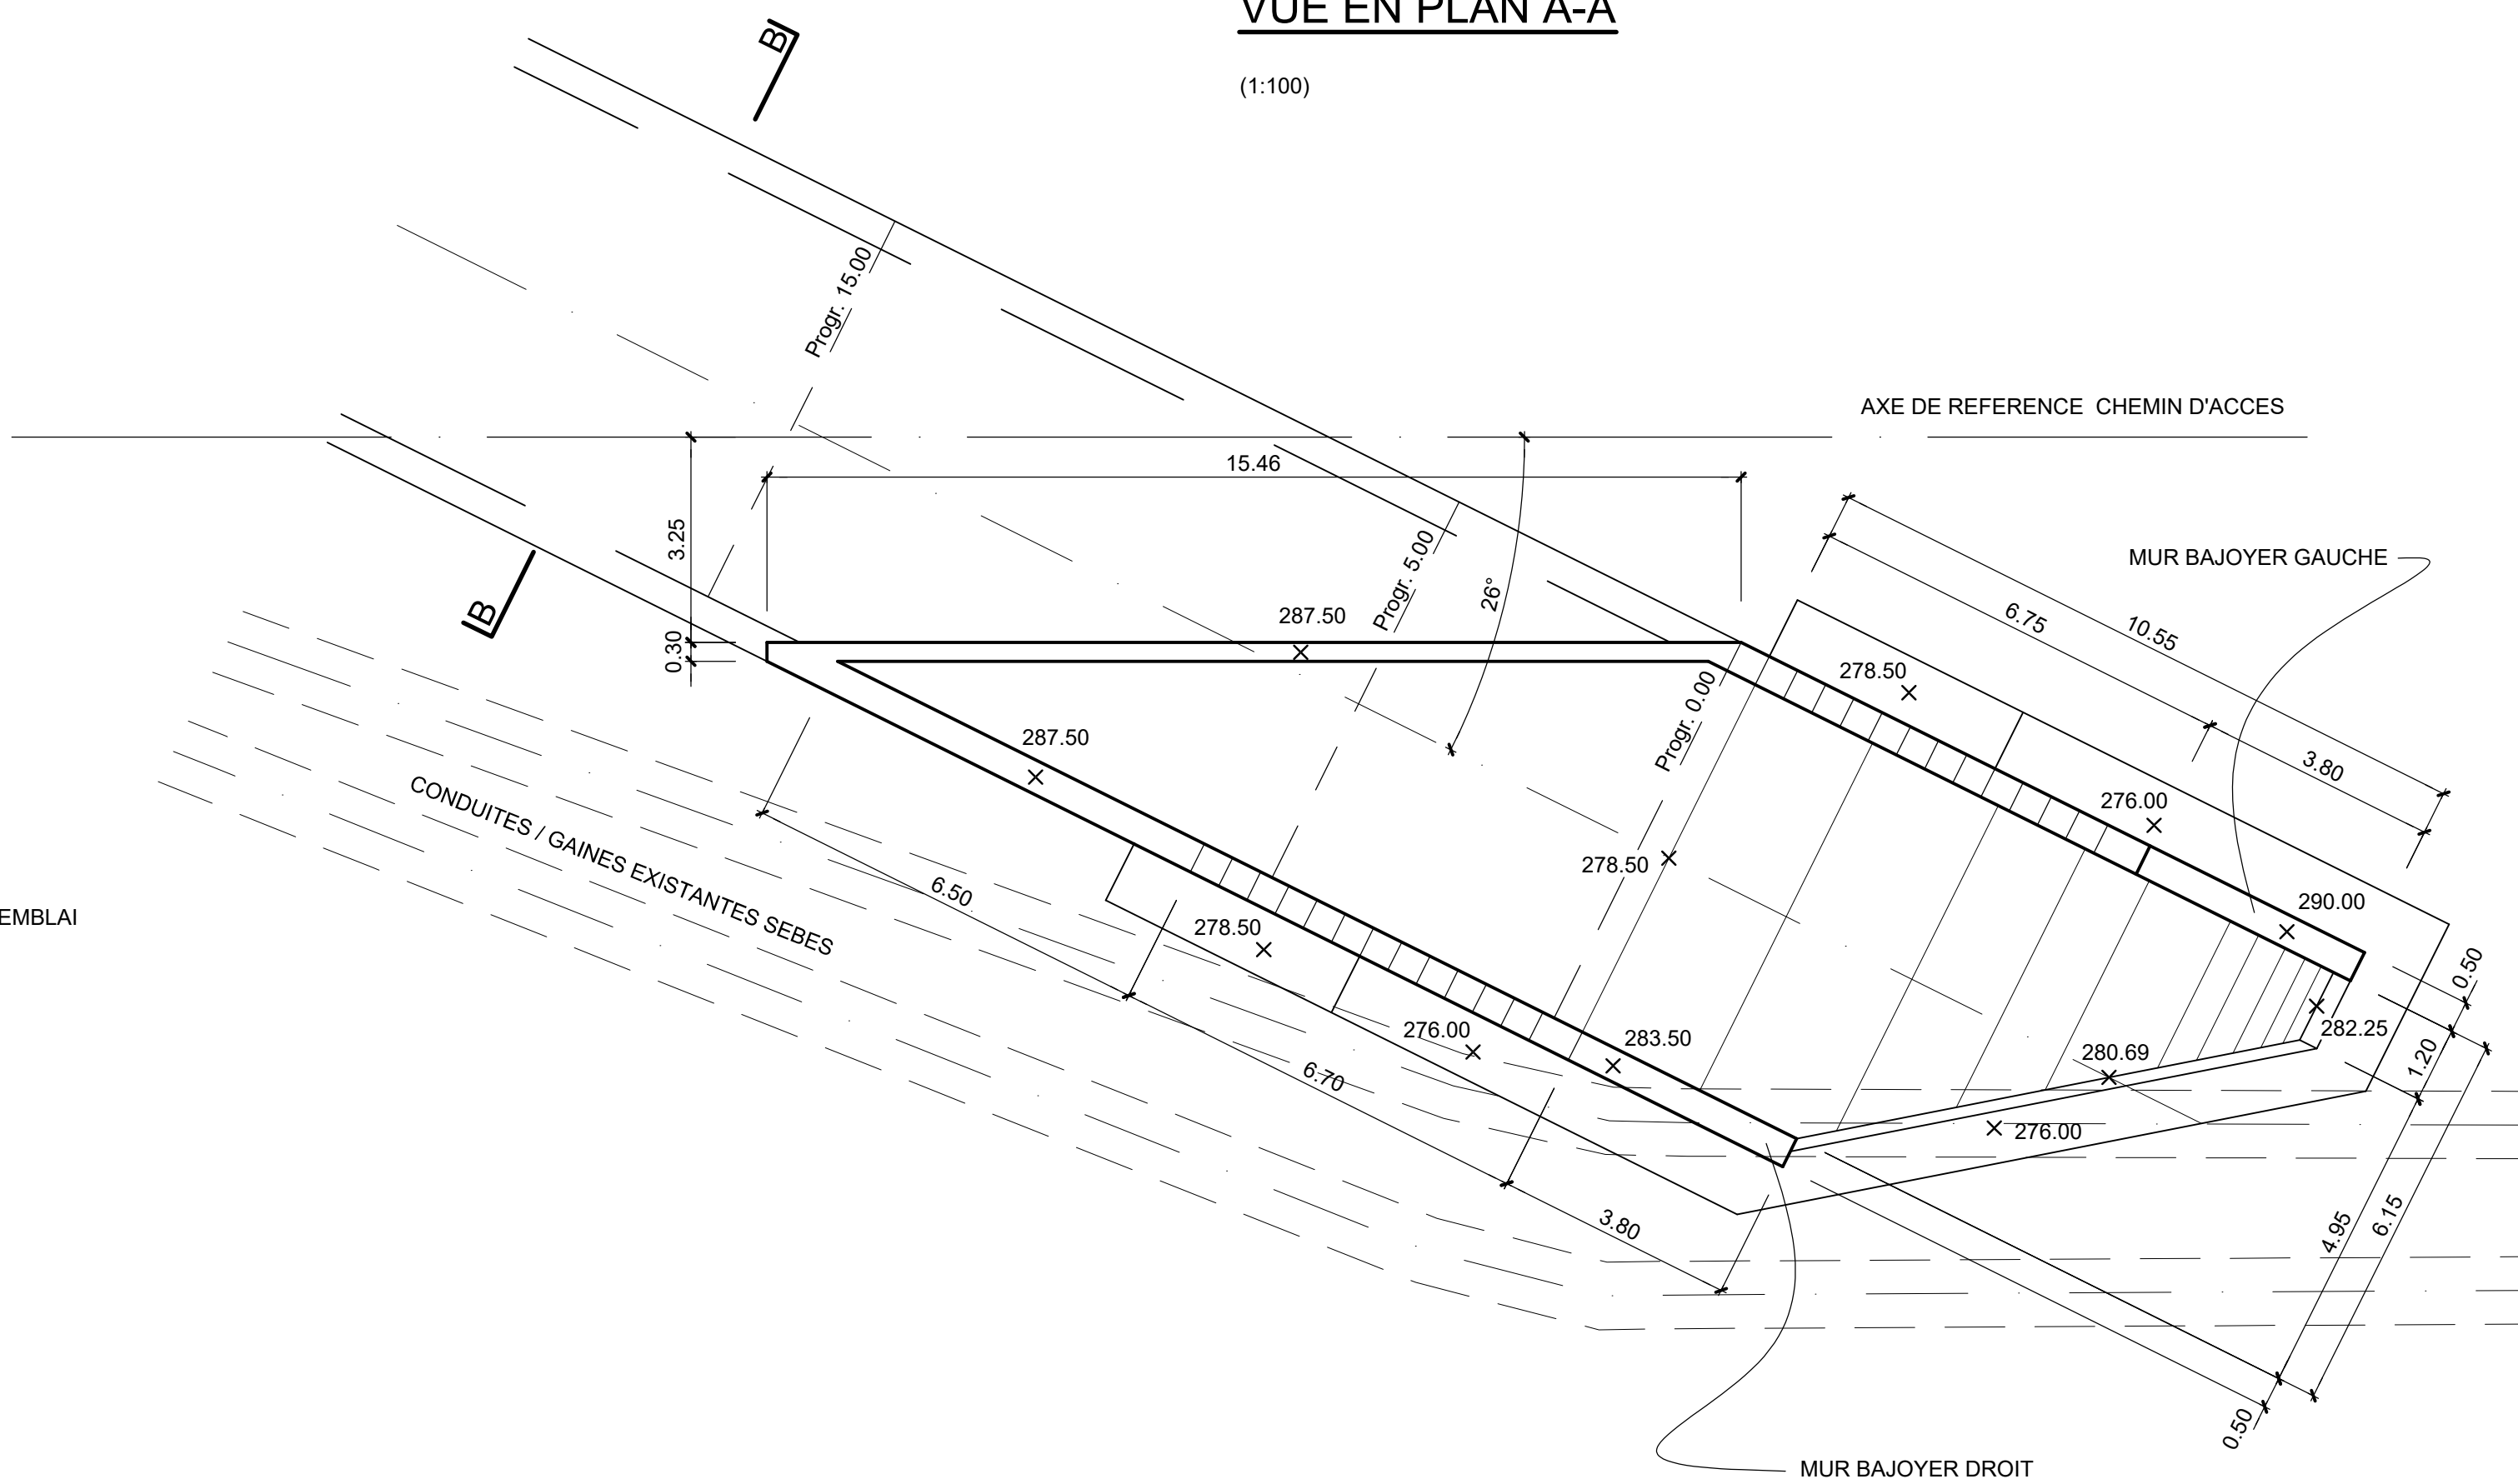


COUPE B-B
(1:100)

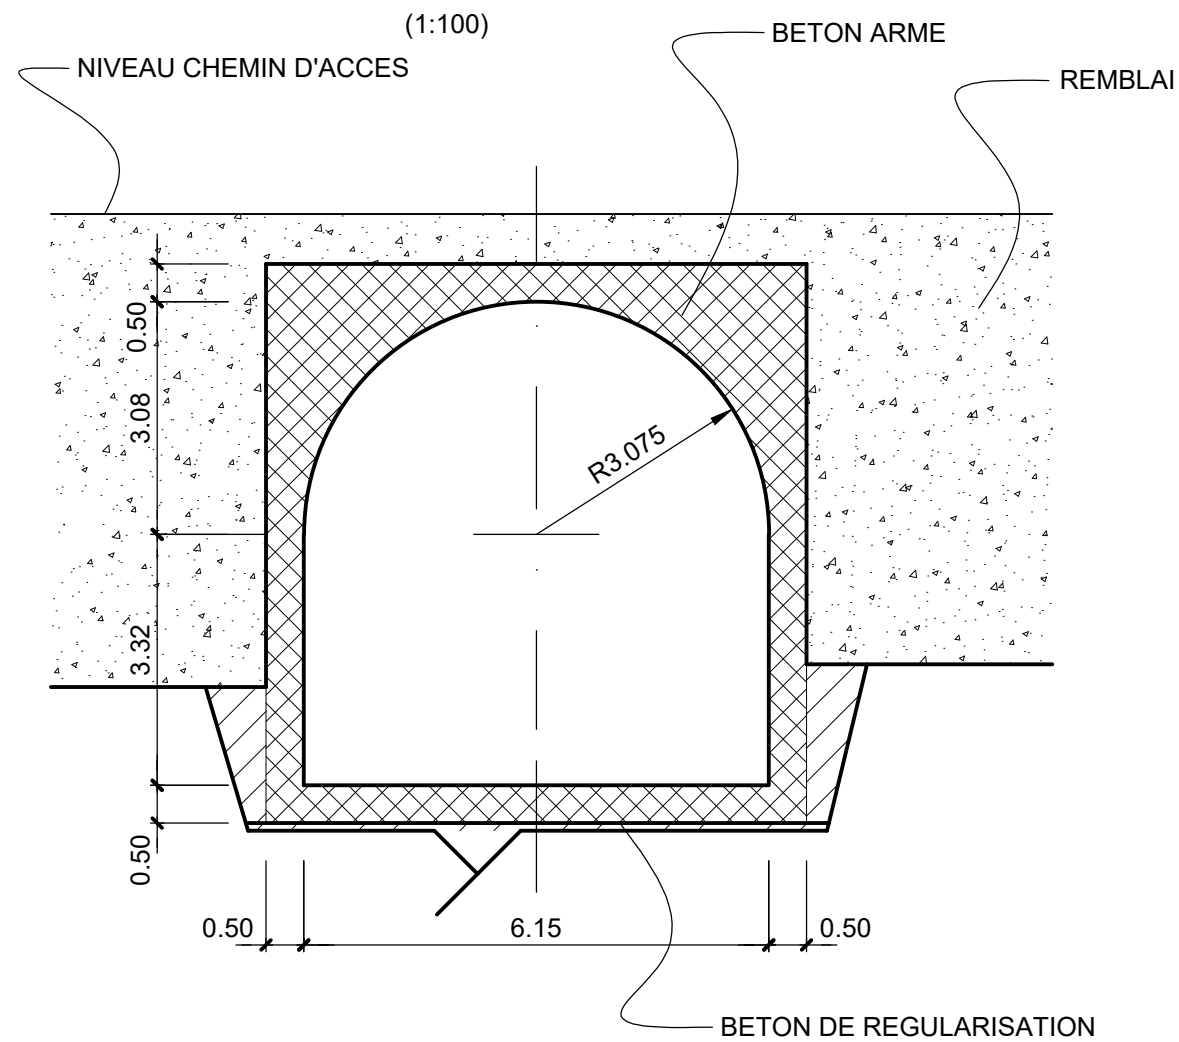

NOTES:

-BETON: TYPE C30/37

ECHELLE GRAPHIQUE : (1:100)

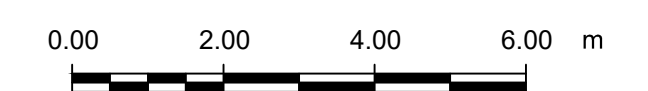

		LE GOUVERNEMENT DU GRAND-DUCHÉ DE LUXEMBOURG MINISTÈRE DE LA MOBILITÉ ET DES TRAVAUX PUBLICS ADMINISTRATION DES PONTS ET CHAUSSEES			
BARRAGE D'ESCH-SUR-SURE Evacuateur de crue complémentaire OA1158					
SOUSSION					
OUVRAGE DE RESTITUTION PROFIL LONGITUDINAL ET COUPES					
				C	
19.08.2019		LME	MID	MID	B
Date:	Dess.	Verif.	Appr.	Actualisation SEBES	
				Description modification	
09.06.2015		UP	Fel	BF	A1 (84 x 60)
Date:	Dess.	Verif.	Appr.	Dim. :	7500.4-P-323A
				Norm fichier	
Echelle : 1:100		No. Lo : 7500.4-P-323A		No. 48944	A