
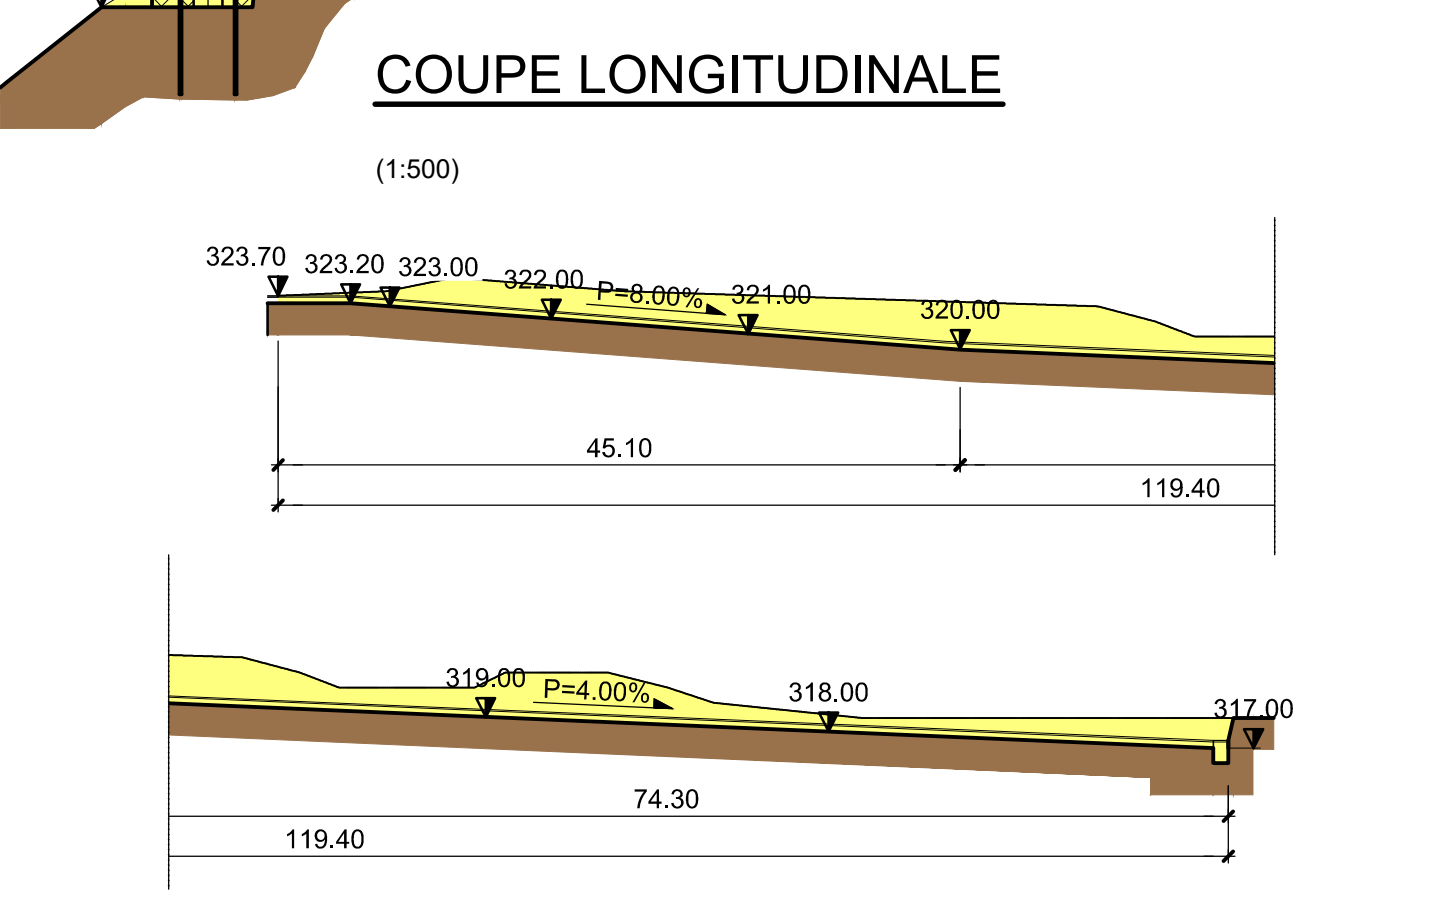
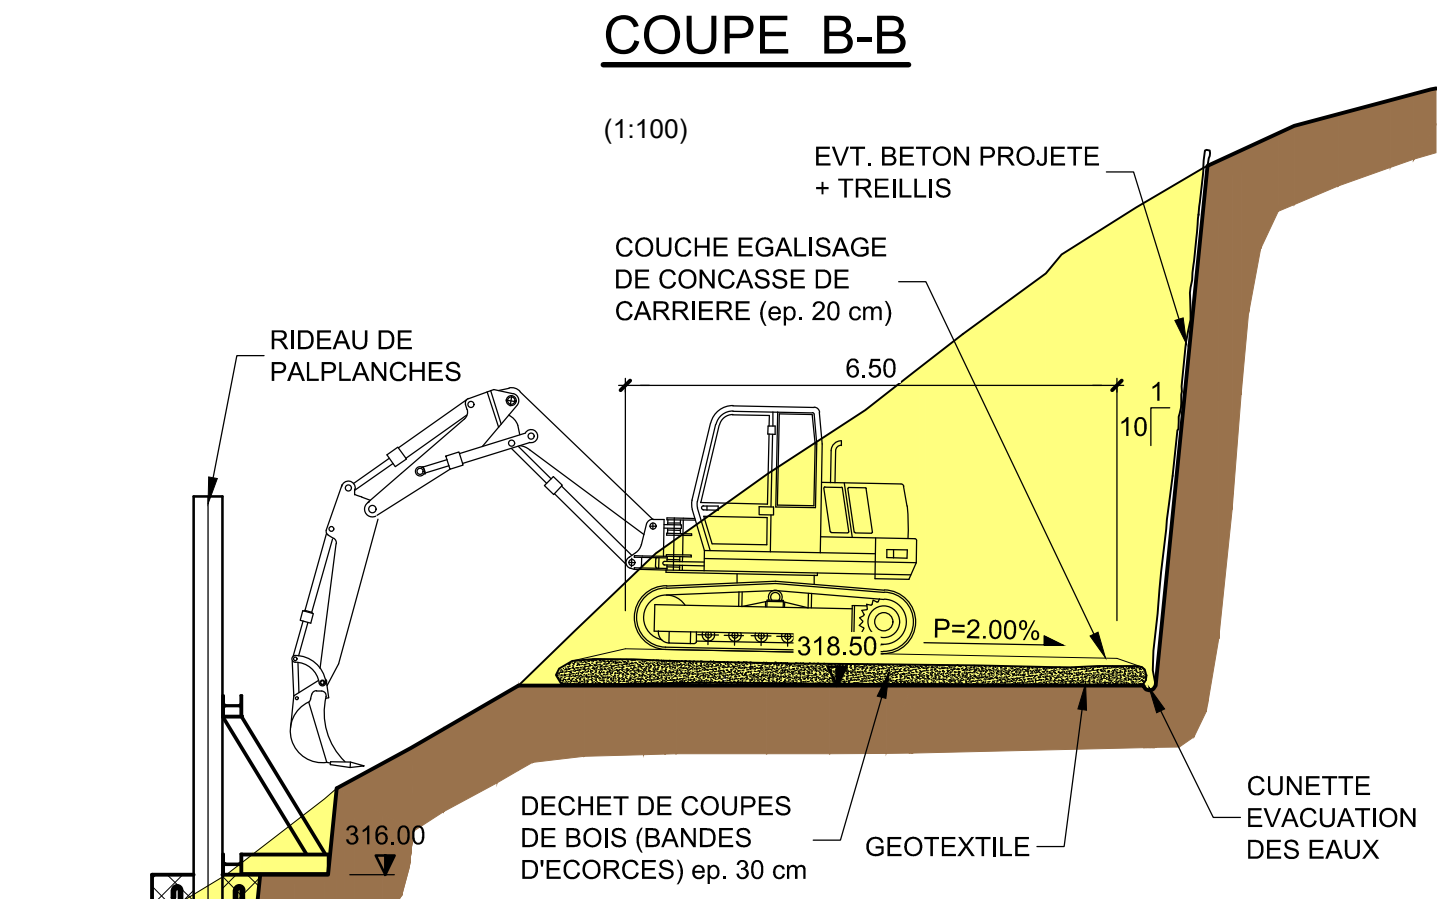
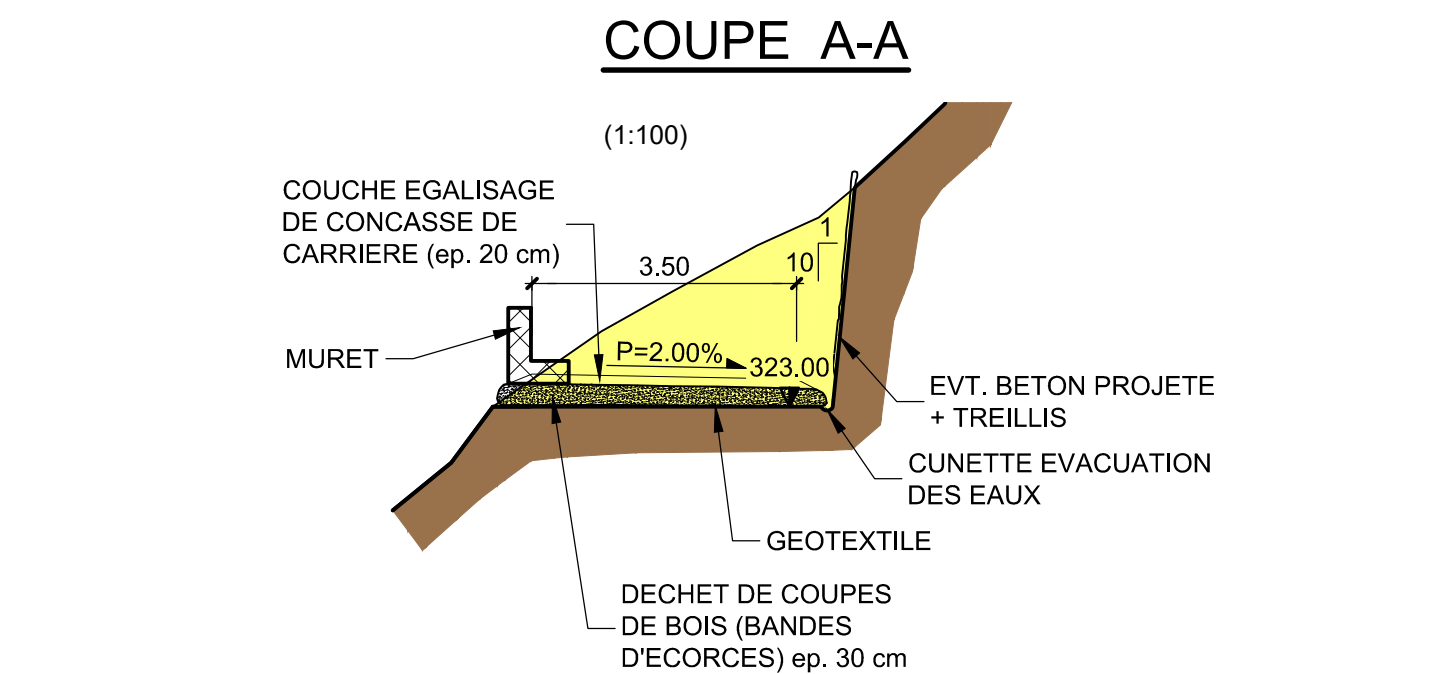
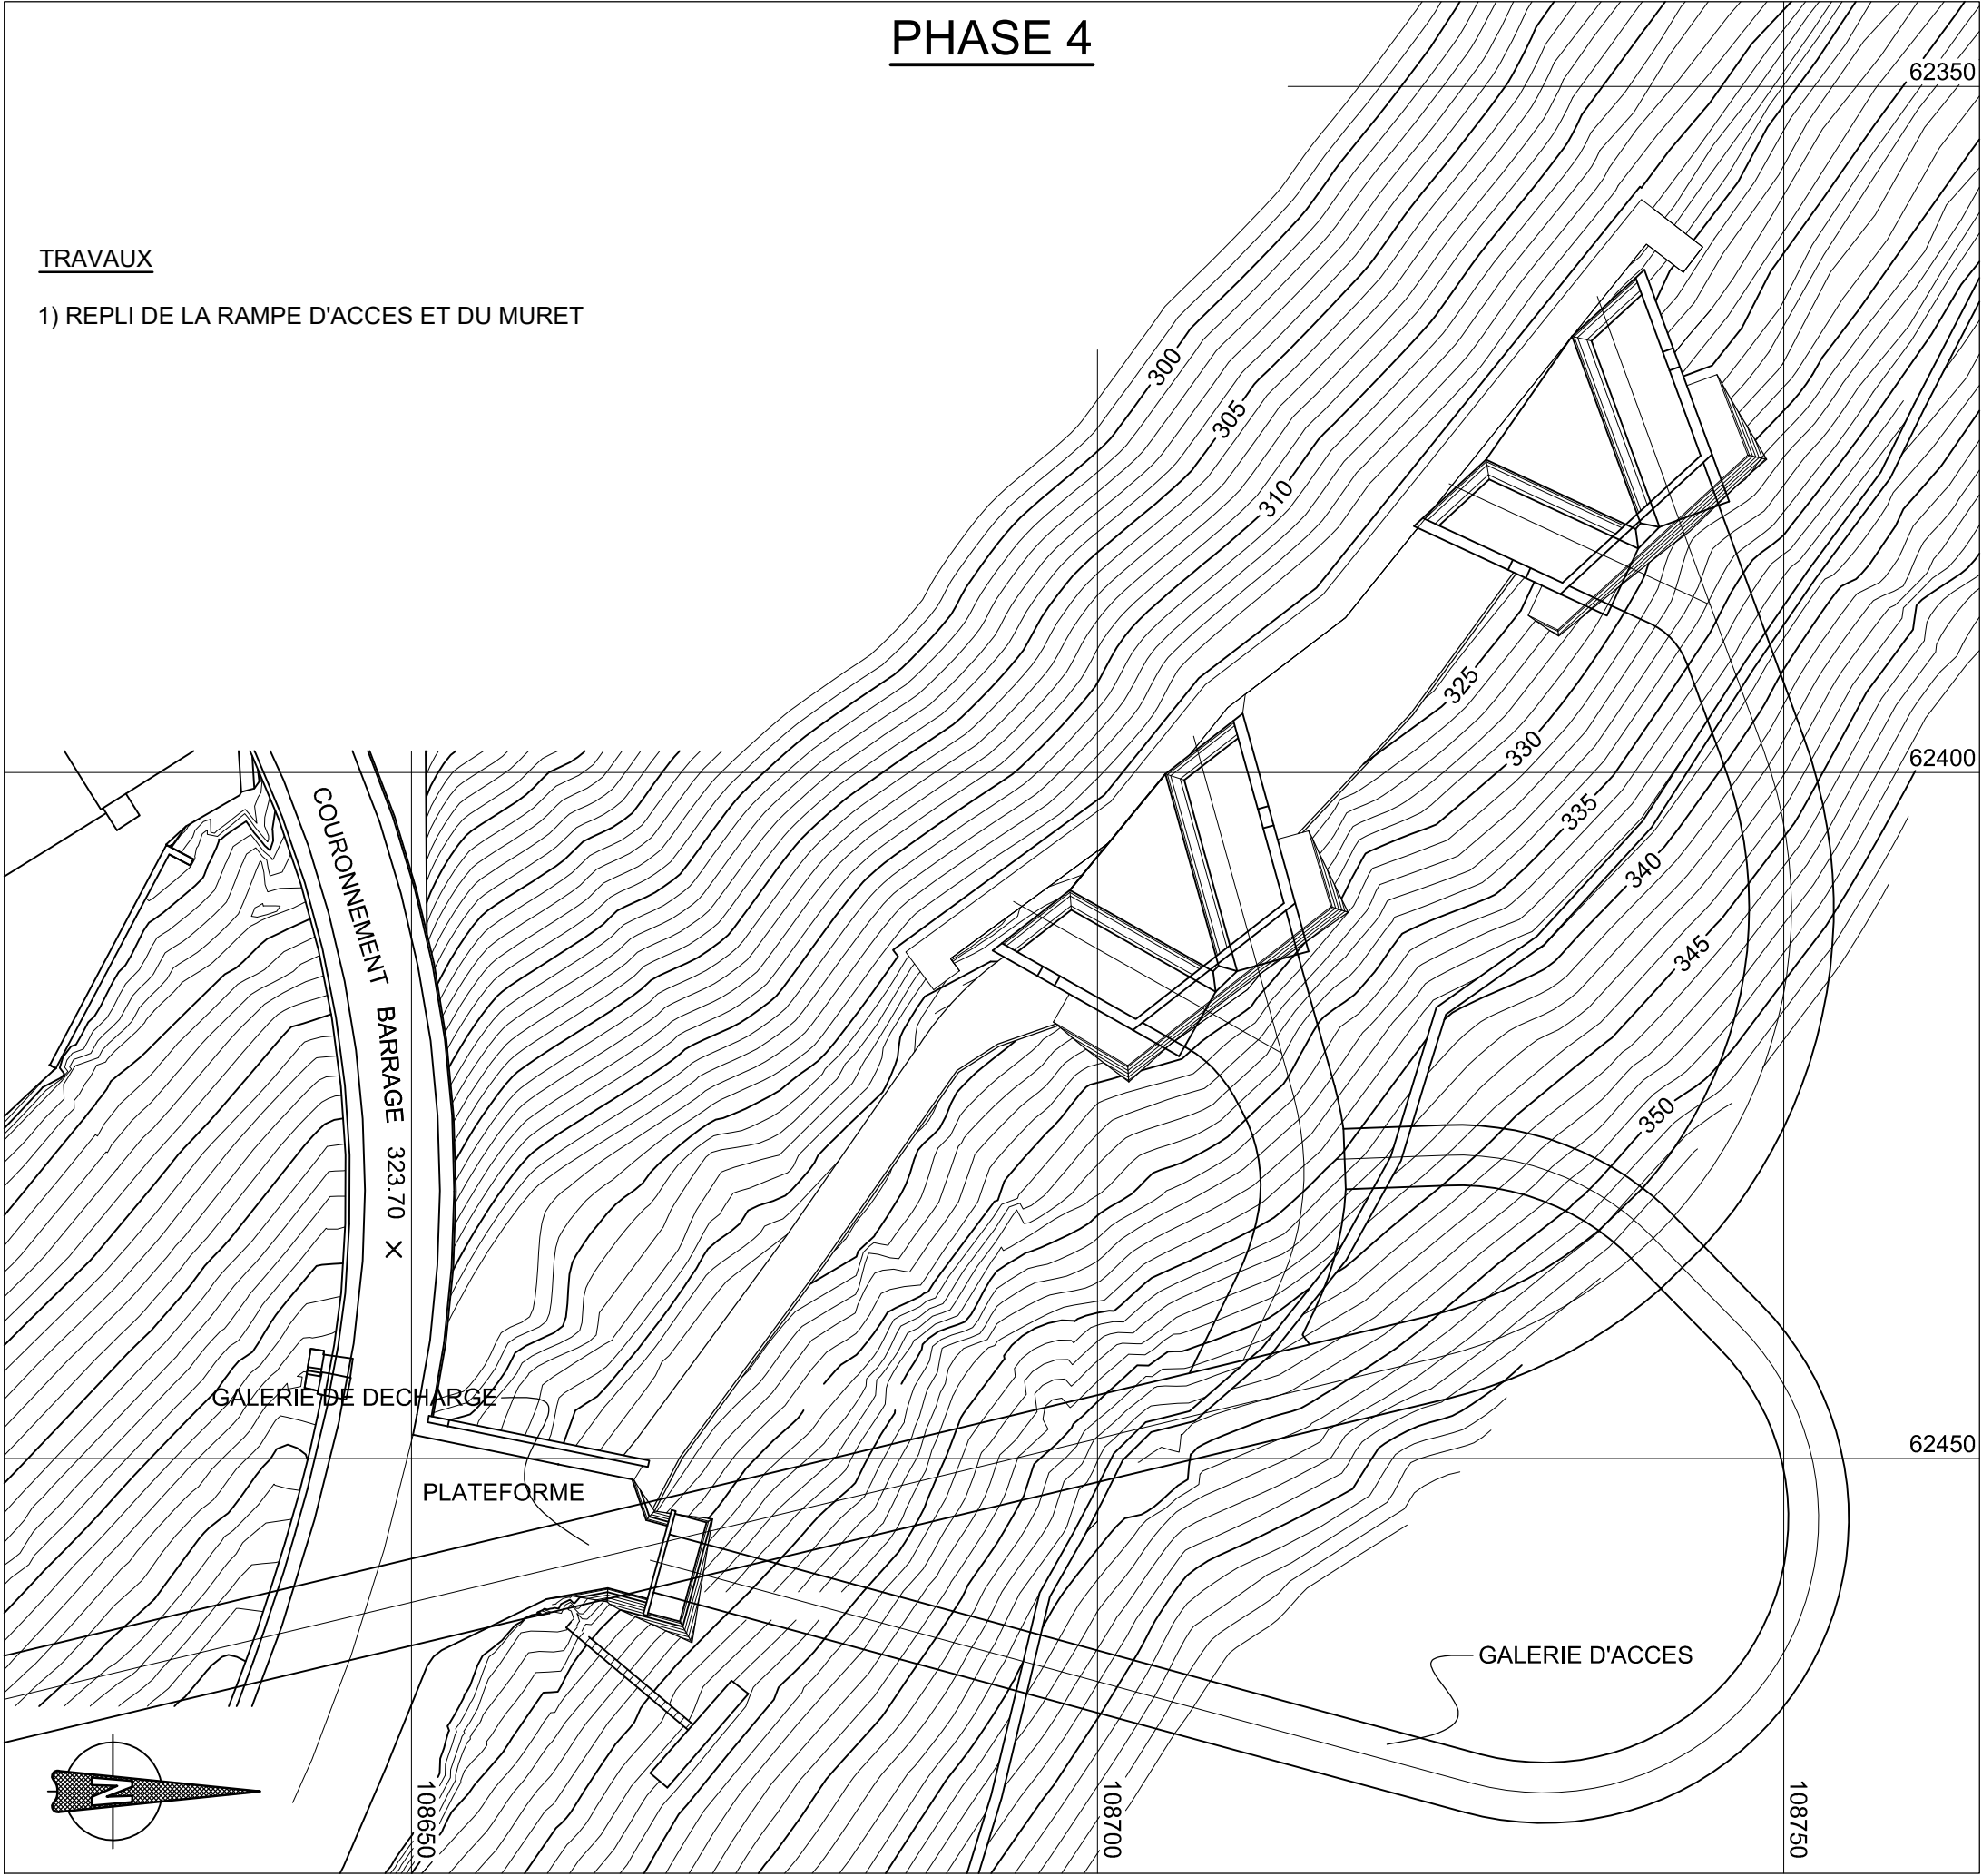
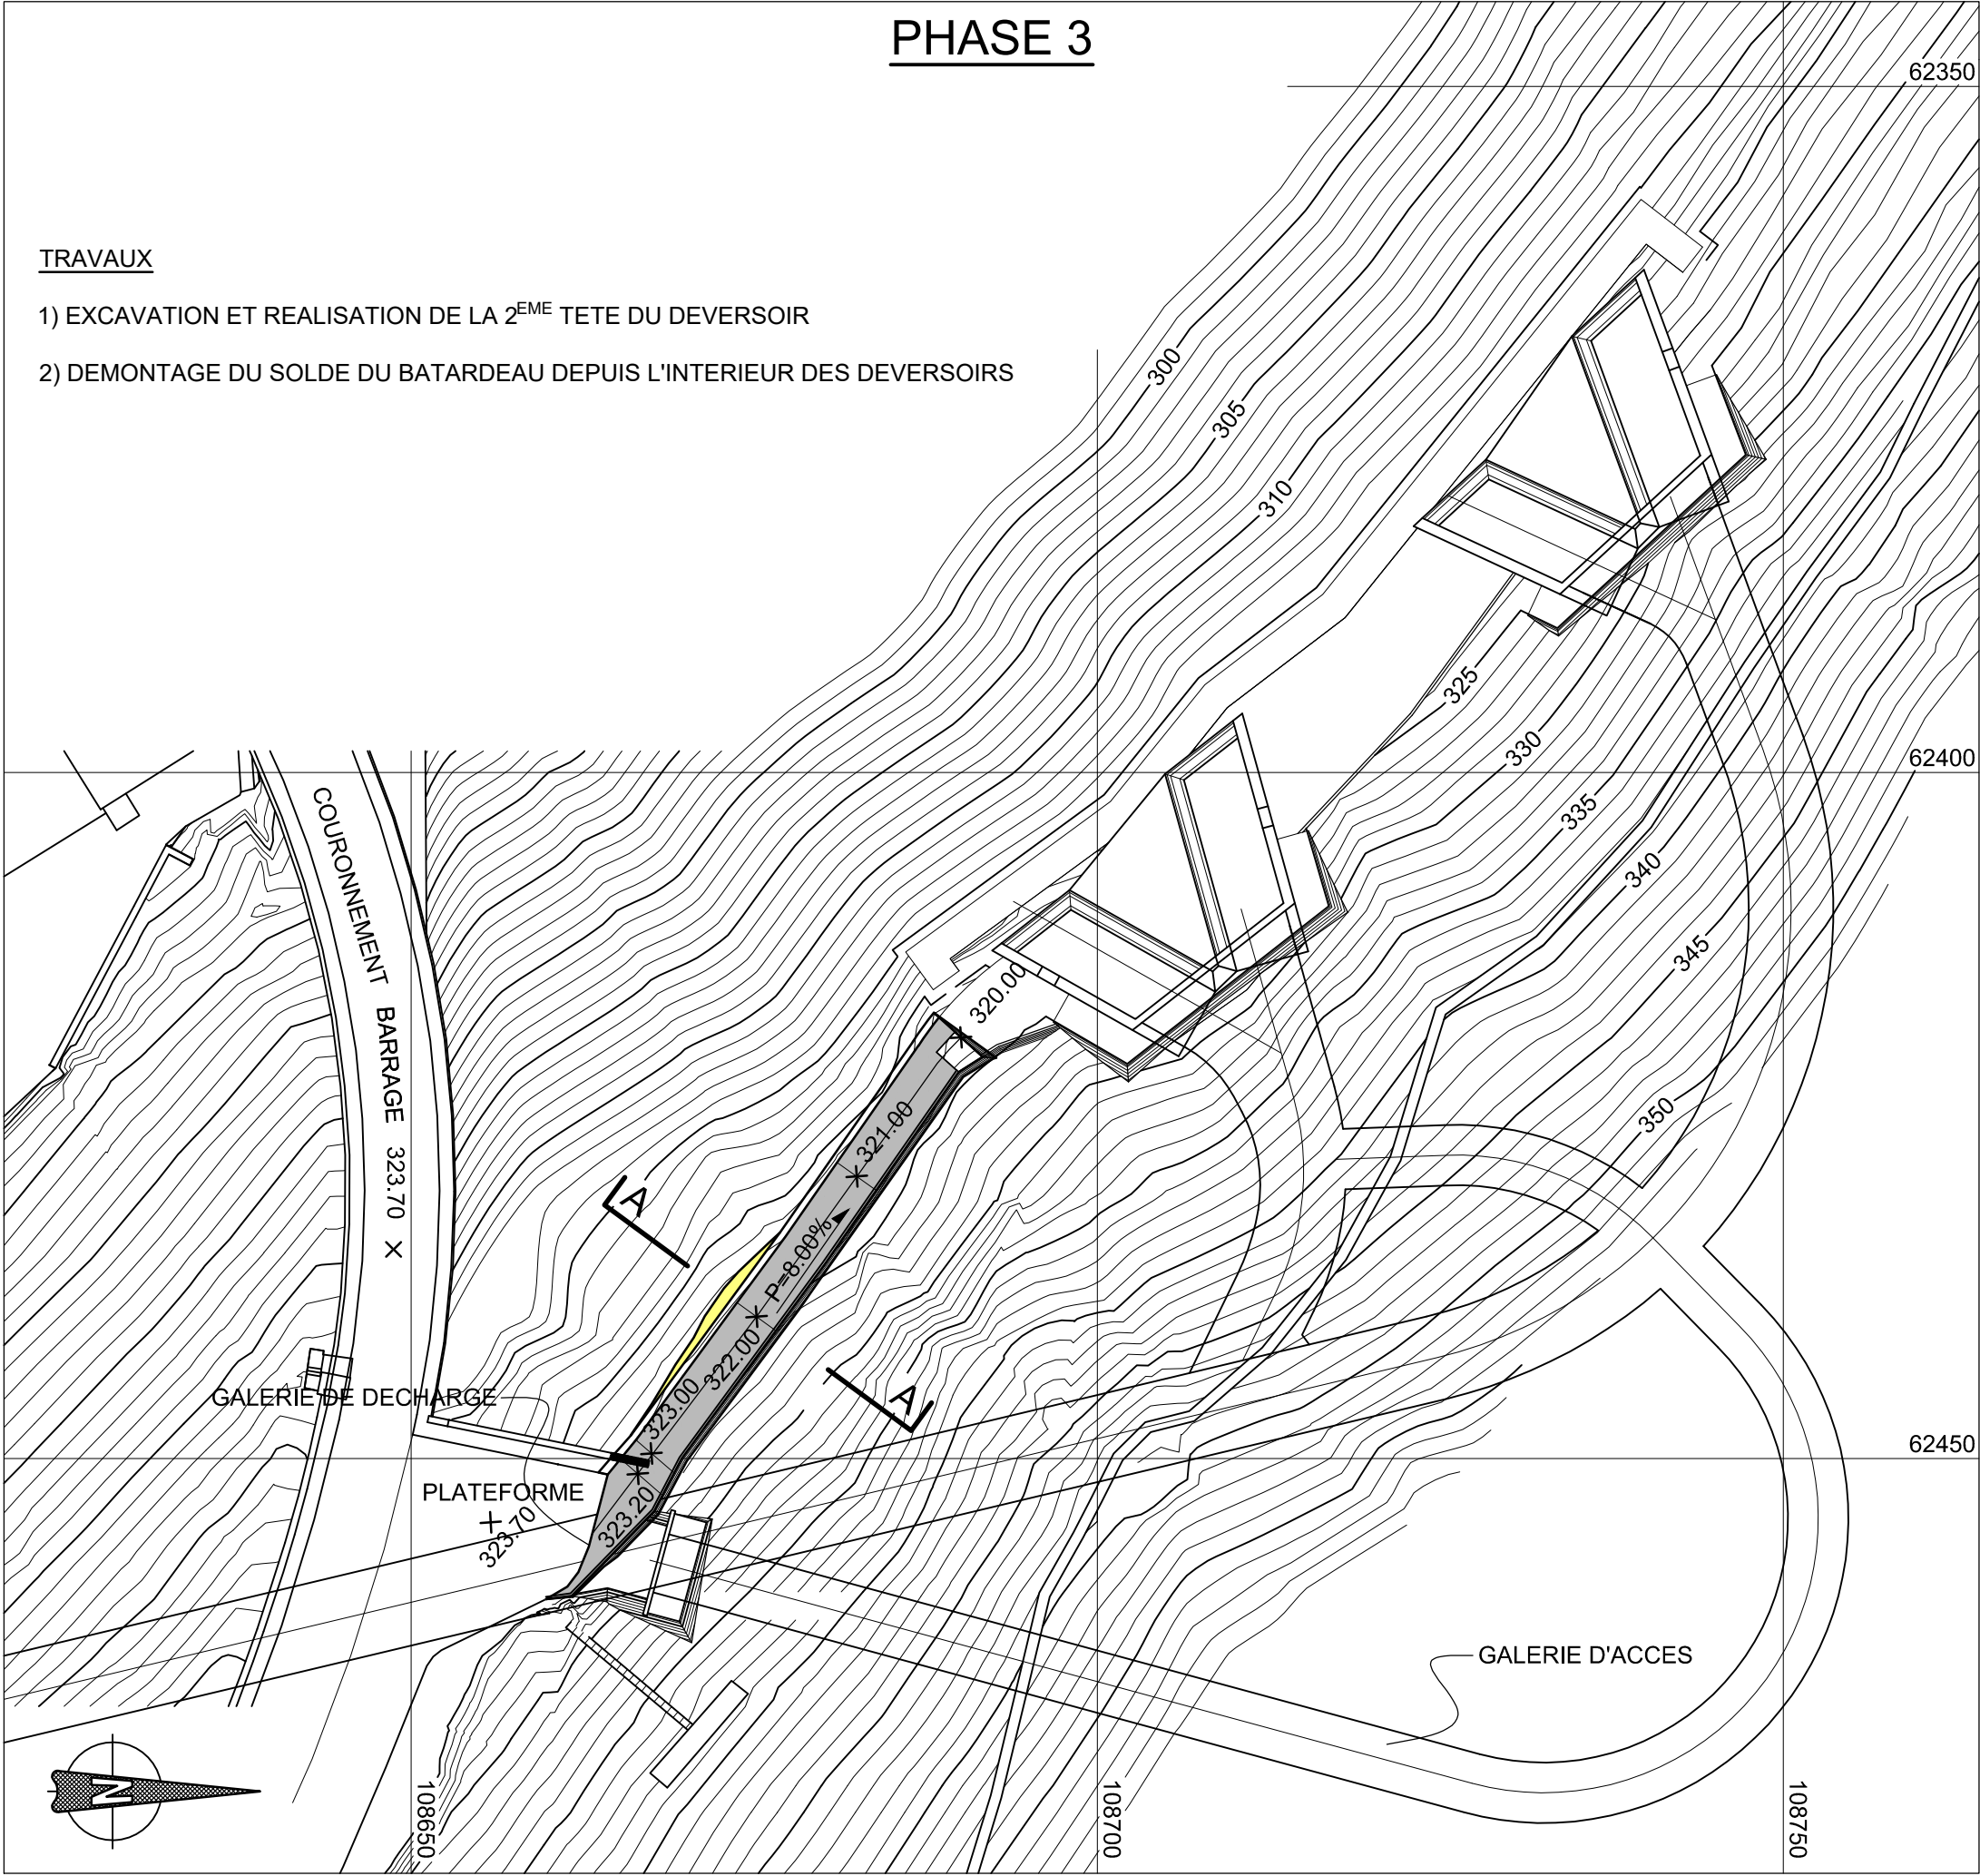
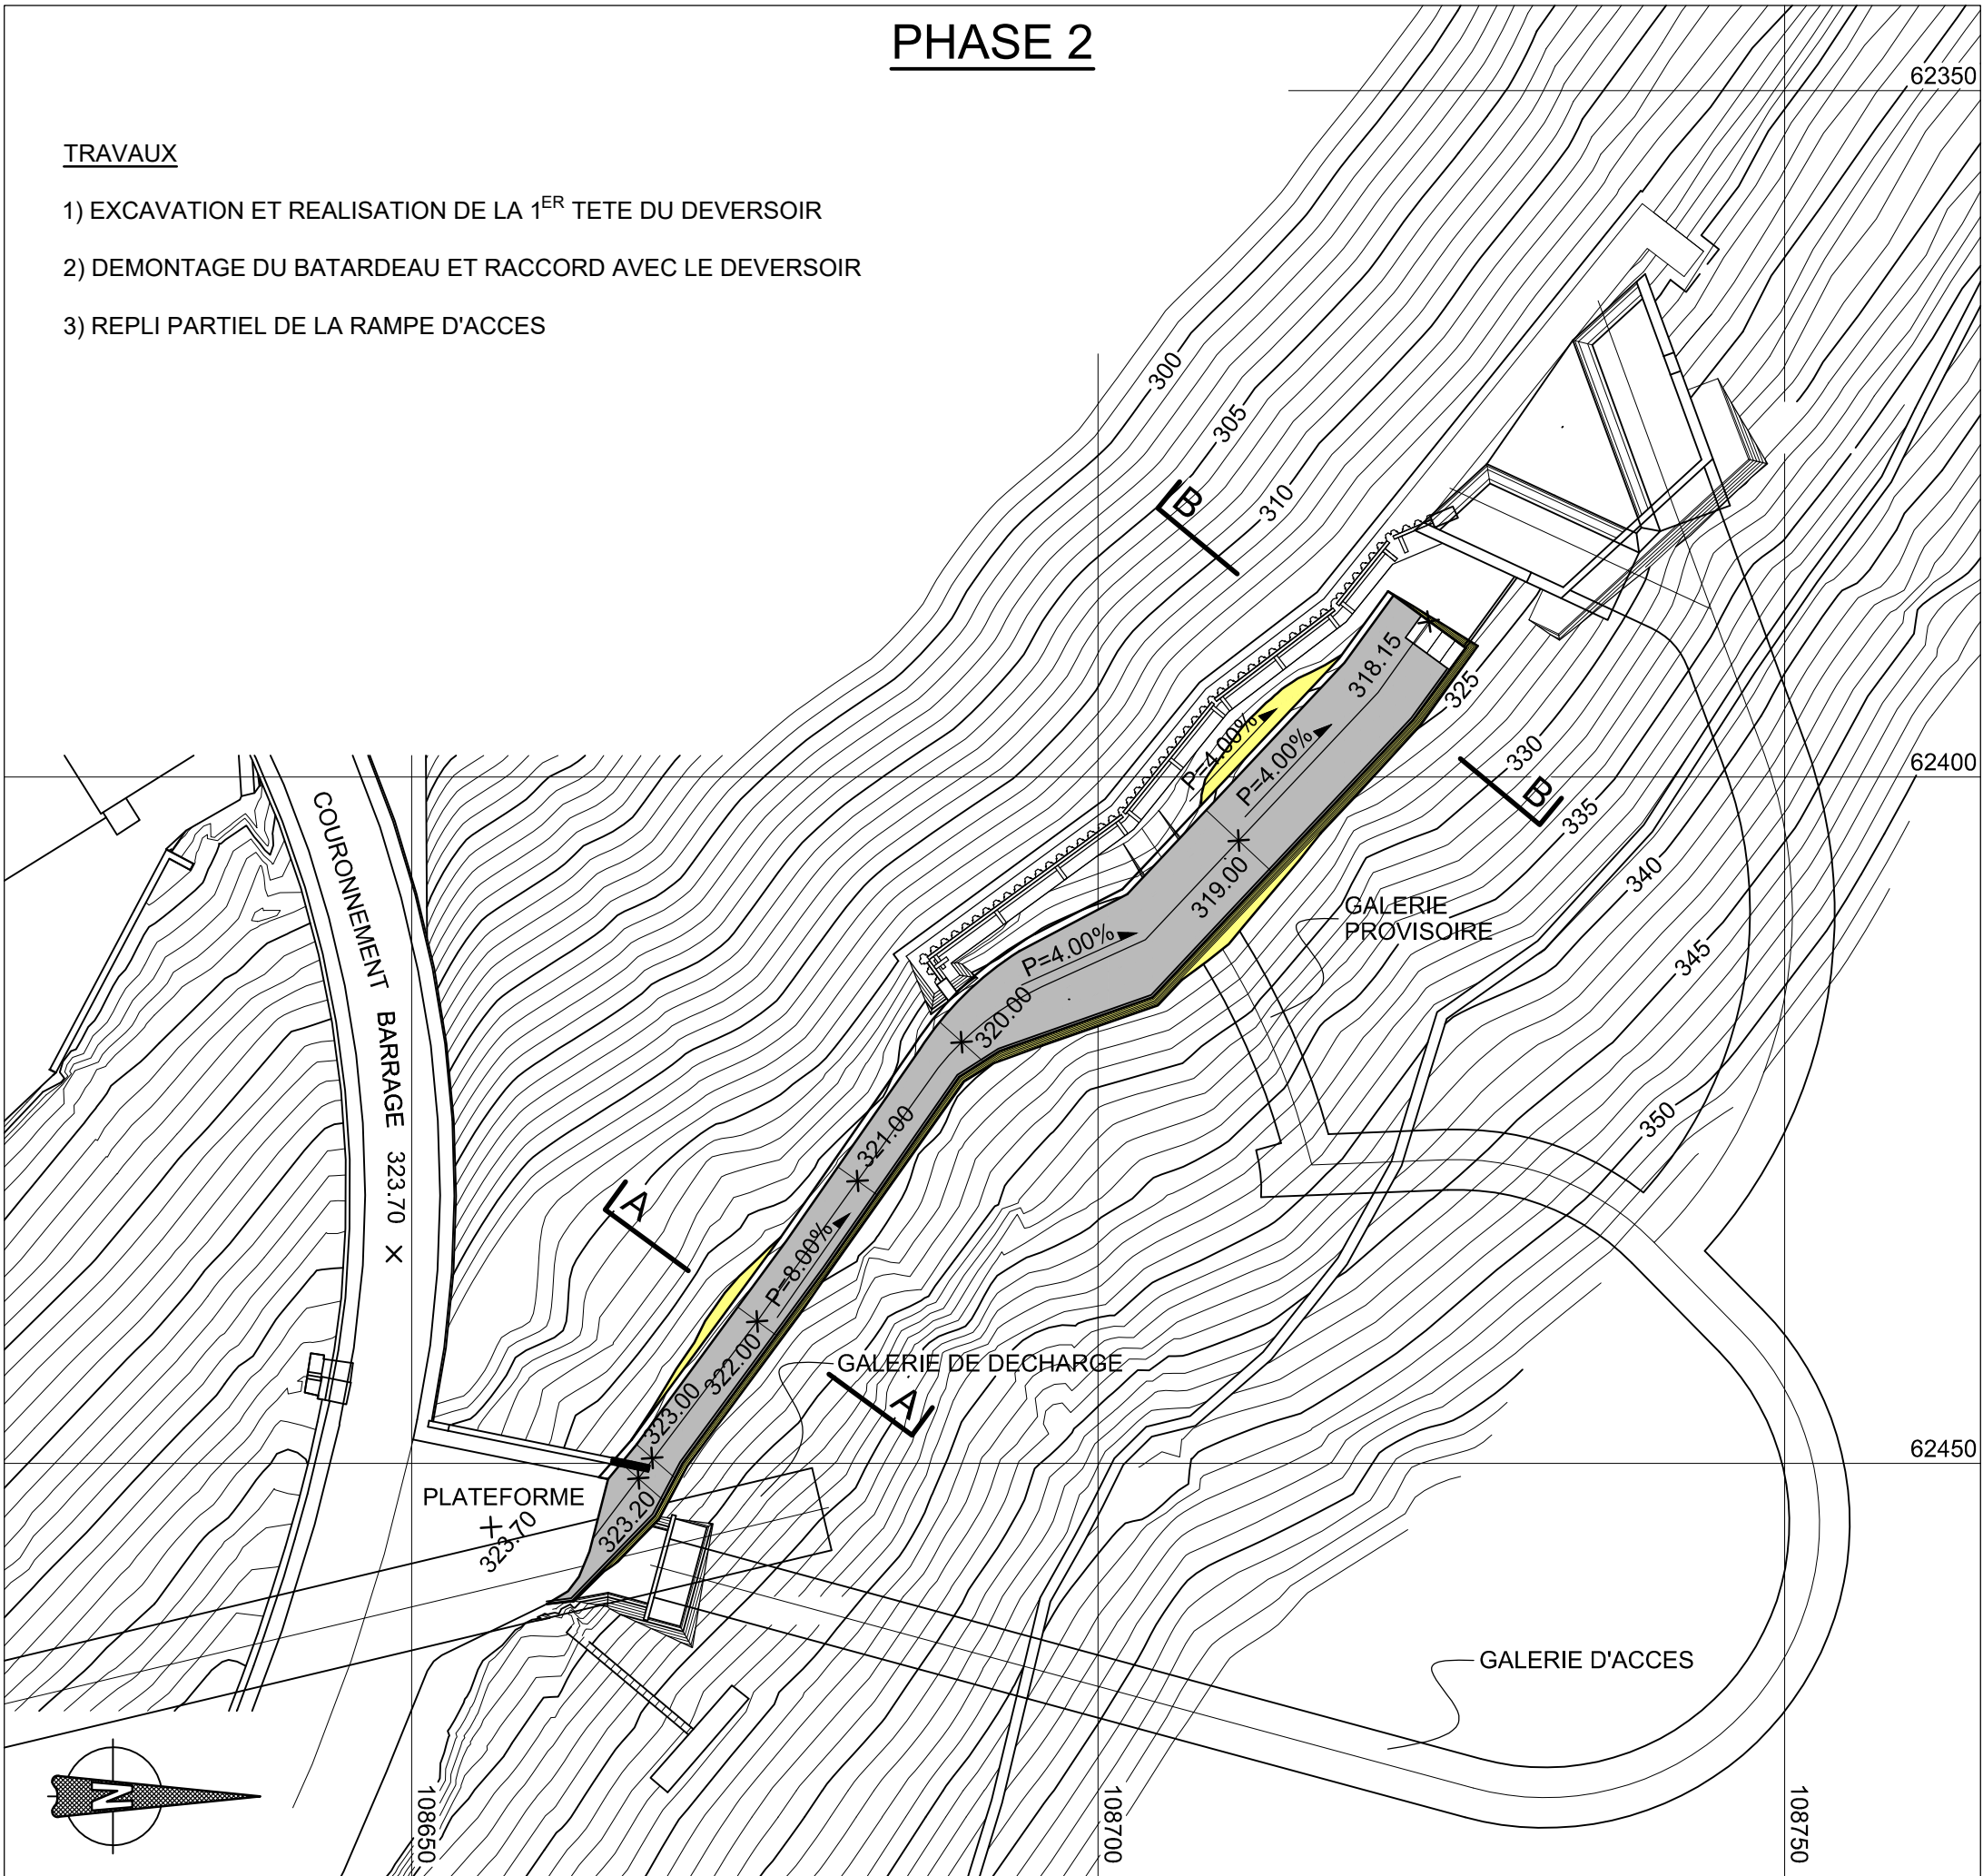


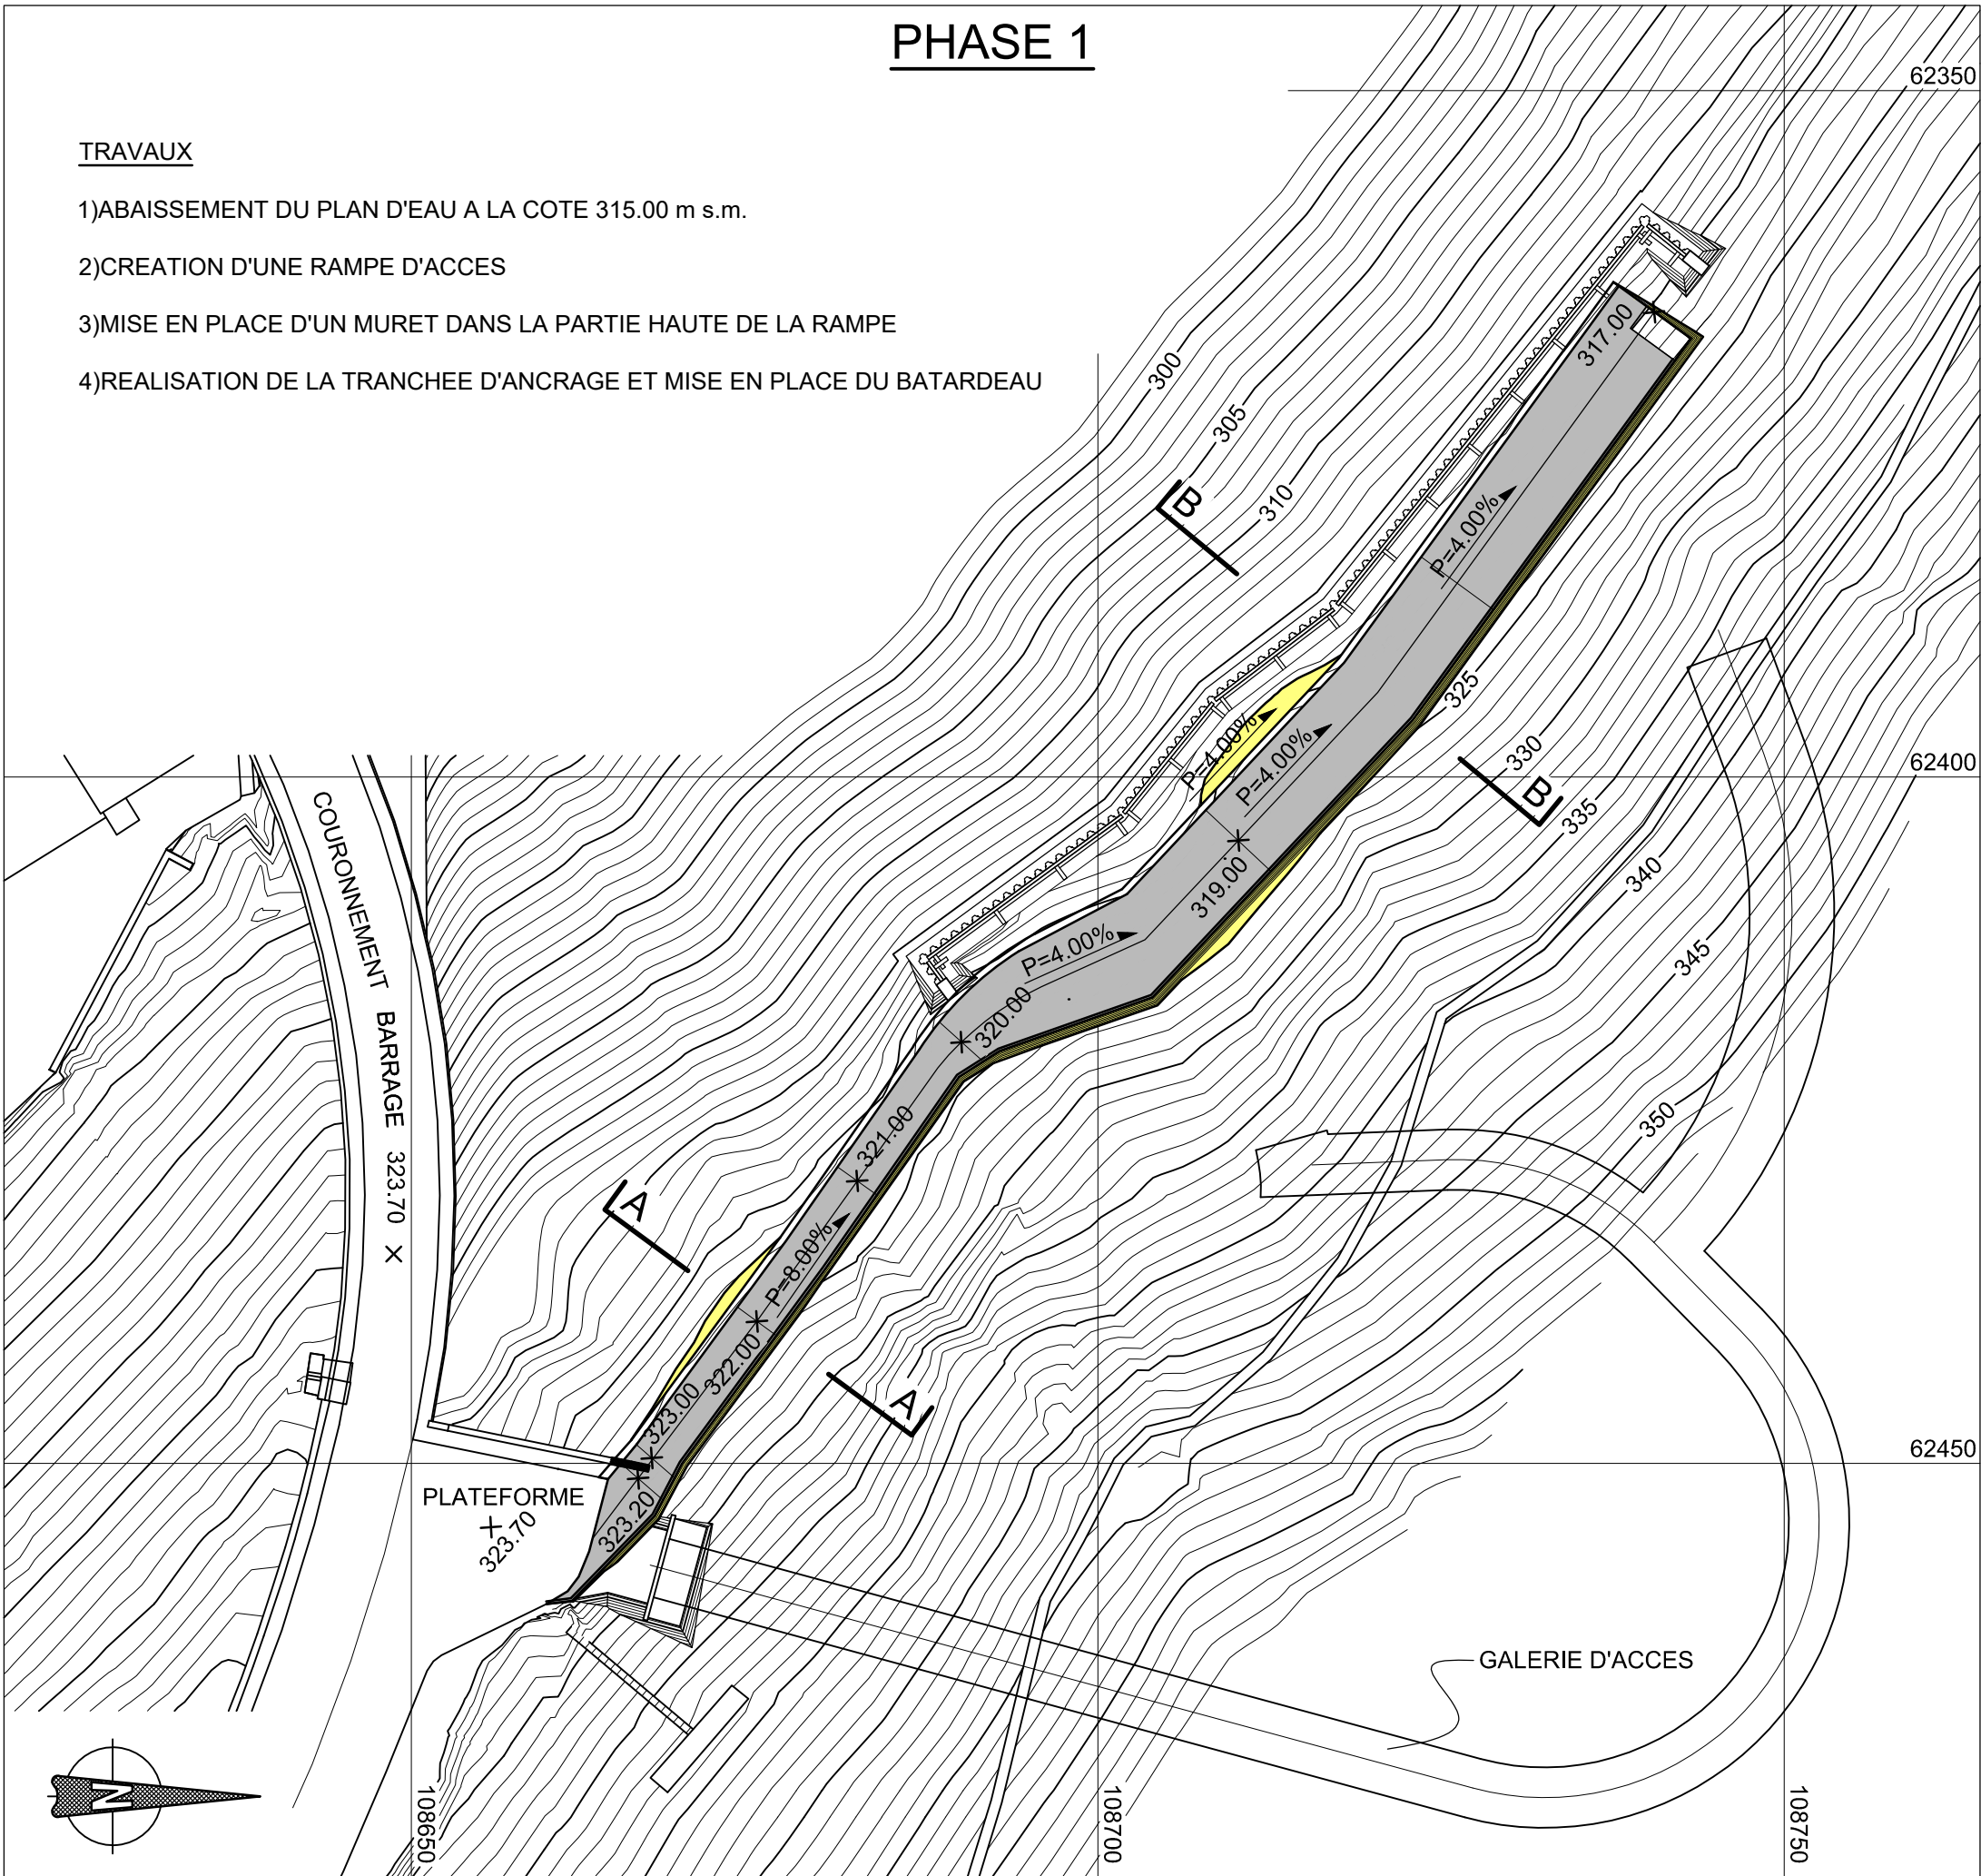

NOTES:

-LES DESSINS SONT ILLUSTRATIFS ET RENDENT COMPTE DE LA SITUATION A LA FIN DE CHAQUE PHASE

-LE RIDEAU DE PALPLANCHES CONTRIBUE EGALEMENT A PROTEGER LA RETENUE CONTRE TOUT RISQUE DE POLLUTION PENDANT LE CHANTIER

LEGENDE:

EXCAVATION

ECHELLE GRAPHIQUE :

(1:500)

0.00 10.00 20.00 30.00 m

(1:100)

0.00 2.00 4.00 6.00 m

REFERENCE:

-DEVERSOIRS LABYRINTHE PHASES PRINCIPALES DES TRAVAUX EN COUPE VOIR PLAN N.° 48949

LE GOUVERNEMENT DU GRAND-DUCHE DE LUXEMBOURG

MINISTRE DE LA MOBILITE ET DES TRAVAUX PUBLICS

ADMINISTRATION DES PONT ET CHAUSSÉES

Lombardi

BARRAGE D'ESCH-SUR-SURE

Evacuateur de crue complémentaire OA1158

SOUSSION

DEVERSOIRS LABYRINTHE

PHASES PRINCIPALES DES TRAVAUX EN SITUATION

Date	Dess.	Verif.	Appr.	Description	Modif.
10.04.2018	Ka	Fel	La	Modification concept	A
09.06.2015	UP	Fel	BF	A1 (84 x 60)	7500.4-P-333A
Date	Dess.	Verif.	Appr.	Dim. :	Nom fichier

Echelle : 1:500, 1:100

No. Lo : 7500.4-P-333A

No. 48948

A