


Coordonnées		
Point	Est [m]	Nord [m]
P1	62517	108488
P2	62533	108501
P3	62494	108549
P4	62488	108577
P5	62475	108573
P6	62457	108588
P7	62442	108574
P8	62462	108657
P9	62469	108674
P10	62447	108677
P11	62422	108695
P12	62428	108702
P13	62411	108723
P14	62403	108719
P15	62392	108729
P16	62395	108734
P17	62379	108753
P18	62361	108748
P19	62354	108739
P20	62411	108684
P21	62449	108660

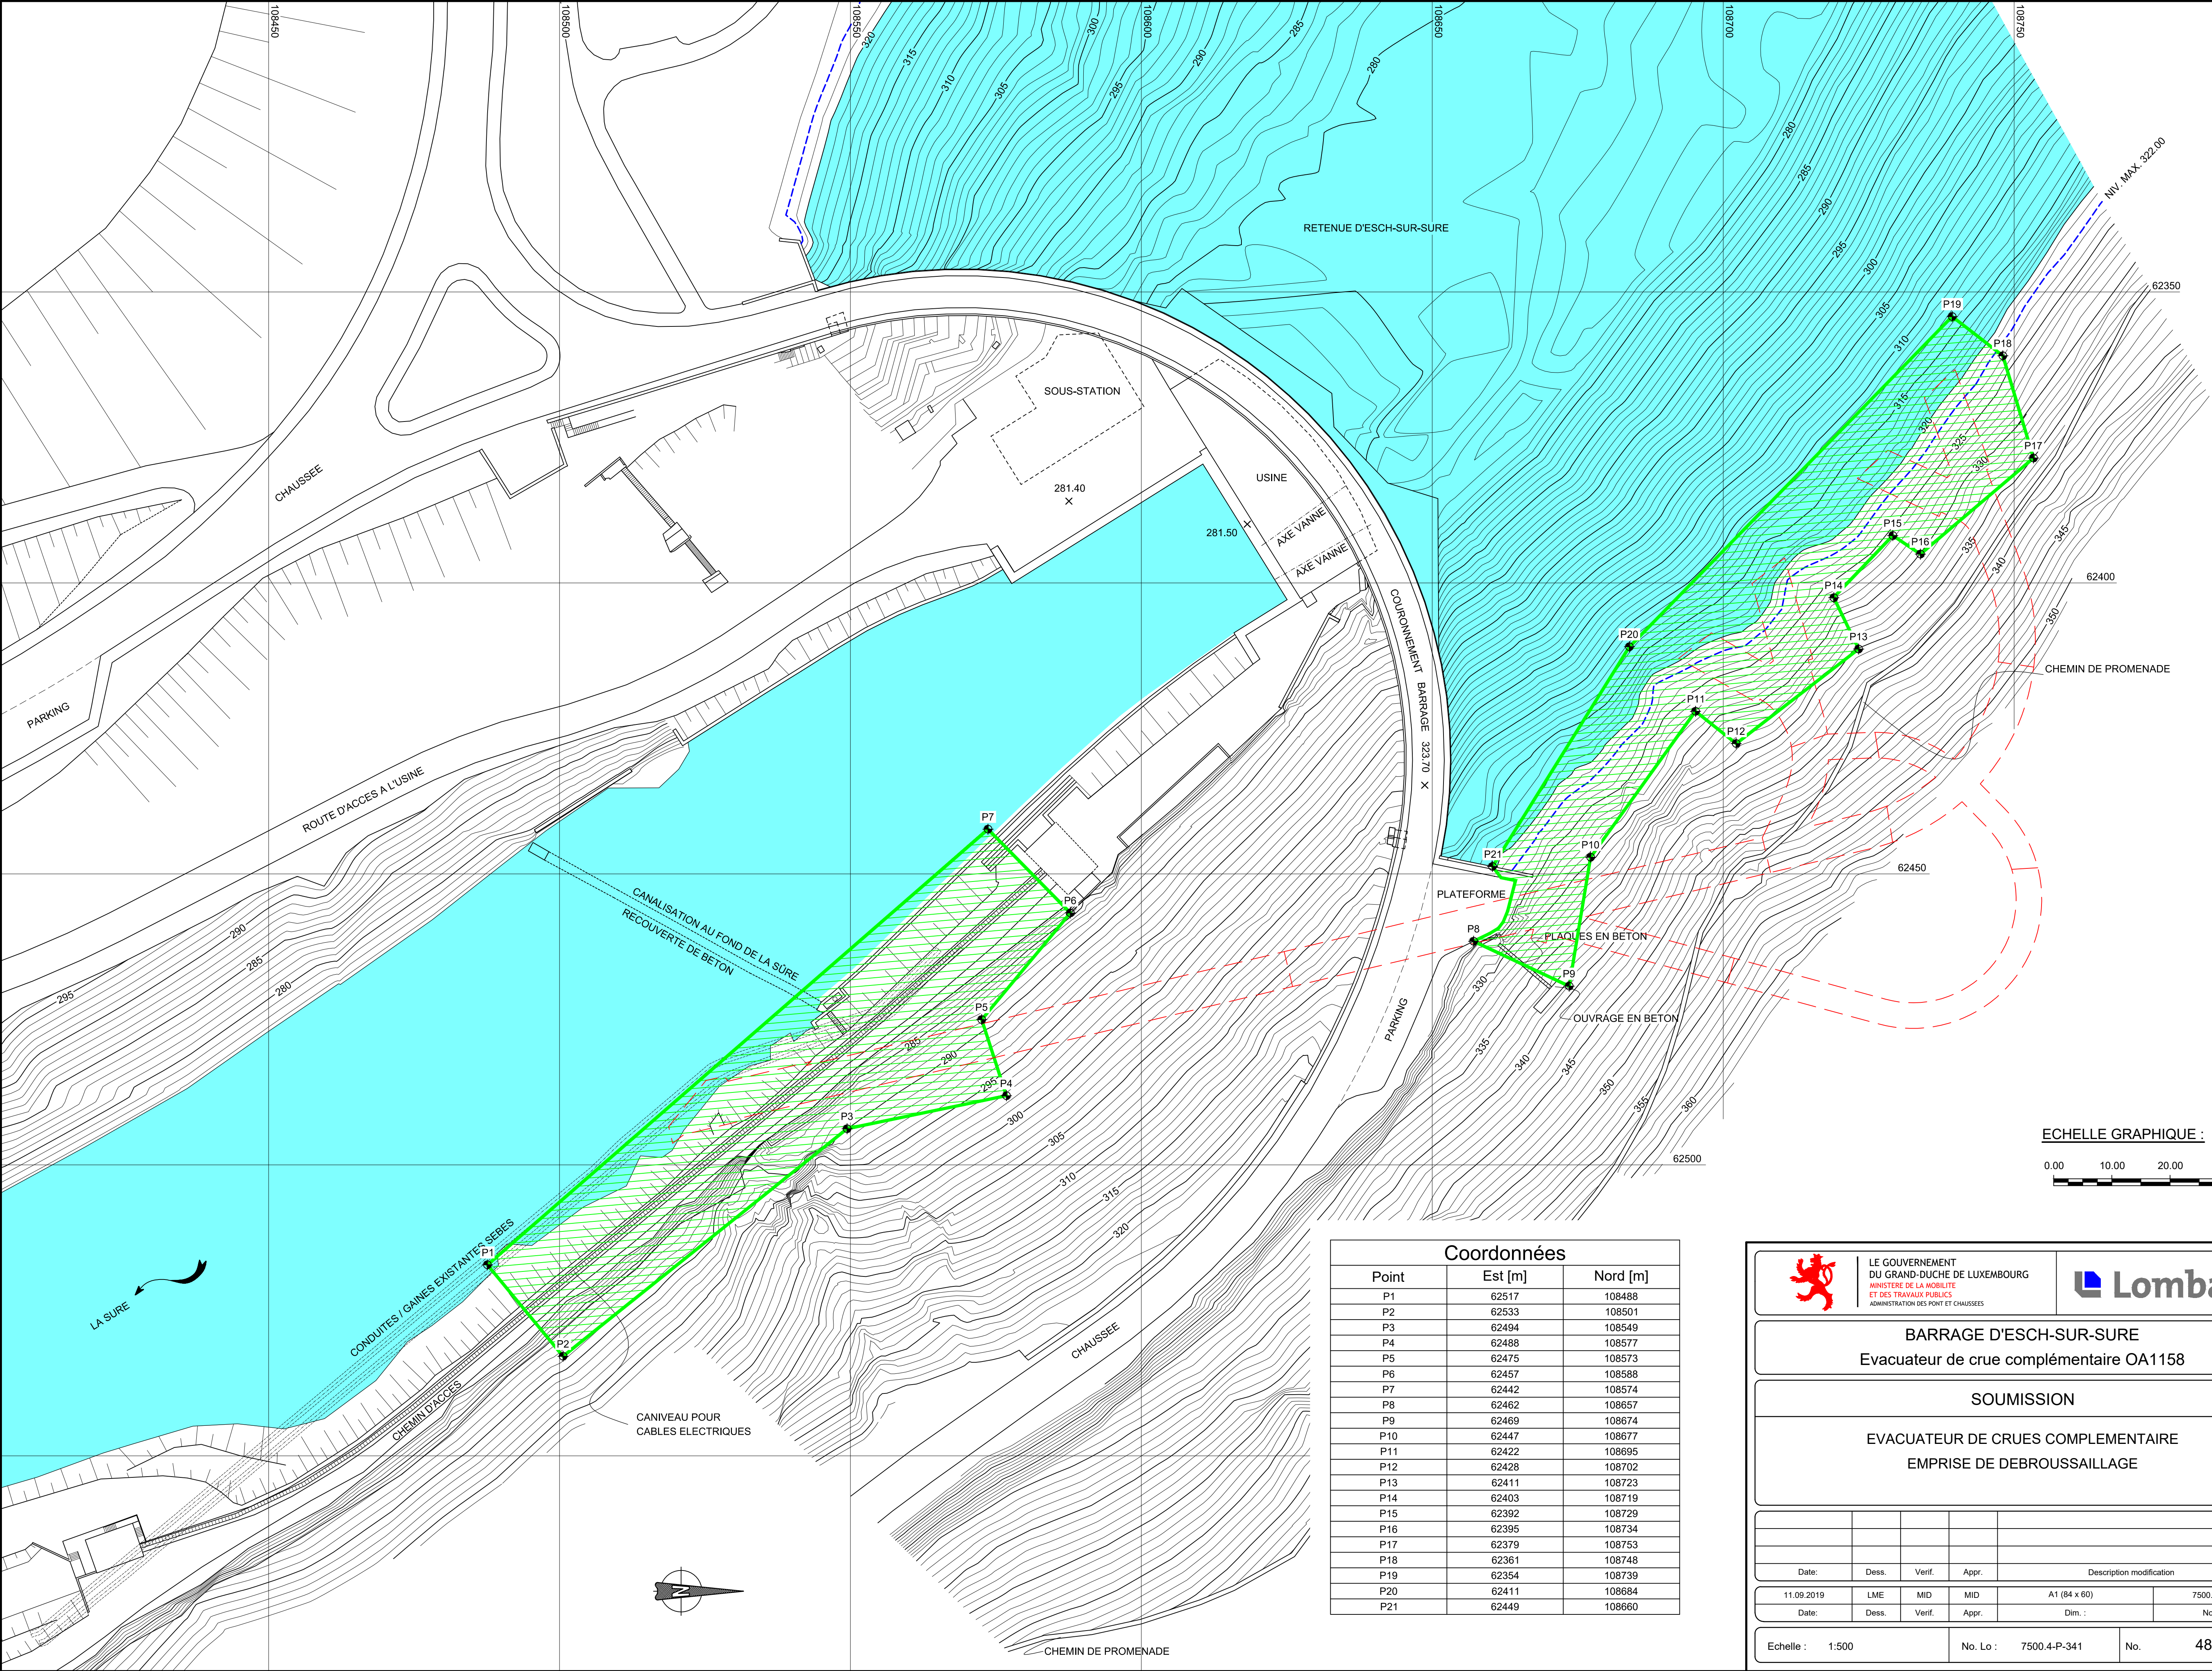

LE GOUVERNEMENT
DU GRAND-DUCHÉ DE LUXEMBOURG
MINISTÈRE DE LA MOBILITÉ
ET DES TRAVAUX PUBLICS
ADMINISTRATION DES PONTS ET CHAUSSÉES



BARRAGE D'ESCH-SUR-SÛRE

Evacuateur de crue complémentaire OA1158

SOUSSION

EVACUATEUR DE CRUES COMPLEMENTAIRE

EMPRISE DE DEBROUSSAILLAGE

					C
					B
					A
Date:	Dess.	Verif.	Appr.	Description modification	
11.09.2019	LME	MID	MID	A1 (84 x 60)	7500.4-P-341
Date:	Dess.	Verif.	Appr.	Dim. :	Nom fichier
Echelle :	1:500	No. Lo :	7500.4-P-341	No.	48953