


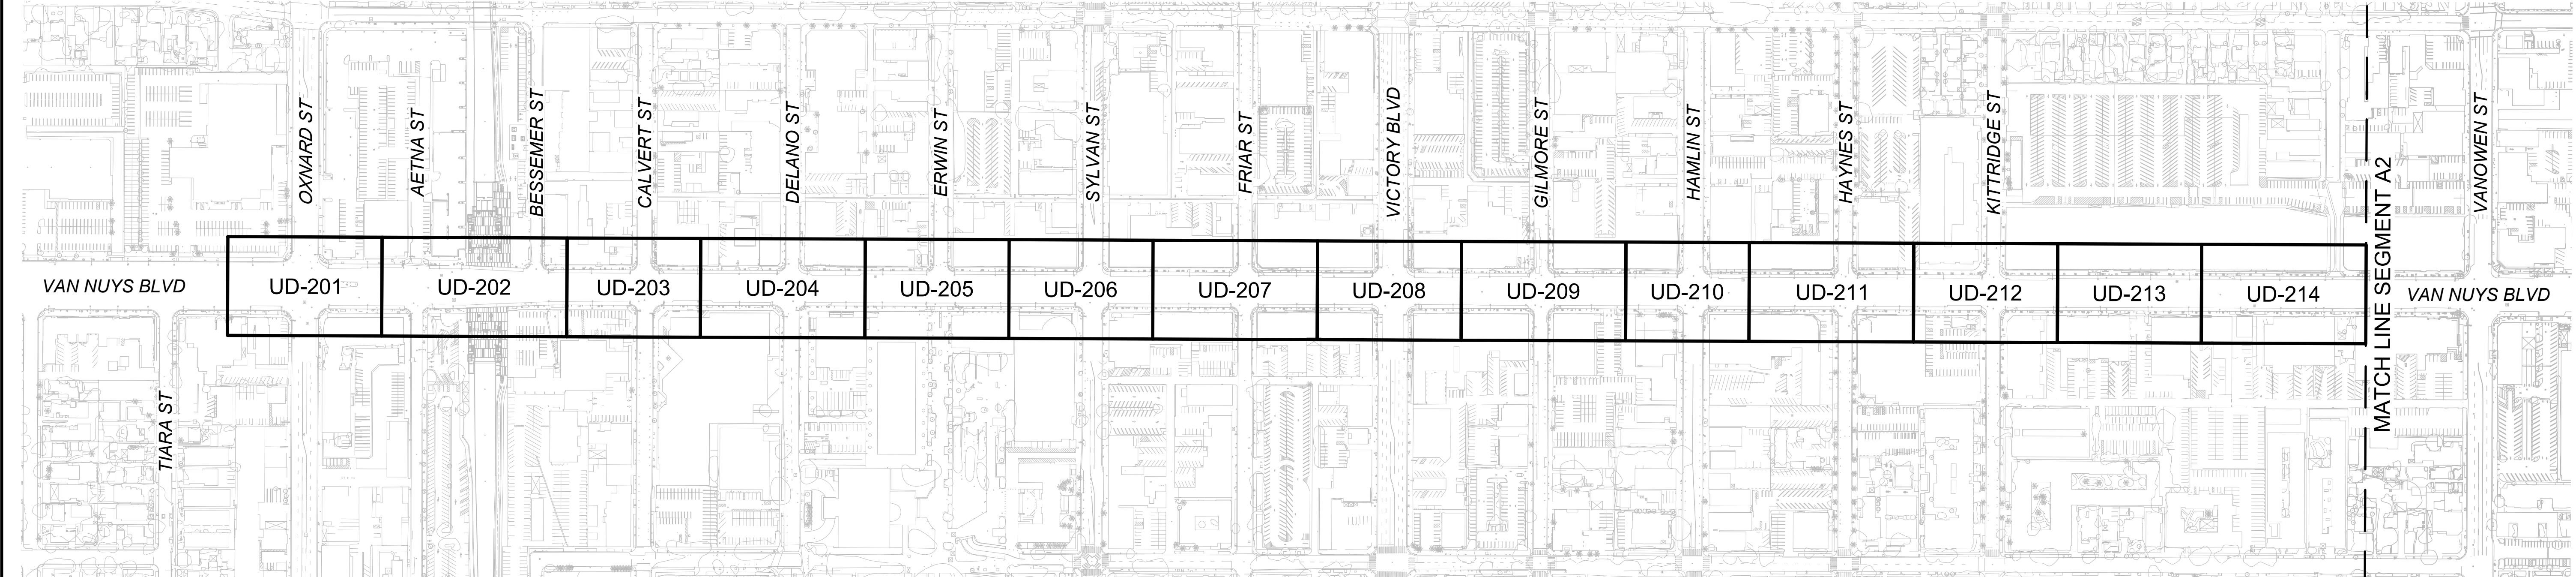


KEY MAP - SEGMENT A1



THE PREPARATION OF THIS DRAWING HAS BEEN FINANCED IN PART THROUGH A GRANT FROM THE U.S. DEPARTMENT OF TRANSPORTATION, FEDERAL TRANSIT ADMINISTRATION (FTA) UNDER THE FEDERAL TRANSIT ACT OF 1964, AS AMENDED, AND IN PART BY THE TAXES OF THE CITIZENS OF LOS ANGELES COUNTY AND OF THE STATE OF CALIFORNIA.										DESIGNED BY N. SOTO		M Metro San Fernando Transit Constructors 14300 ARMINTA ST. LOS ANGELES, CA 91402 TEL: 951.684.5360	LOS ANGELES COUNTY METROPOLITAN TRANSPORTATION AUTHORITY		100% SUBMITTAL - NOT FOR CONSTRUCTION V&A INC 1111 S. GRAND AVE. SUITE 103 LOS ANGELES, CA 90015 213.922.0700	EAST SAN FERNANDO VALLEY LRT DU06 - CIVIL SEGMENT A1		CONTRACT NO PS89616000					
										DRAWN BY R. VENEGAS			DRAWING NO UD-202-G			REV							
										CHECKED BY N. BUSCH			SCALE NO SCALE			SHEET NO							
										IN CHARGE N. BUSCH													
REV	DATE	BY	APP	REG NO	EXPIRES	SEAL HOLDER	DESCRIPTION	DATE 12/11/2025															
C	12/15/25	NS	JR	C78082	09/30/27	J. RIMORIN	100% SUBMITTAL																
B	08/18/25	AR	NB	C65608	09/30/27	N.BUSCH	85% SUBMITTAL																
A	03/07/25	KM	JR	C78082	09/30/27	J. RIMORIN	60% SUBMITTAL																

FILE PATH: \\80724957-ESFV-PH2\PROJECT FILES\900_CAD\20_SHEETS\DU06\09_UD_DRAINAGE\PS89616000-DU06-UD-202-G.DWG
PLOT DATE: 12/16/2025 - 9:56 AM USER: ADRIANROBLES

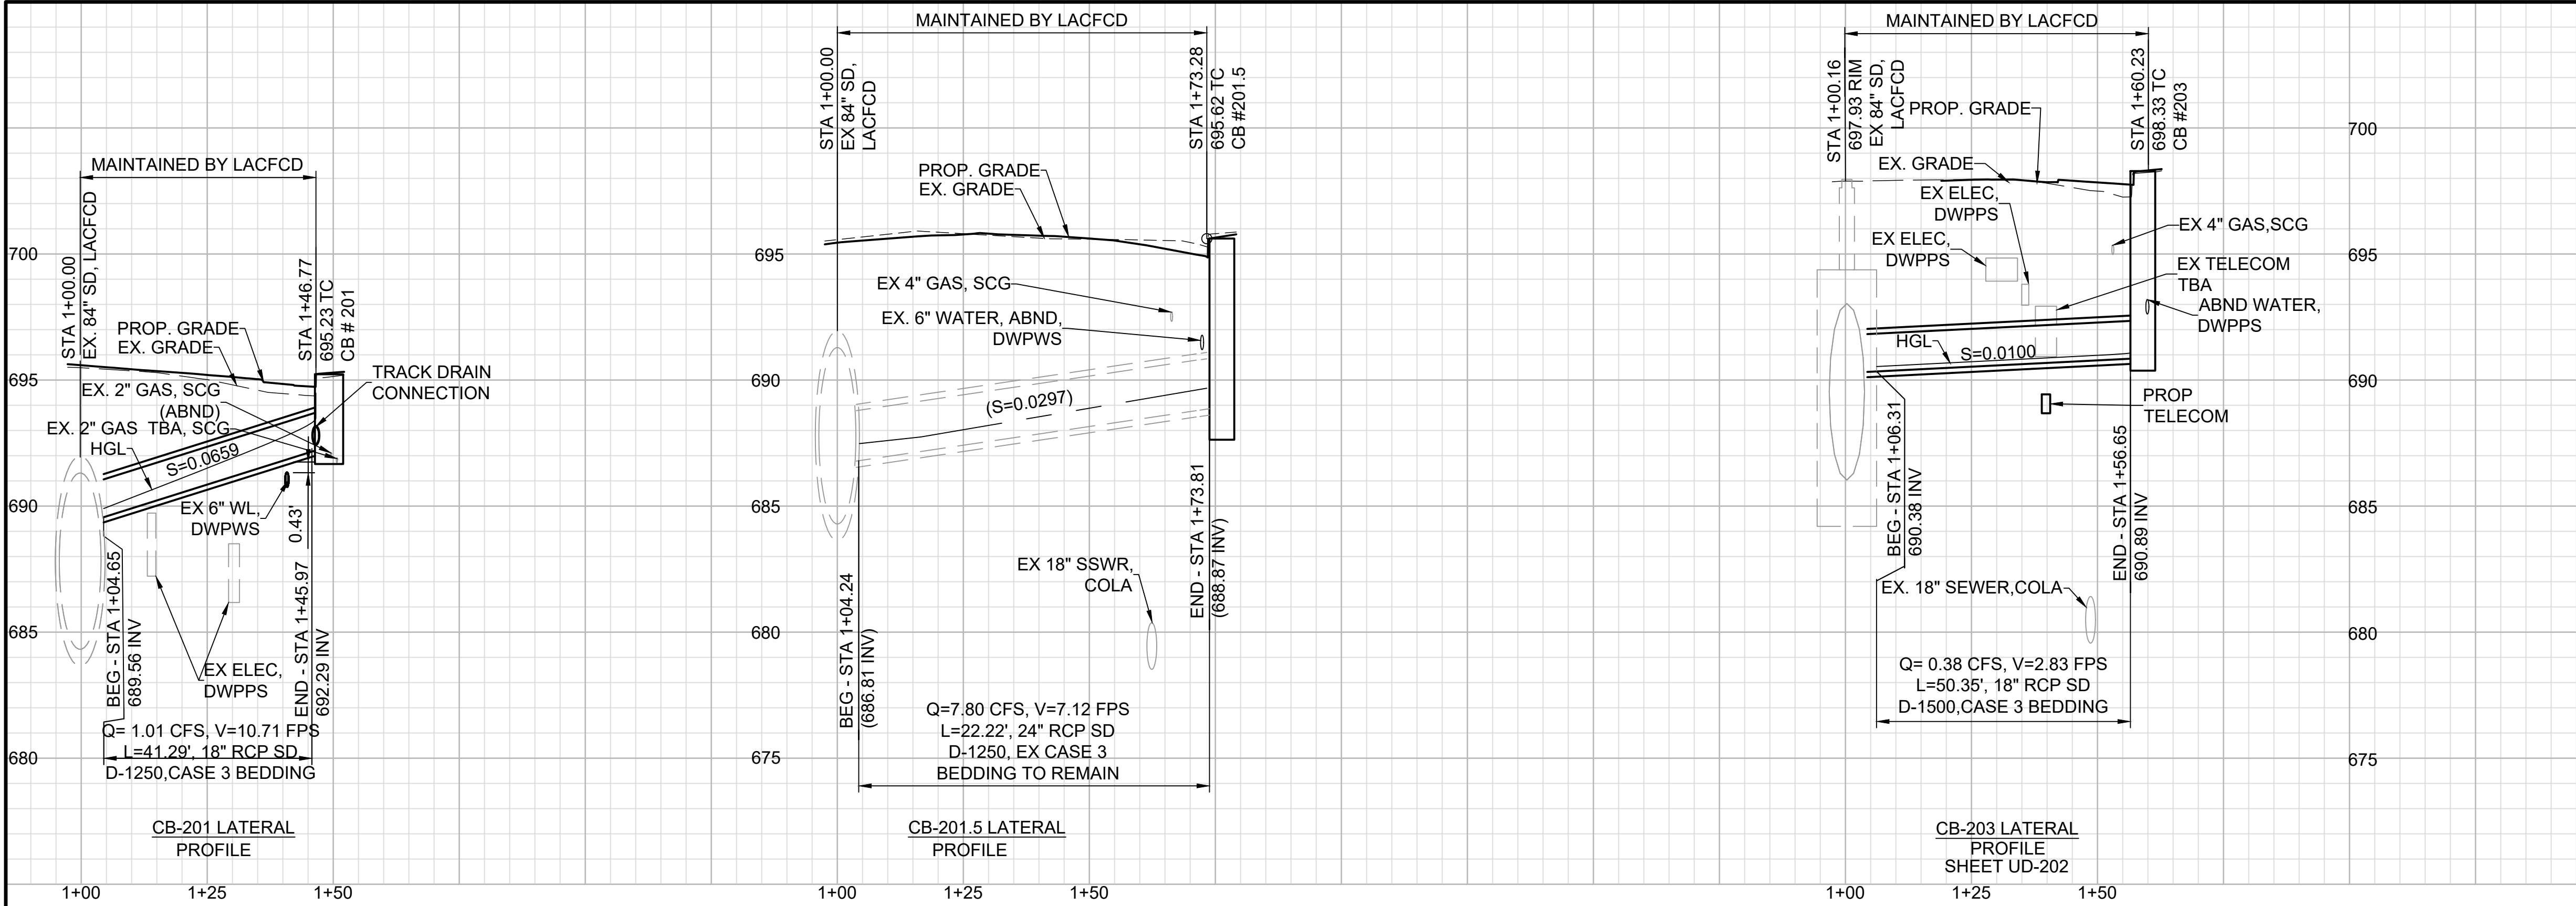

PROFILE SCALE
HORIZ: 1"=20'
VERT: 1"=4'

CONSTRUCTION SYMBOLS:

- CONSTRUCT ○◻ REMODEL EXISTING
◻ EXISTING ◻○ REMOVE AND CONSTRUCT
◻ REMOVE ○ WORK BY OTHERS



CONSTRUCTION NOTES:

- 79 REINFORCED CONCRETE PIPE
82 JUNCTION STRUCTURE
85 STORM DRAIN MANHOLE
86 WARPED GUTTER AT CATCH BASIN
97 CONCRETE COLLAR
99 CURB OPENING CATCH BASIN
102 OFFSET MANHOLE "TYPE B"

NOTES:

- SEE COMPOSITE UTILITY REARRANGEMENT PLANS (UR) FOR EXISTING UTILITY CONFLICTS AND PROPOSED RELOCATIONS. CONTRACTOR TO DETERMINE UTILITY DEPTHS AND LOCATIONS ON STORM DRAIN PROFILES PRIOR TO CONSTRUCTION.
- SEE TRACKWORK PLANS (T) FOR TRACK DRAIN DETAILS, SWITCH MACHINE DRAIN DETAILS, AND TRACK-RELATED WORK.
- SEE STREET IMPROVEMENT PLANS (CS) FOR ROADWAY-RELATED WORK.
- SEE DU04-SEGMENT B METRO TRACK GUIDEWAY PLANS (D) FOR TRACK GUIDEWAY STORM DRAIN IMPROVEMENTS.
- ALL NEW AND REMOVED/REPLACED CATCH BASINS UNDER THIS PROJECT SHALL INCLUDE CATCH BASIN OPENING SCREENS AND INSERTS. REUSE EXISTING SCREENS WHEN APPLICABLE.
- ALL NEW AND REMOVED/REPLACED CATCH BASINS UNDER THIS PROJECT SHALL BE STENCILED WITH PROHIBITIVE LANGUAGE "NO DUMPING - DRAIN TO OCEAN."
- SEE TRAFFIC AND SIGNAL PLANS FOR SIGNAL RELATED WORK.
- PROTECT IN PLACE ALL EXISTING BEDDING, UNLESS STATED ON PROFILE.

LINE/CURVE DATA TABLE			
NO.	LENGTH	BEARING/DELTA	RADIUS
L2	3.43	N71° 56' 19.68"W	--
L3	47.36	S57° 43' 27.34"W	--

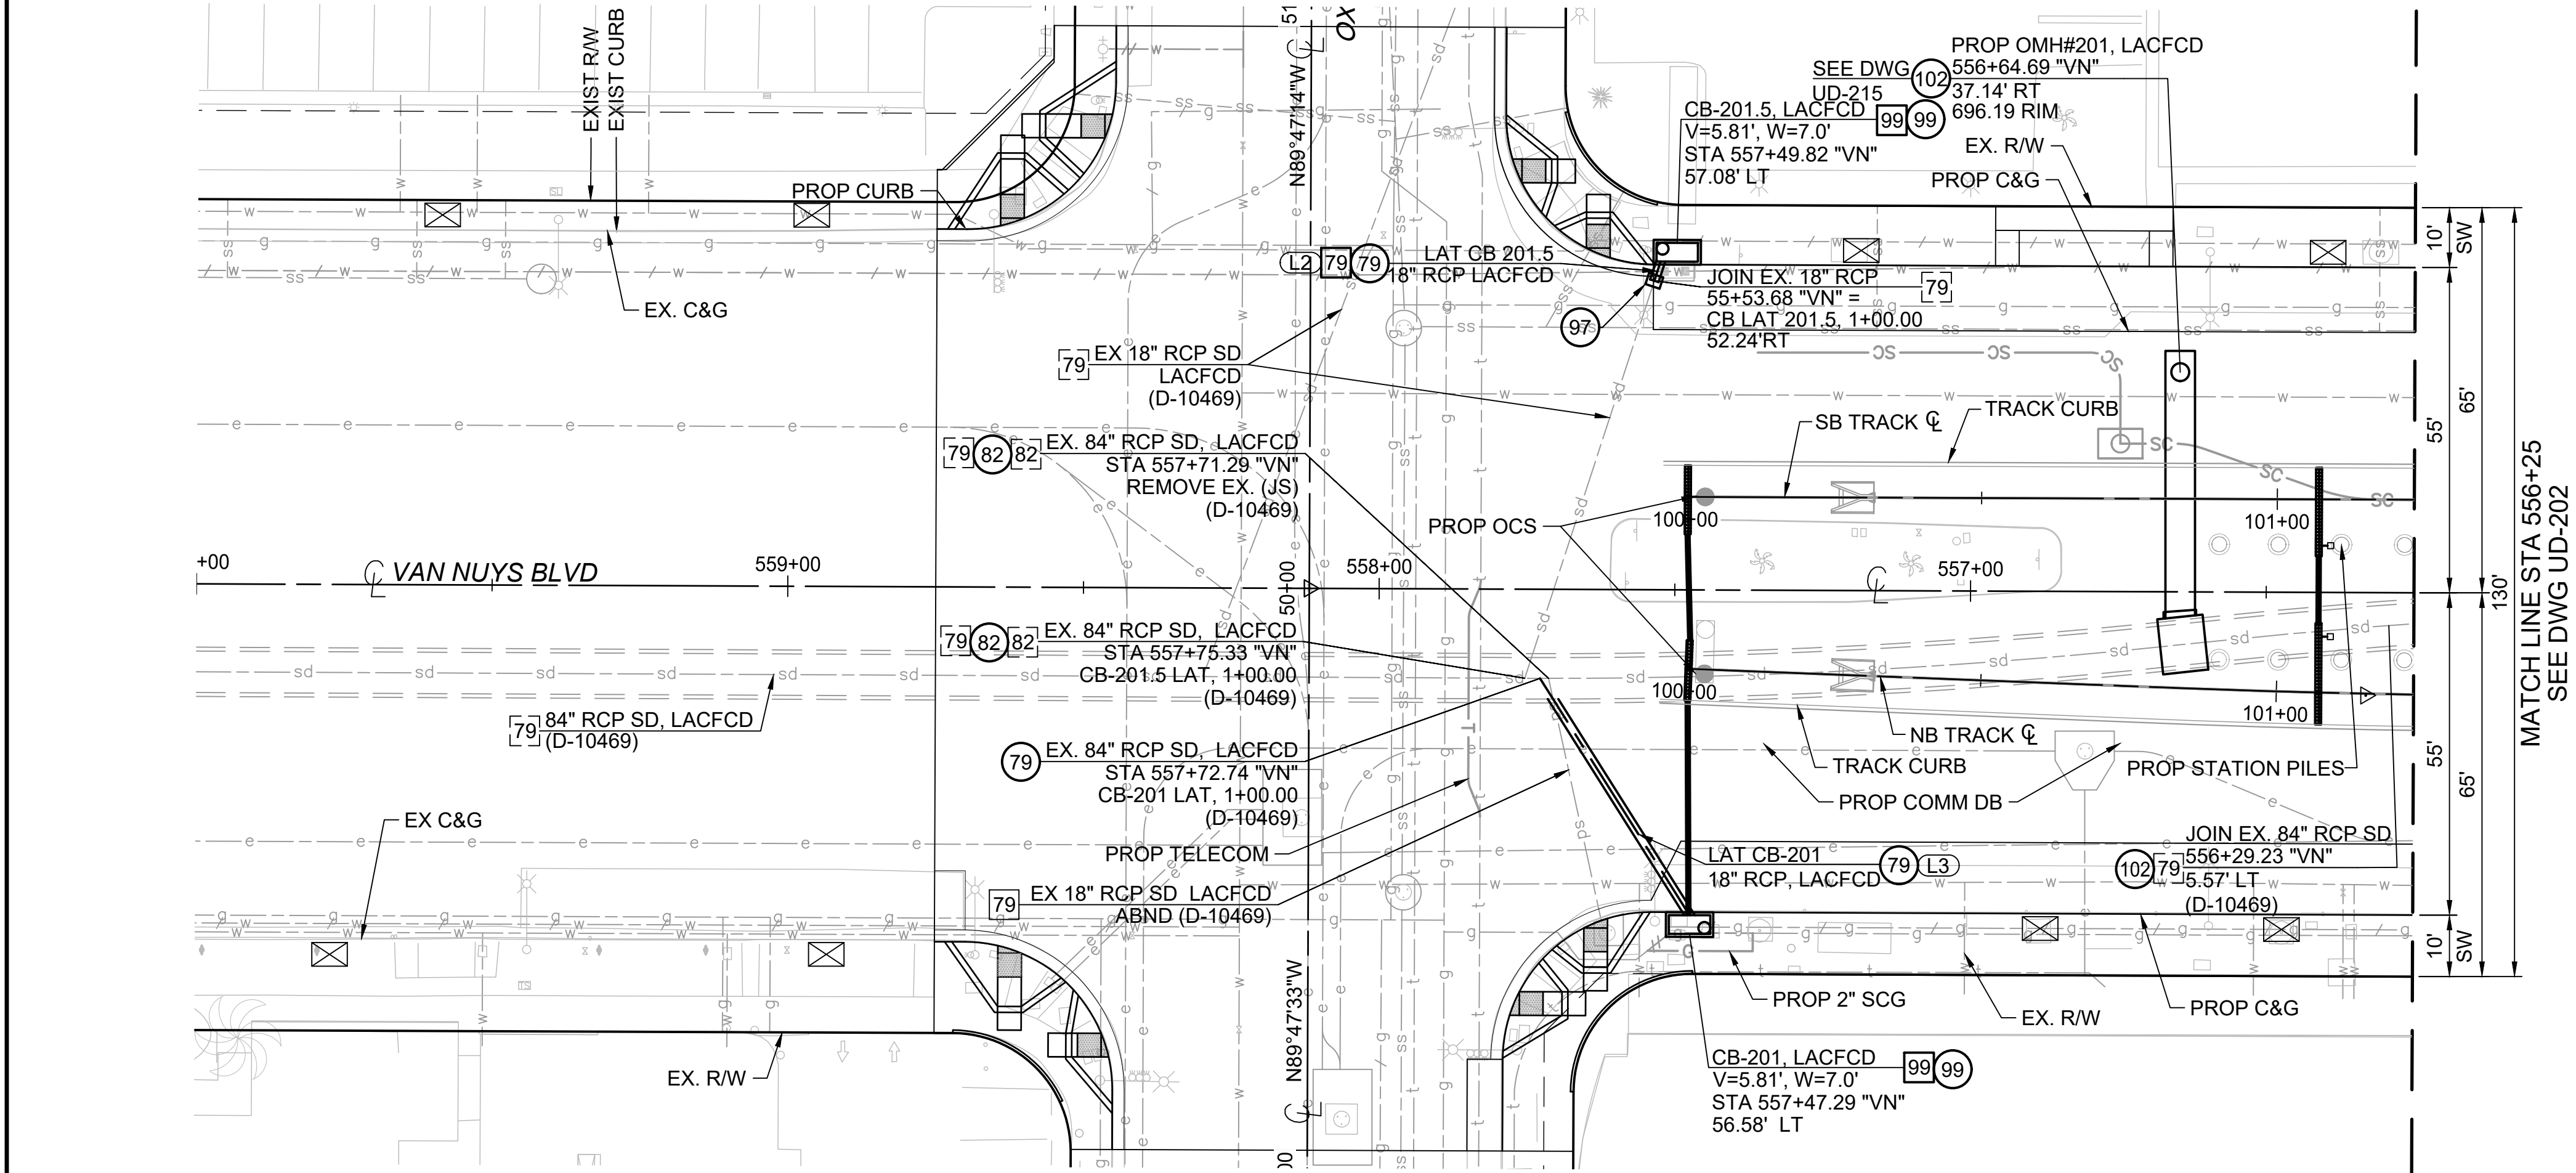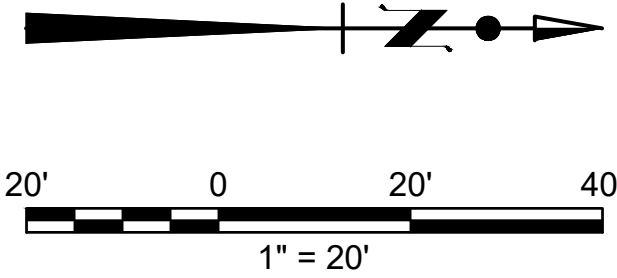

THE PREPARATION OF THIS DRAWING HAS BEEN FINANCED IN PART THROUGH A GRANT FROM THE U.S. DEPARTMENT OF TRANSPORTATION, FEDERAL TRANSIT ADMINISTRATION (FTA), UNDER THE FEDERAL TRANSIT ACT OF 1964, AS AMENDED, AND IN PART BY THE TAXES OF THE CITIZENS OF LOS ANGELES COUNTY AND OF THE STATE OF CALIFORNIA.								DESIGNED BY N. SOTO
								DRAWN BY R. VENEGAS
								CHECKED BY N. BUSCH
								IN CHARGE N. BUSCH
								DATE 12/11/2025
C	12/15/25	NS	JR	C78082	09/30/27	J. RIMORIN	100% SUBMITTAL	
B	08/18/25	AR	NB	C65608	09/30/27	N. BUSCH	85% SUBMITTAL	
A	03/07/25	KM	JR	C78082	09/30/27	J. RIMORIN	60% SUBMITTAL	
REV	DATE	BY	APP	REG NO	EXPIRES	SEAL HOLDER	DESCRIPTION	

**LOS ANGELES COUNTY**
METROPOLITAN TRANSPORTATION AUTHORITY

**San Fernando Transit Constructors**

**AECOM**

14300 ARMINA ST.
LOS ANGELES, CA 91402
TEL: 951.684.5360


1111 S. GARDEN AVE. SUITE 103
LOS ANGELES, CA 90015
213.922.0200

100% SUBMITTAL - NOT FOR CONSTRUCTION

EAST SAN FERNANDO VALLEY LRT
DU06 - DRAINAGE SEGMENT A1
STORM DRAIN PLAN AND PROFILE
VAN NUYS BLVD STA 556+25 TO 560+00

CONTRACT NO PS89616000	REV
DRAWING NO UD-201	
SCALE 1" = 20'	
SHEET NO	

FILE PATH: \\80724957-ESFV-PH2\PROJECT FILES\900_CAD\20_SHEETS\DU0609_UD_DRAINAGE\PS89616000-DU06-UD-201.DWG
PLOT DATE: 12/16/2025 - 1:14 PM USER: ADRIANROBLES

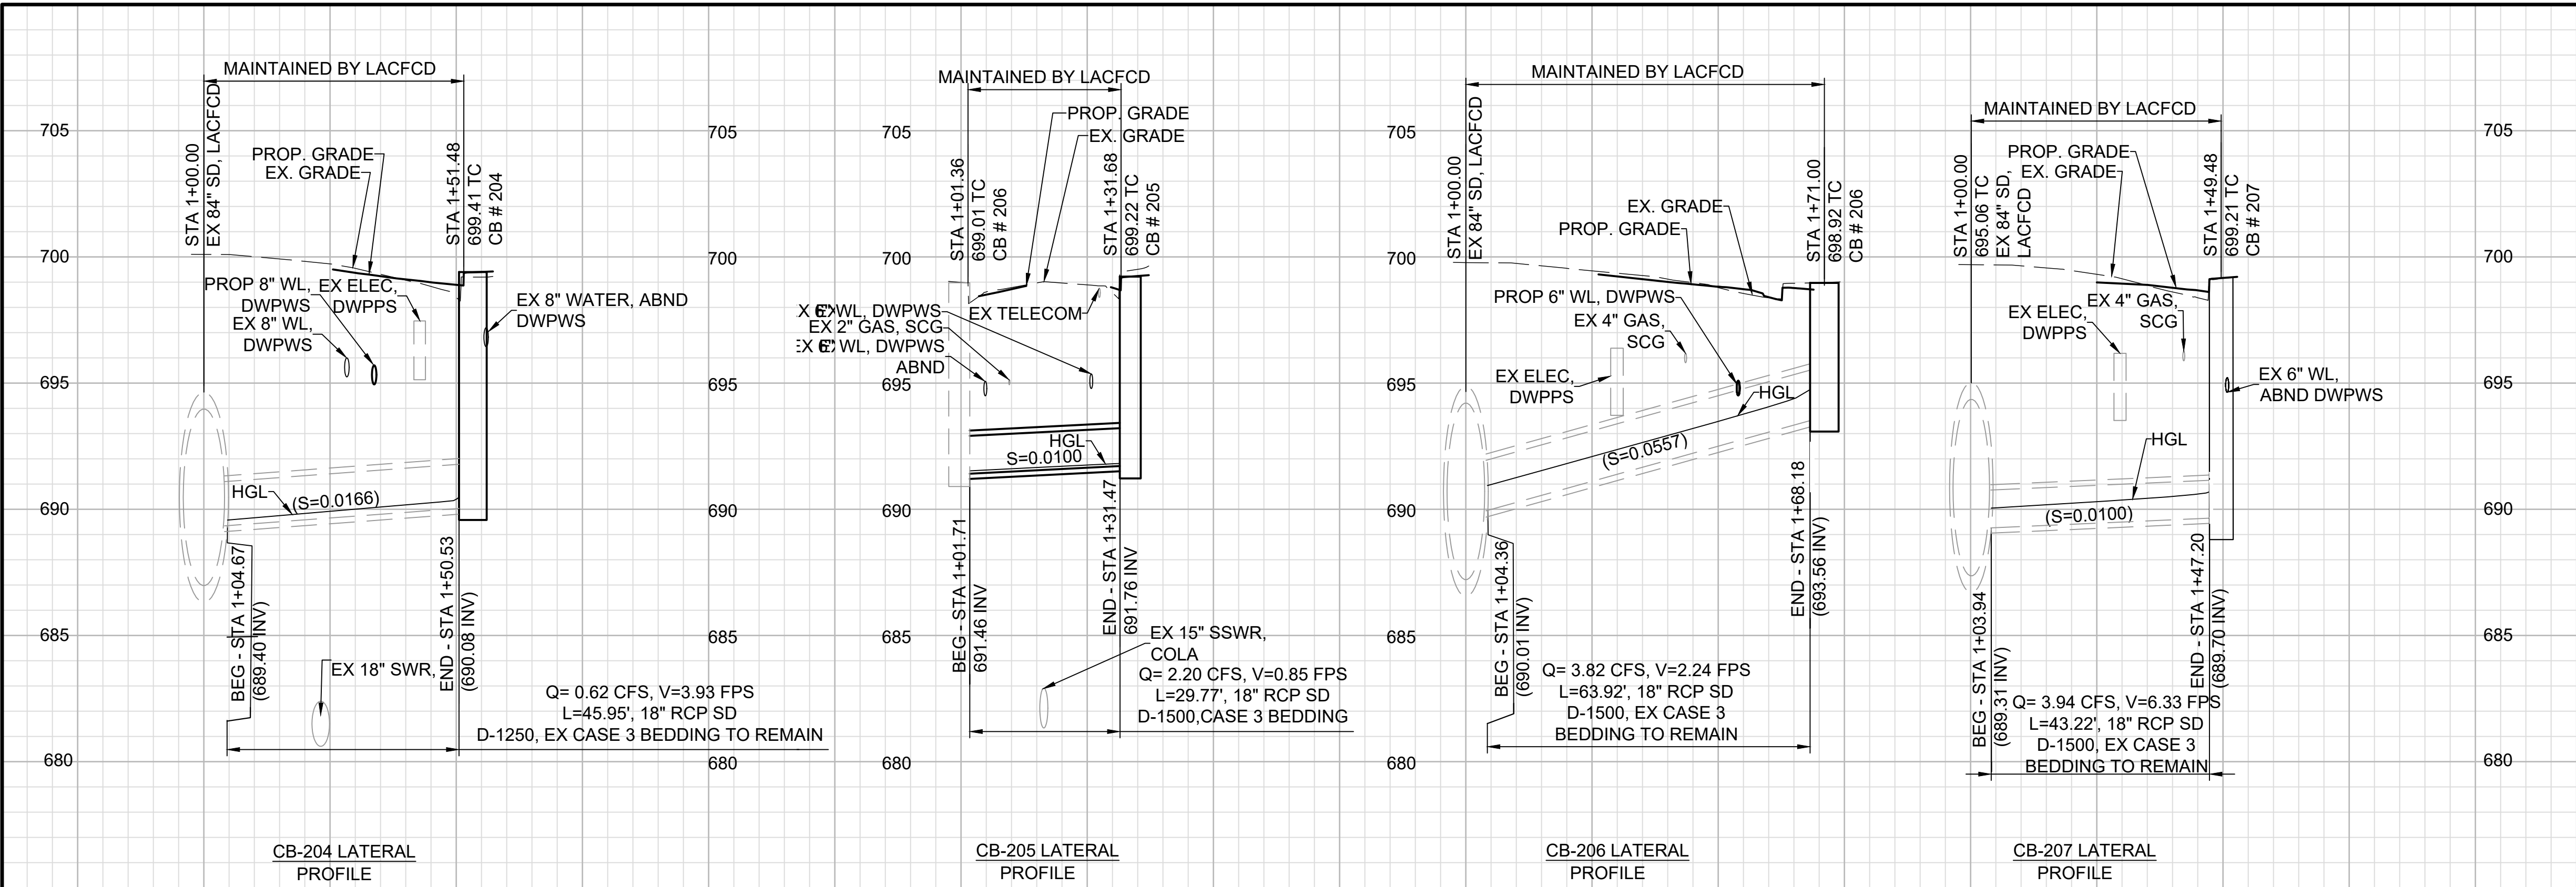

CONSTRUCTION SYMBOLS:

- CONSTRUCT ○ REMODEL EXISTING
□ EXISTING □ REMOVE AND CONSTRUCT
□ REMOVE ○ WORK BY OTHERS

CONSTRUCTION NOTES:


- 79 REINFORCED CONCRETE PIPE
82 JUNCTION STRUCTURE
85 STORM DRAIN MANHOLE
97 CONCRETE COLLAR
98 MONOLITHIC CATCH BASIN CONNECTION
99 CURB OPENING CATCH BASIN
102 OFFSET MANHOLE "TYPE B"
115 CAP MH

NOTES:

- SEE COMPOSITE UTILITY REARRANGEMENT PLANS (UR) FOR EXISTING UTILITY CONFLICTS AND PROPOSED RELOCATIONS. CONTRACTOR TO DETERMINE UTILITY DEPTHS AND LOCATIONS ON STORM DRAIN PROFILES PRIOR TO CONSTRUCTION.
- SEE TRACKWORK PLANS (T) FOR TRACK DRAIN DETAILS, SWITCH MACHINE DRAIN DETAILS, AND TRACK-RELATED WORK.
- SEE STREET IMPROVEMENT PLANS (CS) FOR ROADWAY-RELATED WORK.
- SEE DU04-SEGMENT B METRO TRACK GUIDEWAY PLANS (D) FOR TRACK GUIDEWAY STORM DRAIN IMPROVEMENTS.
- ALL NEW AND REMOVED/REPLACED CATCH BASINS UNDER THIS PROJECT SHALL INCLUDE CATCH BASIN OPENING SCREENS AND INSERTS. REUSE EXISTING SCREENS WHEN APPLICABLE.
- ALL NEW AND REMOVED/REPLACED CATCH BASINS UNDER THIS PROJECT SHALL BE STENCILED WITH PROHIBITIVE LANGUAGE "NO DUMPING - DRAIN TO OCEAN."
- SEE TRAFFIC AND SIGNAL PLANS FOR SIGNAL RELATED WORK


PROFILE SCALE
HORIZ: 1"=20'
VERT: 1"=4'

LINE/CURVE DATA TABLE			
NO.	LENGTH	BEARING/DELTA	RADIUS
L1	23.34	S85° 00' 56.07"E	--
L2	57.26	S72° 14' 52.35"E	--
L3	0.90	S59° 00' 12.30"W	--
L4	30.80	N06° 08' 37.74"E	--

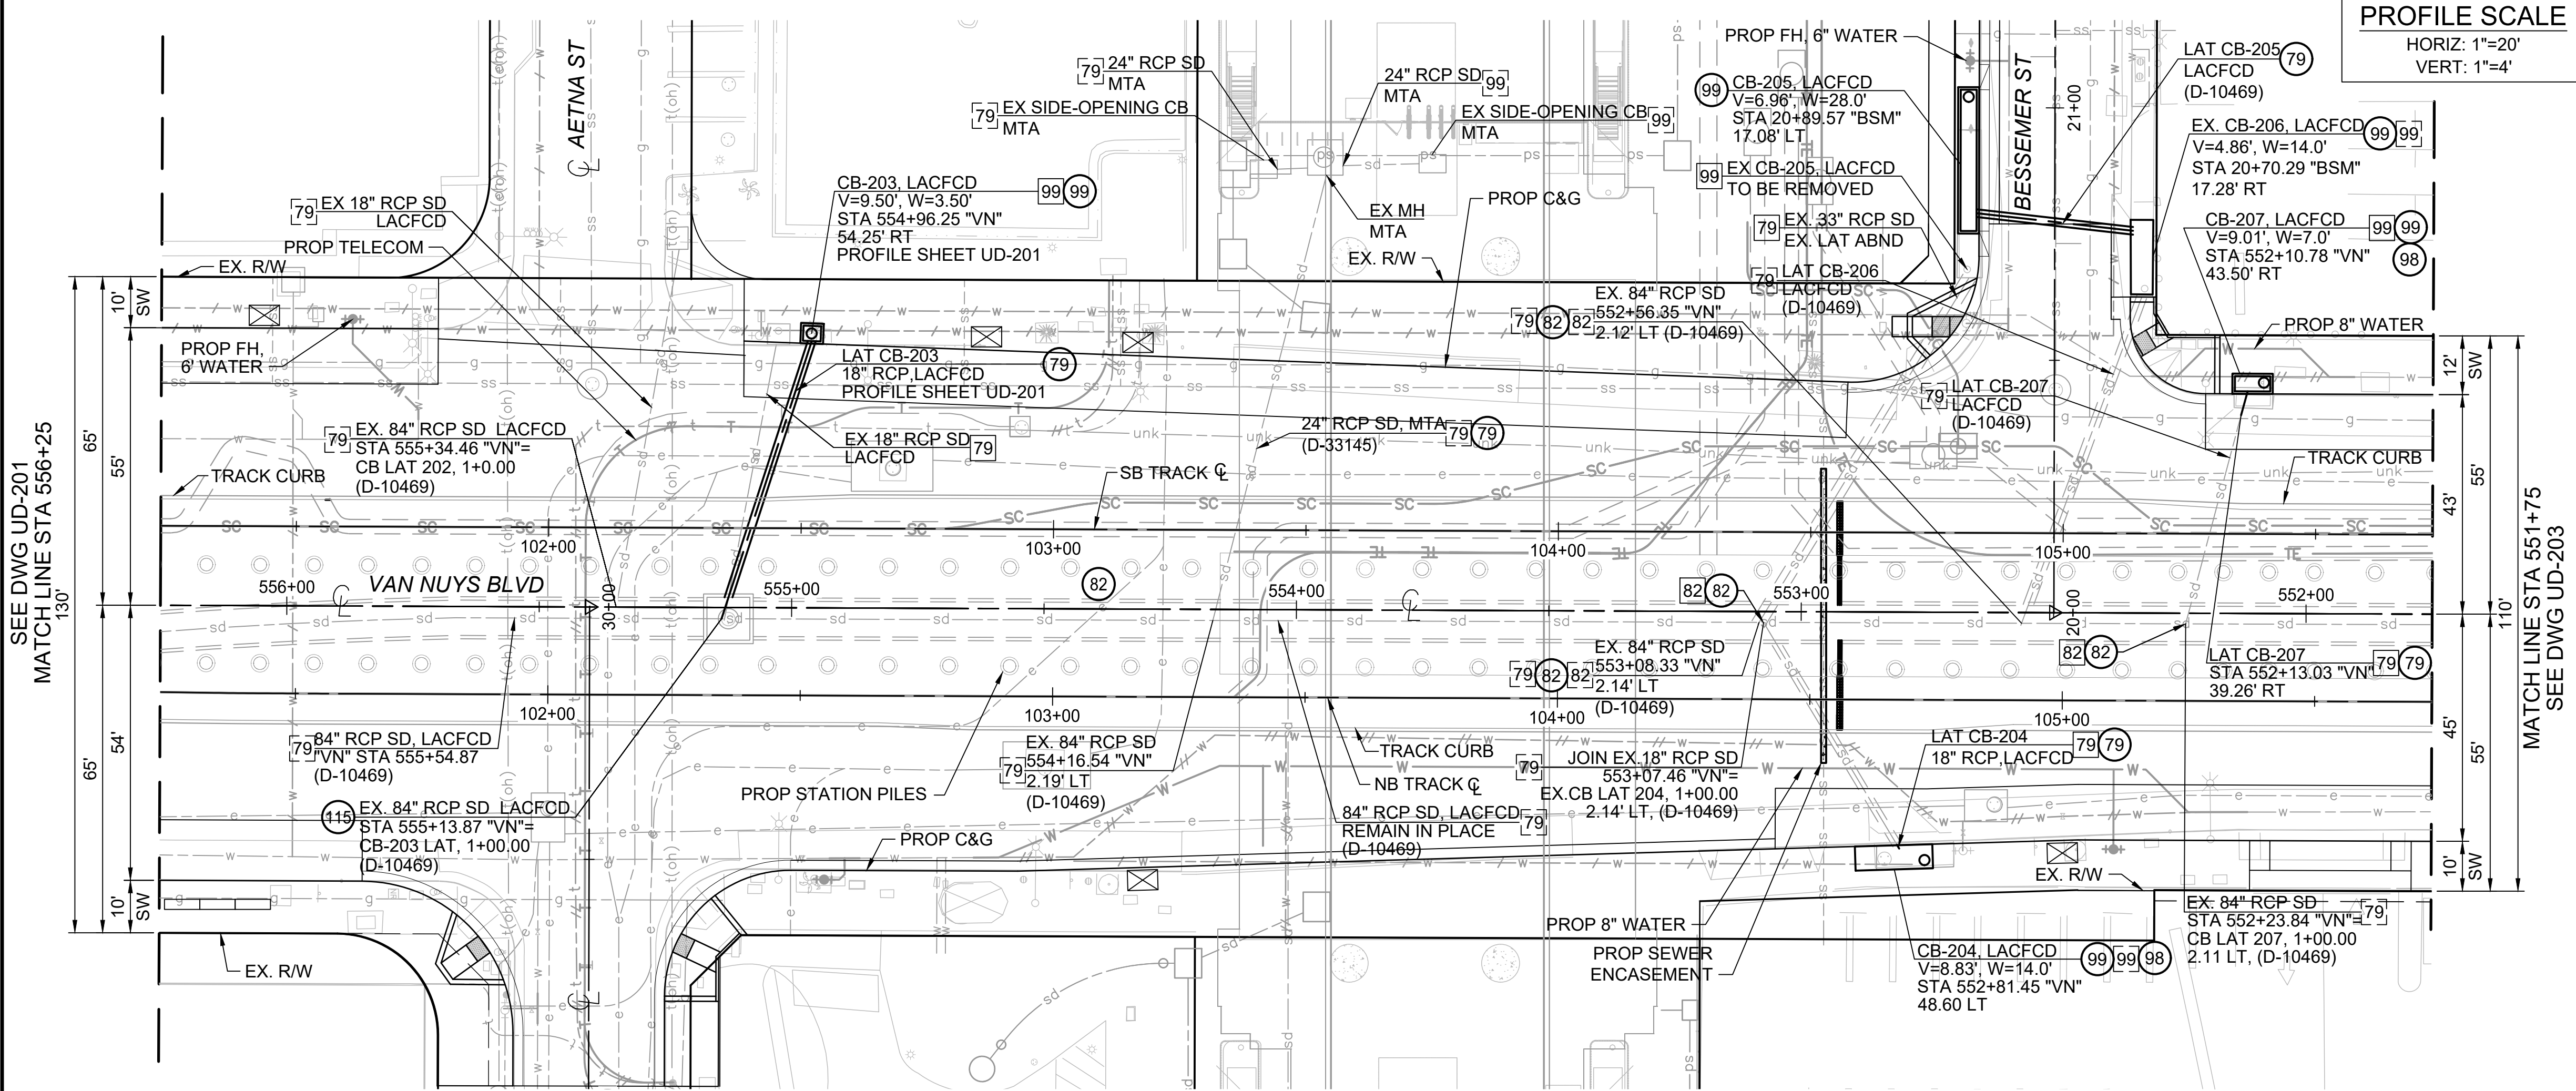

THE PREPARATION OF THIS DRAWING HAS BEEN FINANCED IN PART THROUGH A GRANT FROM THE U.S. DEPARTMENT OF TRANSPORTATION, FEDERAL TRANSIT ADMINISTRATION (FTA), UNDER THE FEDERAL TRANSIT ACT OF 1964, AS AMENDED, AND IN PART BY THE TAXES OF THE CITIZENS OF LOS ANGELES COUNTY AND OF THE STATE OF CALIFORNIA.	DESIGNED BY N.SOTO	LOS ANGELES COUNTY METROPOLITAN TRANSPORTATION AUTHORITY	EAST SAN FERNANDO VALLEY LRT DU06 - DRAINAGE SEGMENT A1	CONTRACT NO PS89616000									
	DRAWN BY R.VENEGAS			DRAWING NO UD-202									
	CHECKED BY N.BUSCH			SCALE 1" = 20'									
	IN CHARGE N.BUSCH			SHEET NO									
REV	DATE	BY	APP	REG NO	EXPIRES	SEAL HOLDER	DESCRIPTION	DATE 12/11/2025	14300 ARMINA ST. LOS ANGELES, CA 91402 TEL: 951.684.5360	San Fernando Transit Constructors	AECOM	100% SUBMITTAL - NOT FOR CONSTRUCTION	STORM DRAIN PLAN AND PROFILE VAN NUYS BLVD STA 551+75 TO 556+25
C	12/15/25	NS	JR	C78082	09/30/27	J. RIMORIN	100% SUBMITTAL						
B	08/18/25	AR	NB	C65608	09/30/27	N.BUSCH	85% SUBMITTAL						
A	03/07/25	KM	JR	C78082	09/30/27	J. RIMORIN	60% SUBMITTAL						

FILE PATH: \\S0724657-ESFV-PH2\PROJECT FILES\900_CAD\20_SHEETS\DU0609_UD_DRAINAGE\PS89616000-DU06-UD-202.DWG
PLOT DATE: 12/16/2025 - 4:56 PM USER: ADRIANROBLES

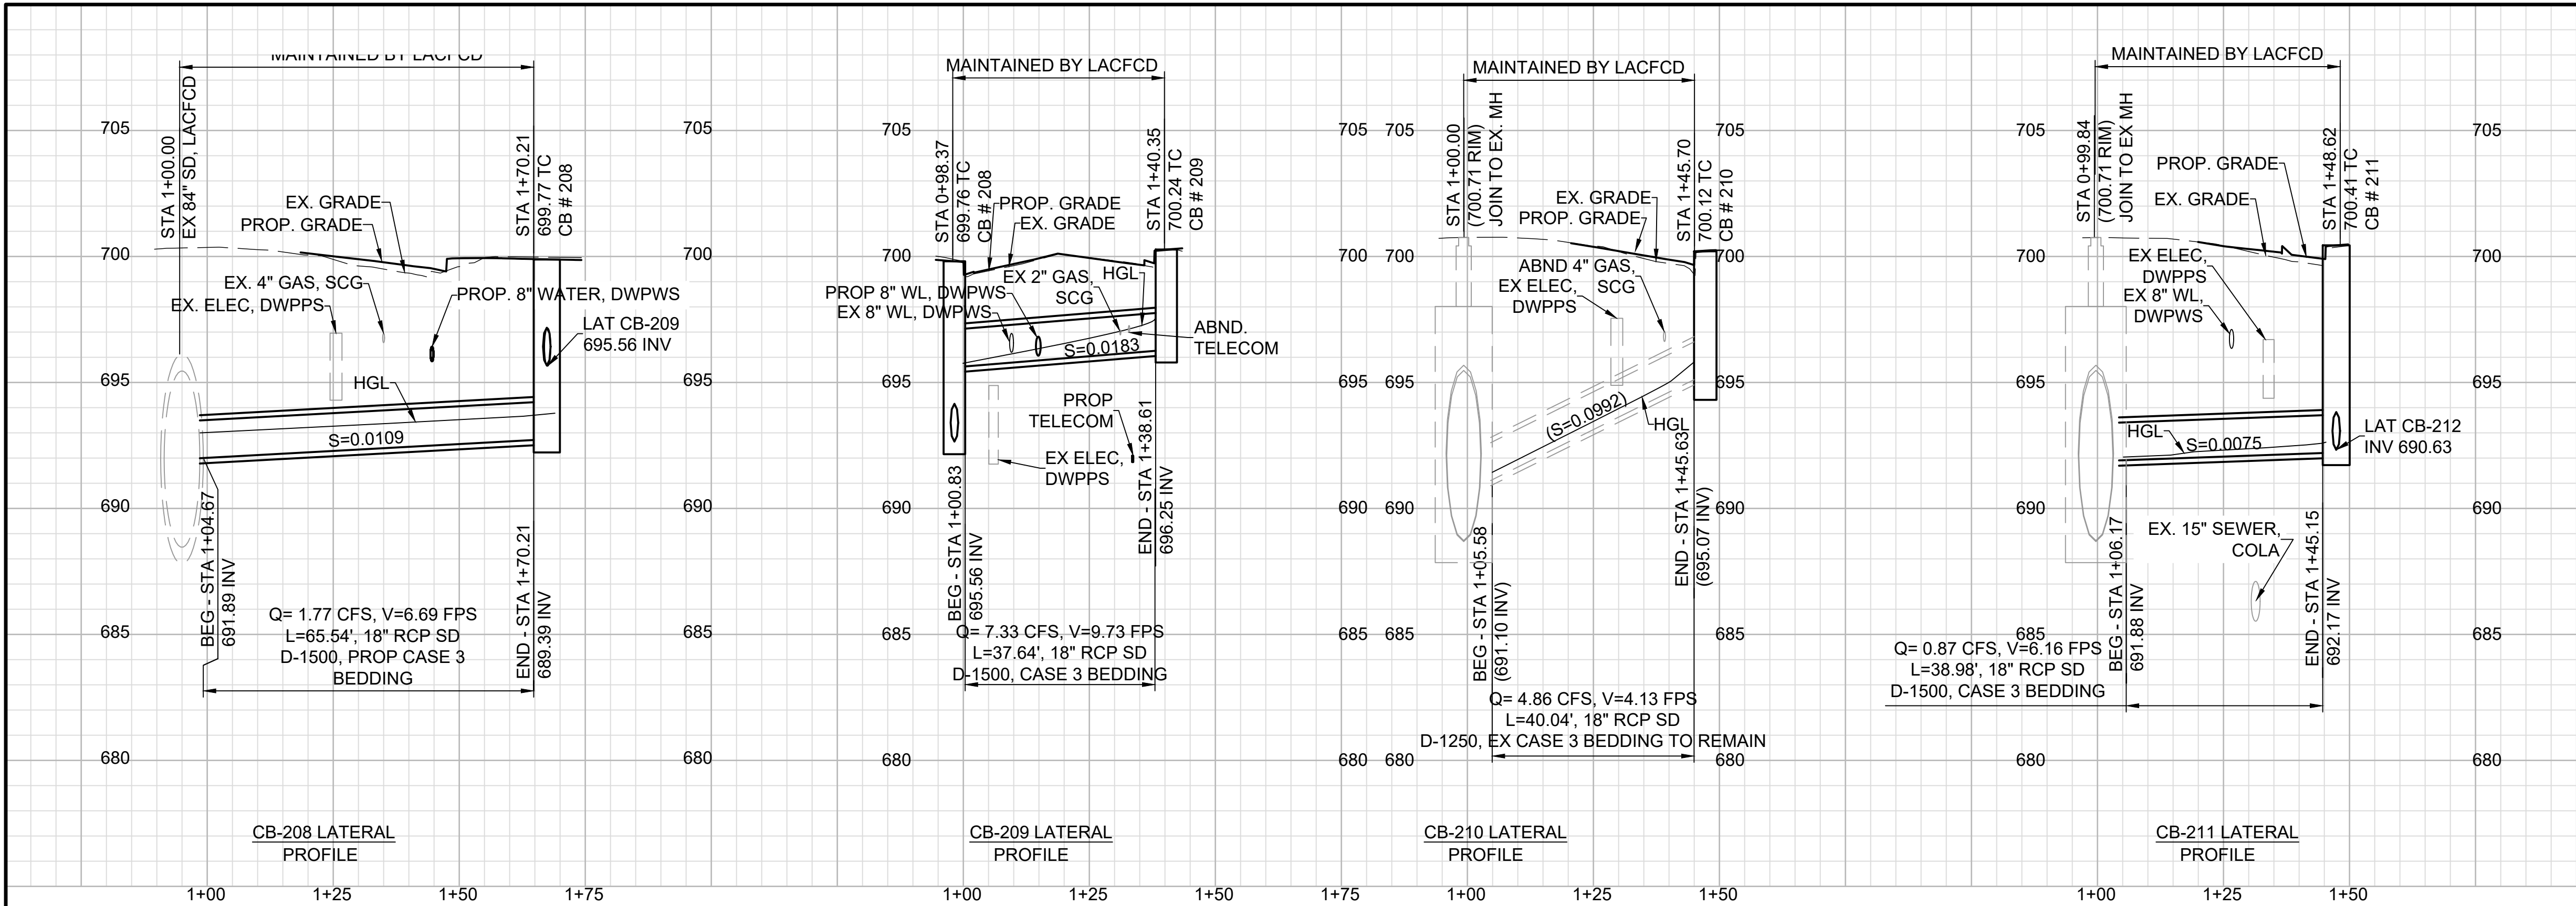

CONSTRUCTION SYMBOLS:

- CONSTRUCT ○◻ REMODEL EXISTING
◻ EXISTING ◻○ REMOVE AND CONSTRUCT
◻ REMOVE ○ WORK BY OTHERS

CONSTRUCTION NOTES:

- 79 REINFORCED CONCRETE PIPE
82 JUNCTION STRUCTURE
85 STORM DRAIN MANHOLE
97 CONCRETE COLLAR
98 MONOLITHIC CATCH BASIN CONNECTION
99 CURB OPENING CATCH BASIN
102 OFFSET MANHOLE "TYPE B"
115 CAP MH



NOTES:

- SEE COMPOSITE UTILITY REARRANGEMENT PLANS (UR) FOR EXISTING UTILITY CONFLICTS AND PROPOSED RELOCATIONS. CONTRACTOR TO DETERMINE UTILITY DEPTHS AND LOCATIONS ON STORM DRAIN PROFILES PRIOR TO CONSTRUCTION.
- SEE TRACKWORK PLANS (T) FOR TRACK DRAIN DETAILS, SWITCH MACHINE DRAIN DETAILS, AND TRACK-RELATED WORK.
- SEE STREET IMPROVEMENT PLANS (CS) FOR ROADWAY-RELATED WORK.
- SEE DU04-SEGMENT B METRO TRACK GUIDEWAY PLANS (D) FOR TRACK GUIDEWAY STORM DRAIN IMPROVEMENTS.
- ALL NEW AND REMOVED/REPLACED CATCH BASINS UNDER THIS PROJECT SHALL INCLUDE CATCH BASIN OPENING SCREENS AND INSERTS. REUSE EXISTING SCREENS WHEN APPLICABLE.
- ALL NEW AND REMOVED/REPLACED CATCH BASINS UNDER THIS PROJECT SHALL BE STENCILED WITH PROHIBITIVE LANGUAGE "NO DUMPING - DRAIN TO OCEAN."
- SEE TRAFFIC AND SIGNAL PLANS FOR SIGNAL RELATED WORK.
- PROTECT IN PLACE ALL EXISTING BEDDING, UNLESS STATED ON PROFILE.

PROFILE SCALE

HORIZ: 1"=20'
VERT: 1"=4'

LINE/CURVE DATA TABLE			
NO.	LENGTH	BEARING/Delta	RADIUS
L1	65.13	S80° 29' 19.50"E	--
L2	38.89	S07° 53' 46.18"E	--
L3	41.56	N63° 56' 22.84"E	--
L4	36.89	S44° 46' 48.91"E	--

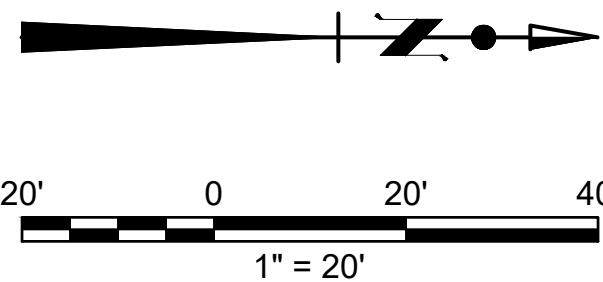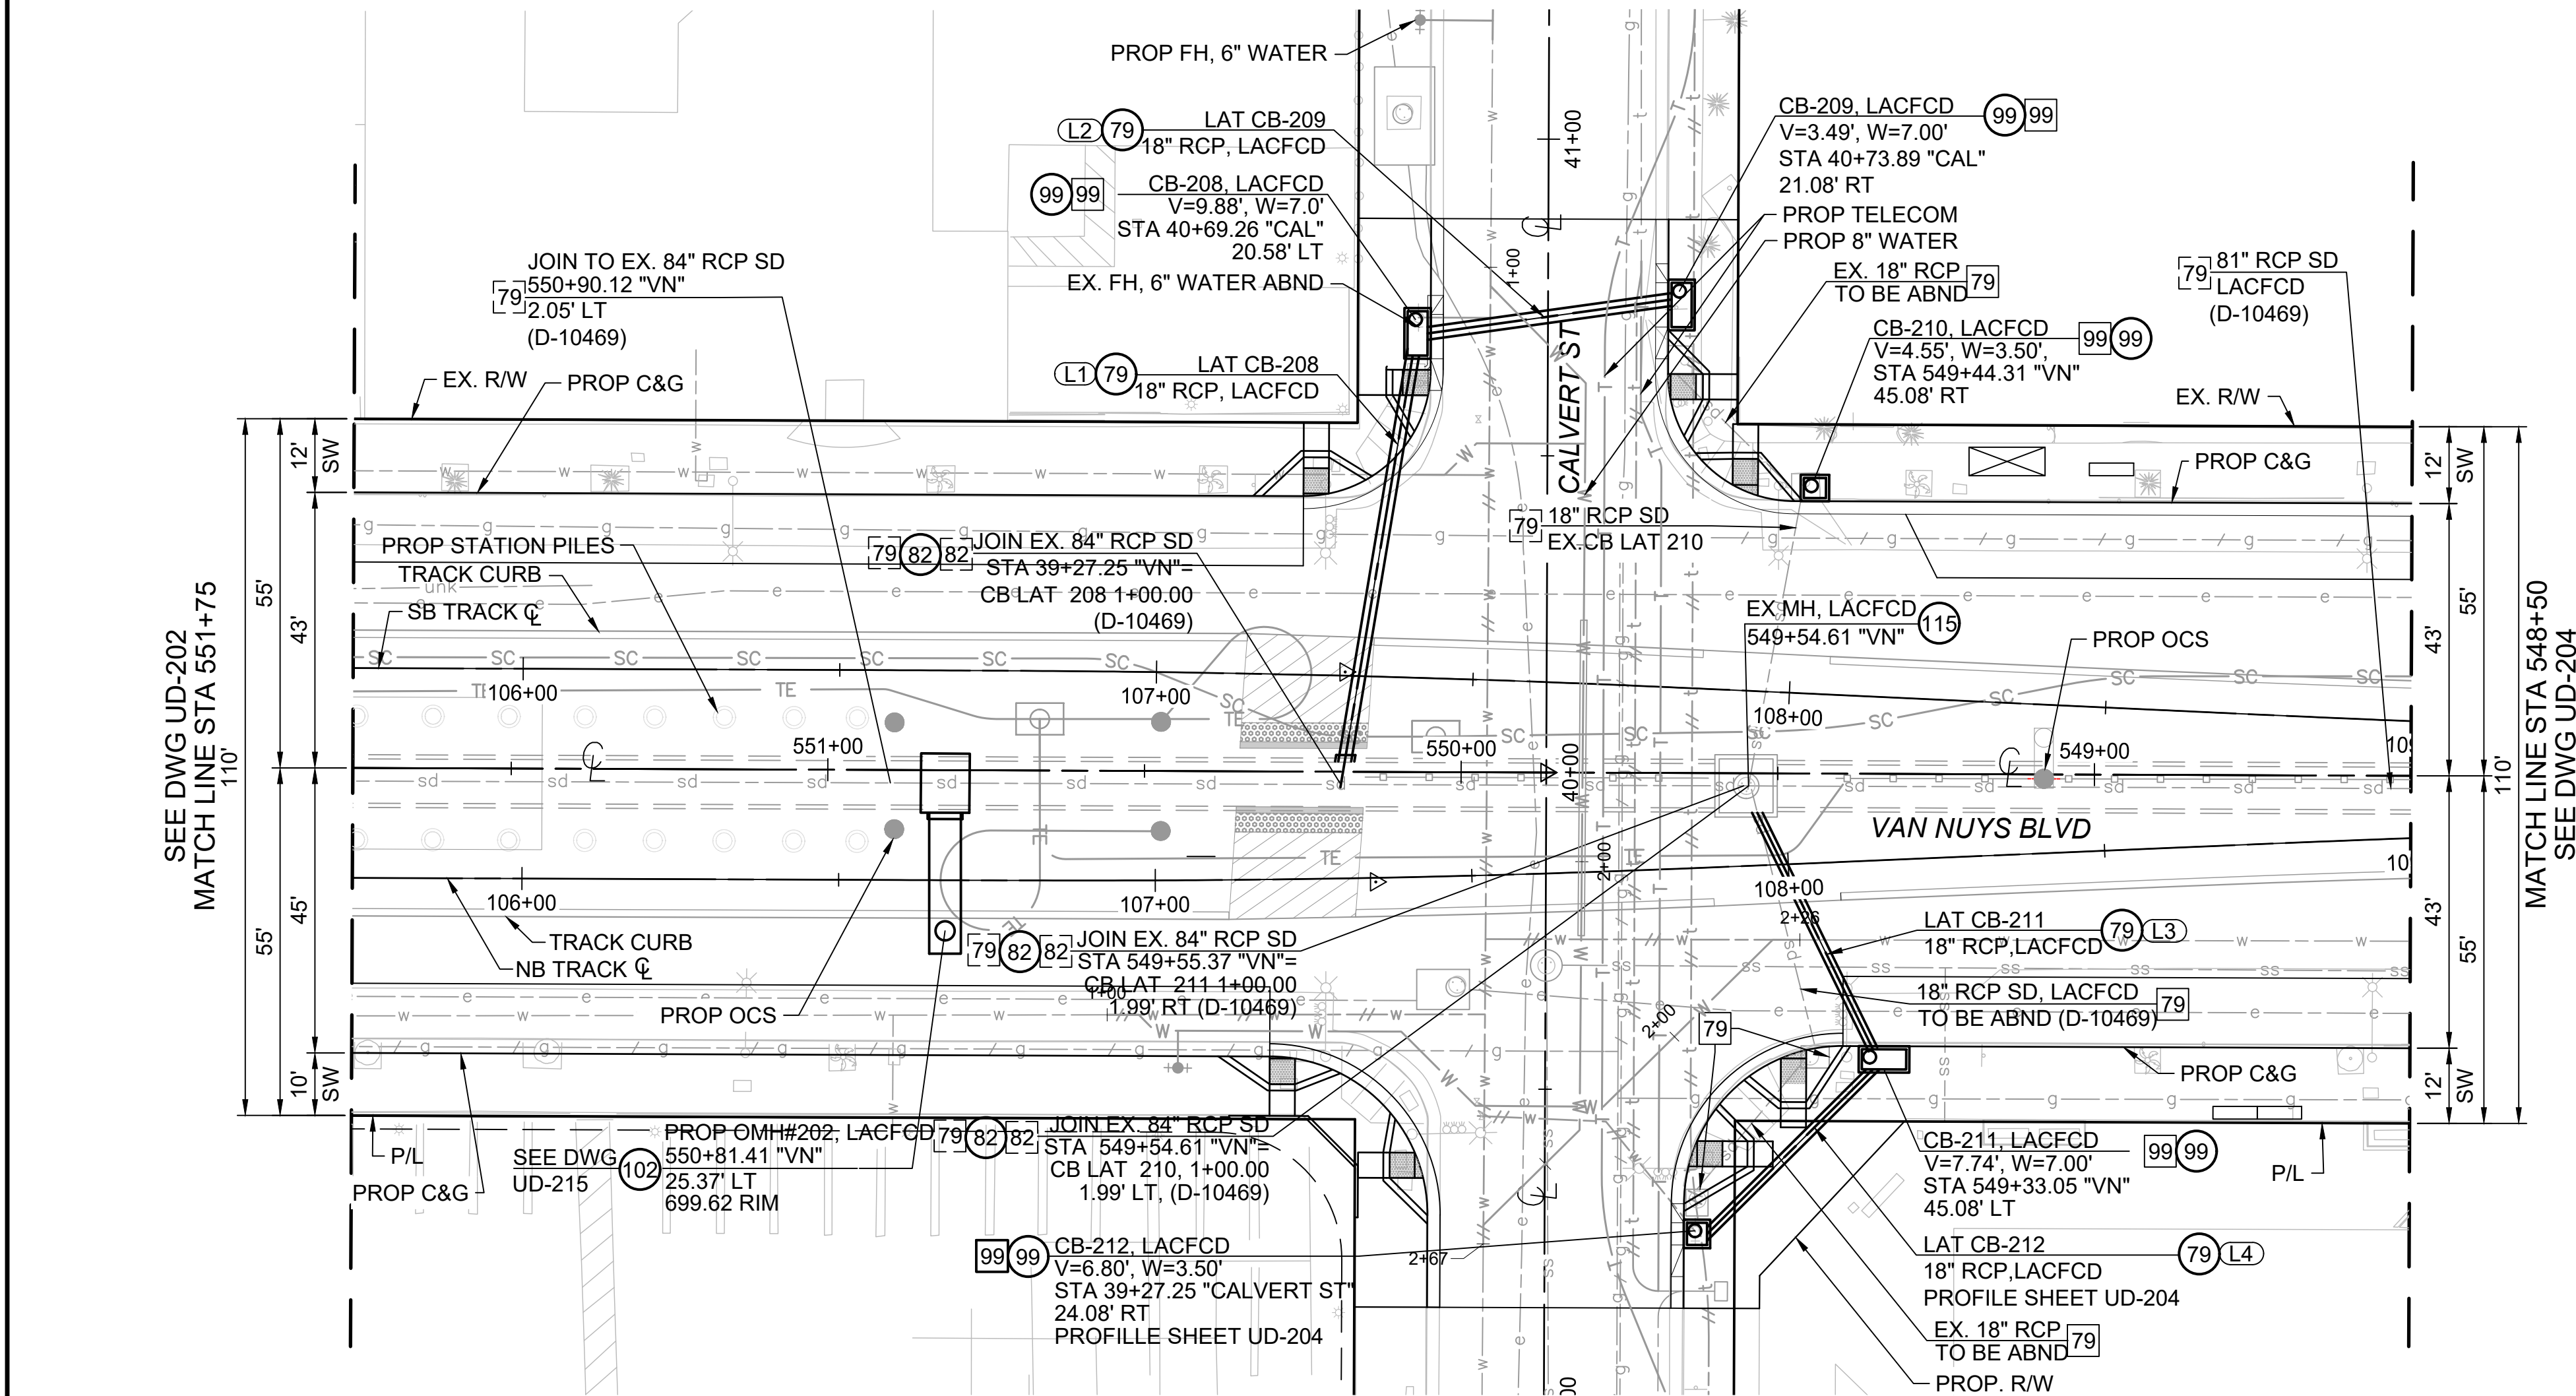

THE PREPARATION OF THIS DRAWING HAS BEEN FINANCED IN PART THROUGH A GRANT FROM THE U.S. DEPARTMENT OF TRANSPORTATION, FEDERAL TRANSIT ADMINISTRATION (FTA), UNDER THE FEDERAL TRANSIT ACT OF 1964, AS AMENDED, AND IN PART BY THE TAXES OF THE CITIZENS OF LOS ANGELES COUNTY AND OF THE STATE OF CALIFORNIA.						
REV	DATE	BY	APP	REG NO	EXPIRES	DESCRIPTION
C	12/15/25	NS	JR	C78082	09/30/27	J. RIMORIN 100% SUBMITTAL
B	08/18/25	AR	NB	C65608	09/30/27	N. BUSCH 85% SUBMITTAL
A	03/07/25	KM	JR	C78082	09/30/27	J. RIMORIN 60% SUBMITTAL

DESIGNED BY N.SOTO
DRAWN BY R.VENEGAS
CHECKED BY N. BUSCH
IN CHARGE N. BUSCH
DATE 12/11/2025

**LOS ANGELES COUNTY**
METROPOLITAN TRANSPORTATION AUTHORITY

**San Fernando Transit Constructors**

**AECOM**

14300 ARMINA ST.
LOS ANGELES, CA 91402
TEL: 951.684.5360


1111 S. GRAND AVE. SUITE 103
LOS ANGELES, CA 90015
213.922.0000

100% SUBMITTAL - NOT FOR CONSTRUCTION

EAST SAN FERNANDO VALLEY LRT
DU06 - DRAINAGE SEGEMENT A1
STORM DRAIN PLAN AND PROFILE
VAN NUYS BLVD STA 548+50 TO 551+75

CONTRACT NO PS89616000	REV
DRAWING NO UD-203	
SCALE 1" = 20'	
SHEET NO	

FILE PATH: \\S0724657-ESFV-PH2\PROJECT FILES\900_CAD\20_SHEETS\DU0609_UD_DRAINAGE\PS89616000-DU06-UD-203.DWG
PLOT DATE: 12/16/2025 - 4:52 PM USER: ADRIANROBLES

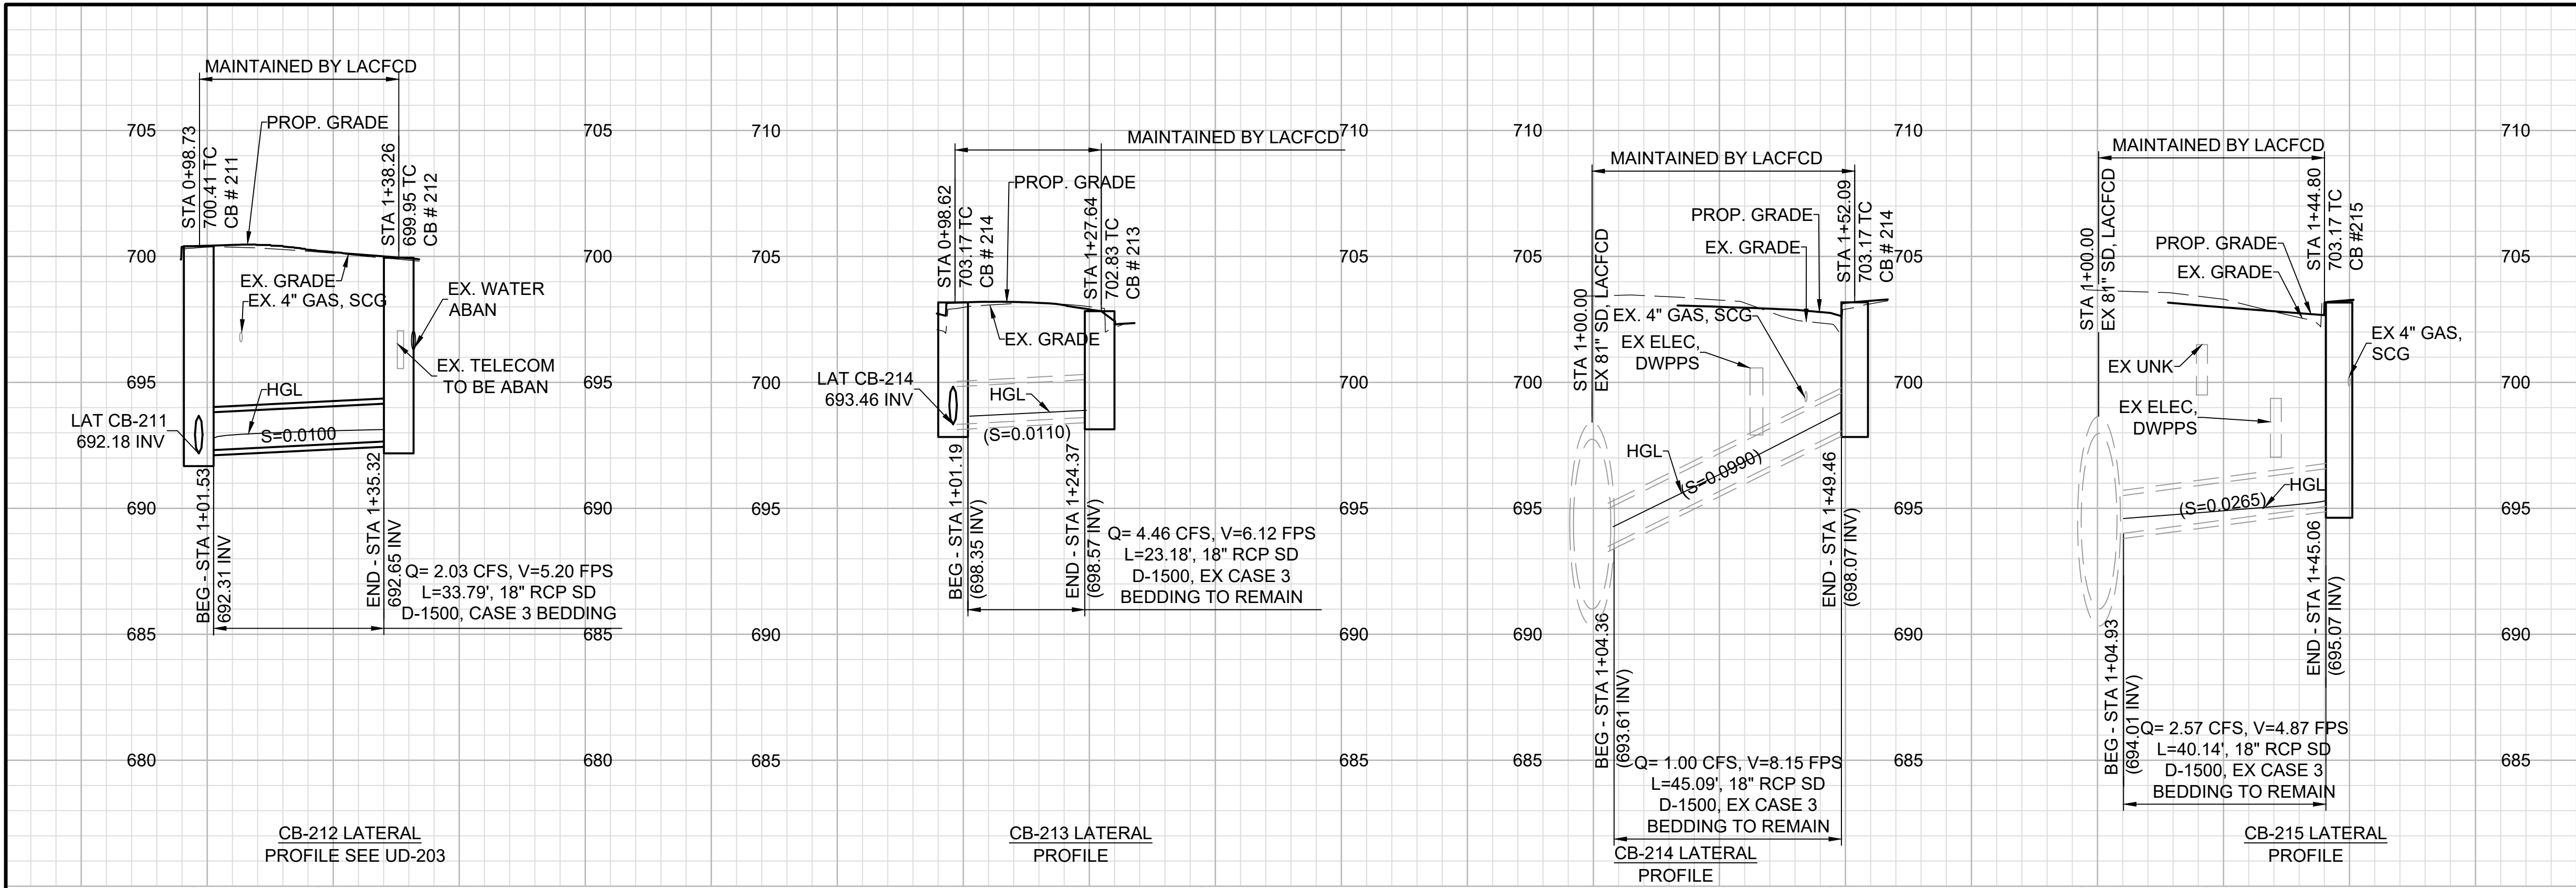

CONSTRUCTION SYMBOLS:

- CONSTRUCT ○◻ REMODEL EXISTING
◻ EXISTING ◻○ REMOVE AND CONSTRUCT
◻ REMOVE ○ WORK BY OTHERS



CONSTRUCTION NOTES:

- 79 REINFORCED CONCRETE PIPE
82 JUNCTION STRUCTURE
85 STORM DRAIN MANHOLE
97 CONCRETE COLLAR
98 MONOLITHIC CATCH BASIN CONNECTION
99 CURB OPENING CATCH BASIN
102 OFFSET MANHOLE "TYPE B"
115 CAP MH

NOTES:

1. SEE COMPOSITE UTILITY REARRANGEMENT PLANS (UR) FOR EXISTING UTILITY CONFLICTS AND PROPOSED RELOCATIONS. CONTRACTOR TO DETERMINE UTILITY DEPTHS AND LOCATIONS ON STORM DRAIN PROFILES PRIOR TO CONSTRUCTION.
2. SEE TRACKWORK PLANS (T) FOR TRACK DRAIN DETAILS, SWITCH MACHINE DRAIN DETAILS, AND TRACK-RELATED WORK.
3. SEE STREET IMPROVEMENT PLANS (C) FOR ROADWAY-RELATED WORK.
4. SEE VOLUME 2 STORM DRAIN PLANS (D) LA COUNTY FLOOD CONTROL DISTRICT (LACFCD) RELATED STORM DRAIN IMPROVEMENTS.
5. ALL NEW TRACK DRAINS UNDER THIS PROJECT SHALL INCLUDE SCREENS.
6. ALL NEW AND REMOVED/REPLACED CATCH BASINS UNDER THIS PROJECT SHALL INCLUDE CATCH BASIN OPENING SCREENS. REUSE EXISTING SCREENS WHEN APPLICABLE.
7. ALL NEW AND REMOVED/REPLACED CATCH BASINS UNDER THIS PROJECT SHALL BE STENCILED WITH PROHIBITIVE LANGUAGE "NO DUMPING - DRAIN TO OCEAN."

PROFILE SCALE
HORIZ: 1"=20'
VERT: 1"=4'

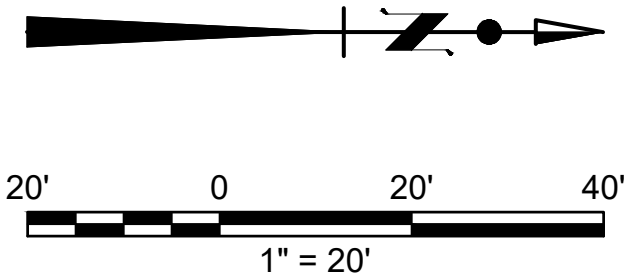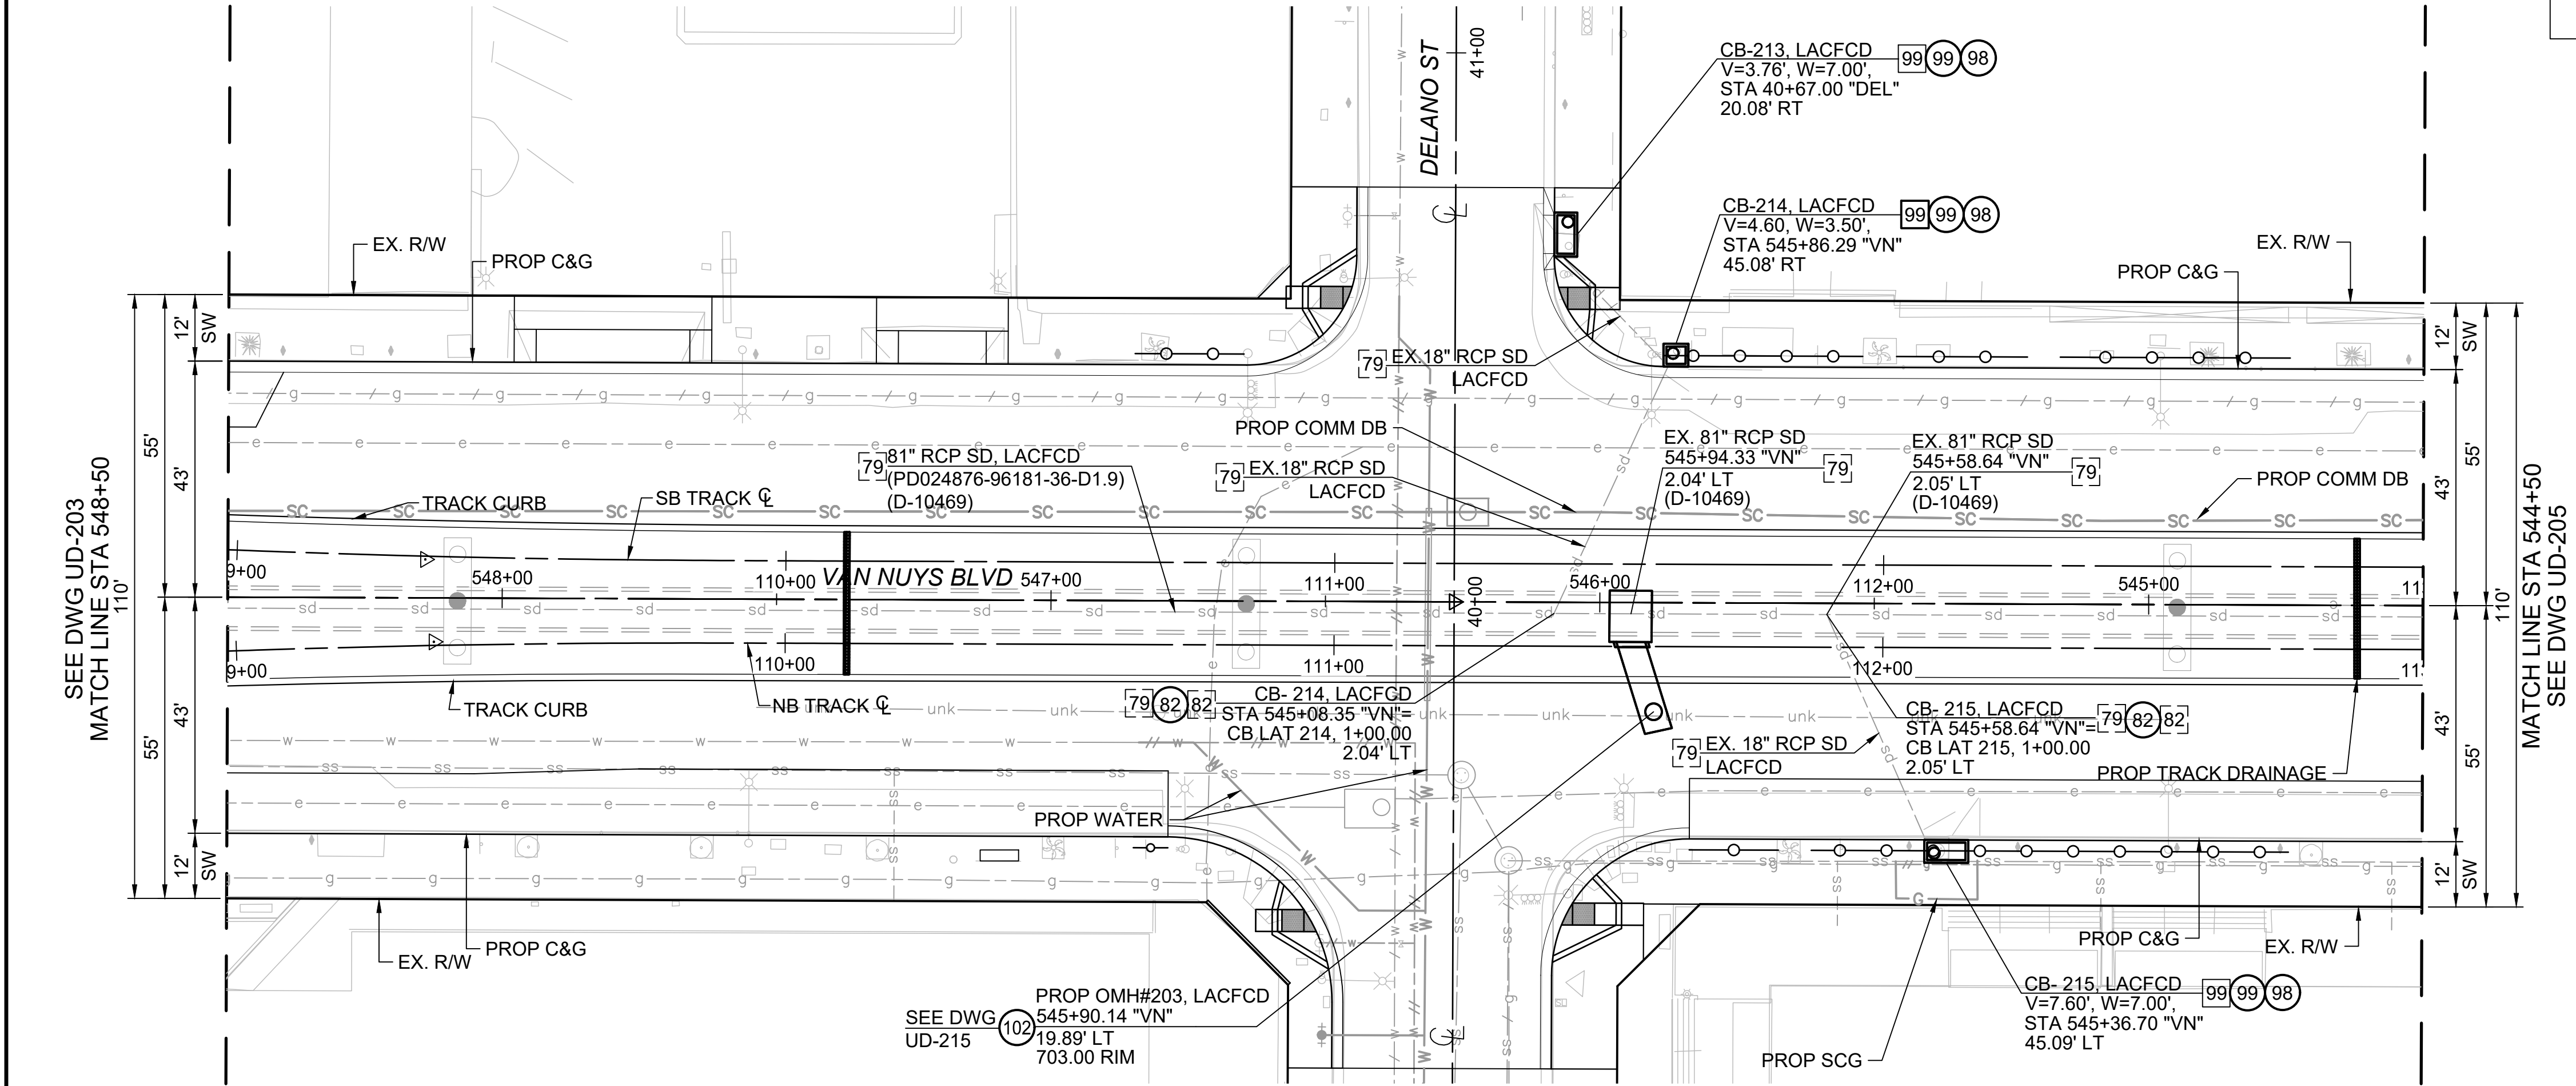

THE PREPARATION OF THIS DRAWING HAS BEEN FINANCED IN PART THROUGH A GRANT FROM THE U.S. DEPARTMENT OF TRANSPORTATION, FEDERAL TRANSIT ADMINISTRATION (FTA), UNDER THE FEDERAL TRANSIT ACT OF 1964, AS AMENDED, AND IN PART BY THE TAXES OF THE CITIZENS OF LOS ANGELES COUNTY AND OF THE STATE OF CALIFORNIA.							DESIGNED BY N. SOTO
							DRAWN BY R. VENEGAS
							CHECKED BY N. BUSCH
							IN CHARGE N. BUSCH
							DATE 12/11/2025
C	12/15/25	NS	JR	C78082	09/30/27	J. RIMORIN	100% SUBMITTAL
B	08/18/25	AR	NB	C65608	09/30/27	N. BUSCH	85% SUBMITTAL
A	03/07/25	KM	JR	C78082	09/30/27	J. RIMORIN	60% SUBMITTAL
REV	DATE	BY	APP	REG NO	EXPIRES	SEAL HOLDER	DESCRIPTION

**LOS ANGELES COUNTY**
METROPOLITAN TRANSPORTATION AUTHORITY

**San Fernando Transit Constructors**

**AECOM**

**V&A INC**
1111 S. GARDEN AVE. SUITE 103
LOS ANGELES, CA 90015
213.972.0700

14300 ARMINTA ST.
LOS ANGELES, CA 91402
TEL: 951.684.5360

100% SUBMITTAL - NOT FOR CONSTRUCTION

EAST SAN FERNANDO VALLEY LRT
DU06 - DRAINAGE SEGMENT A1
STORM DRAIN PLAN AND PROFILE
VAN NUYS BLVD STA 544+50 TO 548+50


CONTRACT NO
PS89616000

DRAWING NO
UD-204

SCALE
1" = 20'

SHEET NO

FILE PATH: \\S072457-ESFV-PH2\PROJECT FILES\900_CAD\20_SHEETS\DU06\09_UD_DRAINAGE\PS89616000-DU06-UD-204_NS\WORKING.DWG
PLOT DATE: 12/16/2025 - 4:47 PM USER: ADRIANROBLES

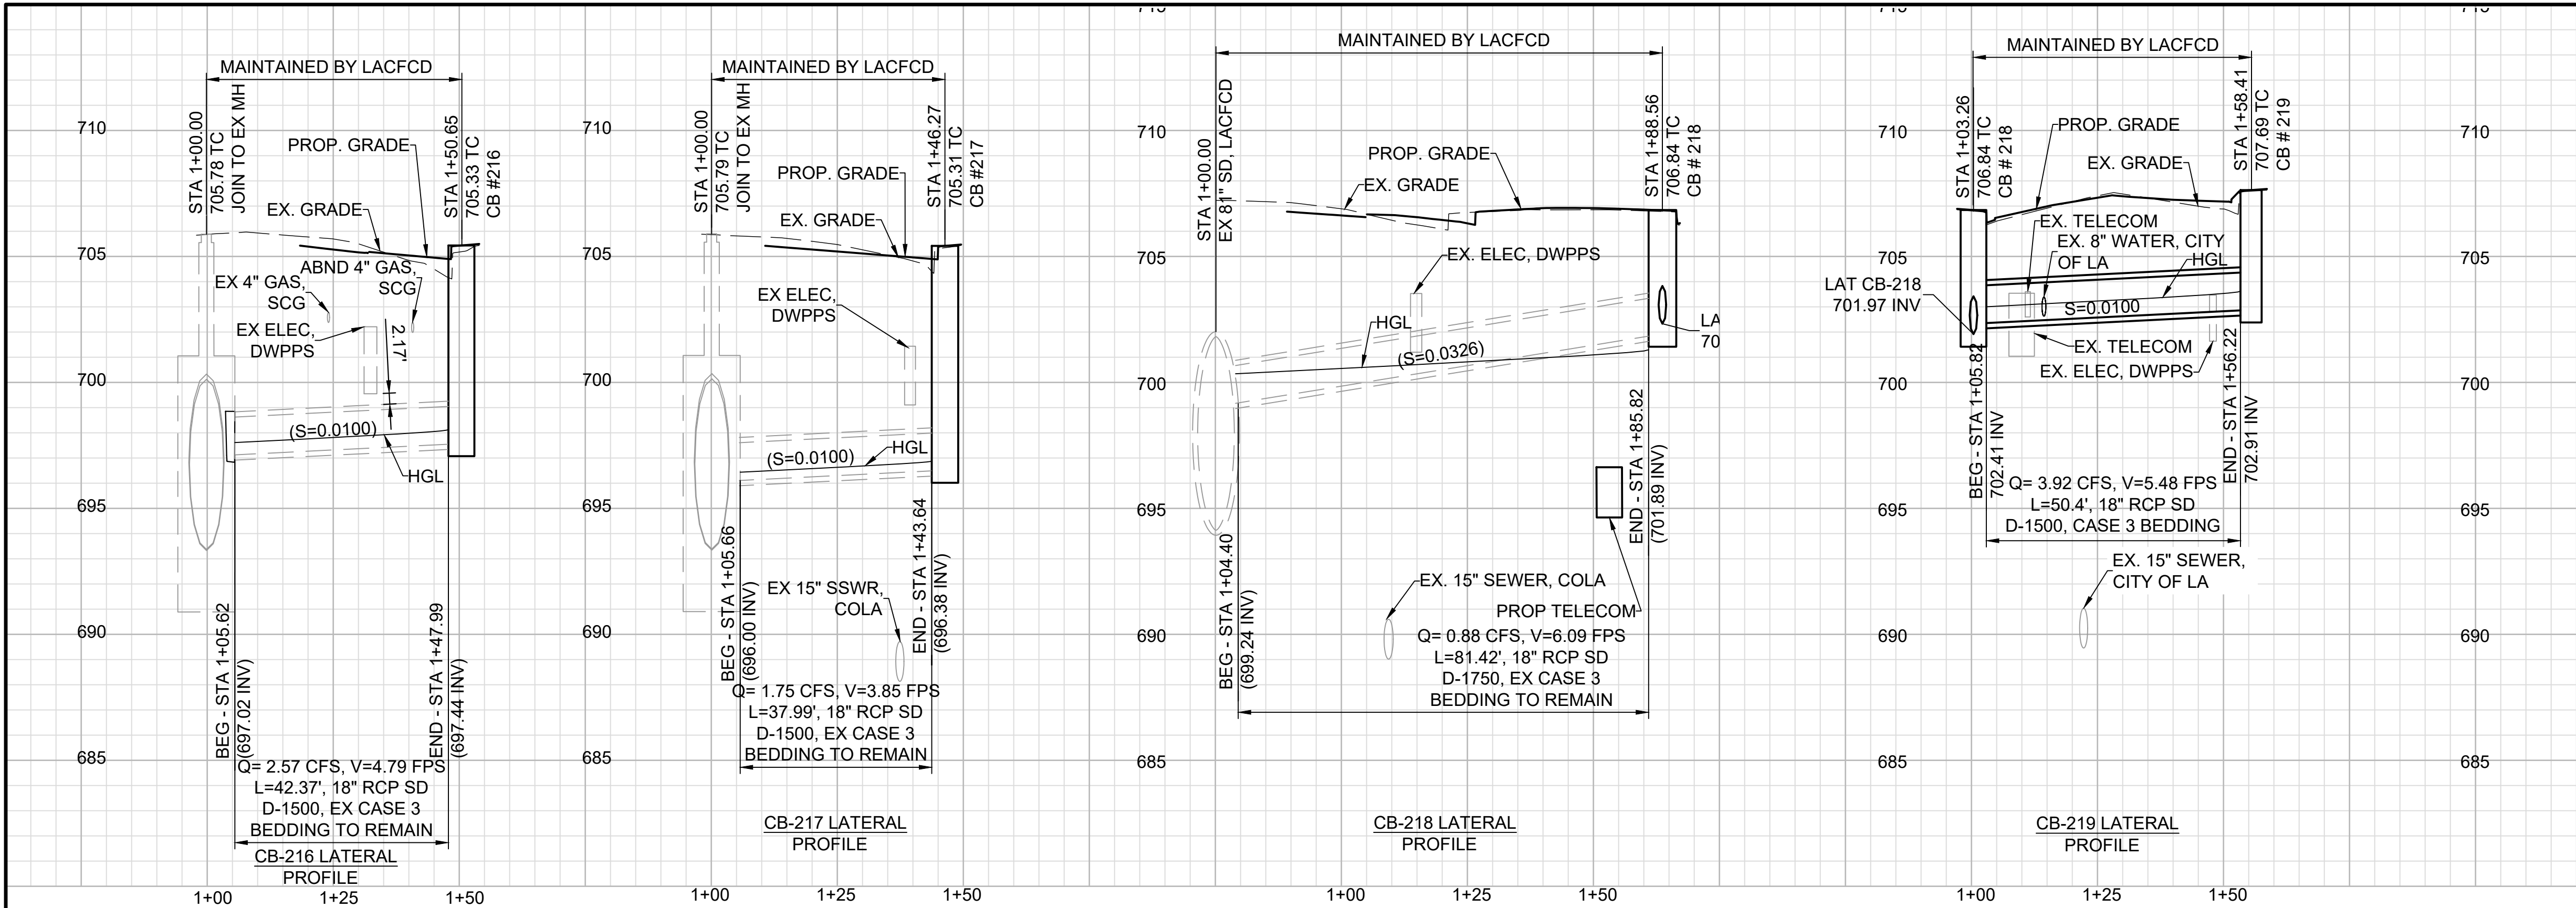

CONSTRUCTION SYMBOLS:

- CONSTRUCT
- REMODEL EXISTING
- EXISTING
- REMOVE AND CONSTRUCT
- REMOVE
- WORK BY OTHERS



CONSTRUCTION NOTES:

- 79 REINFORCED CONCRETE PIPE
- 82 JUNCTION STRUCTURE
- 85 STORM DRAIN MANHOLE
- 97 CONCRETE COLLAR
- 98 MONOLITHIC CATCH BASIN CONNECTION
- 99 CURB OPENING CATCH BASIN
- 102 OFFSET MANHOLE "TYPE B"
- 115 CAP MH

NOTES:

- SEE COMPOSITE UTILITY REARRANGEMENT PLANS (UR) FOR EXISTING UTILITY CONFLICTS AND PROPOSED RELOCATIONS. CONTRACTOR TO DETERMINE UTILITY DEPTHS AND LOCATIONS ON STORM DRAIN PROFILES PRIOR TO CONSTRUCTION.
- SEE TRACKWORK PLANS (T) FOR TRACK DRAIN DETAILS, SWITCH MACHINE DRAIN DETAILS, AND TRACK-RELATED WORK.
- SEE STREET IMPROVEMENT PLANS (CS) FOR ROADWAY-RELATED WORK.
- SEE DU04-SEGMENT B METRO TRACK GUIDEWAY PLANS (D) FOR TRACK GUIDEWAY STORM DRAIN IMPROVEMENTS.
- ALL NEW AND REMOVED/REPLACED CATCH BASINS UNDER THIS PROJECT SHALL INCLUDE CATCH BASIN OPENING SCREENS AND INSERTS. REUSE EXISTING SCREENS WHEN APPLICABLE.
- ALL NEW AND REMOVED/REPLACED CATCH BASINS UNDER THIS PROJECT SHALL BE STENCILED WITH PROHIBITIVE LANGUAGE "NO DUMPING - DRAIN TO OCEAN."
- SEE TRAFFIC AND SIGNAL PLANS FOR SIGNAL RELATED WORK

PROFILE SCALE
HORIZ: 1"=20'
VERT: 1"=4'

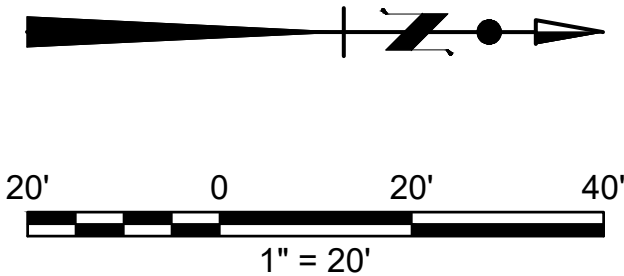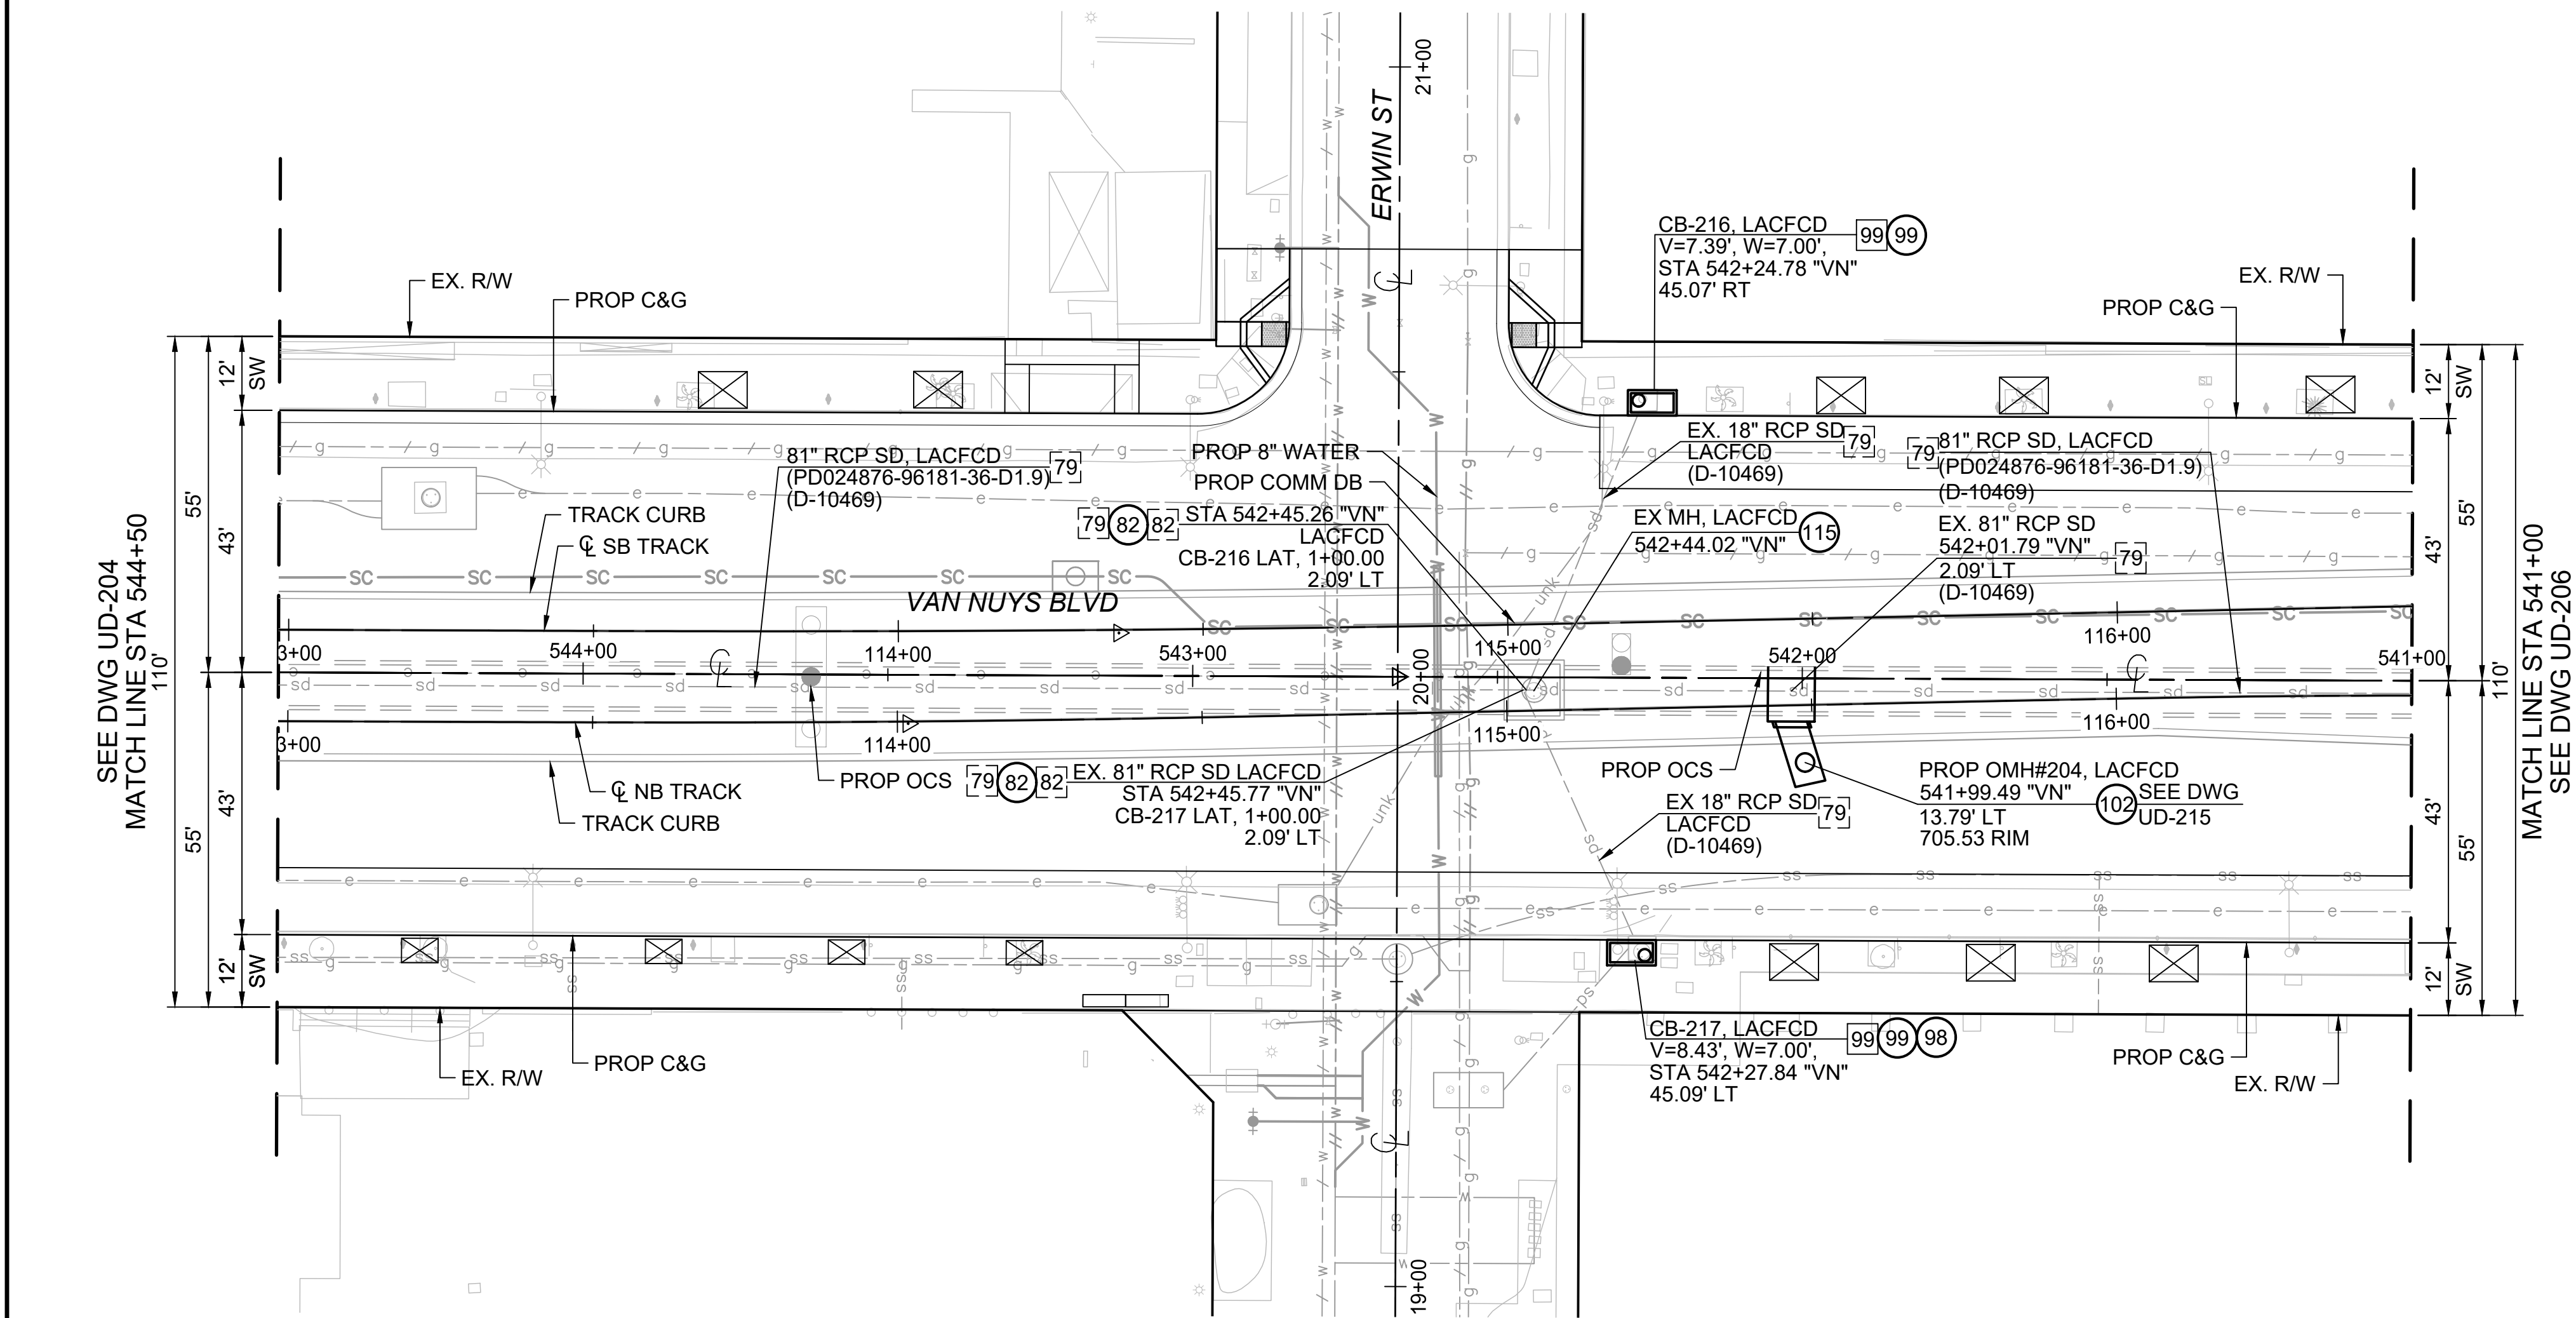

THE PREPARATION OF THIS DRAWING HAS BEEN FINANCED IN PART THROUGH A GRANT FROM THE U.S. DEPARTMENT OF TRANSPORTATION, FEDERAL TRANSIT ADMINISTRATION (FTA), UNDER THE FEDERAL TRANSIT ACT OF 1964, AS AMENDED, AND IN PART BY THE TAXES OF THE CITIZENS OF LOS ANGELES COUNTY AND OF THE STATE OF CALIFORNIA.									
DESIGNED BY	N. SOTO								
DRAWN BY	R. VENEGAS								
CHECKED BY	N. BUSCH								
IN CHARGE	N. BUSCH								
DATE	12/11/2025								
REV	DATE	BY	APP	REG NO	EXPIRES	SEAL HOLDER	DESCRIPTION		
C	12/15/25	NS	JR	C78082	09/30/27	J. RIMORIN	100% SUBMITTAL		
B	08/18/25	AR	NB	C65608	09/30/27	N. BUSCH	85% SUBMITTAL		
A	03/07/25	KM	JR	C78082	09/30/27	J. RIMORIN	60% SUBMITTAL		



LOS ANGELES COUNTY
METROPOLITAN TRANSPORTATION AUTHORITY



San Fernando Transit
Constructors



AECOM

14300 ARMINTA ST.
LOS ANGELES, CA 91402
TEL: 951.684.5360



V&A INC
1111 S. GRAND AVE. SUITE 103
LOS ANGELES, CA 90015
213.922.0081

100% SUBMITTAL - NOT FOR CONSTRUCTION

EAST SAN FERNANDO VALLEY LRT
DU06 - DRAINAGE SEGMENT A1
STORM DRAIN PLAN AND PROFILE
VAN NUYS BLVD STA 541+00 TO 544+50


CONTRACT NO
PS89616000

DRAWING NO
UD-205

SCALE
1" = 20'

SHEET NO

FILE PATH: \\N0724957-ESFV-PH2\PROJECT FILES\900_CAD\20_SHEETS\DU06\09_UD_DRAINAGE\PS89616000-DU06-UD-205.DWG
PLOT DATE: 12/16/2025 - 5:26 PM USER: NEREDASOTO

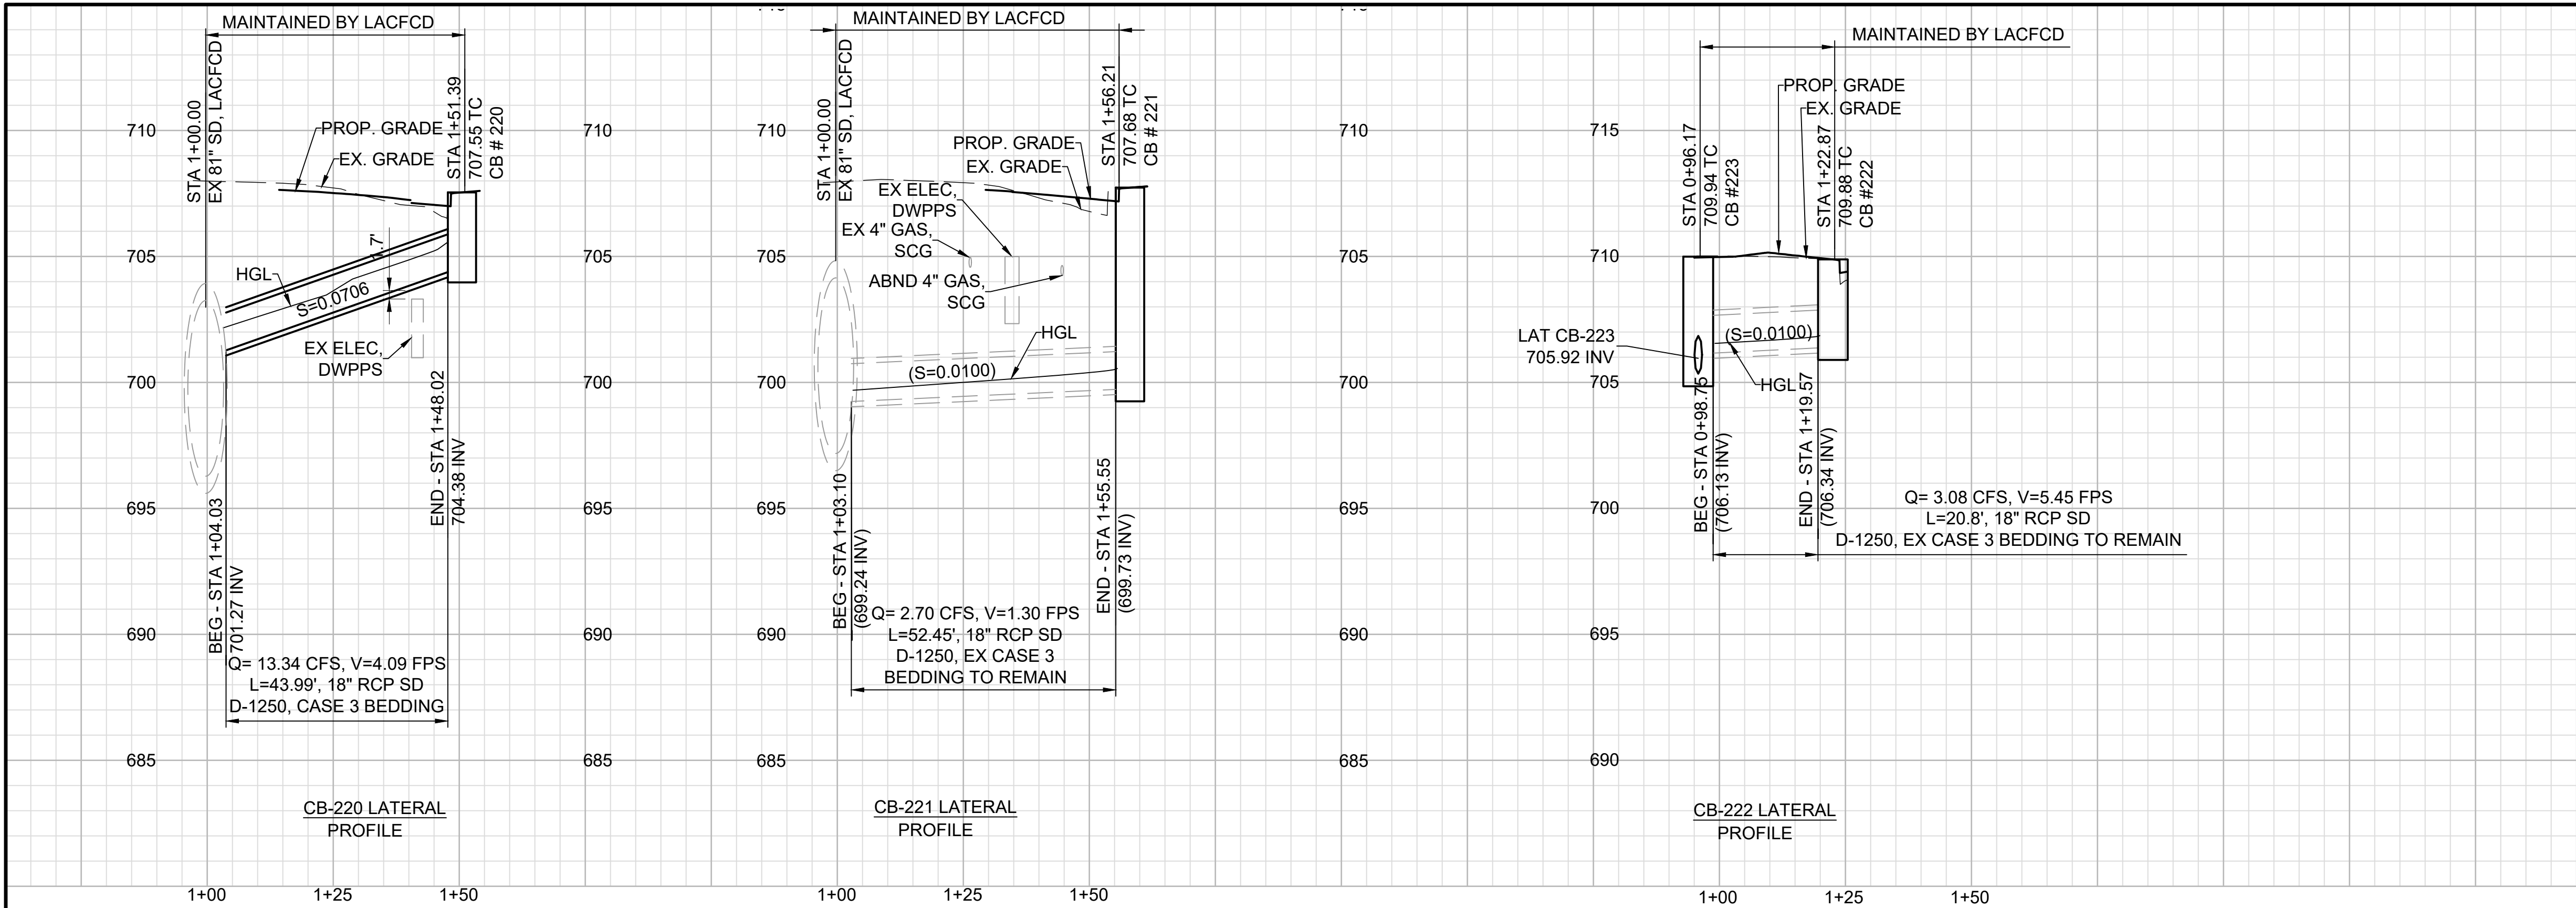

PROFILE SCALE
HORIZ: 1"=20'
VERT: 1"=4'

CONSTRUCTION SYMBOLS:

- CONSTRUCT ◻ REMODEL EXISTING
◻ EXISTING ◻○ REMOVE AND CONSTRUCT
◻ REMOVE ⦿ WORK BY OTHERS



CONSTRUCTION NOTES:

- 79 REINFORCED CONCRETE PIPE
82 JUNCTION STRUCTURE
85 STORM DRAIN MANHOLE
97 CONCRETE COLLAR
98 MONOLITHIC CATCH BASIN CONNECTION
99 CURB OPENING CATCH BASIN
102 OFFSET MANHOLE "TYPE B"
115 CAP MH

NOTES:

- SEE COMPOSITE UTILITY REARRANGEMENT PLANS (UR) FOR EXISTING UTILITY CONFLICTS AND PROPOSED RELOCATIONS. CONTRACTOR TO DETERMINE UTILITY DEPTHS AND LOCATIONS ON STORM DRAIN PROFILES PRIOR TO CONSTRUCTION.
- SEE TRACKWORK PLANS (T) FOR TRACK DRAIN DETAILS, SWITCH MACHINE DRAIN DETAILS, AND TRACK-RELATED WORK.
- SEE STREET IMPROVEMENT PLANS (CS) FOR ROADWAY-RELATED WORK.
- SEE DU04-SEGMENT B METRO TRACK GUIDEWAY PLANS (D) FOR TRACK GUIDEWAY STORM DRAIN IMPROVEMENTS.
- ALL NEW AND REMOVED/REPLACED CATCH BASINS UNDER THIS PROJECT SHALL INCLUDE CATCH BASIN OPENING SCREENS AND INSERTS. REUSE EXISTING SCREENS WHEN APPLICABLE.
- ALL NEW AND REMOVED/REPLACED CATCH BASINS UNDER THIS PROJECT SHALL BE STENCILED WITH PROHIBITIVE LANGUAGE "NO DUMPING - DRAIN TO OCEAN."
- SEE TRAFFIC AND SIGNAL PLANS FOR SIGNAL RELATED WORK.
- PROTECT IN PLACE ALL EXISTING BEDDING, UNLESS STATED ON PROFILE.

LINE/CURVE DATA TABLE			
NO.	LENGTH	BEARING/DELTA	RADIUS
L1	81.96	N60° 56' 22.60"E	--
L2	51.48	N07° 35' 31.53"W	--
L3	45.28	S57° 20' 18.01"W	--
L4	2.76	N56° 42' 13.33"W	--

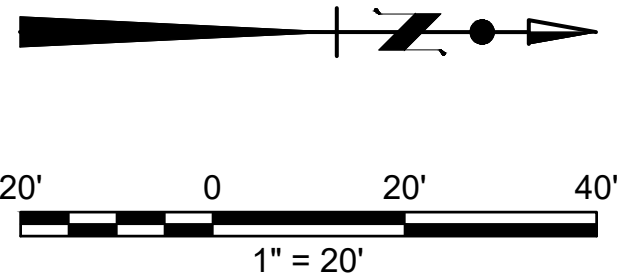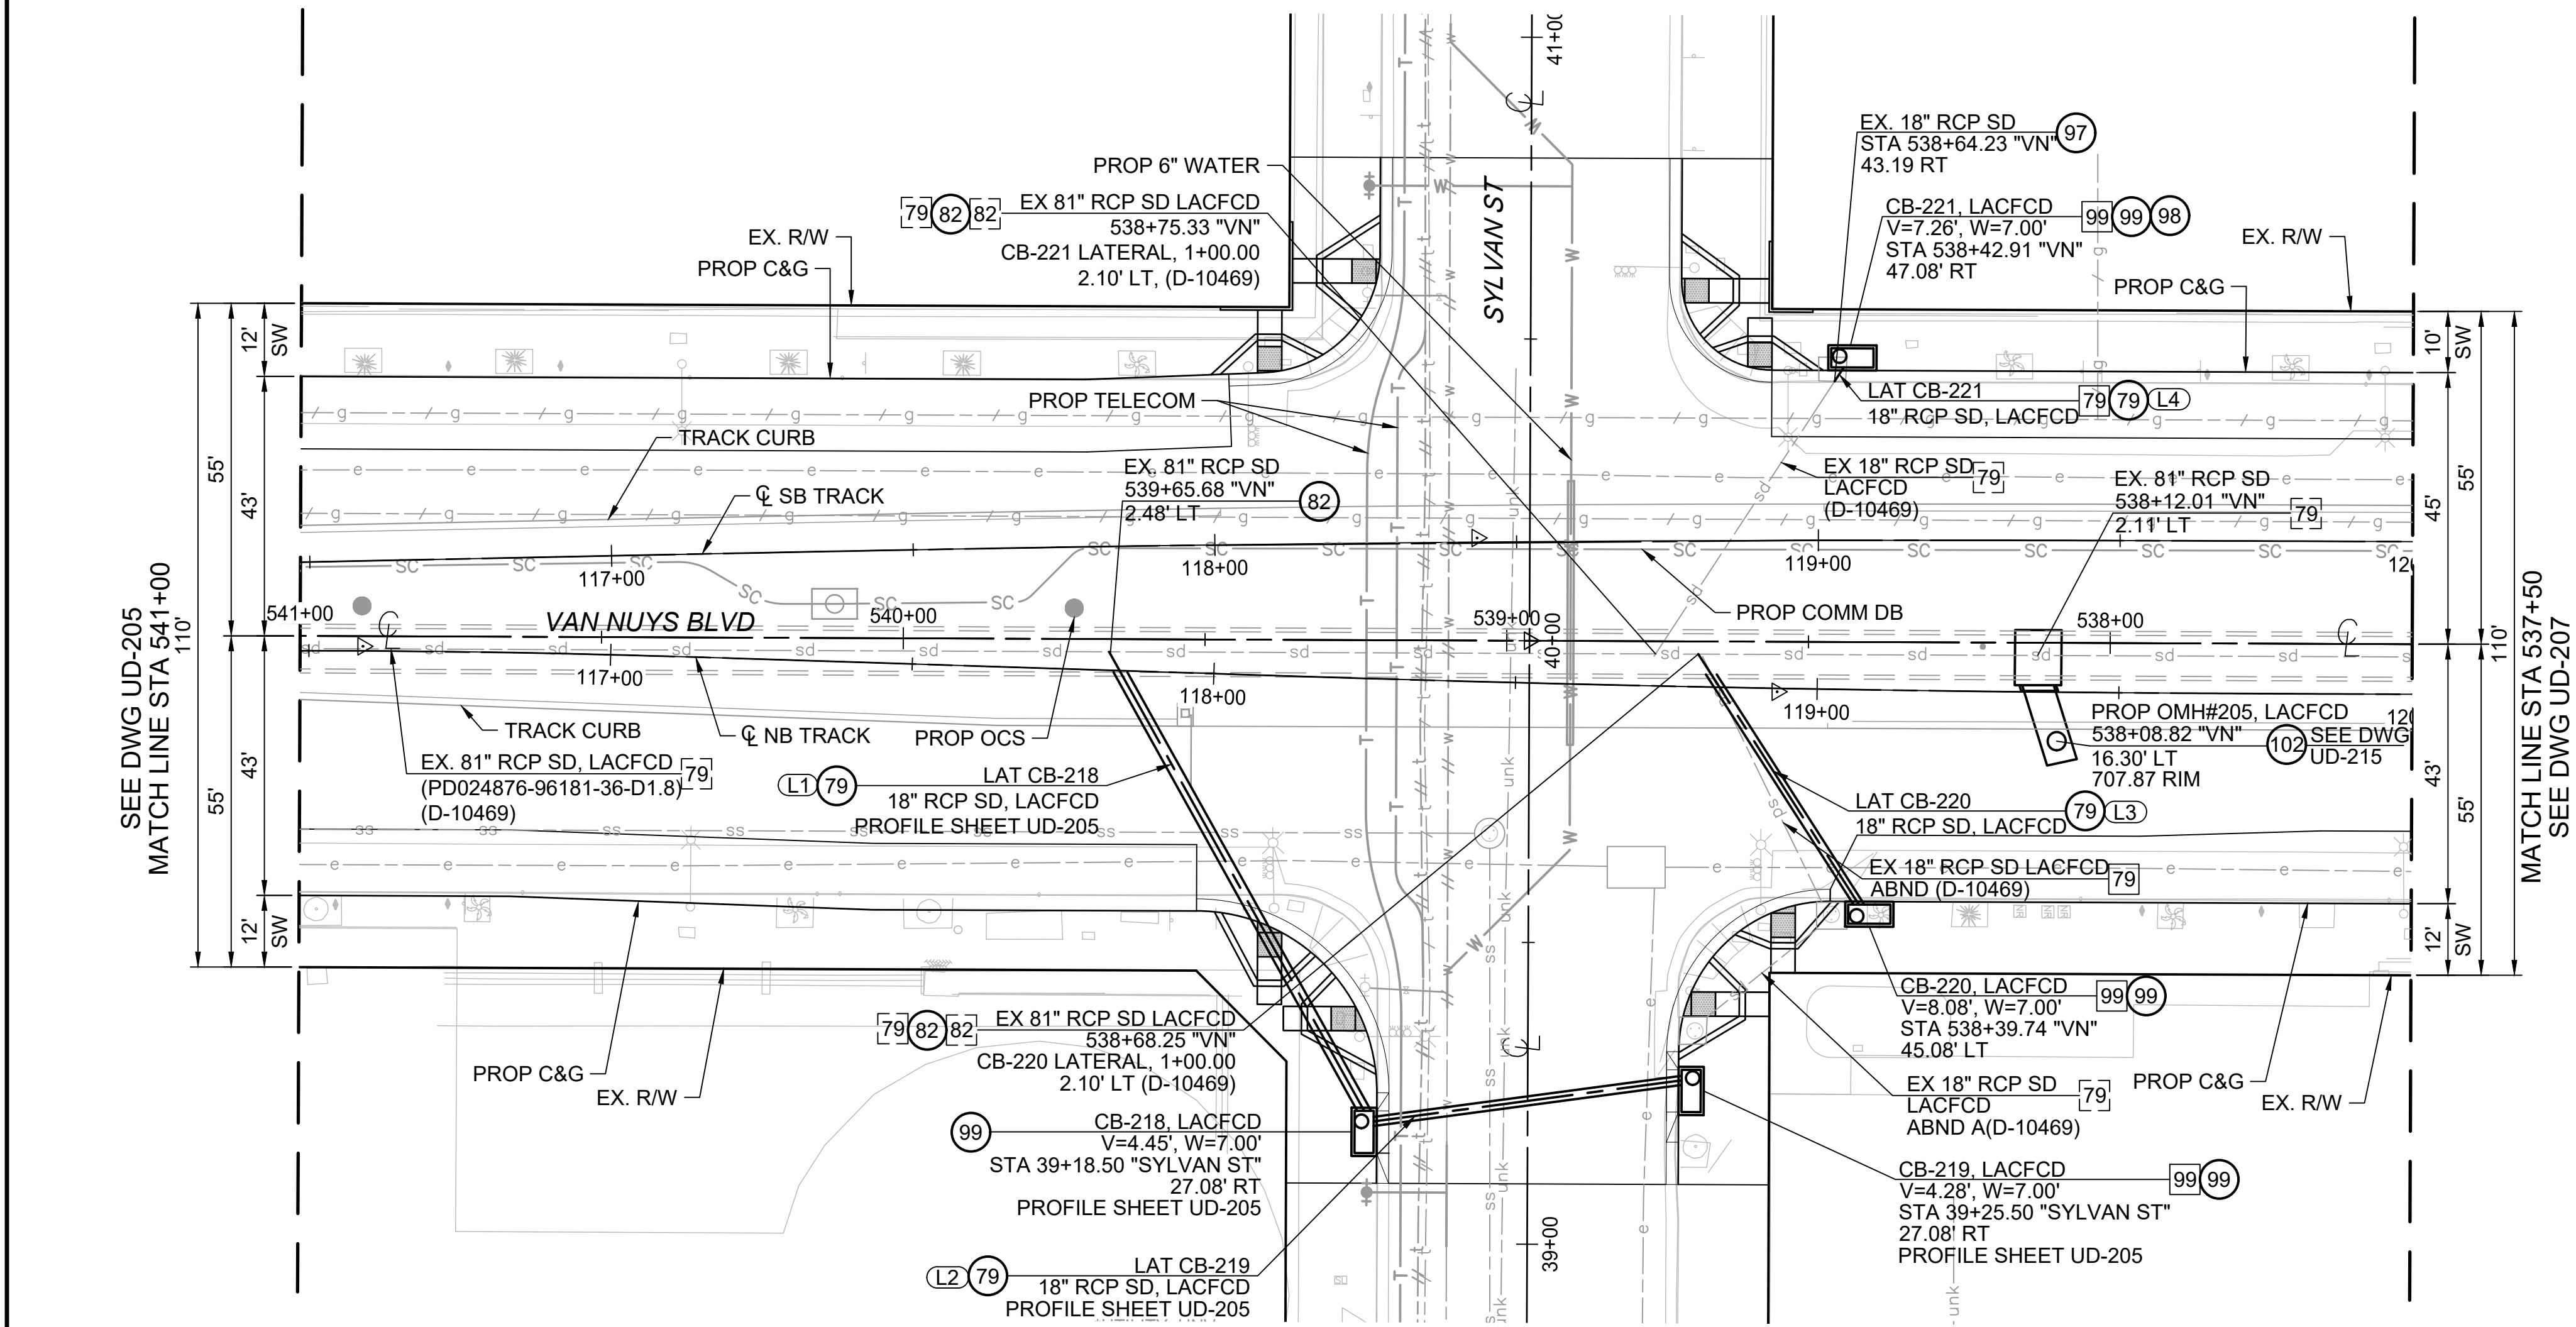

THE PREPARATION OF THIS DRAWING HAS BEEN FINANCED IN PART THROUGH A GRANT FROM THE U.S. DEPARTMENT OF TRANSPORTATION, FEDERAL TRANSIT ADMINISTRATION (FTA), UNDER THE FEDERAL TRANSIT ACT OF 1964, AS AMENDED, AND IN PART BY THE TAXES OF THE CITIZENS OF LOS ANGELES COUNTY AND OF THE STATE OF CALIFORNIA.							
REV	DATE	BY	APP	REG NO	EXPIRES	SEAL HOLDER	DESCRIPTION
C	12/15/25	NS	JR	C78082	09/30/27	J. RIMORIN	100% SUBMITTAL
B	08/18/25	AR	NB	C65608	09/30/27	N. BUSCH	85% SUBMITTAL
A	03/07/25	KM	JR	C78082	09/30/27	J. RIMORIN	60% SUBMITTAL

DESIGNED BY N. SOTO
DRAWN BY R. VENEGAS
CHECKED BY N. BUSCH
IN CHARGE N. BUSCH
DATE 12/11/2025

**LOS ANGELES COUNTY**
METROPOLITAN TRANSPORTATION AUTHORITY

**San Fernando Transit Constructors**


**AECOM**

100% SUBMITTAL - NOT FOR CONSTRUCTION

EAST SAN FERNANDO VALLEY LRT
DU06 - DRAINAGE SEGMENT A1
STORM DRAIN PLAN AND PROFILE
VAN NUYS BLVD STA 537+50 TO 541+00

CONTRACT NO PS89616000
DRAWING NO UD-206
SCALE 1" = 20'
SHEET NO

FILE PATH: \\S0724957-ESFV-PH2\PROJECT FILES\900_CAD\20_SHEETS\DU06\09_UD_DRAINAGE\PS89616000-DU06-UD-206.DWG
PLOT DATE: 12/16/2025 - 1:32 PM USER: ADRIANROBLES

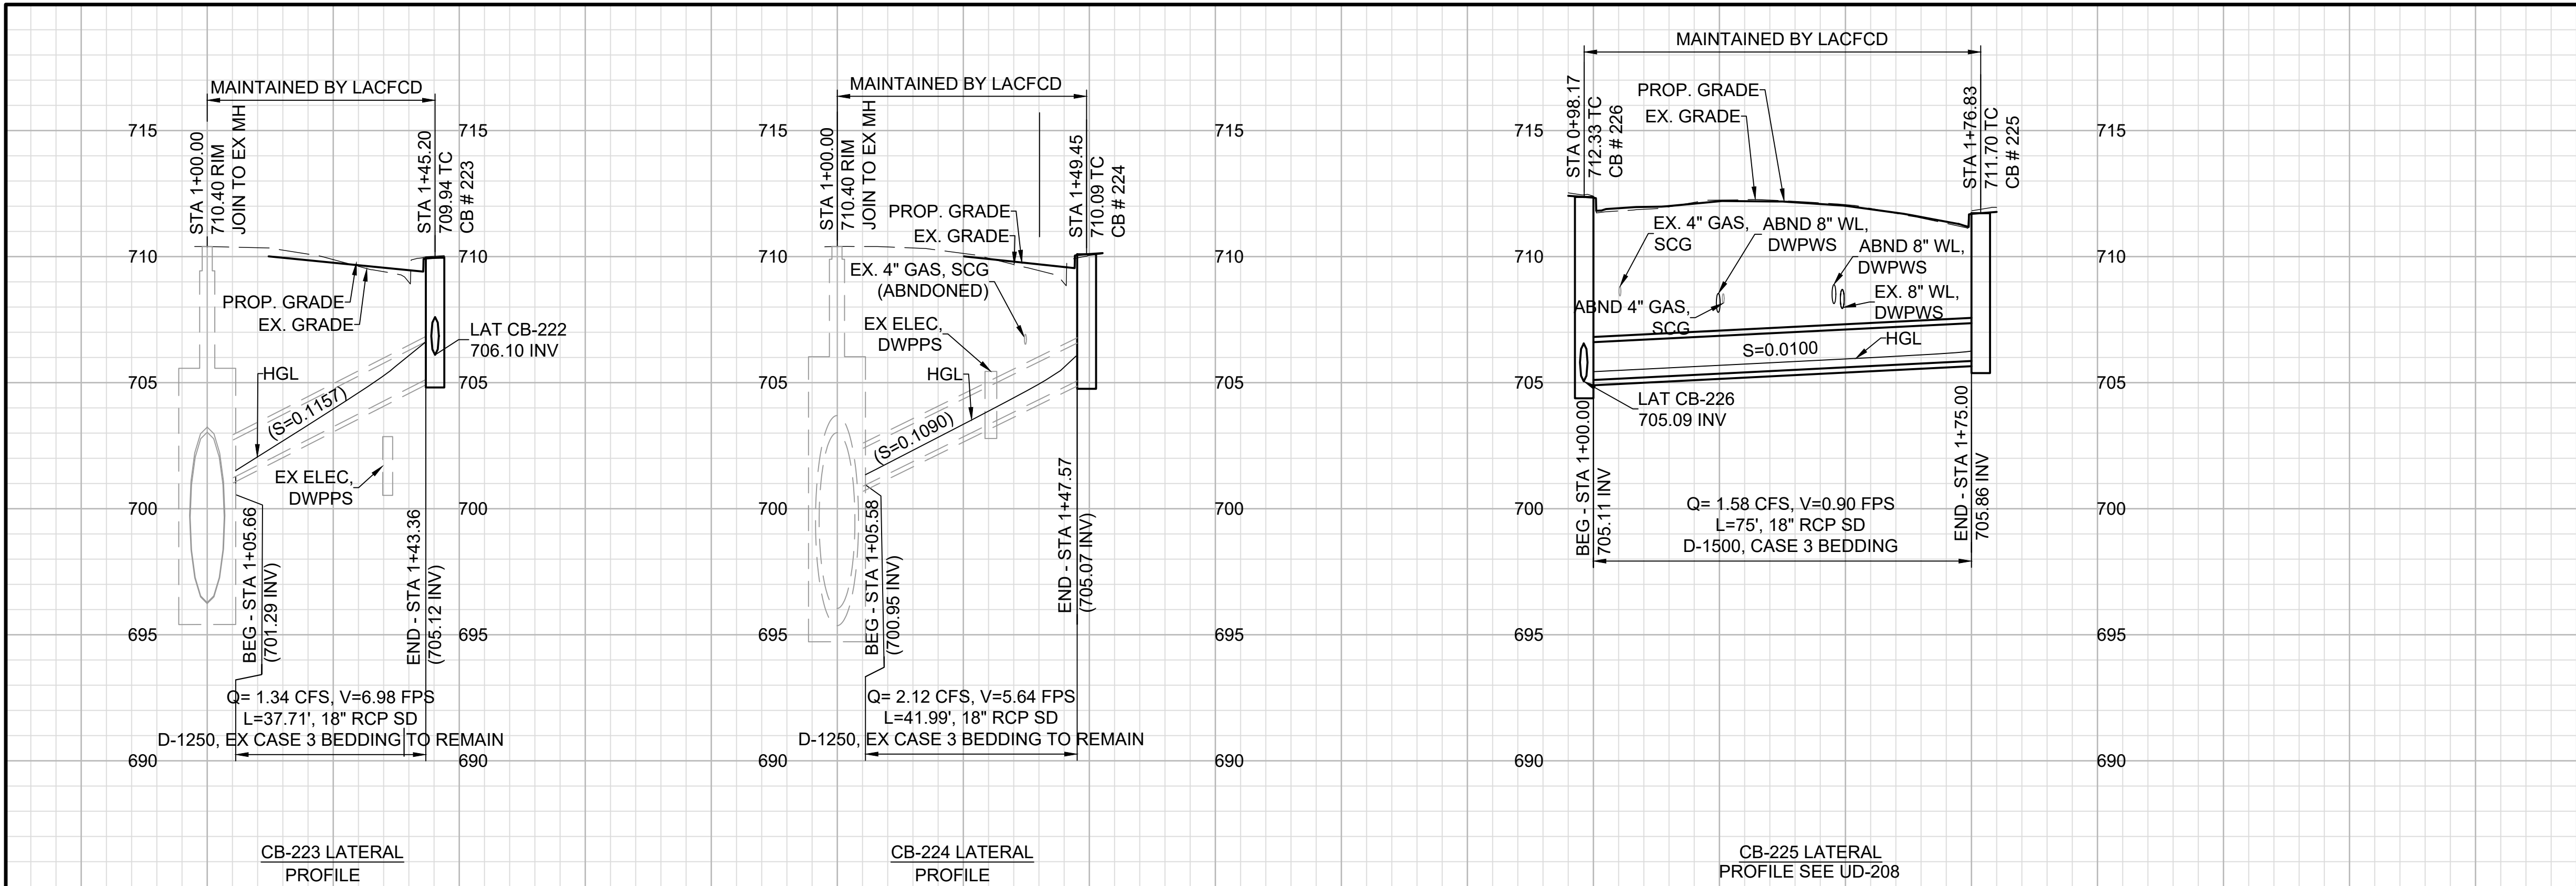

PROFILE SCALE
HORIZ: 1"=20'
VERT: 1"=4'

CONSTRUCTION SYMBOLS:

- CONSTRUCT ○◻ REMODEL EXISTING
◻ EXISTING ◻○ REMOVE AND CONSTRUCT
◻ REMOVE ○ WORK BY OTHERS



CONSTRUCTION NOTES:

- 79 REINFORCED CONCRETE PIPE
82 JUNCTION STRUCTURE
85 STORM DRAIN MANHOLE
97 CONCRETE COLLAR
98 MONOLITHIC CATCH BASIN CONNECTION
99 CURB OPENING CATCH BASIN
102 OFFSET MANHOLE "TYPE B"
115 CAP MH

NOTES:

- SEE COMPOSITE UTILITY REARRANGEMENT PLANS (UR) FOR EXISTING UTILITY CONFLICTS AND PROPOSED RELOCATIONS. CONTRACTOR TO DETERMINE UTILITY DEPTHS AND LOCATIONS ON STORM DRAIN PROFILES PRIOR TO CONSTRUCTION.
- SEE TRACKWORK PLANS (T) FOR TRACK DRAIN DETAILS, SWITCH MACHINE DRAIN DETAILS, AND TRACK-RELATED WORK.
- SEE STREET IMPROVEMENT PLANS (CS) FOR ROADWAY-RELATED WORK.
- SEE DU04-SEGMENT B METRO TRACK GUIDEWAY PLANS (D) FOR TRACK GUIDEWAY STORM DRAIN IMPROVEMENTS.
- ALL NEW AND REMOVED/REPLACED CATCH BASINS UNDER THIS PROJECT SHALL INCLUDE CATCH BASIN OPENING SCREENS AND INSERTS. REUSE EXISTING SCREENS WHEN APPLICABLE.
- ALL NEW AND REMOVED/REPLACED CATCH BASINS UNDER THIS PROJECT SHALL BE STENCILED WITH PROHIBITIVE LANGUAGE "NO DUMPING - DRAIN TO OCEAN."
- SEE TRAFFIC AND SIGNAL PLANS FOR SIGNAL RELATED WORK.
- PROTECT IN PLACE ALL EXISTING BEDDING, UNLESS STATED ON PROFILE.

LINE/CURVE DATA TABLE			
NO.	LENGTH	BEARING/DELTA	RADIUS
L1	2.66	S89° 46' 52.33"E	-
L2	2.04	S89° 50' 16.37"E	-

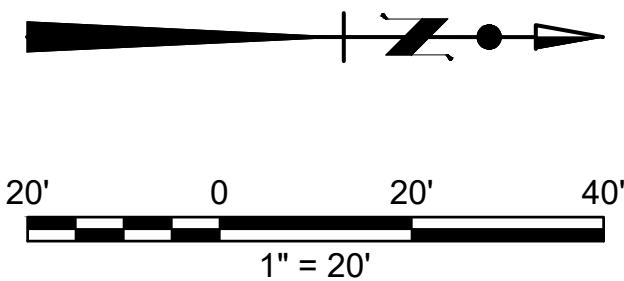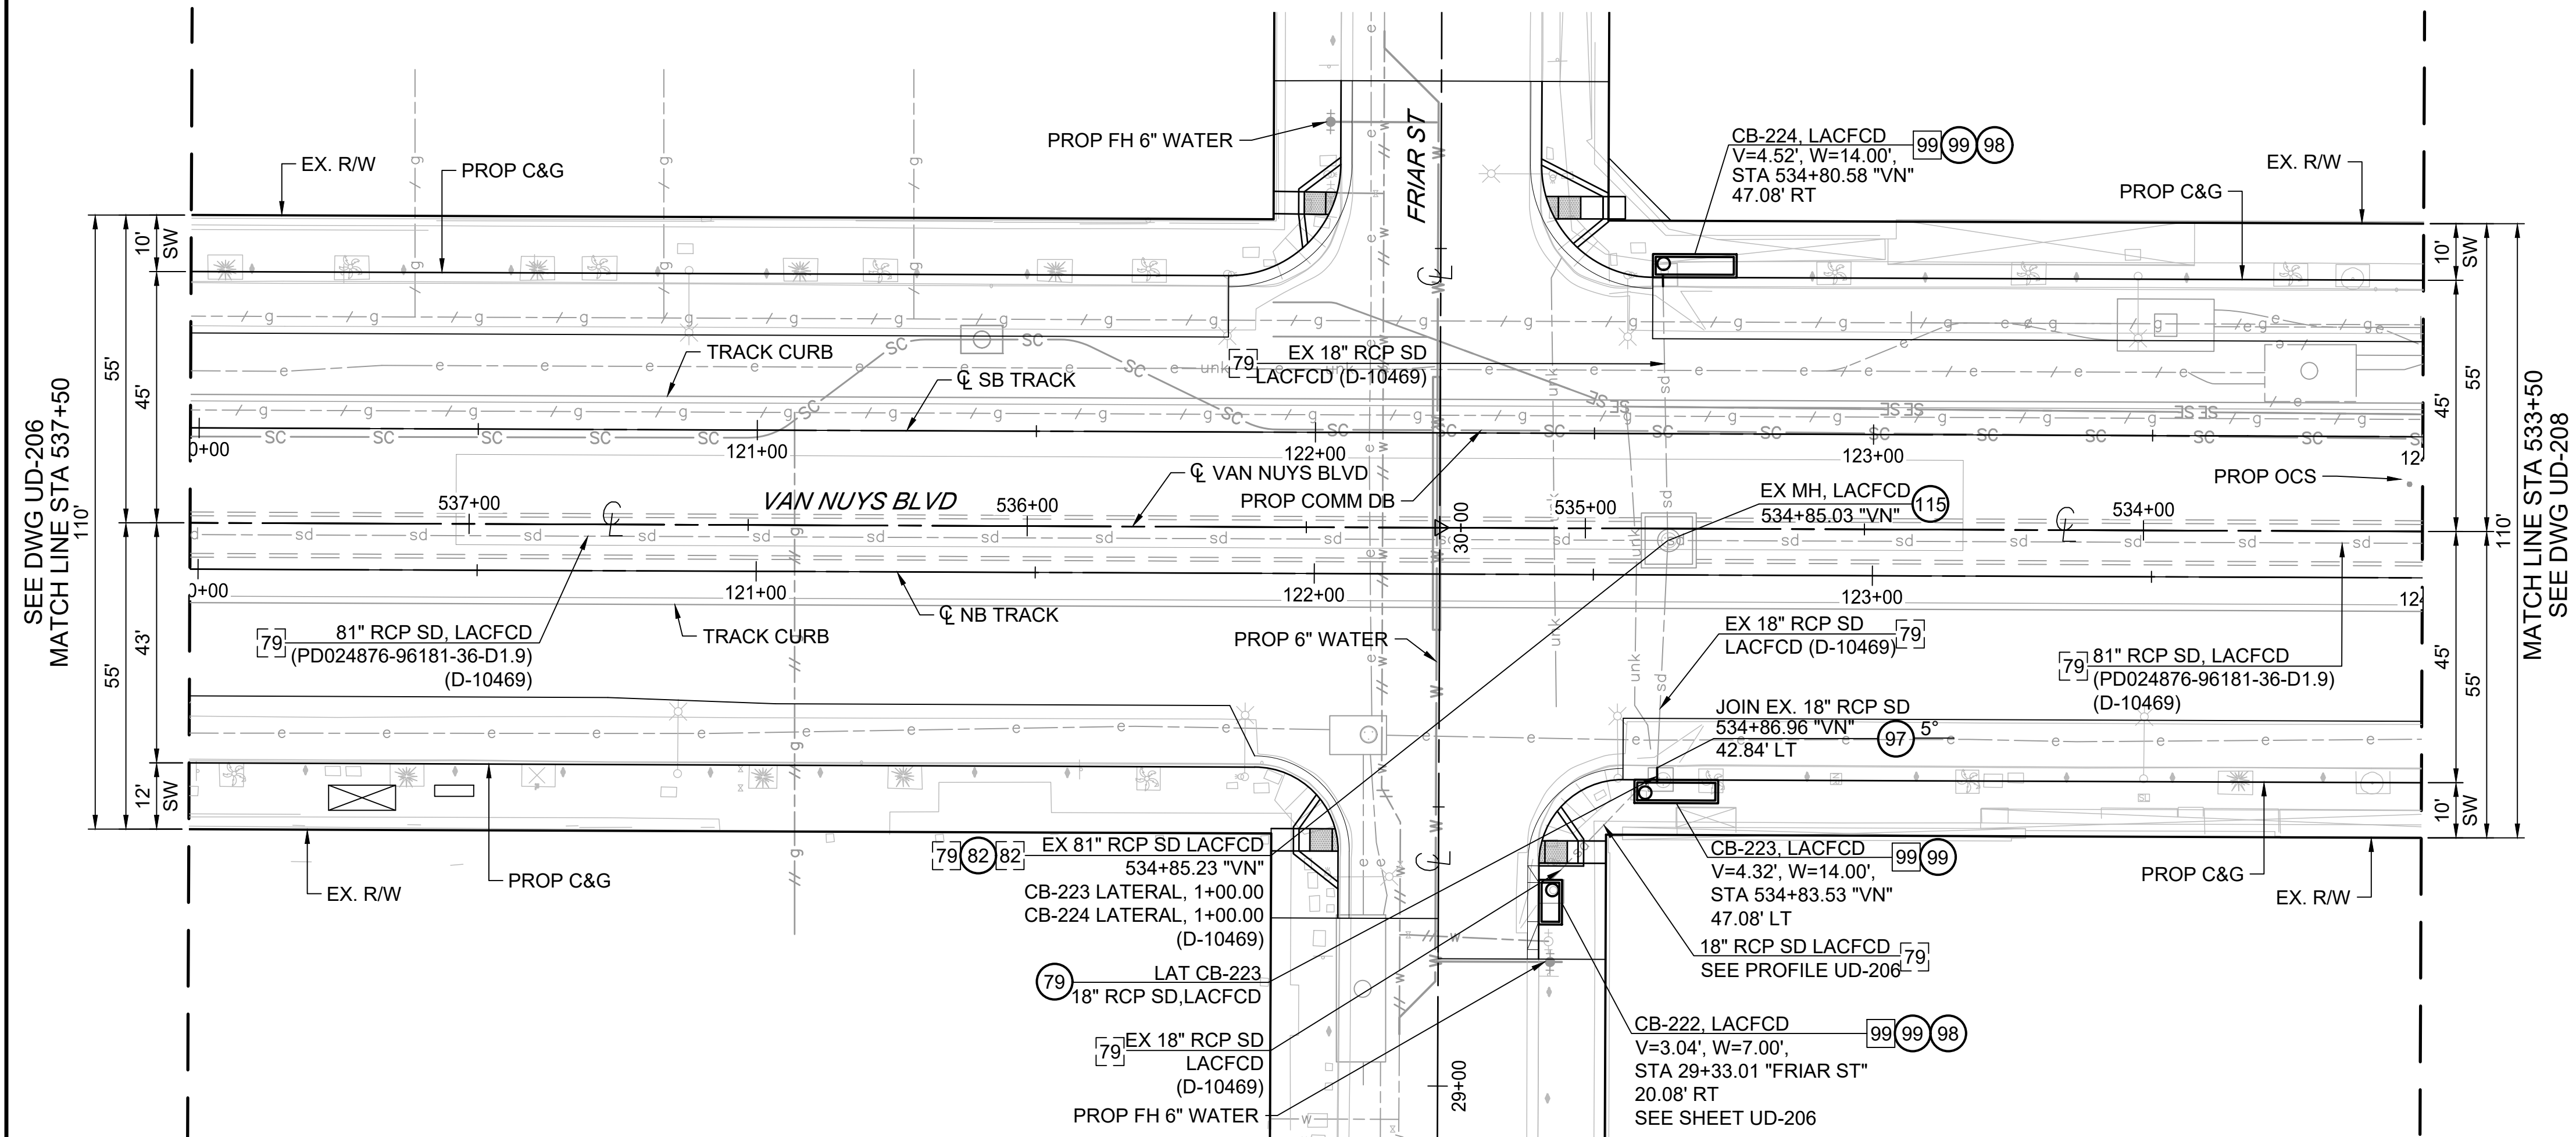

THE PREPARATION OF THIS DRAWING HAS BEEN FINANCED IN PART THROUGH A GRANT FROM THE U.S. DEPARTMENT OF TRANSPORTATION, FEDERAL TRANSIT ADMINISTRATION (FTA), UNDER THE FEDERAL TRANSIT ACT OF 1964, AS AMENDED, AND IN PART BY THE TAXES OF THE CITIZENS OF LOS ANGELES COUNTY AND OF THE STATE OF CALIFORNIA.						
REV	DATE	BY	APP	REG NO	EXPIRES	SEAL HOLDER
C	12/15/25	NS	JR	C78082	09/30/27	J. RIMORIN
B	08/18/25	AR	NB	C65608	09/30/27	N. BUSCH
A	03/07/25	KM	JR	C78082	09/30/27	J. RIMORIN
						DESCRIPTION
						100% SUBMITTAL
						85% SUBMITTAL
						60% SUBMITTAL

DESIGNED BY N. SOTO
DRAWN BY R. VENEGAS
CHECKED BY N. BUSCH
IN CHARGE N. BUSCH
DATE 12/11/2025



LOS ANGELES COUNTY
METROPOLITAN TRANSPORTATION AUTHORITY




100% SUBMITTAL - NOT FOR CONSTRUCTION

EAST SAN FERNANDO VALLEY LRT
DU06 - DRAINAGE SEGMENT A1
STORM DRAIN PLAN AND PROFILE
VAN NUYS BLVD STA 533+50 TO 537+50

CONTRACT NO PS89616000
DRAWING NO UD-207
SCALE 1" = 20'
SHEET NO

FILE PATH: \\S072457-ESFV-PH2\PROJECT FILES\900_CAD\20_SHEETS\DU06\99_UD_DRAINAGE\PS89616000-DU06-UD-207.DWG
PLOT DATE: 12/16/2025 - 2:00 PM USER: ADRIANROBLES

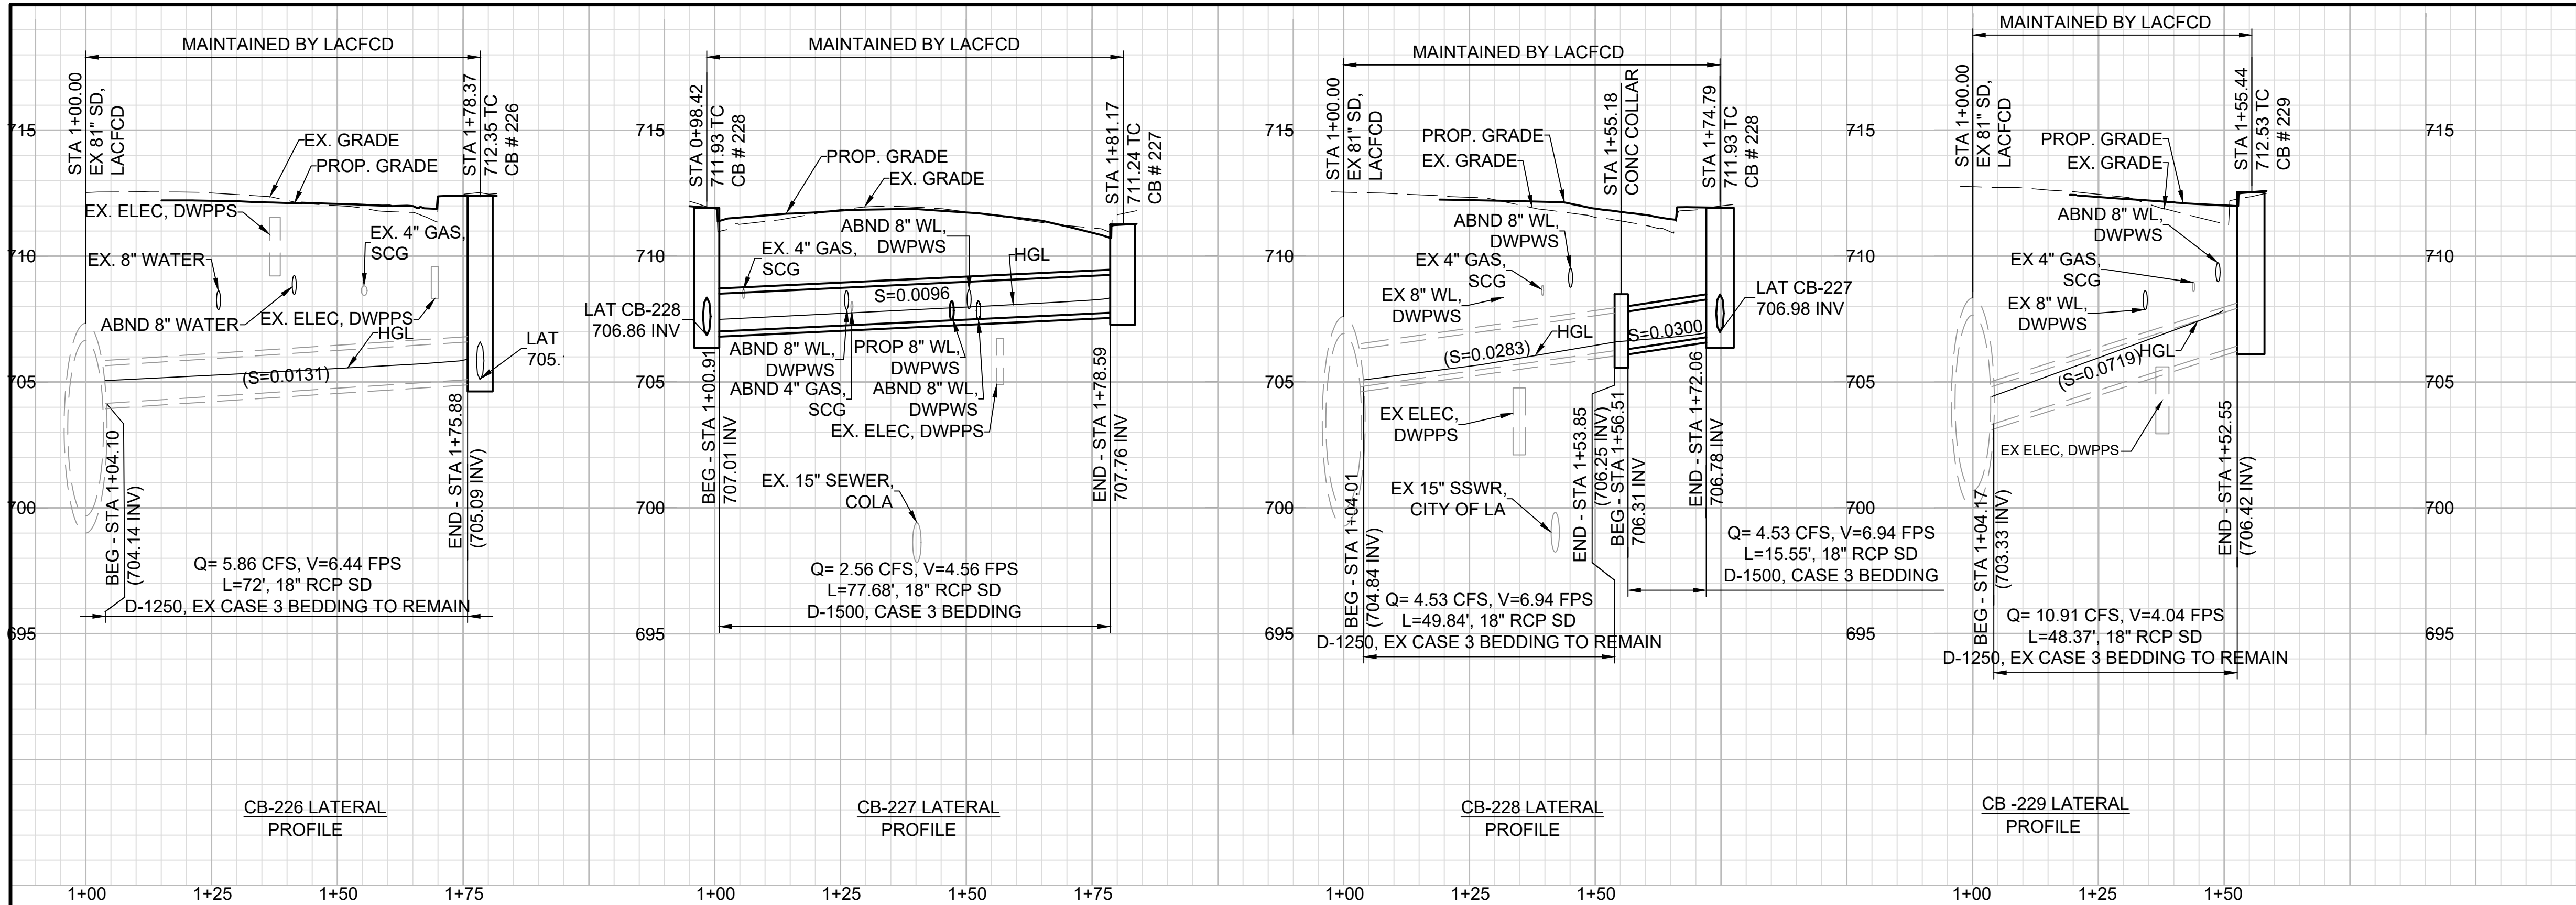

CONSTRUCTION SYMBOLS:

- CONSTRUCT ○◻ REMODEL EXISTING
◻ EXISTING ◻○ REMOVE AND CONSTRUCT
◻ REMOVE ○ WORK BY OTHERS

CONSTRUCTION NOTES:

- 79 REINFORCED CONCRETE PIPE
82 JUNCTION STRUCTURE
85 STORM DRAIN MANHOLE
97 CONCRETE COLLAR
98 MONOLITHIC CATCH BASIN CONNECTION
99 CURB OPENING CATCH BASIN
102 OFFSET MANHOLE "TYPE B"
115 CAP MH



NOTES:

- SEE COMPOSITE UTILITY REARRANGEMENT PLANS (UR) FOR EXISTING UTILITY CONFLICTS AND PROPOSED RELOCATIONS. CONTRACTOR TO DETERMINE UTILITY DEPTHS AND LOCATIONS ON STORM DRAIN PROFILES PRIOR TO CONSTRUCTION.
- SEE TRACKWORK PLANS (T) FOR TRACK DRAIN DETAILS, SWITCH MACHINE DRAIN DETAILS, AND TRACK-RELATED WORK.
- SEE STREET IMPROVEMENT PLANS (CS) FOR ROADWAY-RELATED WORK.
- SEE DU04-SEGMENT B METRO TRACK GUIDEWAY PLANS (D) FOR TRACK GUIDEWAY STORM DRAIN IMPROVEMENTS.
- ALL NEW AND REMOVED/REPLACED CATCH BASINS UNDER THIS PROJECT SHALL INCLUDE CATCH BASIN OPENING SCREENS AND INSERTS. REUSE EXISTING SCREENS WHEN APPLICABLE.
- ALL NEW AND REMOVED/REPLACED CATCH BASINS UNDER THIS PROJECT SHALL BE STENCILED WITH PROHIBITIVE LANGUAGE "NO DUMPING - DRAIN TO OCEAN."
- SEE TRAFFIC AND SIGNAL PLANS FOR SIGNAL RELATED WORK.
- PROTECT IN PLACE ALL EXISTING BEDDING, UNLESS STATED ON PROFILE.

PROFILE SCALE


HORIZ: 1"=20'
VERT: 1"=4'

LINE/CURVE DATA TABLE			
NO.	LENGTH	BEARING/DELTA	RADIUS
L1	75.07	N02° 39' 45.81"E	--
L2	80.75	S72° 10' 06.10"W	--
L3	79.38	S19° 20' 48.08"W	--
L4	16.86	N74° 22' 55.77"W	--

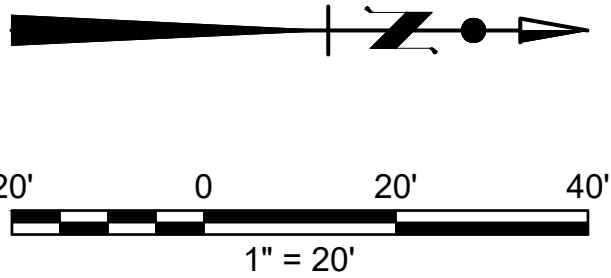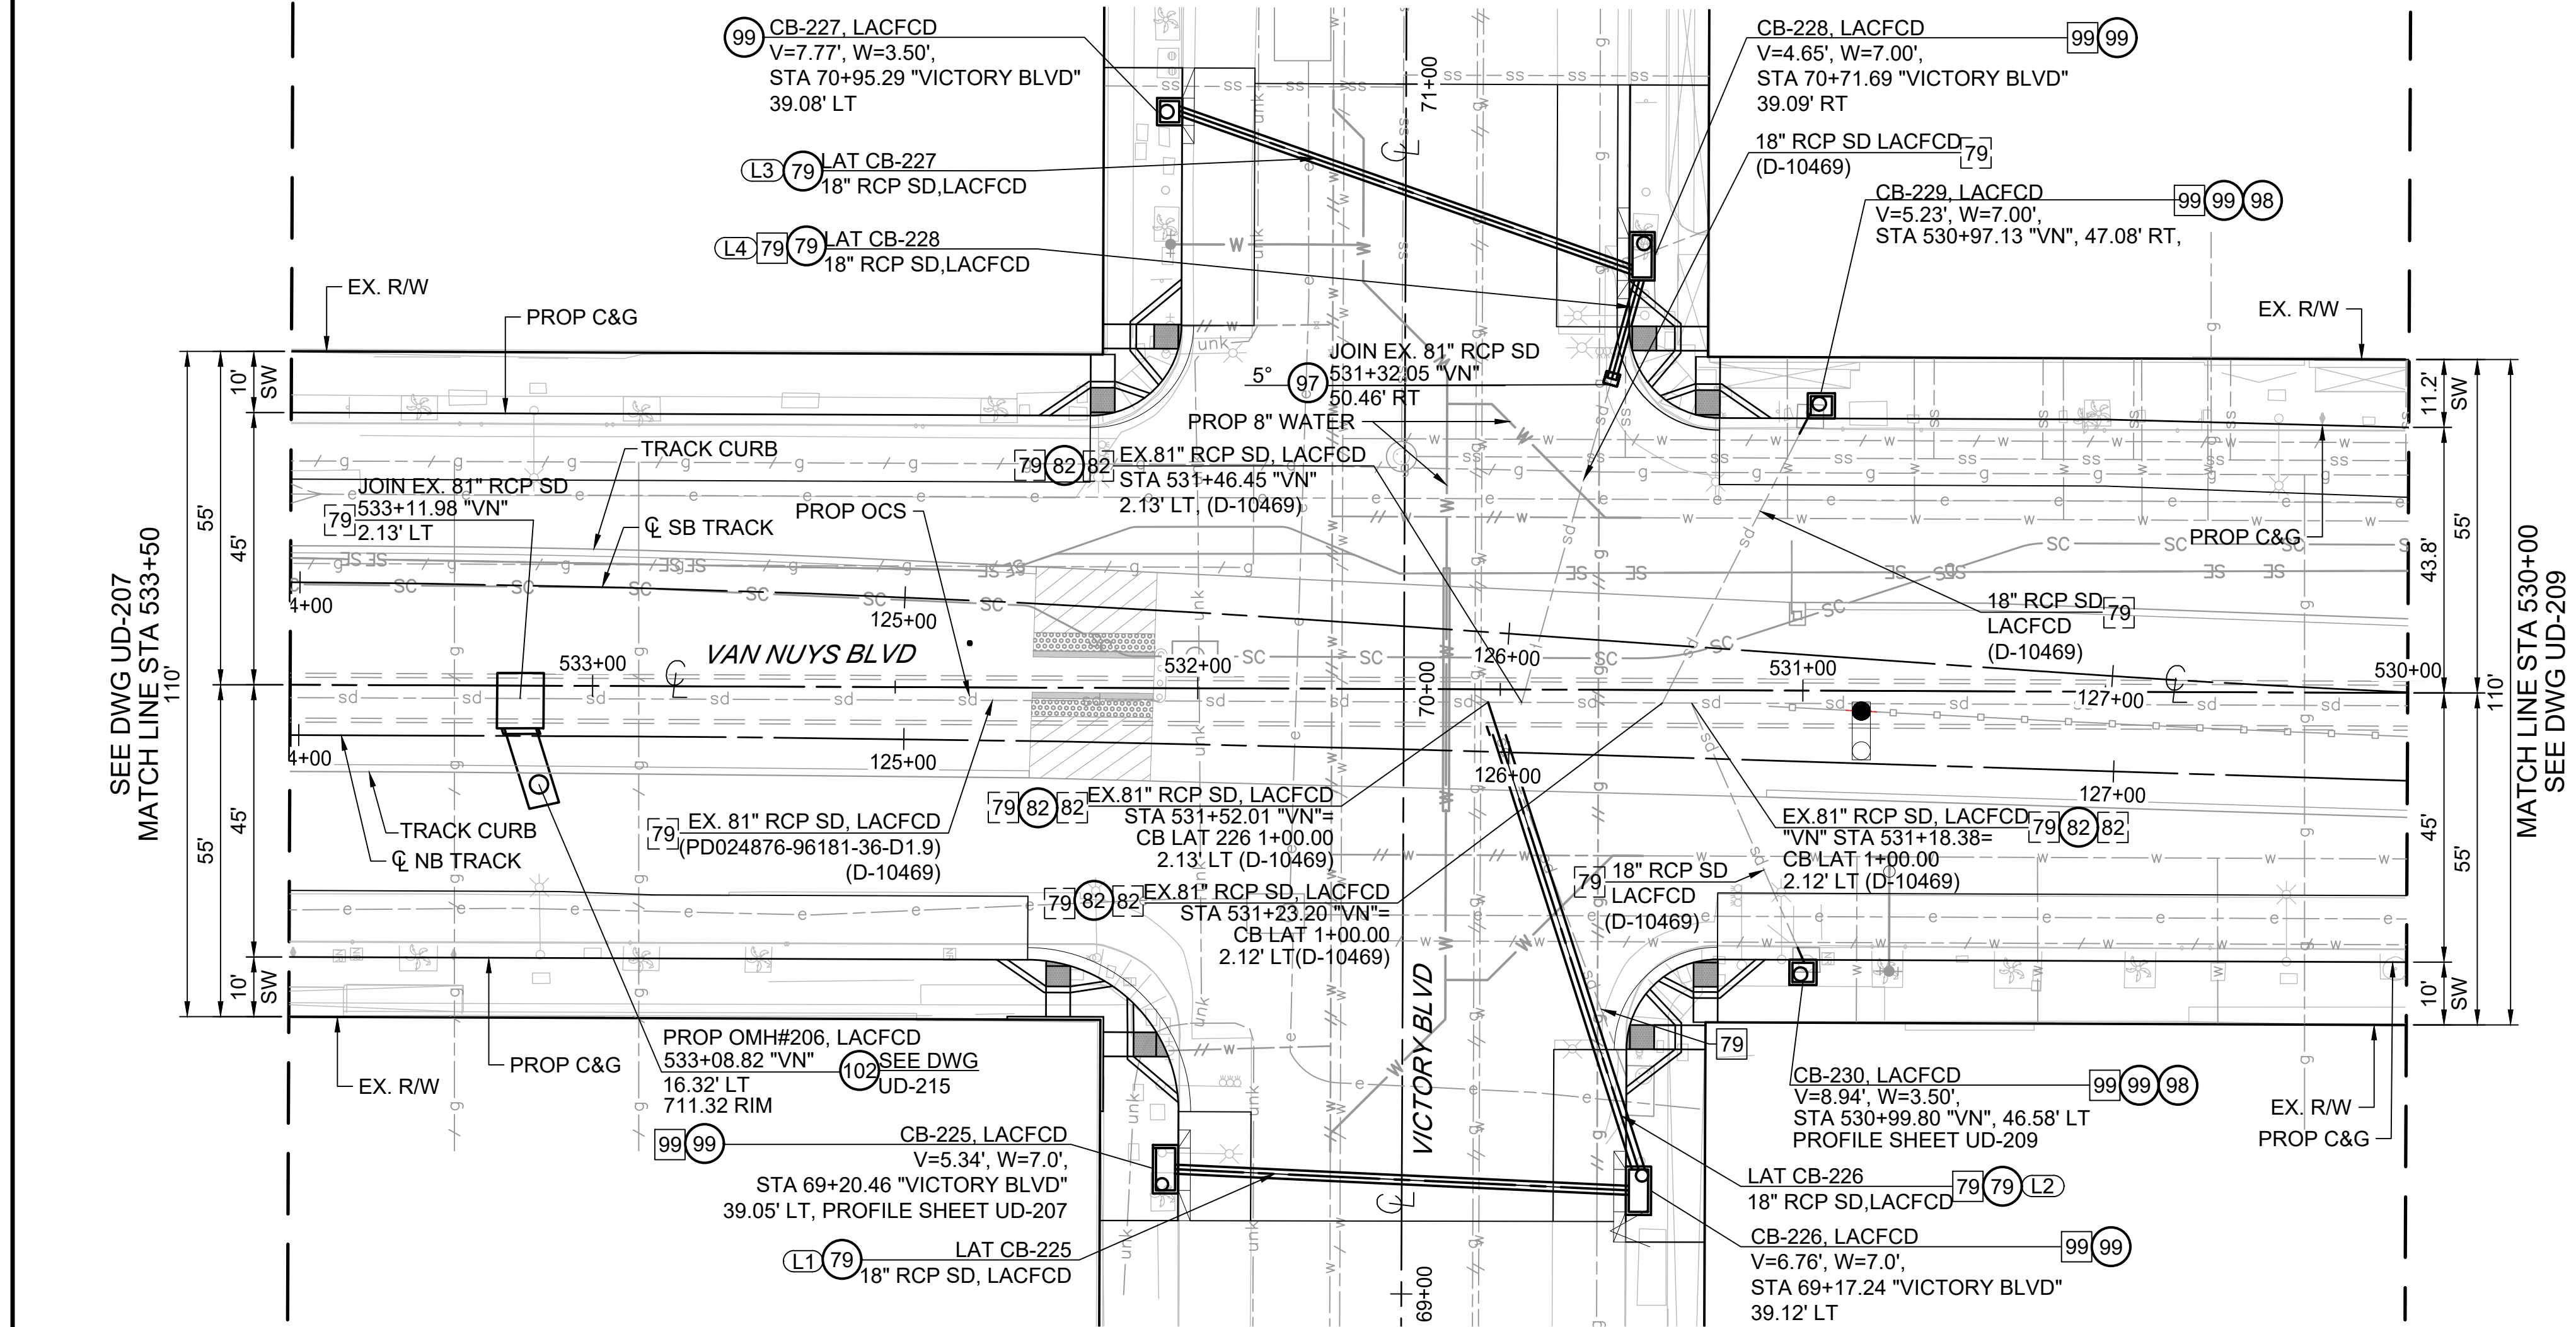

THE PREPARATION OF THIS DRAWING HAS BEEN FINANCED IN PART THROUGH A GRANT FROM THE U.S. DEPARTMENT OF TRANSPORTATION, FEDERAL TRANSIT ADMINISTRATION (FTA), UNDER THE FEDERAL TRANSIT ACT OF 1964, AS AMENDED, AND IN PART BY THE TAXES OF THE CITIZENS OF LOS ANGELES COUNTY AND OF THE STATE OF CALIFORNIA.										DESIGNED BY N.SOTO DRAWN BY R.VENEGAS CHECKED BY N.BUSCH IN CHARGE N.BUSCH DATE 12/11/2025										LOS ANGELES COUNTY METROPOLITAN TRANSPORTATION AUTHORITY San Fernando Transit Constructors 14300 ARMINA ST. LOS ANGELES, CA 91402 TEL: 951.684.5360										AECOM 100% SUBMITTAL - NOT FOR CONSTRUCTION										EAST SAN FERNANDO VALLEY LRT DU06 - DRAINAGE SEGMENT A1 STORM DRAIN PLAN AND PROFILE VAN BUYS BLVD STA 530+00 TO 533+50										CONTRACT NO PS89616000 DRAWING NO UD-208 SCALE 1" = 20' SHEET NO									
REV	DATE	BY	APP	REG NO	EXPIRES	SEAL HOLDER	DESCRIPTION	C	12/15/25	NS	JR	C78082	09/30/27	J. RIMORIN	100% SUBMITTAL	B	08/18/25	AR	NB	C65608	09/30/27	N. BUSCH	85% SUBMITTAL	A	03/07/25	KM	JR	C78082	09/30/27	J. RIMORIN	60% SUBMITTAL																												

FILE PATH: \\80724657-ESFV-PH2\PROJECT FILES\900_CAD\20_SHEETS\DU06\9_UD_DRAINAGE\PS89616000-DU06-UD-208.DWG
PLOT DATE: 12/16/2025 - 2:18 PM USER: ADRIANROBLES

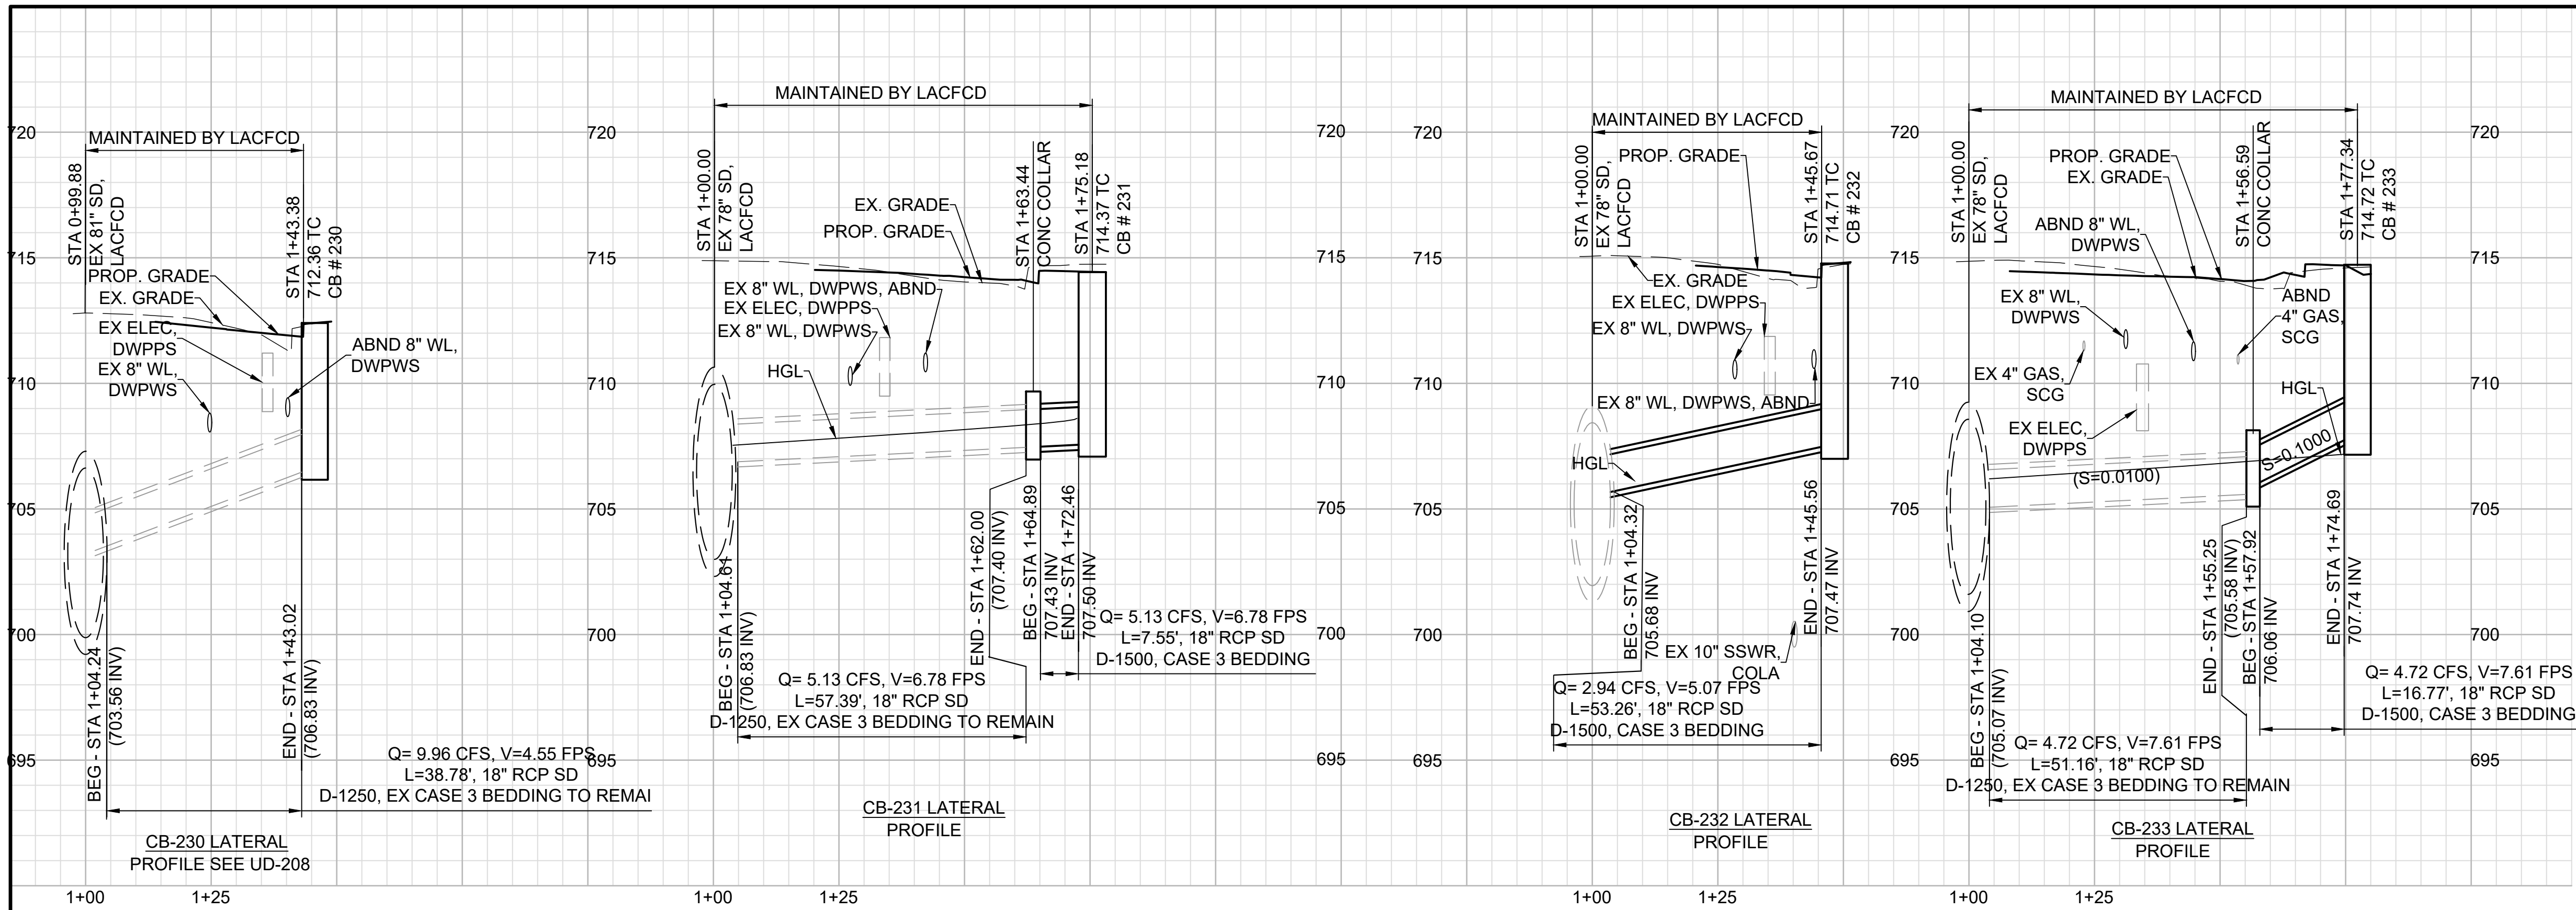

PROFILE SCALE
HORIZ: 1"=20'
VERT: 1"=4'

CONSTRUCTION SYMBOLS:

- CONSTRUCT ○◻ REMODEL EXISTING
◻ EXISTING ◻○ REMOVE AND CONSTRUCT
◻ REMOVE ○ WORK BY OTHERS



CONSTRUCTION NOTES:

- 79 REINFORCED CONCRETE PIPE
82 JUNCTION STRUCTURE
85 STORM DRAIN MANHOLE
97 CONCRETE COLLAR
98 MONOLITHIC CATCH BASIN CONNECTION
99 CURB OPENING CATCH BASIN
102 OFFSET MANHOLE "TYPE B"
115 CAP MH

NOTES:

- SEE COMPOSITE UTILITY REARRANGEMENT PLANS (UR) FOR EXISTING UTILITY CONFLICTS AND PROPOSED RELOCATIONS. CONTRACTOR TO DETERMINE UTILITY DEPTHS AND LOCATIONS ON STORM DRAIN PROFILES PRIOR TO CONSTRUCTION.
- SEE TRACKWORK PLANS (T) FOR TRACK DRAIN DETAILS, SWITCH MACHINE DRAIN DETAILS, AND TRACK-RELATED WORK.
- SEE STREET IMPROVEMENT PLANS (CS) FOR ROADWAY-RELATED WORK.
- SEE DU04-SEGMENT B METRO TRACK GUIDEWAY PLANS (D) FOR TRACK GUIDEWAY STORM DRAIN IMPROVEMENTS.
- ALL NEW AND REMOVED/REPLACED CATCH BASINS UNDER THIS PROJECT SHALL INCLUDE CATCH BASIN OPENING SCREENS AND INSERTS. REUSE EXISTING SCREENS WHEN APPLICABLE.
- ALL NEW AND REMOVED/REPLACED CATCH BASINS UNDER THIS PROJECT SHALL BE STENCILED WITH PROHIBITIVE LANGUAGE "NO DUMPING - DRAIN TO OCEAN."
- SEE TRAFFIC AND SIGNAL PLANS FOR SIGNAL RELATED WORK.
- PROTECT IN PLACE ALL EXISTING BEDDING, UNLESS STATED ON PROFILE.

LINE/CURVE DATA TABLE			
NO.	LENGTH	BEARING/DELTA	RADIUS
L1	9.09	S78° 03' 24.69"W	--
L2	42.60	N63° 52' 45.17"E	--
L3	17.99	N78° 07' 02.99"W	--
L4	49.77	N58° 01' 54.70"W	--

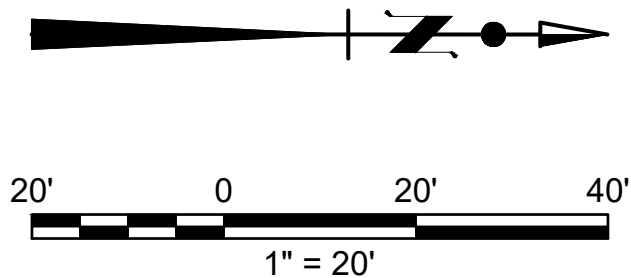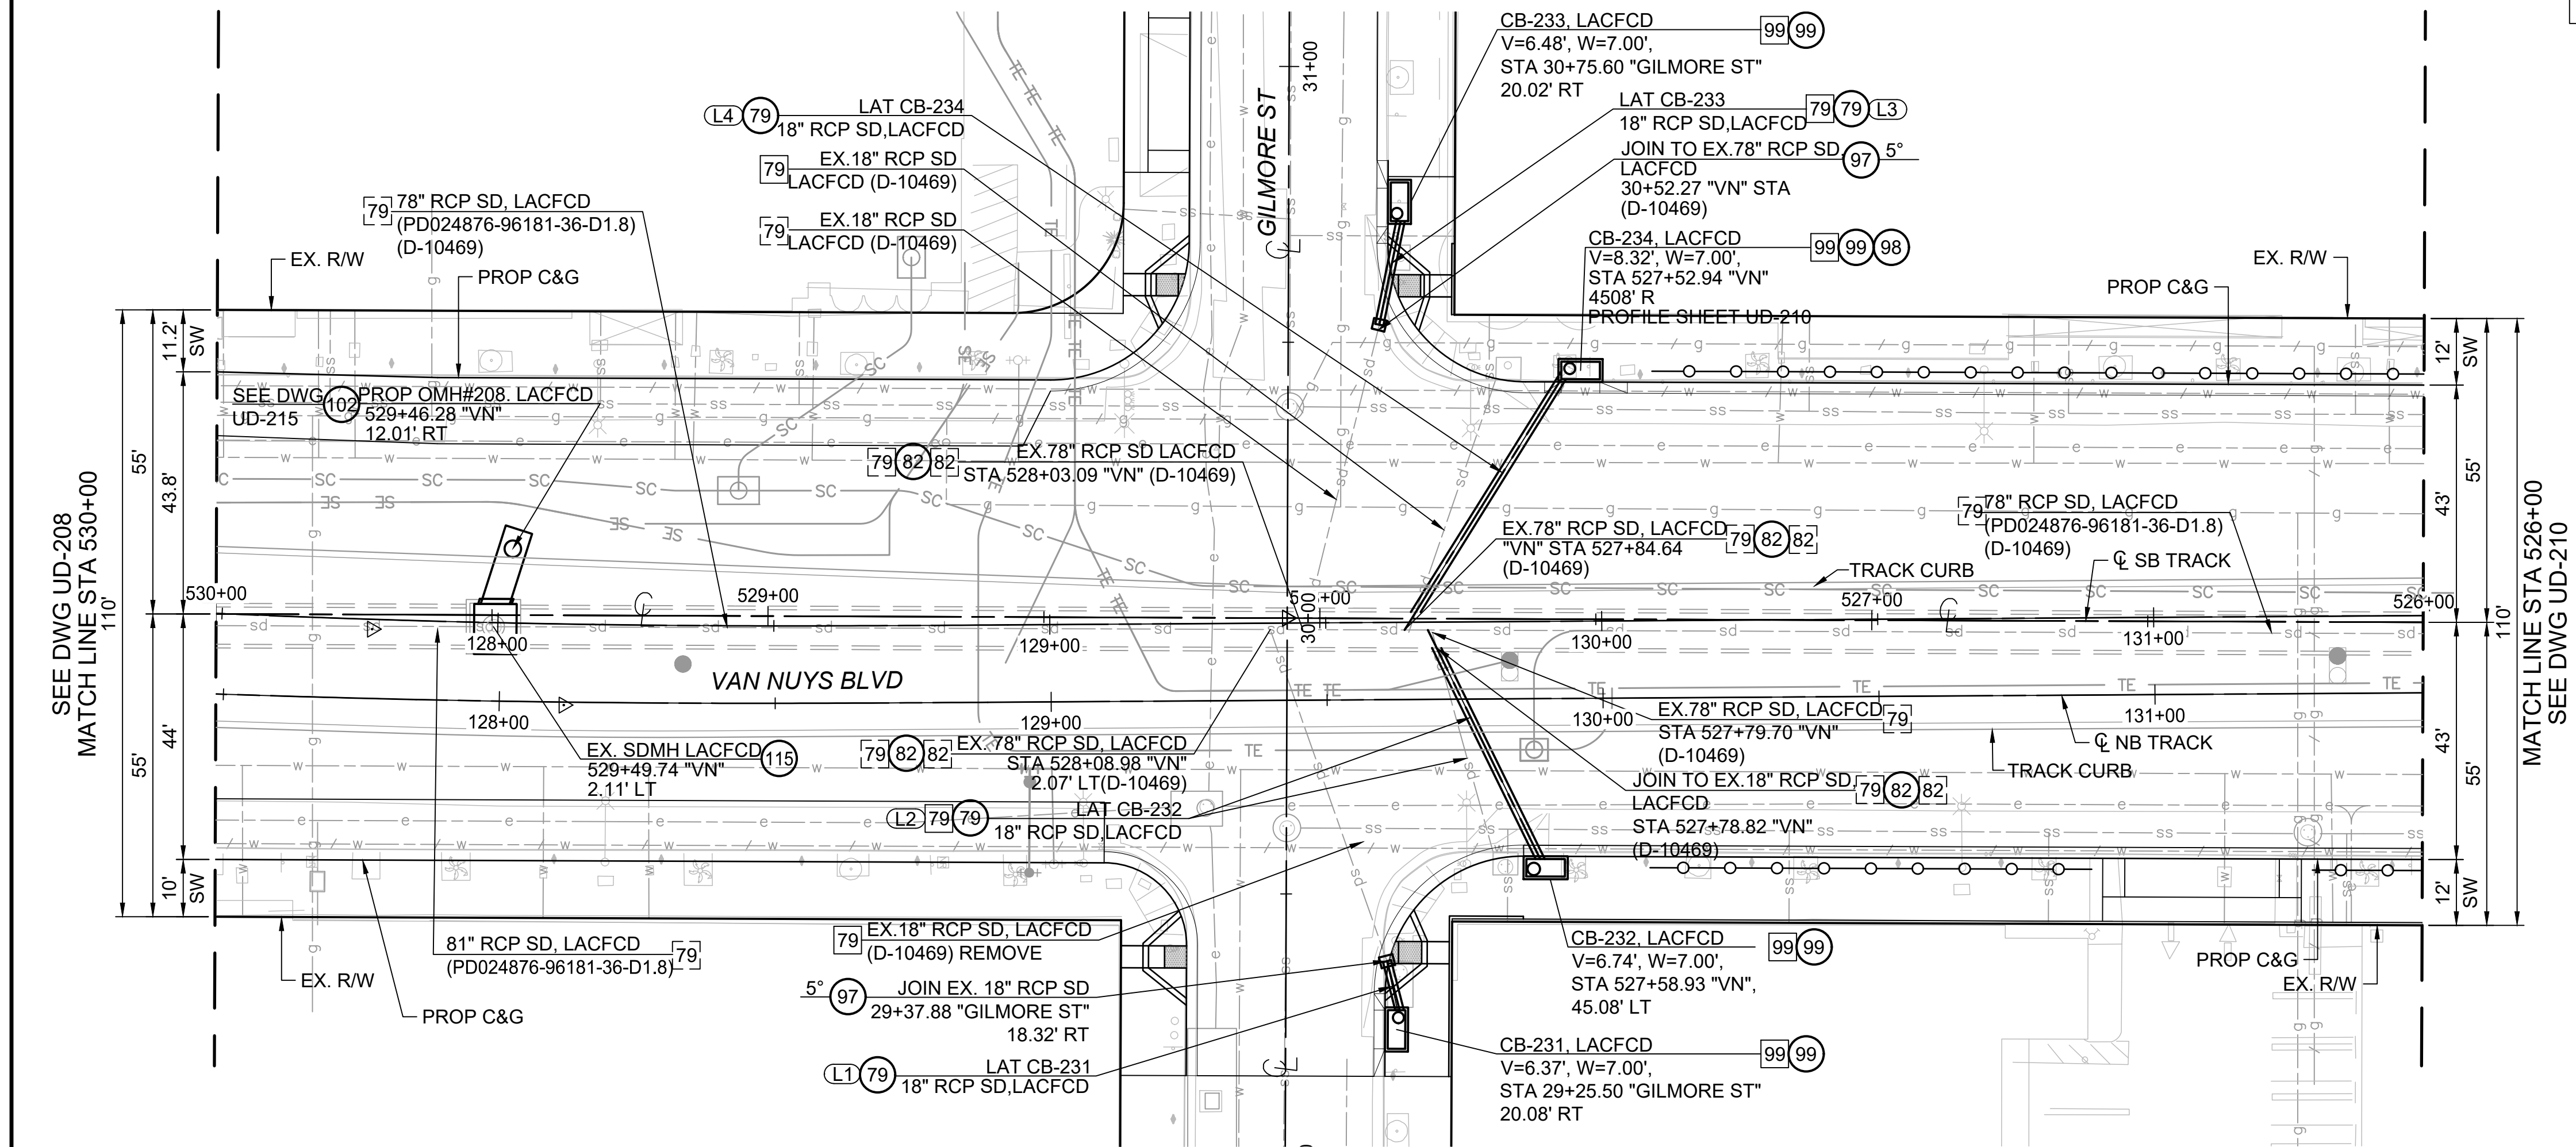

THE PREPARATION OF THIS DRAWING HAS BEEN FINANCED IN PART THROUGH A GRANT FROM THE U.S. DEPARTMENT OF TRANSPORTATION, FEDERAL TRANSIT ADMINISTRATION (FTA), UNDER THE FEDERAL TRANSIT ACT OF 1964, AS AMENDED, AND IN PART BY THE TAXES OF THE CITIZENS OF LOS ANGELES COUNTY AND OF THE STATE OF CALIFORNIA.									
REV	DATE	BY	APP	REG NO	EXPIRES	SEAL HOLDER	DESCRIPTION		
C	12/15/25	NS	JR	C78082	09/30/27	J. RIMORIN	100% SUBMITTAL		
B	08/18/25	AR	NB	C65608	09/30/27	N. BUSCH	85% SUBMITTAL		
A	03/07/25	KM	JR	C78082	09/30/27	J. RIMORIN	60% SUBMITTAL		

DESIGNED BY
N. SOTO
DRAWN BY
R. VENEGAS
CHECKED BY
N. BUSCH
IN CHARGE
N. BUSCH
DATE
12/11/2025

LOS ANGELES COUNTY METROPOLITAN TRANSPORTATION AUTHORITY

San Fernando Transit Constructors

AECOM

V&A INC

14300 ARMINA ST.
LOS ANGELES, CA 91402
TEL: 951.684.5360

1111 S. GARDEN AVE. SUITE 103
LOS ANGELES, CA 90015
213.922.0000

100% SUBMITTAL - NOT FOR CONSTRUCTION

EAST SAN FERNANDO VALLEY LRT
DU06 - DRAINAGE SEGMENT A1
STORM DRAIN PLAN AND PROFILE
VAN NUYS BLVD STA 526+00 TO 530+00


CONTRACT NO
PS89616000

DRAWING NO
UD-209

SCALE
1" = 20'

SHEET NO

FILE PATH: \\S072457-ESFV-PH2\PROJECT FILES\900_CAD\20_SHEETS\DU06\09_UD_DRAINAGE\PS89616000-DU06-UD-209.DWG
PLOT DATE: 12/16/2025 - 2:07 PM USER: ADRIANROBLES

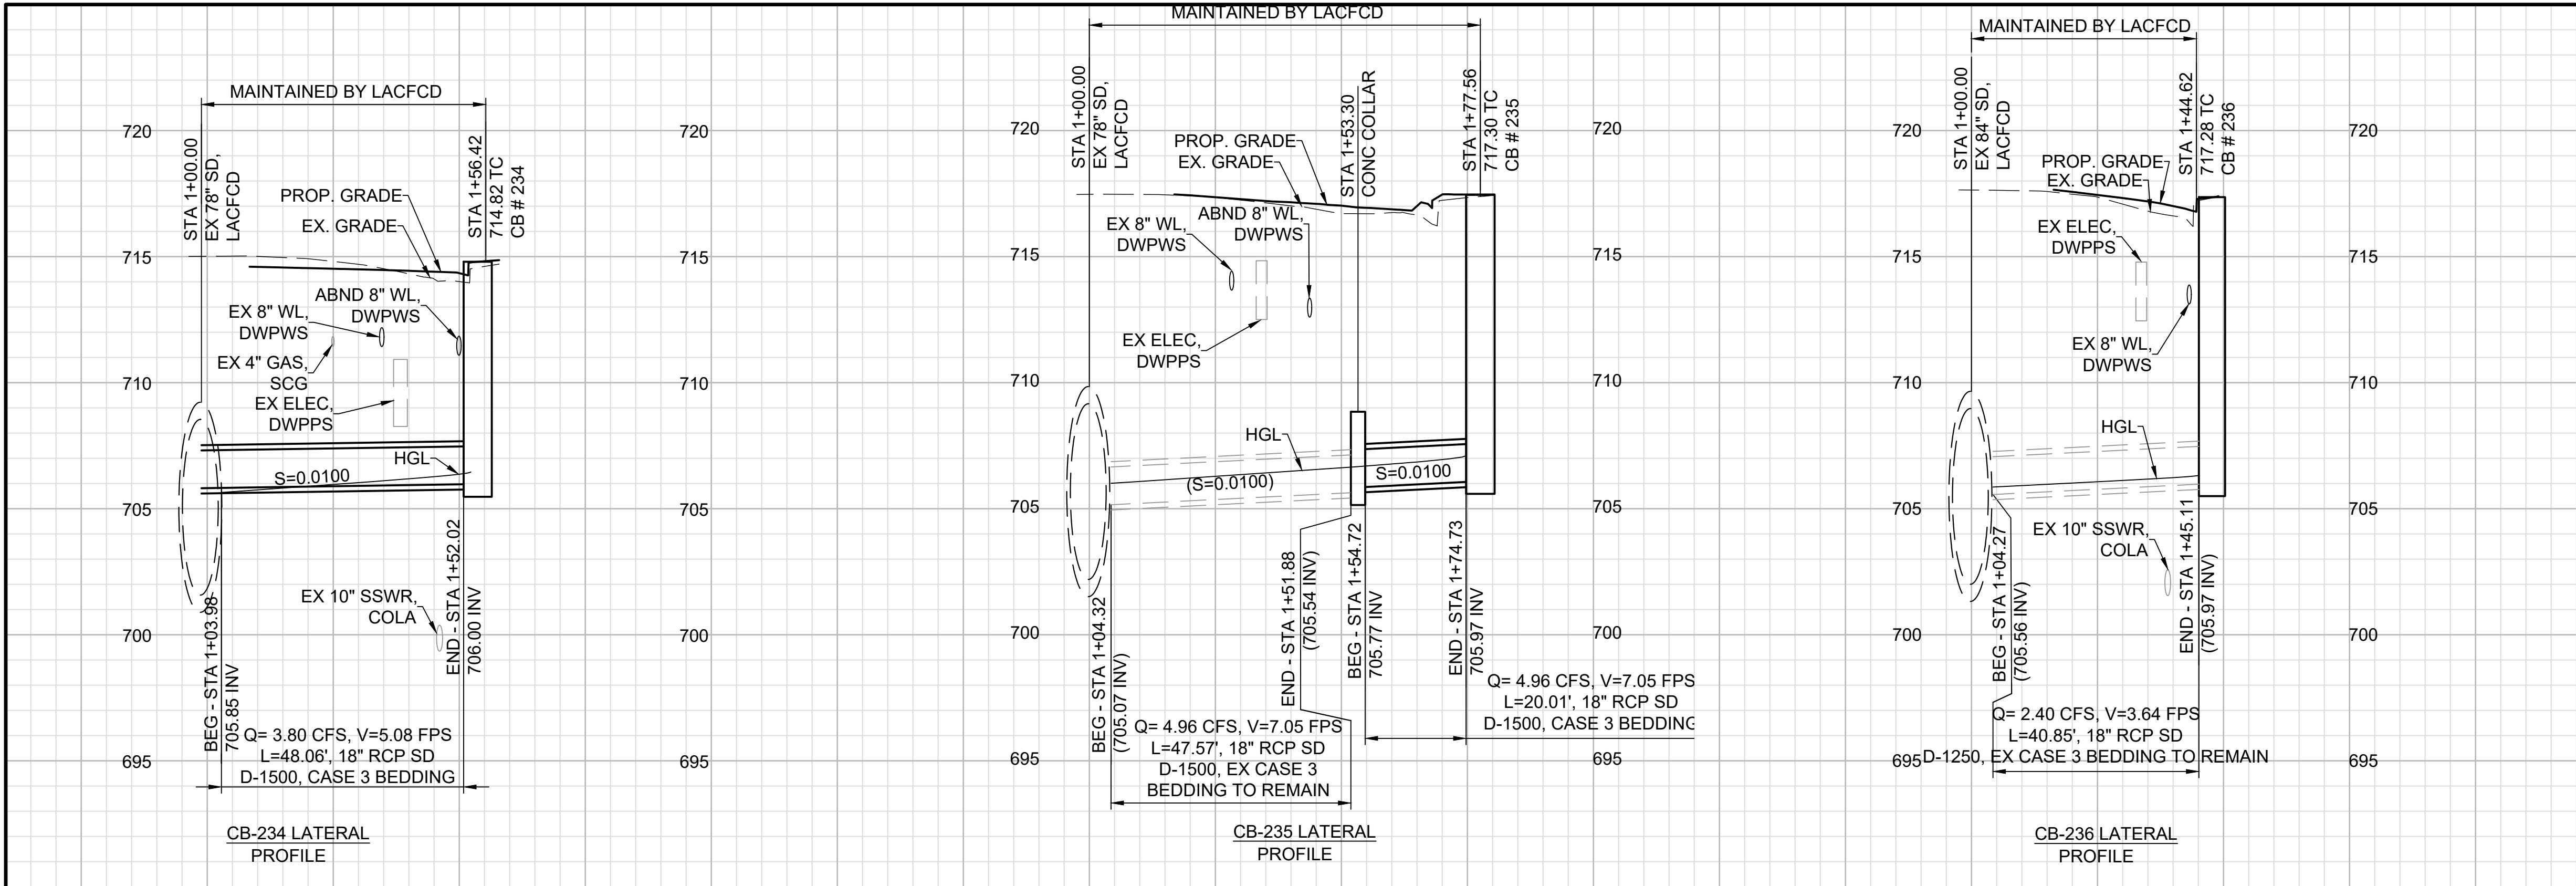

CONSTRUCTION SYMBOLS:

- CONSTRUCT
- ◻ REMODEL EXISTING
- ◻ EXISTING
- ◻○ REMOVE AND CONSTRUCT
- ◻ REMOVE
- WORK BY OTHERS

CONSTRUCTION NOTES:

- 79 REINFORCED CONCRETE PIPE
- 82 JUNCTION STRUCTURE
- 85 STORM DRAIN MANHOLE
- 97 CONCRETE COLLAR
- 98 MONOLITHIC CATCH BASIN CONNECTION
- 99 CURB OPENING CATCH BASIN
- 102 OFFSET MANHOLE "TYPE B"
- 115 CAP MH



NOTES:

- SEE COMPOSITE UTILITY REARRANGEMENT PLANS (UR) FOR EXISTING UTILITY CONFLICTS AND PROPOSED RELOCATIONS. CONTRACTOR TO DETERMINE UTILITY DEPTHS AND LOCATIONS ON STORM DRAIN PROFILES PRIOR TO CONSTRUCTION.
- SEE TRACKWORK PLANS (T) FOR TRACK DRAIN DETAILS, SWITCH MACHINE DRAIN DETAILS, AND TRACK-RELATED WORK.
- SEE STREET IMPROVEMENT PLANS (CS) FOR ROADWAY-RELATED WORK.
- SEE DU04-SEGMENT B METRO TRACK GUIDEWAY PLANS (D) FOR TRACK GUIDEWAY STORM DRAIN IMPROVEMENTS.
- ALL NEW AND REMOVED/REPLACED CATCH BASINS UNDER THIS PROJECT SHALL INCLUDE CATCH BASIN OPENING SCREENS AND INSERTS. REUSE EXISTING SCREENS WHEN APPLICABLE.
- ALL NEW AND REMOVED/REPLACED CATCH BASINS UNDER THIS PROJECT SHALL BE STENCILED WITH PROHIBITIVE LANGUAGE "NO DUMPING - DRAIN TO OCEAN."
- SEE TRAFFIC AND SIGNAL PLANS FOR SIGNAL RELATED WORK.
- PROTECT IN PLACE ALL EXISTING BEDDING, UNLESS STATED ON PROFILE.

PROFILE SCALE

HORIZ: 1"=20'
VERT: 1"=4'

LINE/CURVE DATA TABLE			
NO.	LENGTH	BEARING/DELTA	RADIUS
L1	22.09	N69° 11' 12.10"E	--

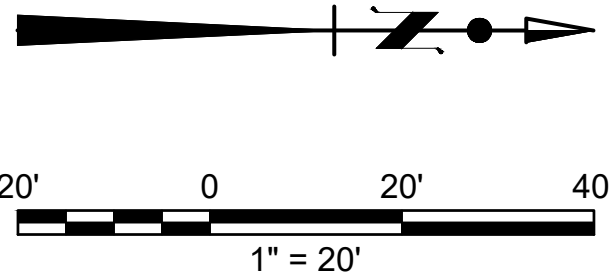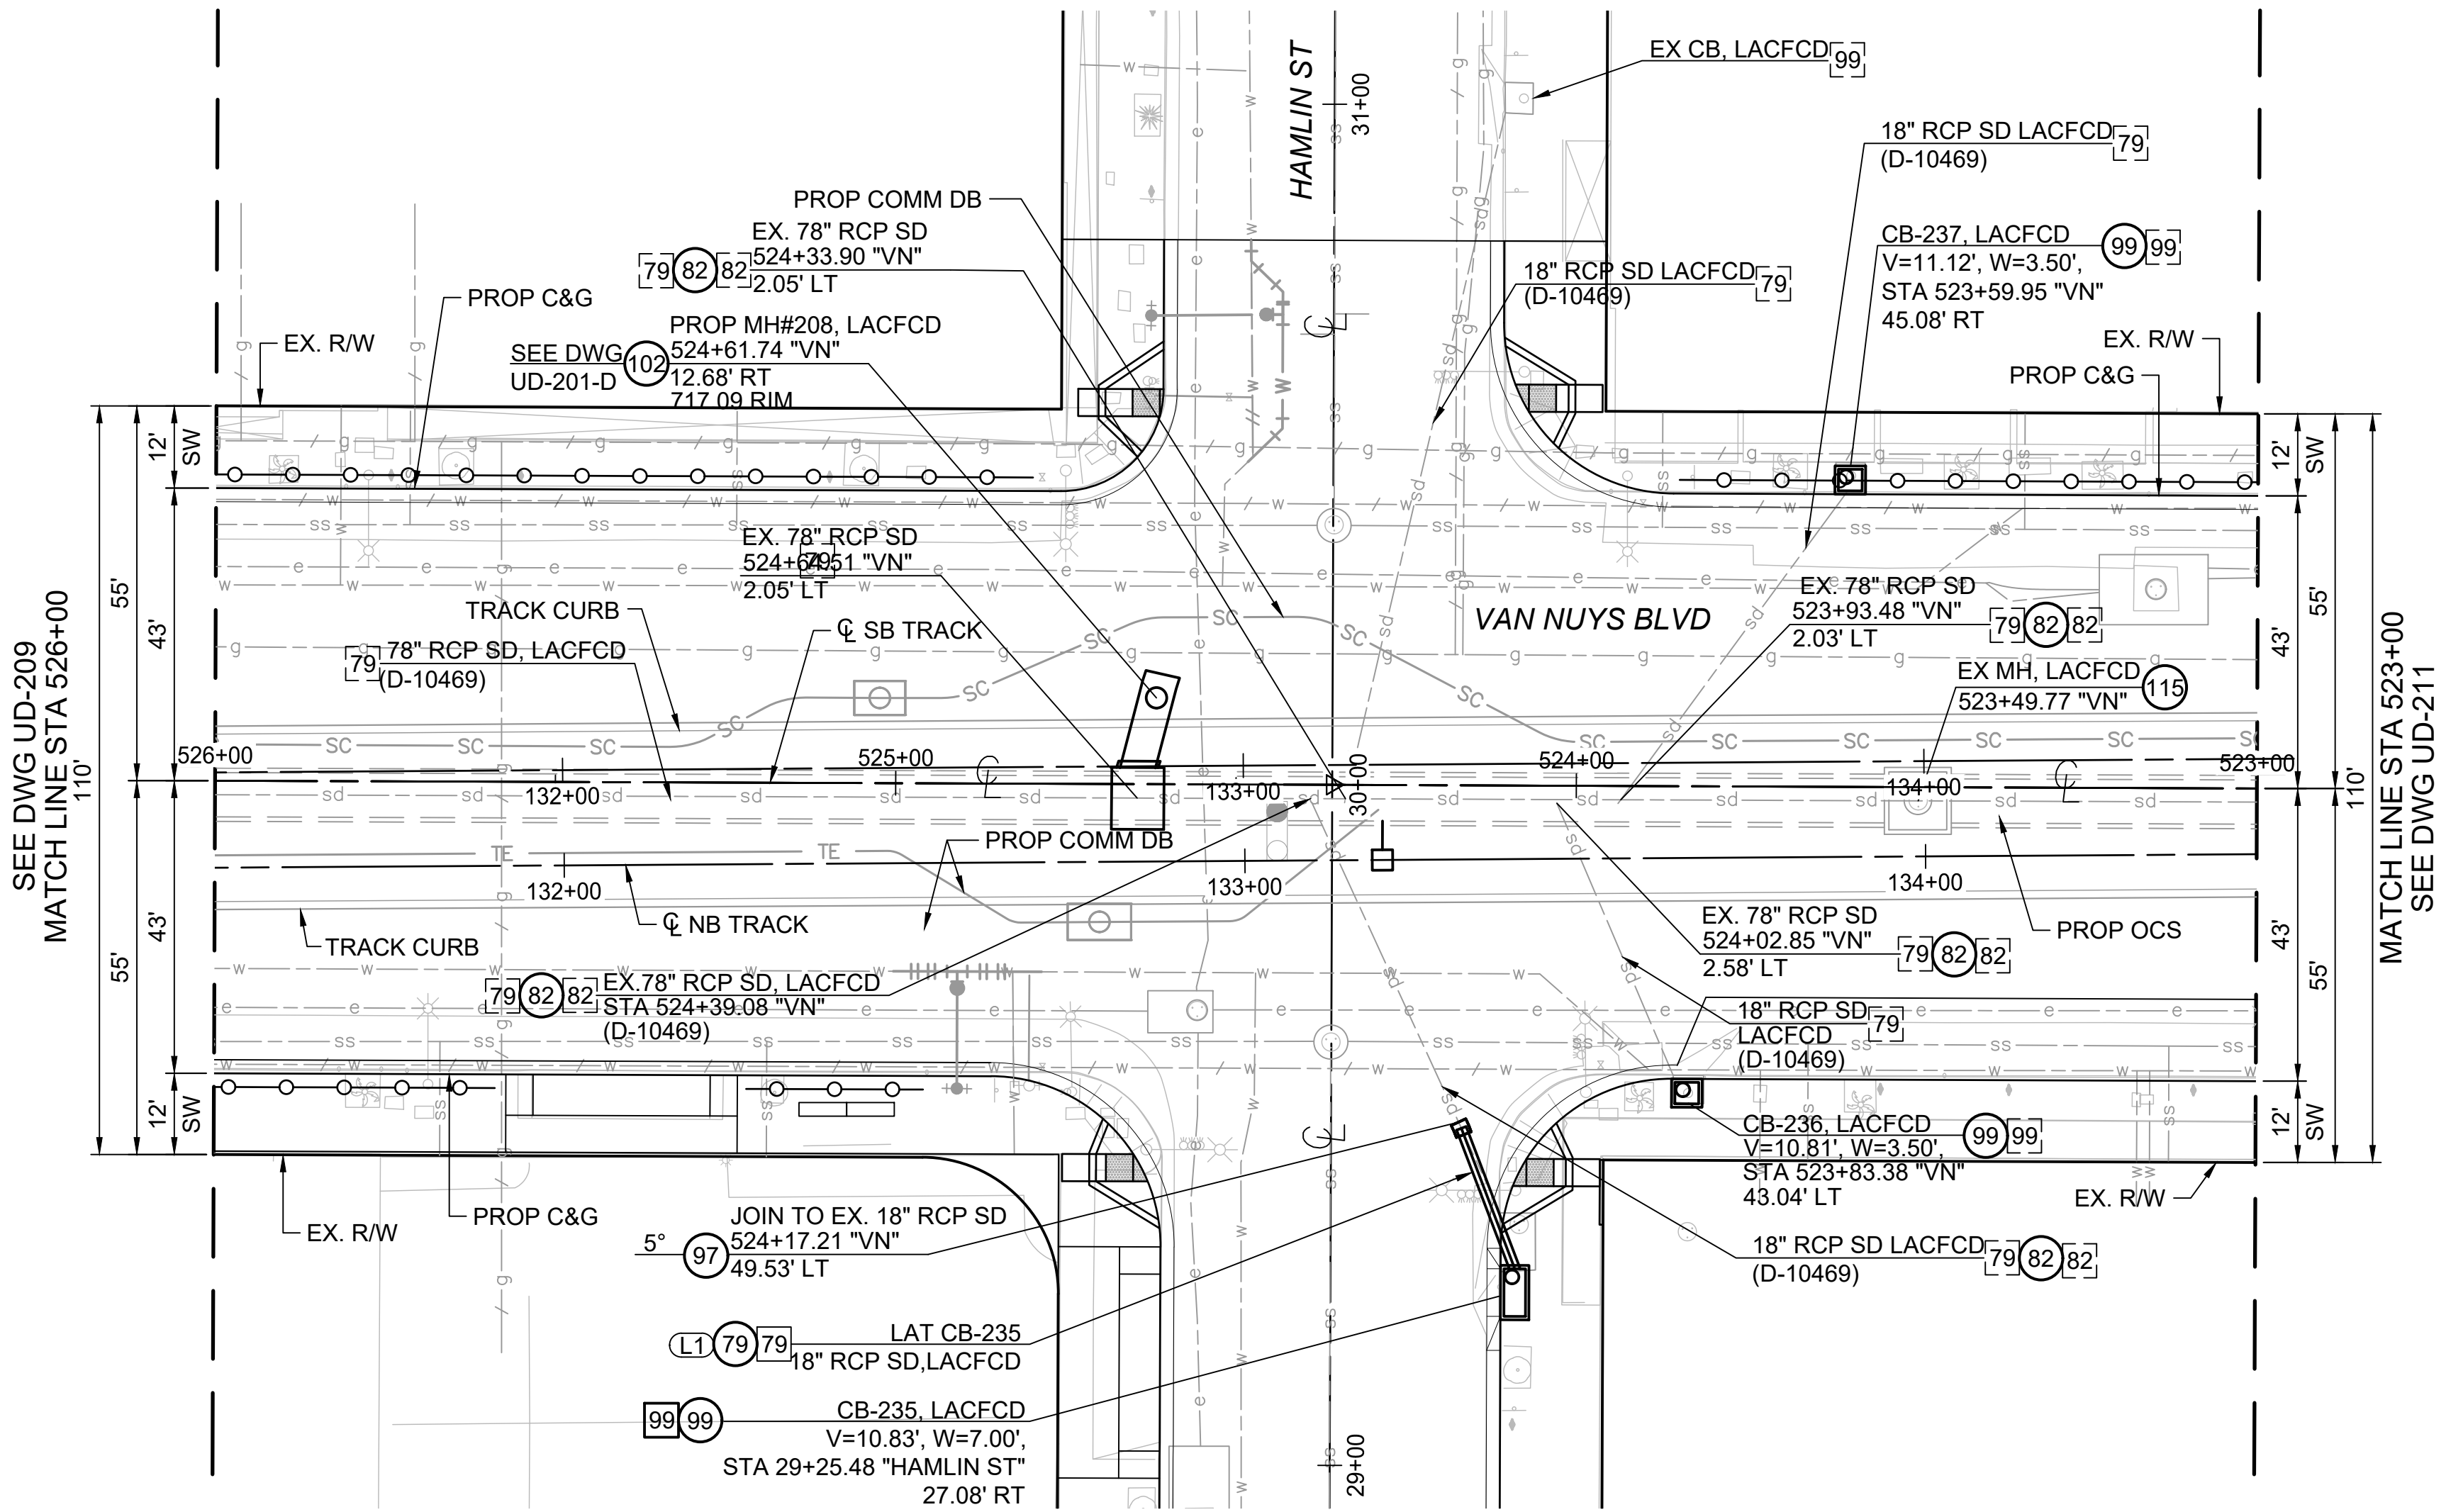

THE PREPARATION OF THIS DRAWING HAS BEEN FINANCED IN PART THROUGH A GRANT FROM THE U.S. DEPARTMENT OF TRANSPORTATION, FEDERAL TRANSIT ADMINISTRATION (FTA), UNDER THE FEDERAL TRANSIT ACT OF 1964, AS AMENDED, AND IN PART BY THE TAXES OF THE CITIZENS OF LOS ANGELES COUNTY AND OF THE STATE OF CALIFORNIA.									
REV	DATE	BY	APP	REG NO	EXPIRES	SEAL HOLDER	DESCRIPTION	DESIGNED BY N. SOTO	
C	12/15/25	NS	JR	C78082	09/30/27	J. RIMORIN	100% SUBMITTAL	DRAWN BY R. VENEGAS	
B	08/18/25	AR	NB	C65608	09/30/27	N. BUSCH	85% SUBMITTAL	CHECKED BY N. BUSCH	
A	03/07/25	KM	JR	C78082	09/30/27	J. RIMORIN	60% SUBMITTAL	IN CHARGE N. BUSCH	
								DATE 12/11/2025	

**LOS ANGELES COUNTY**
METROPOLITAN TRANSPORTATION AUTHORITY

**San Fernando Transit Constructors**

**AECOM**


14300 ARMINA ST.
LOS ANGELES, CA 91402
TEL: 951.684.5360

100% SUBMITTAL - NOT FOR CONSTRUCTION

EAST SAN FERNANDO VALLEY LRT
DU06 - DRAINAGE SEGMENT A1
STORM DRAIN PLAN AND PROFILE
VAN NUYS BLVD STA 523+00 TO 526+00

CONTRACT NO PS89616000	REV
DRAWING NO UD-210	
SCALE 1" = 20'	
SHEET NO	

FILE PATH: \\S072457-ESFV-PH2\PROJECT FILES\900_CAD\20_SHEETS\DU06\09_UD_DRAINAGE\PS89616000-DU06-UD-210.DWG
PLOT DATE: 12/16/2025 - 1:38 PM USER: NEREDASOTO

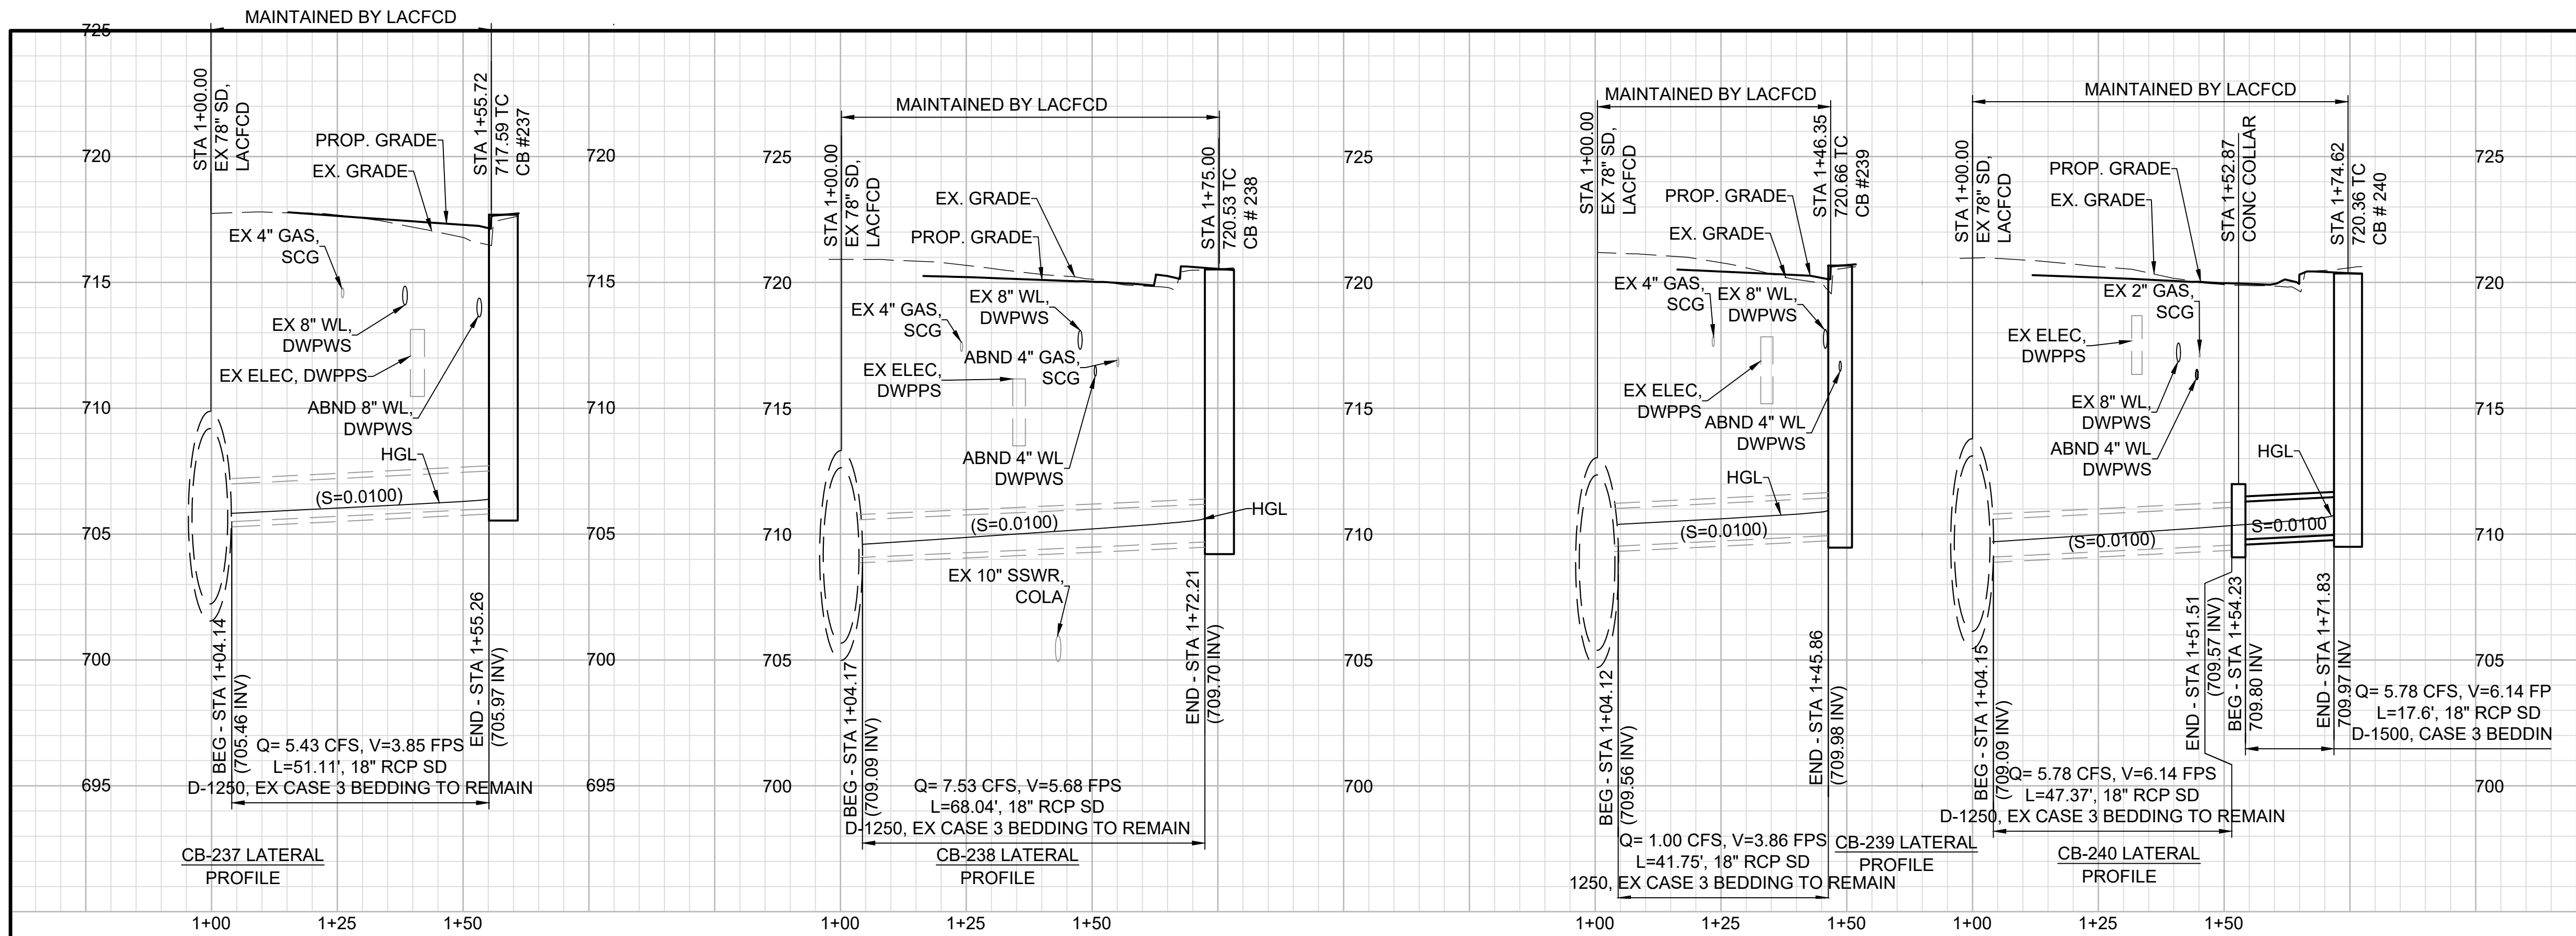

CONSTRUCTION SYMBOLS:

- CONSTRUCT ○◻ REMODEL EXISTING
◻ EXISTING ◻○ REMOVE AND CONSTRUCT
◻ REMOVE ○ WORK BY OTHERS

CONSTRUCTION NOTES:

- 79 REINFORCED CONCRETE PIPE
82 JUNCTION STRUCTURE
85 STORM DRAIN MANHOLE
97 CONCRETE COLLAR
98 MONOLITHIC CATCH BASIN CONNECTION
99 CURB OPENING CATCH BASIN
102 OFFSET MANHOLE "TYPE B"
115 CAP MH



NOTES:

- SEE COMPOSITE UTILITY REARRANGEMENT PLANS (UR) FOR EXISTING UTILITY CONFLICTS AND PROPOSED RELOCATIONS. CONTRACTOR TO DETERMINE UTILITY DEPTHS AND LOCATIONS ON STORM DRAIN PROFILES PRIOR TO CONSTRUCTION.
- SEE TRACKWORK PLANS (T) FOR TRACK DRAIN DETAILS, SWITCH MACHINE DRAIN DETAILS, AND TRACK-RELATED WORK.
- SEE STREET IMPROVEMENT PLANS (CS) FOR ROADWAY-RELATED WORK.
- SEE DU04-SEGMENT B METRO TRACK GUIDEWAY PLANS (D) FOR TRACK GUIDEWAY STORM DRAIN IMPROVEMENTS.
- ALL NEW AND REMOVED/REPLACED CATCH BASINS UNDER THIS PROJECT SHALL INCLUDE CATCH BASIN OPENING SCREENS AND INSERTS. REUSE EXISTING SCREENS WHEN APPLICABLE.
- ALL NEW AND REMOVED/REPLACED CATCH BASINS UNDER THIS PROJECT SHALL BE STENCILED WITH PROHIBITIVE LANGUAGE "NO DUMPING - DRAIN TO OCEAN."
- SEE TRAFFIC AND SIGNAL PLANS FOR SIGNAL RELATED WORK.
- PROTECT IN PLACE ALL EXISTING BEDDING, UNLESS STATED ON PROFILE.

PROFILE SCALE

HORIZ: 1"=20'
VERT: 1"=4'

LINE/CURVE DATA TABLE			
NO.	LENGTH	BEARING/DELTA	RADIUS
L1	19.29	S72° 12' 28.94"W	--

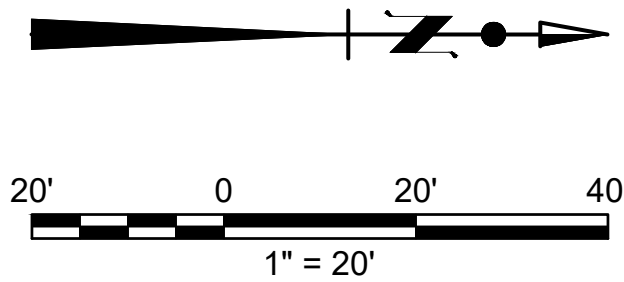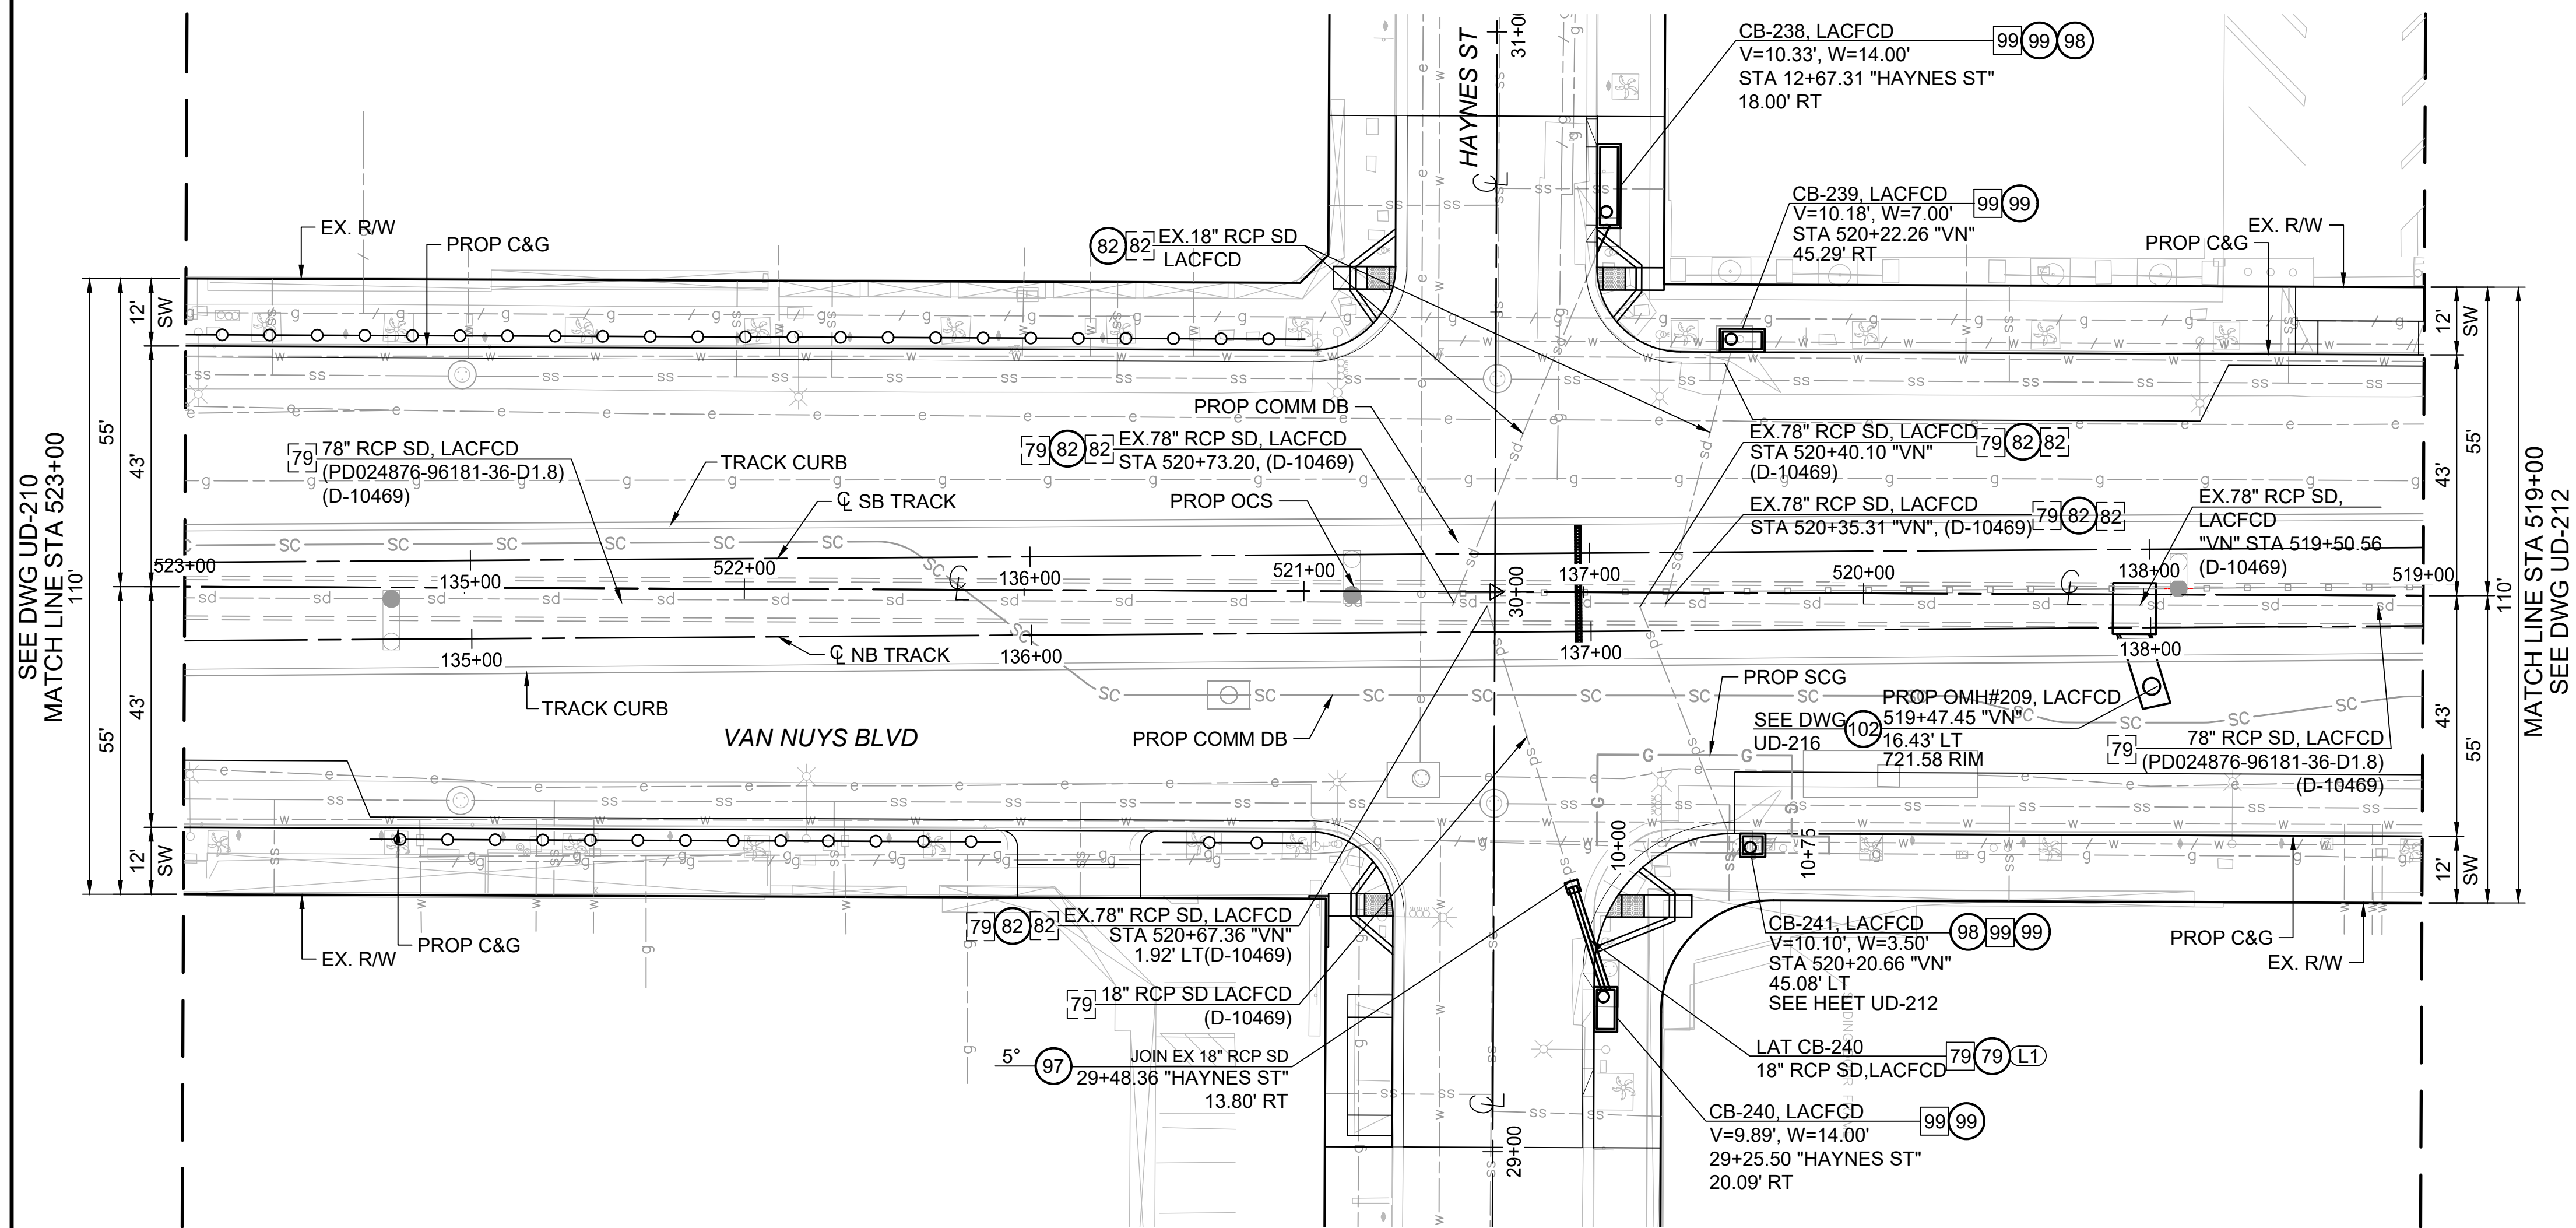

THE PREPARATION OF THIS DRAWING HAS BEEN FINANCED IN PART THROUGH A GRANT FROM THE U.S. DEPARTMENT OF TRANSPORTATION, FEDERAL TRANSIT ADMINISTRATION (FTA), UNDER THE FEDERAL TRANSIT ACT OF 1964, AS AMENDED, AND IN PART BY THE TAXES OF THE CITIZENS OF LOS ANGELES COUNTY AND OF THE STATE OF CALIFORNIA.							DESIGNED BY N. SOTO
							DRAWN BY R. VENEGAS
							CHECKED BY N. BUSCH
							IN CHARGE N. BUSCH
							DATE 12/11/2025
C	12/15/25	NS	JR	C78082	09/30/27	J. RIMORIN	100% SUBMITTAL
B	08/18/25	AR	NB	C65608	09/30/27	N. BUSCH	85% SUBMITTAL
A	03/07/25	KM	JR	C78082	09/30/27	J. RIMORIN	60% SUBMITTAL
REV	DATE	BY	APP	REG NO	EXPIRES	SEAL HOLDER	DESCRIPTION




LOS ANGELES COUNTY
METROPOLITAN TRANSPORTATION AUTHORITY

AECOM

100% SUBMITTAL - NOT FOR CONSTRUCTION

EAST SAN FERNANDO VALLEY LRT
DU06 - DRAINAGE SEGMENT A1
STORM DRAIN PLAN AND PROFILE
VAN NUYS BLVD STA 519+00 TO 523+00

CONTRACT NO PS89616000	REV
DRAWING NO UD-211	
SCALE 1" = 20'	
SHEET NO	

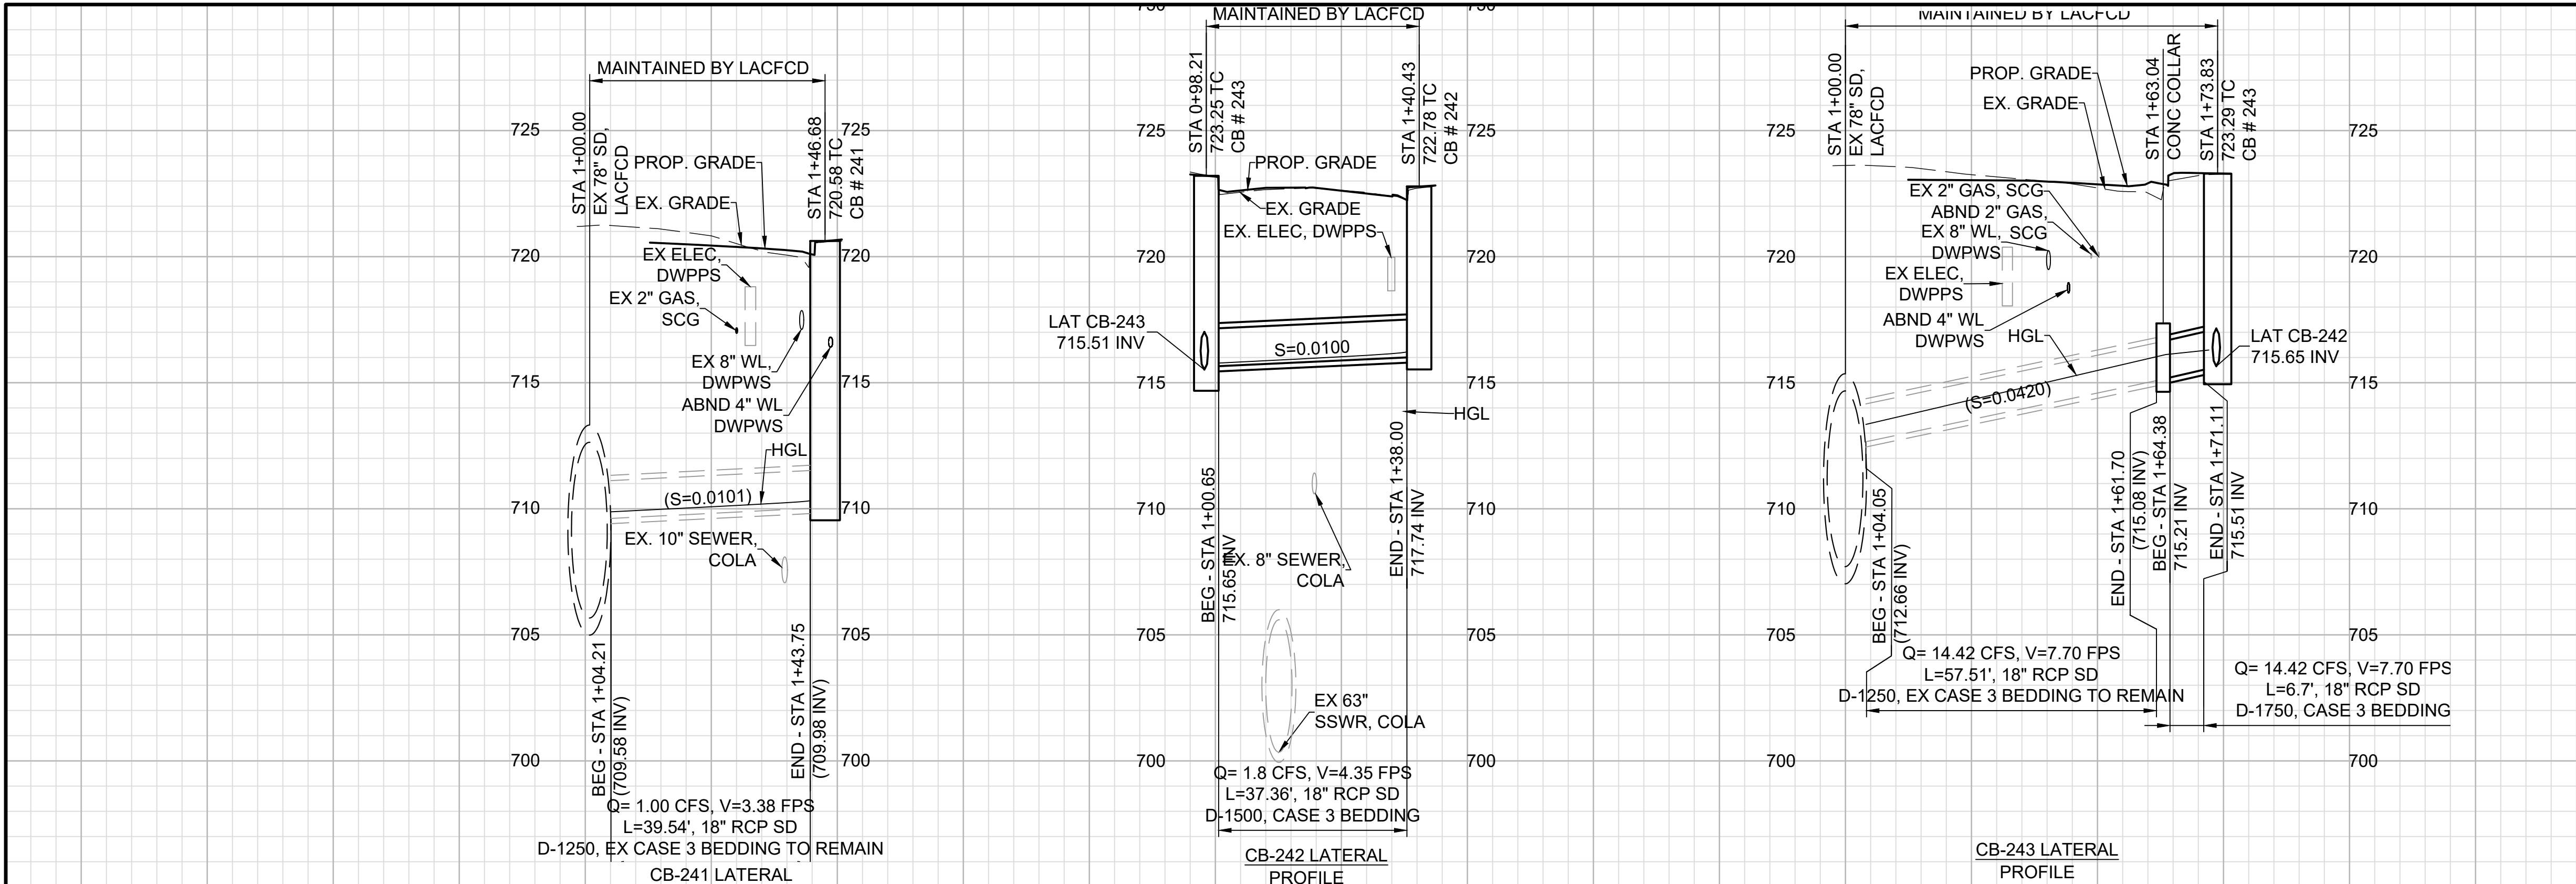

CONSTRUCTION SYMBOLS:

- CONSTRUCT ○◻ REMODEL EXISTING
◻ EXISTING ◻○ REMOVE AND CONSTRUCT
◻ REMOVE ○ WORK BY OTHERS

CONSTRUCTION NOTES:

- 79 REINFORCED CONCRETE PIPE
82 JUNCTION STRUCTURE
85 STORM DRAIN MANHOLE
97 CONCRETE COLLAR
98 MONOLITHIC CATCH BASIN CONNECTION
99 CURB OPENING CATCH BASIN
102 OFFSET MANHOLE "TYPE B"
115 CAP MH



NOTES:

- SEE COMPOSITE UTILITY REARRANGEMENT PLANS (UR) FOR EXISTING UTILITY CONFLICTS AND PROPOSED RELOCATIONS. CONTRACTOR TO DETERMINE UTILITY DEPTHS AND LOCATIONS ON STORM DRAIN PROFILES PRIOR TO CONSTRUCTION.
- SEE TRACKWORK PLANS (T) FOR TRACK DRAIN DETAILS, SWITCH MACHINE DRAIN DETAILS, AND TRACK-RELATED WORK.
- SEE STREET IMPROVEMENT PLANS (CS) FOR ROADWAY-RELATED WORK.
- SEE DU04-SEGMENT B METRO TRACK GUIDEWAY PLANS (D) FOR TRACK GUIDEWAY STORM DRAIN IMPROVEMENTS.
- ALL NEW AND REMOVED/REPLACED CATCH BASINS UNDER THIS PROJECT SHALL INCLUDE CATCH BASIN OPENING SCREENS AND INSERTS. REUSE EXISTING SCREENS WHEN APPLICABLE.
- ALL NEW AND REMOVED/REPLACED CATCH BASINS UNDER THIS PROJECT SHALL BE STENCILED WITH PROHIBITIVE LANGUAGE "NO DUMPING - DRAIN TO OCEAN."
- SEE TRAFFIC AND SIGNAL PLANS FOR SIGNAL RELATED WORK.
- PROTECT IN PLACE ALL EXISTING BEDDING, UNLESS STATED ON PROFILE.

PROFILE SCALE

HORIZ: 1"=20'
VERT: 1"=4'

LINE/CURVE DATA TABLE			
NO.	LENGTH	BEARING/DELTA	RADIUS
L1	38.66	N16° 38' 00.52"W	--
L2	7.15	S75° 26' 06.87"W	--
L3	11.29	S79° 38' 03.78"E	--

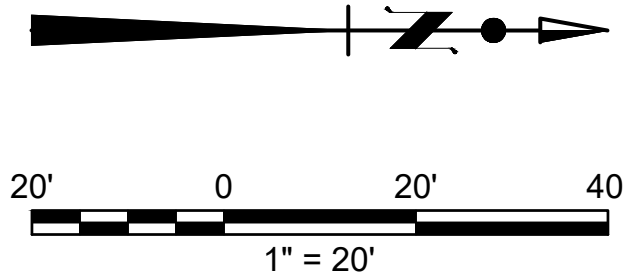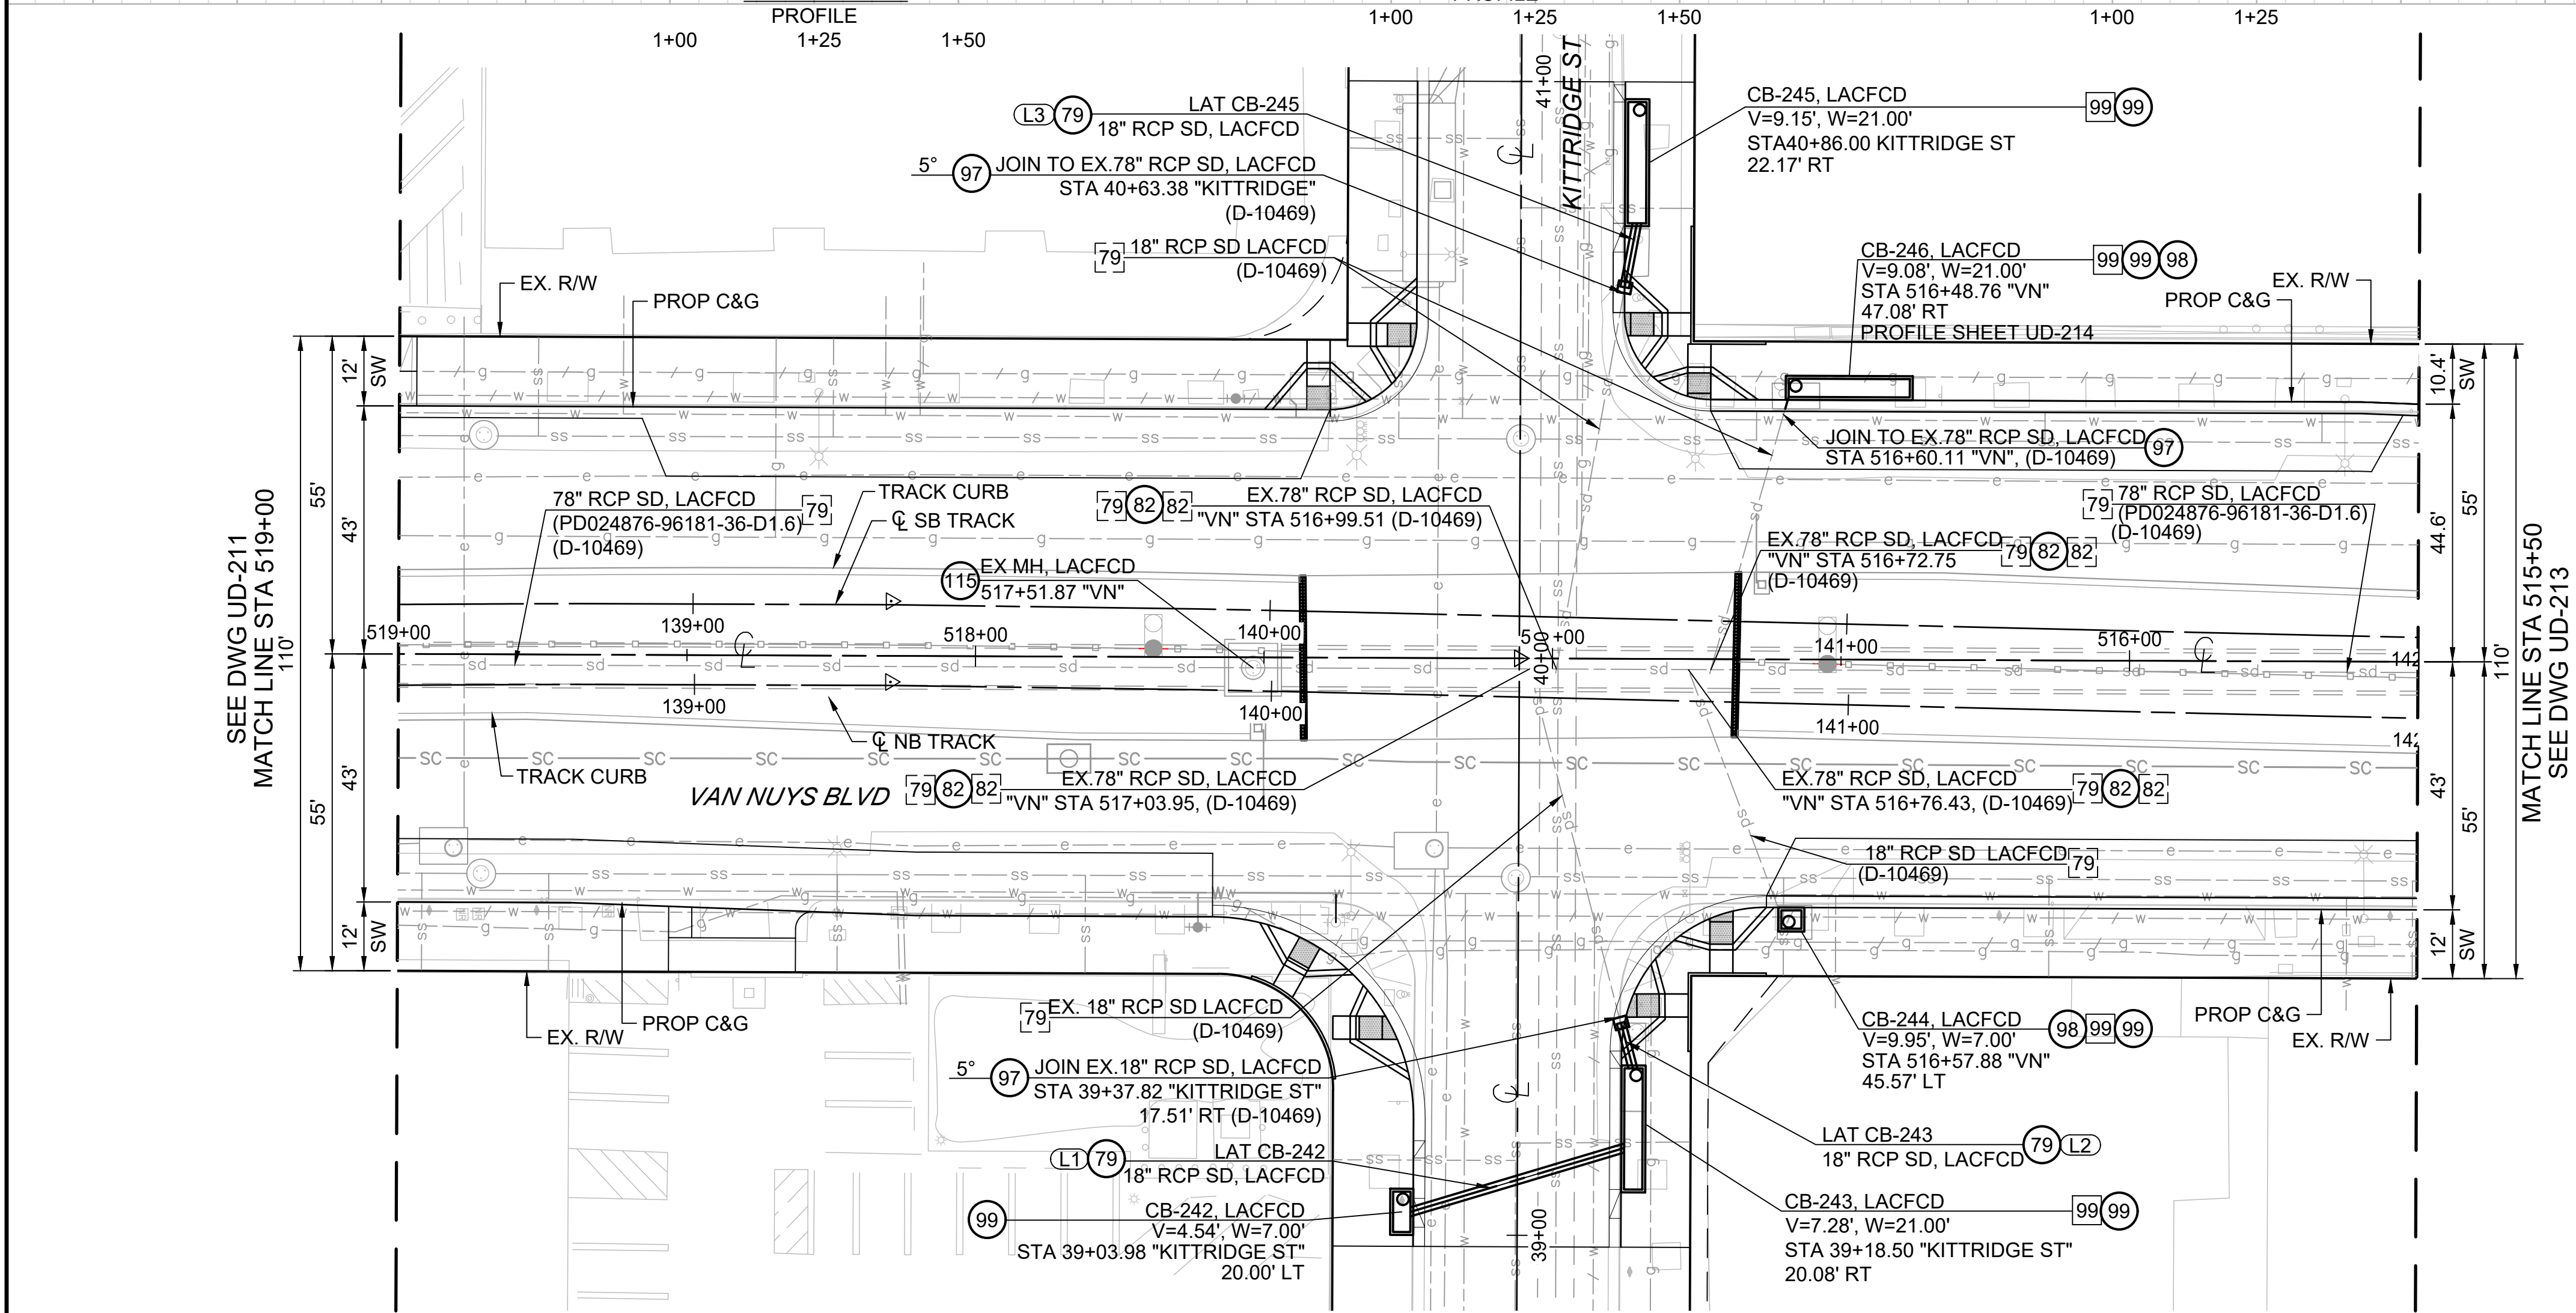

THE PREPARATION OF THIS DRAWING HAS BEEN FINANCED IN PART THROUGH A GRANT FROM THE U.S. DEPARTMENT OF TRANSPORTATION, FEDERAL TRANSIT ADMINISTRATION (FTA), UNDER THE FEDERAL TRANSIT ACT OF 1964, AS AMENDED, AND IN PART BY THE TAXES OF THE CITIZENS OF LOS ANGELES COUNTY AND OF THE STATE OF CALIFORNIA.							DESIGNED BY N. SOTO
							DRAWN BY R. VENEGAS
							CHECKED BY N. BUSCH
							IN CHARGE N. BUSCH
							DATE 12/11/2025
REV	DATE	BY	APP	REG NO	EXPIRES	SEAL HOLDER	DESCRIPTION
C	12/15/25	NS	JR	C78082	09/30/27	J. RIMORIN	100% SUBMITTAL
B	08/18/25	AR	NB	C65608	09/30/27	N. BUSCH	85% SUBMITTAL
A	03/07/25	KM	JR	C78082	09/30/27	J. RIMORIN	60% SUBMITTAL

**LOS ANGELES COUNTY**
METROPOLITAN TRANSPORTATION AUTHORITY

**San Fernando Transit Constructors**

**AECOM**

14300 ARMINTA ST.
LOS ANGELES, CA 91402
TEL: 951.684.5360


1111 S. GRAND AVE., SUITE 103
LOS ANGELES, CA 90015
213.932.0700

100% SUBMITTAL - NOT FOR CONSTRUCTION

EAST SAN FERNANDO VALLEY LRT
DU06 - DRAINAGE SEGMENT A1
STORM DRAIN PLAN AND PROFILE
VAN NUYS BLVD STA 515+50 TO 519+00

CONTRACT NO PS89616000	REV
DRAWING NO UD-212	
SCALE 1" = 20'	
SHEET NO	

FILE PATH: \\S0724657-ESFV-PH2\PROJECT FILES\900_CAD\20_SHEETS\DU06\9_UD_DRAINAGE\PS89616000-DU06-UD-212.DWG
PLOT DATE: 12/16/2025 - 2:23 PM USER: ADRIANROBLES

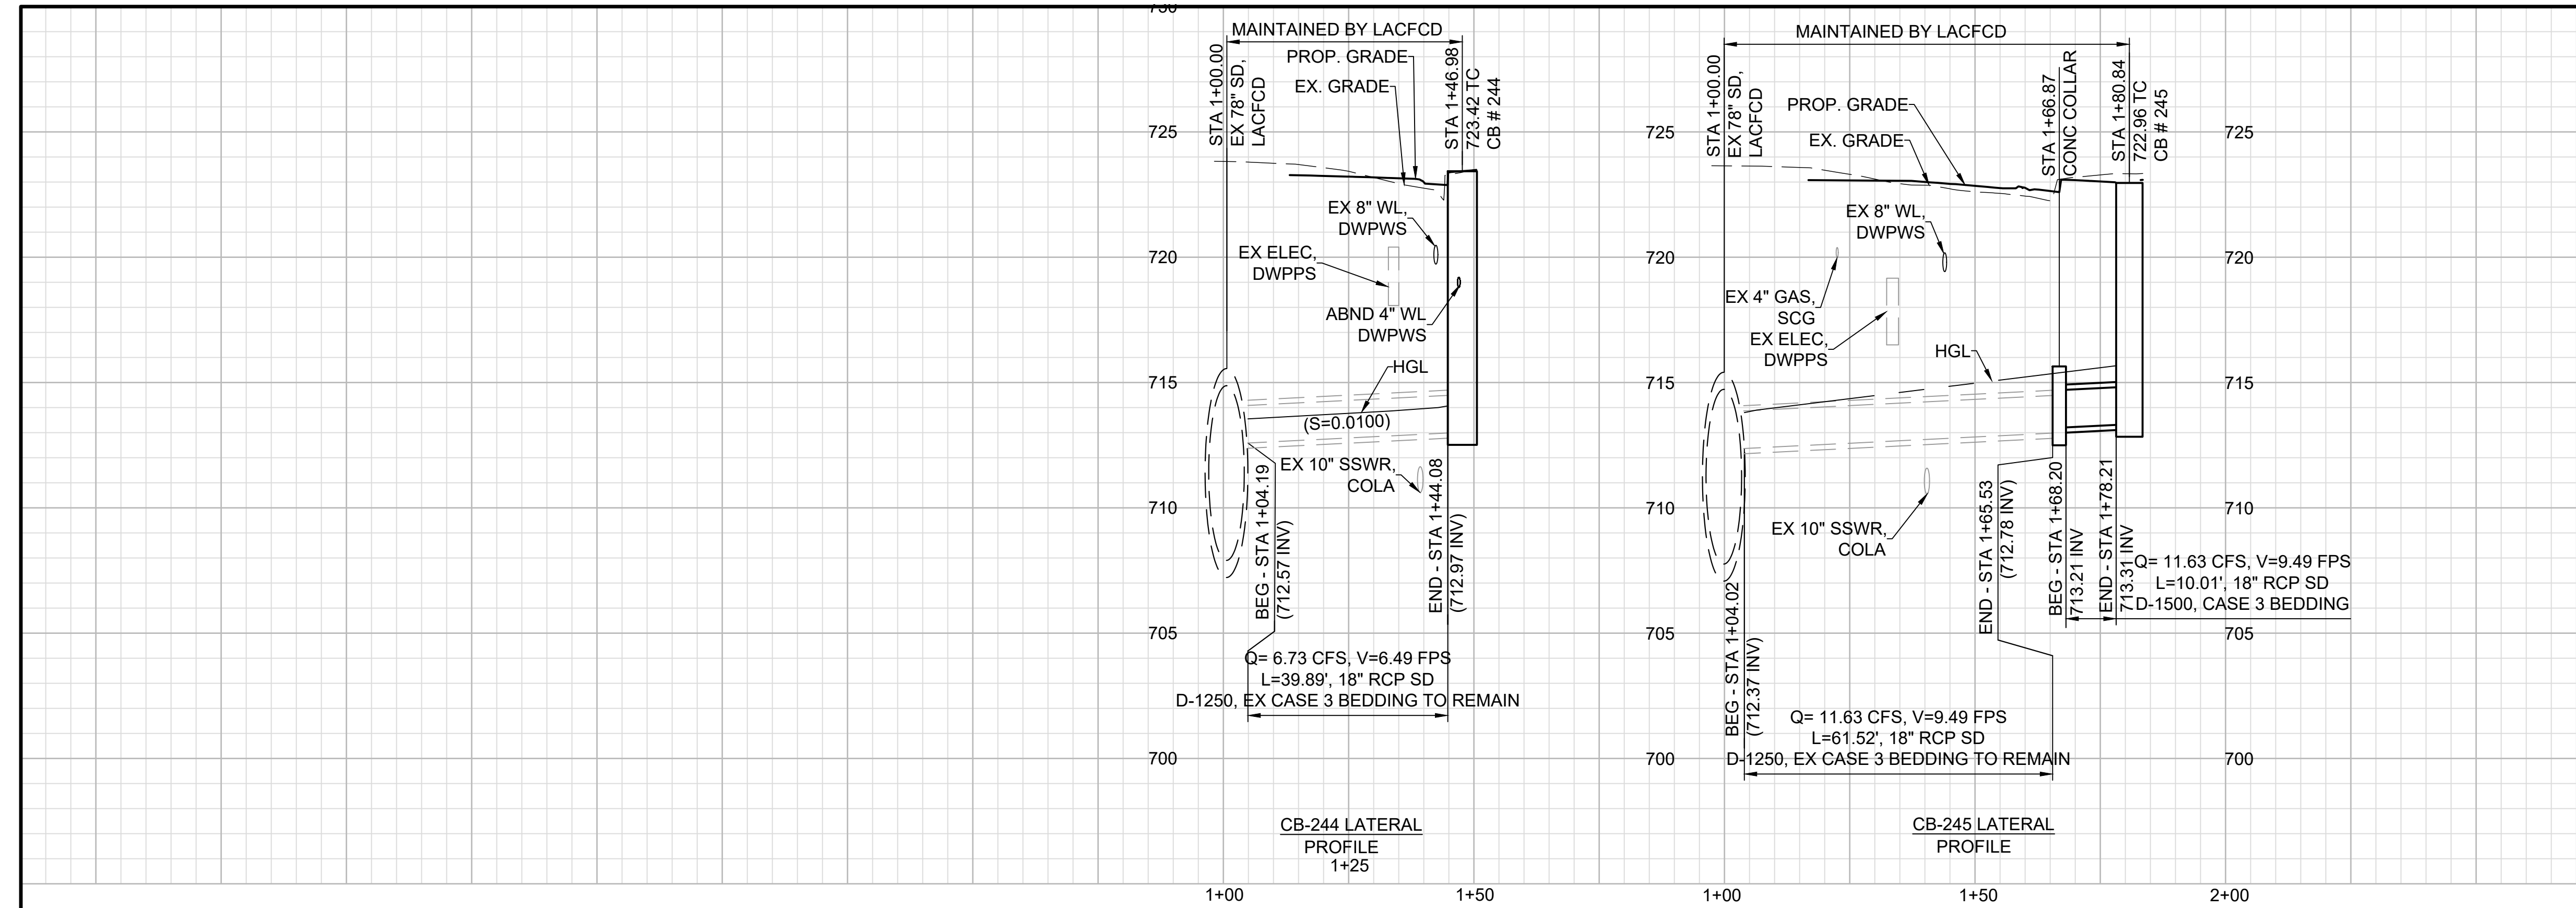

CONSTRUCTION SYMBOLS:

- CONSTRUCT ○◻ REMODEL EXISTING
◻ EXISTING ◻○ REMOVE AND CONSTRUCT
◻ REMOVE ◻ WORK BY OTHERS

CONSTRUCTION NOTES:



- 79 REINFORCED CONCRETE PIPE
82 JUNCTION STRUCTURE
85 STORM DRAIN MANHOLE
97 CONCRETE COLLAR
98 MONOLITHIC CATCH BASIN CONNECTION
99 CURB OPENING CATCH BASIN
102 OFFSET MANHOLE "TYPE B"
115 CAP MH

NOTES:

1. SEE COMPOSITE UTILITY REARRANGEMENT PLANS (UR) FOR EXISTING UTILITY CONFLICTS AND PROPOSED RELOCATIONS. CONTRACTOR TO DETERMINE UTILITY DEPTHS AND LOCATIONS ON STORM DRAIN PROFILES PRIOR TO CONSTRUCTION.
2. SEE TRACKWORK PLANS (T) FOR TRACK DRAIN DETAILS, SWITCH MACHINE DRAIN DETAILS, AND TRACK-RELATED WORK.
3. SEE STREET IMPROVEMENT PLANS (CS) FOR ROADWAY-RELATED WORK.
4. SEE DU04-SEGMENT B METRO TRACK GUIDEWAY PLANS (D) FOR TRACK GUIDEWAY STORM DRAIN IMPROVEMENTS.
5. ALL NEW AND REMOVED/REPLACED CATCH BASINS UNDER THIS PROJECT SHALL INCLUDE CATCH BASIN OPENING SCREENS AND INSERTS. REUSE EXISTING SCREENS WHEN APPLICABLE.
6. ALL NEW AND REMOVED/REPLACED CATCH BASINS UNDER THIS PROJECT SHALL BE STENCILED WITH PROHIBITIVE LANGUAGE "NO DUMPING - DRAIN TO OCEAN."
7. SEE TRAFFIC AND SIGNAL PLANS FOR SIGNAL RELATED WORK.
8. PROTECT IN PLACE ALL EXISTING BEDDING, UNLESS STATED ON PROFILE.


PROFILE SCALE

HORIZ: 1"=20'
VERT: 1"=4'

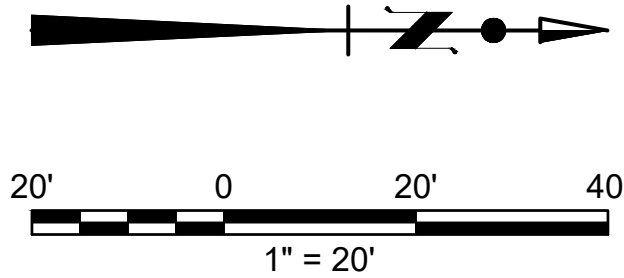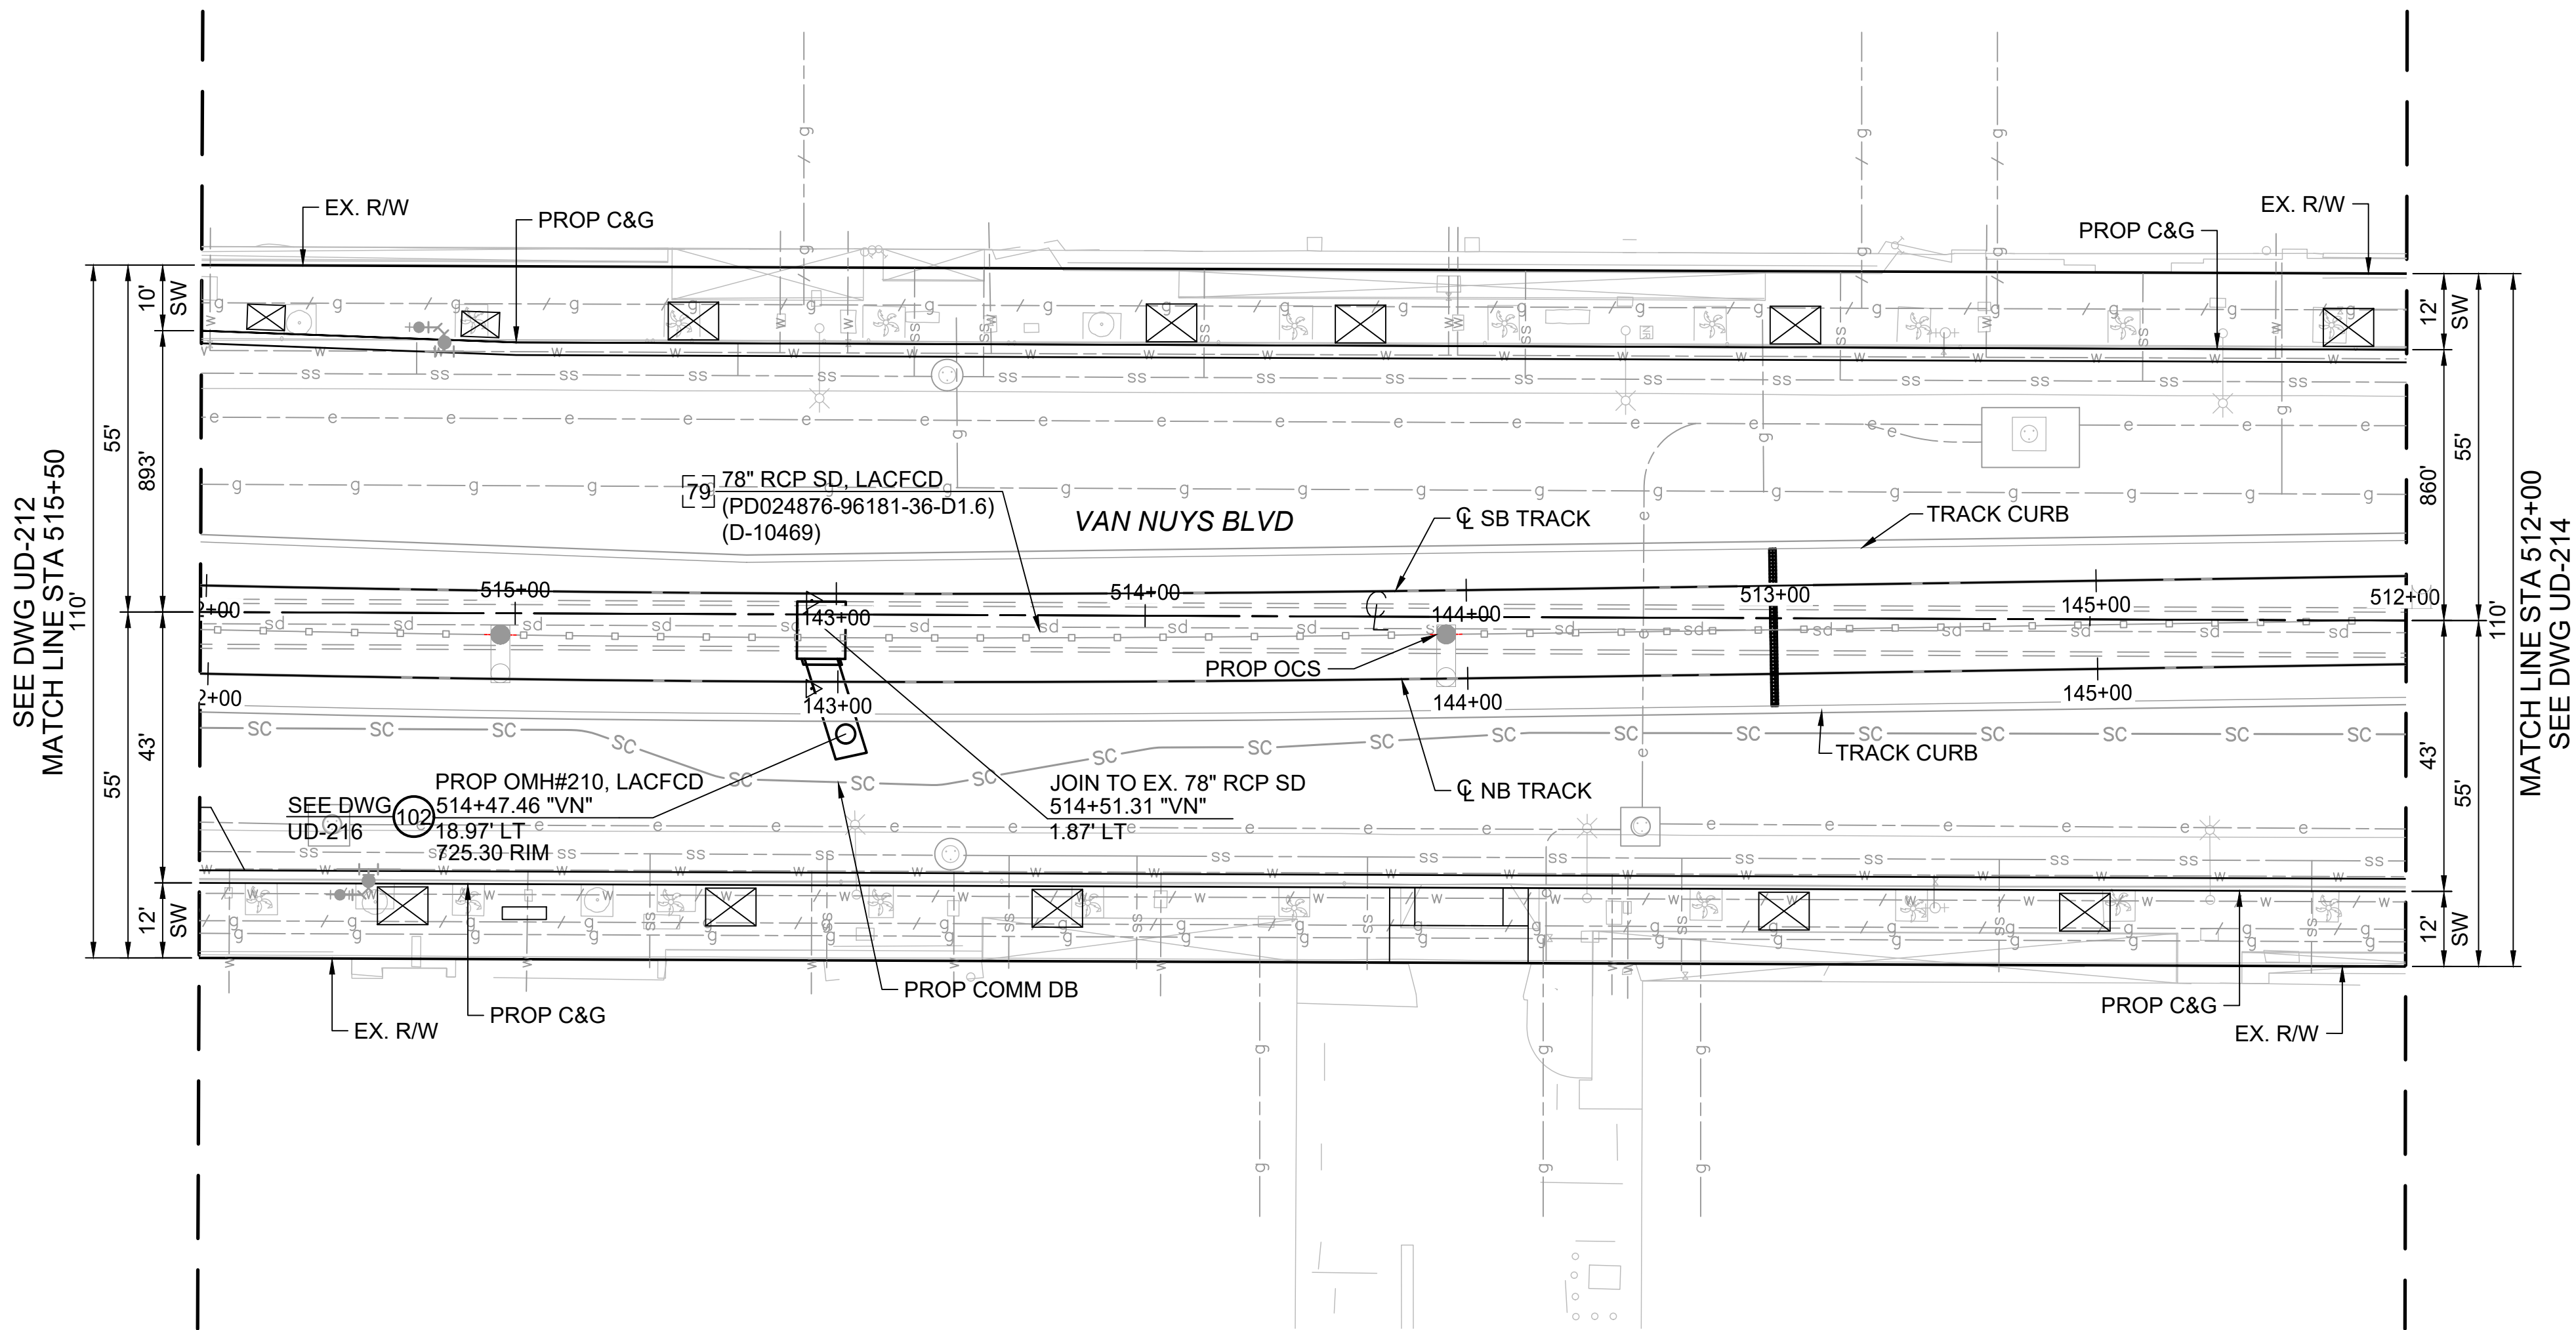

THE PREPARATION OF THIS DRAWING HAS BEEN FINANCED IN PART THROUGH A GRANT FROM THE U.S. DEPARTMENT OF TRANSPORTATION, FEDERAL TRANSIT ADMINISTRATION (FTA), UNDER THE FEDERAL TRANSIT ACT OF 1964, AS AMENDED, AND IN PART BY THE TAXES OF THE CITIZENS OF LOS ANGELES COUNTY AND OF THE STATE OF CALIFORNIA.								DESIGNED BY N. SOTO		 LOS ANGELES COUNTY METROPOLITAN TRANSPORTATION AUTHORITY				 San Fernando Transit Constructors						85% SUBMITTAL - NOT FOR CONSTRUCTION		EAST SAN FERNANDO VALLEY LRT DU06 - DRAINAGE SEGMENT A1 STORM DRAIN PLAN AND PROFILE VAN NUYS BLVD STA 512+00 TO 515+50				CONTRACT NO PS89616000	
								DRAWN BY R. VENEGAS										CHECKED BY N. BUSCH		IN CHARGE N. BUSCH						SHEET NO	
								DATE 12/11/2025		SEAL HOLDER		DESCRIPTION		DRAWING NO UD-213		REV											
								REV		DATE		BY		APP		REG NO		EXPIRES		SHEET NO		SCALE 1" = 20'					
								C		12/15/25		NS		JR		C78082		09/30/27		J. RIMORIN		100% SUBMITTAL					
B		08/18/25		AR		NB		C65608		09/30/27		N.BUSCH		85% SUBMITTAL													
A		03/07/25		KM		JR		C78082		09/30/27		J. RIMORIN		60% SUBMITTAL													

FILE PATH: \\S072457-ESFV-PH2\PROJECT FILES\900_CAD\20_SHEETS\DU06\09_UD_DRAINAGE\PS89616000-DU06-UD-213.DWG
PLOT DATE: 12/16/2025 - 1:12 PM USER: ADRIANROBLES

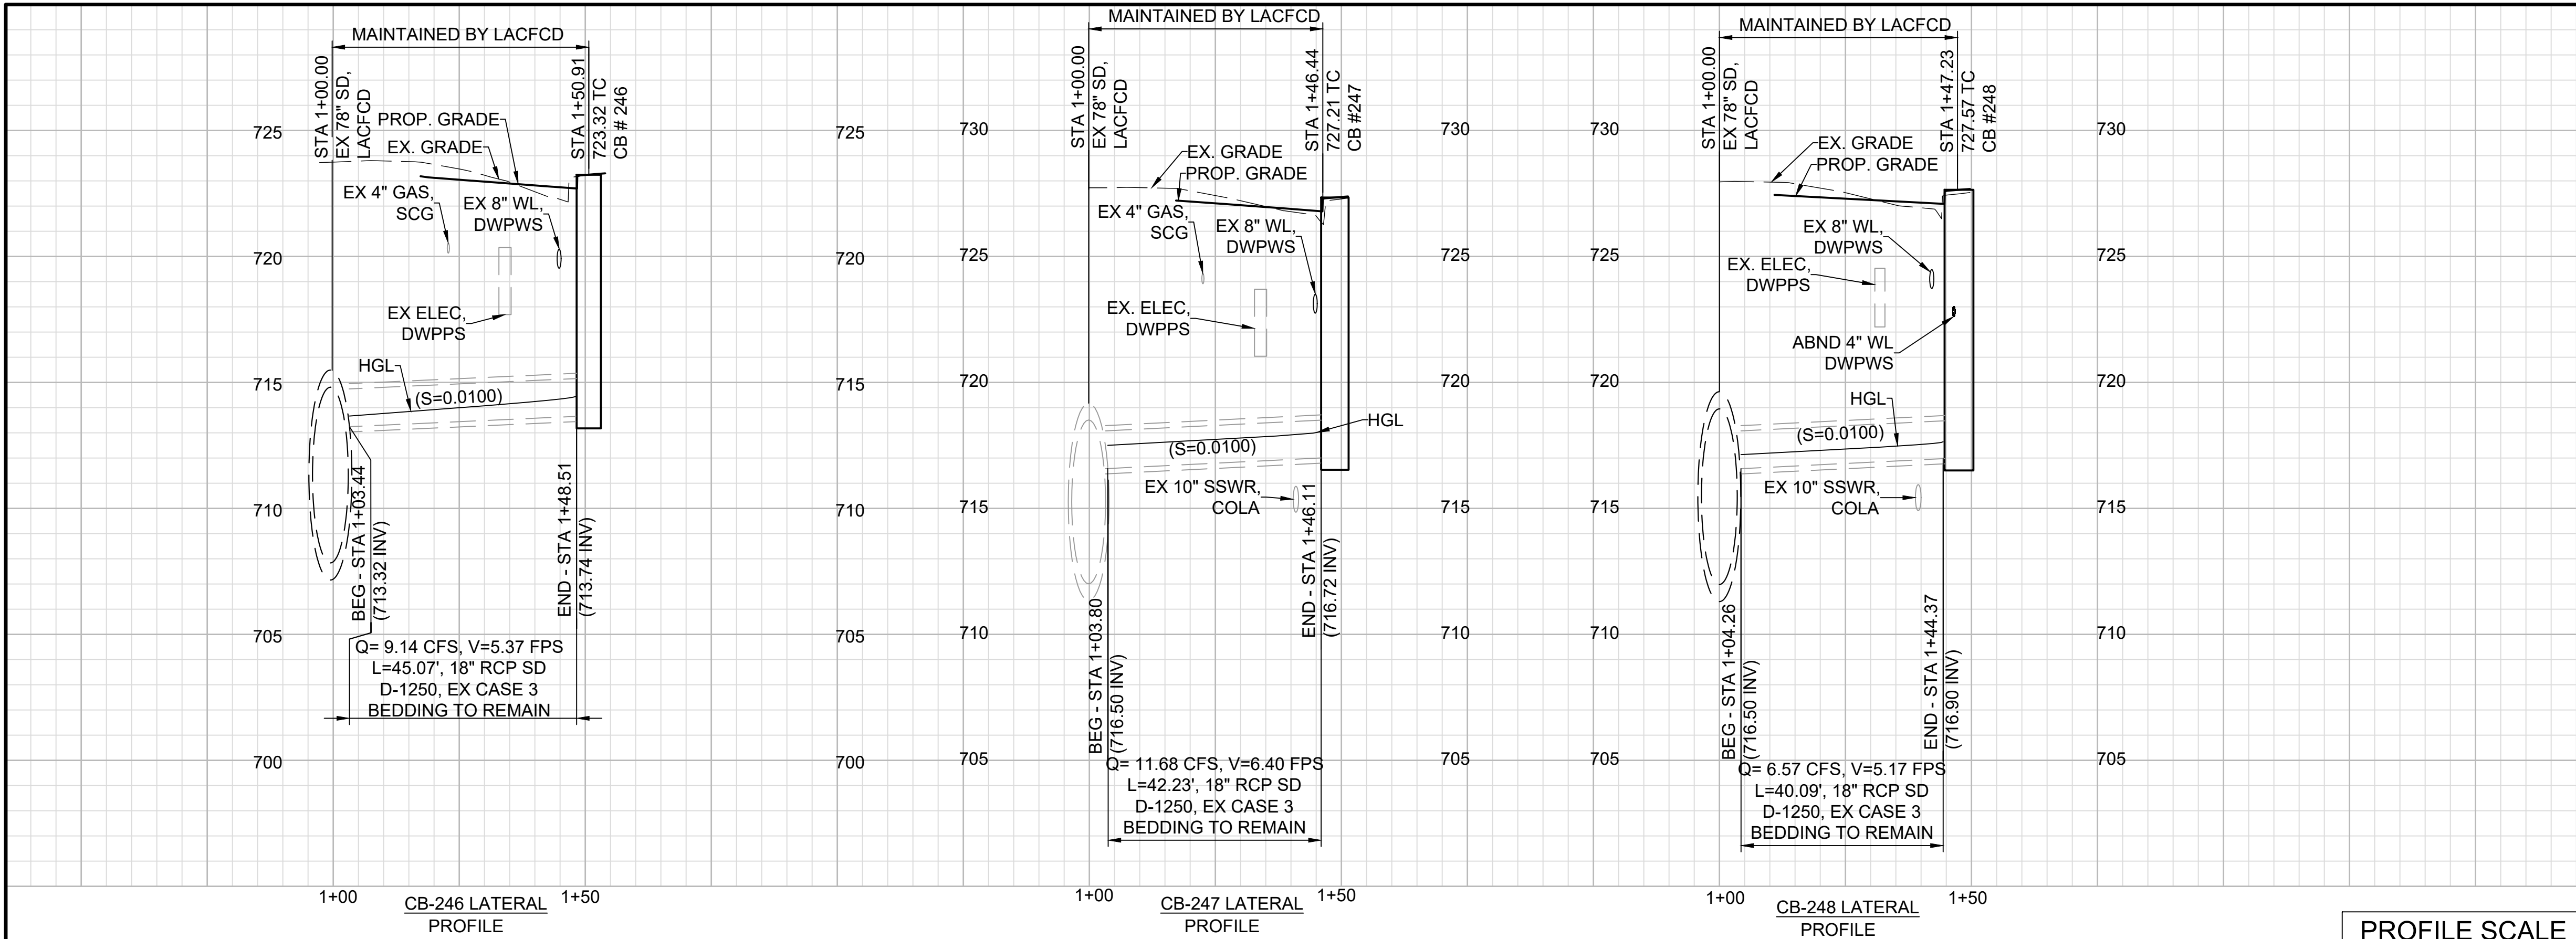

CONSTRUCTION SYMBOLS:

- CONSTRUCT ○◻ REMODEL EXISTING
◻ EXISTING ◻○ REMOVE AND CONSTRUCT
◻ REMOVE ○ WORK BY OTHERS

CONSTRUCTION NOTES:



- 79 REINFORCED CONCRETE PIPE
82 JUNCTION STRUCTURE
85 STORM DRAIN MANHOLE
97 CONCRETE COLLAR
98 MONOLITHIC CATCH BASIN CONNECTION
99 CURB OPENING CATCH BASIN
102 OFFSET MANHOLE "TYPE B"
115 CAP MH

NOTES:

- SEE COMPOSITE UTILITY REARRANGEMENT PLANS (UR) FOR EXISTING UTILITY CONFLICTS AND PROPOSED RELOCATIONS. CONTRACTOR TO DETERMINE UTILITY DEPTHS AND LOCATIONS ON STORM DRAIN PROFILES PRIOR TO CONSTRUCTION.
- SEE TRACKWORK PLANS (T) FOR TRACK DRAIN DETAILS, SWITCH MACHINE DRAIN DETAILS, AND TRACK-RELATED WORK.
- SEE STREET IMPROVEMENT PLANS (CS) FOR ROADWAY-RELATED WORK.
- SEE DU04-SEGMENT B METRO TRACK GUIDEWAY PLANS (D) FOR TRACK GUIDEWAY STORM DRAIN IMPROVEMENTS.
- ALL NEW AND REMOVED/REPLACED CATCH BASINS UNDER THIS PROJECT SHALL INCLUDE CATCH BASIN OPENING SCREENS AND INSERTS. REUSE EXISTING SCREENS WHEN APPLICABLE.
- ALL NEW AND REMOVED/REPLACED CATCH BASINS UNDER THIS PROJECT SHALL BE STENCILED WITH PROHIBITIVE LANGUAGE "NO DUMPING - DRAIN TO OCEAN."
- SEE TRAFFIC AND SIGNAL PLANS FOR SIGNAL RELATED WORK.
- PROTECT IN PLACE ALL EXISTING BEDDING, UNLESS STATED ON PROFILE.

PROFILE SCALE

HORIZ: 1"=20'
VERT: 1"=4'

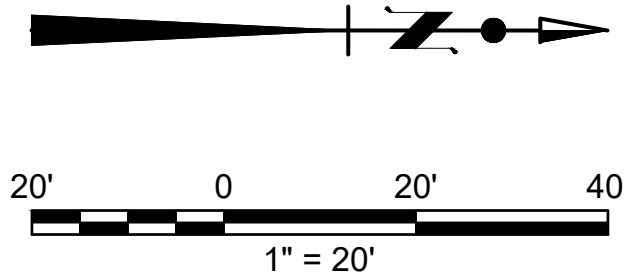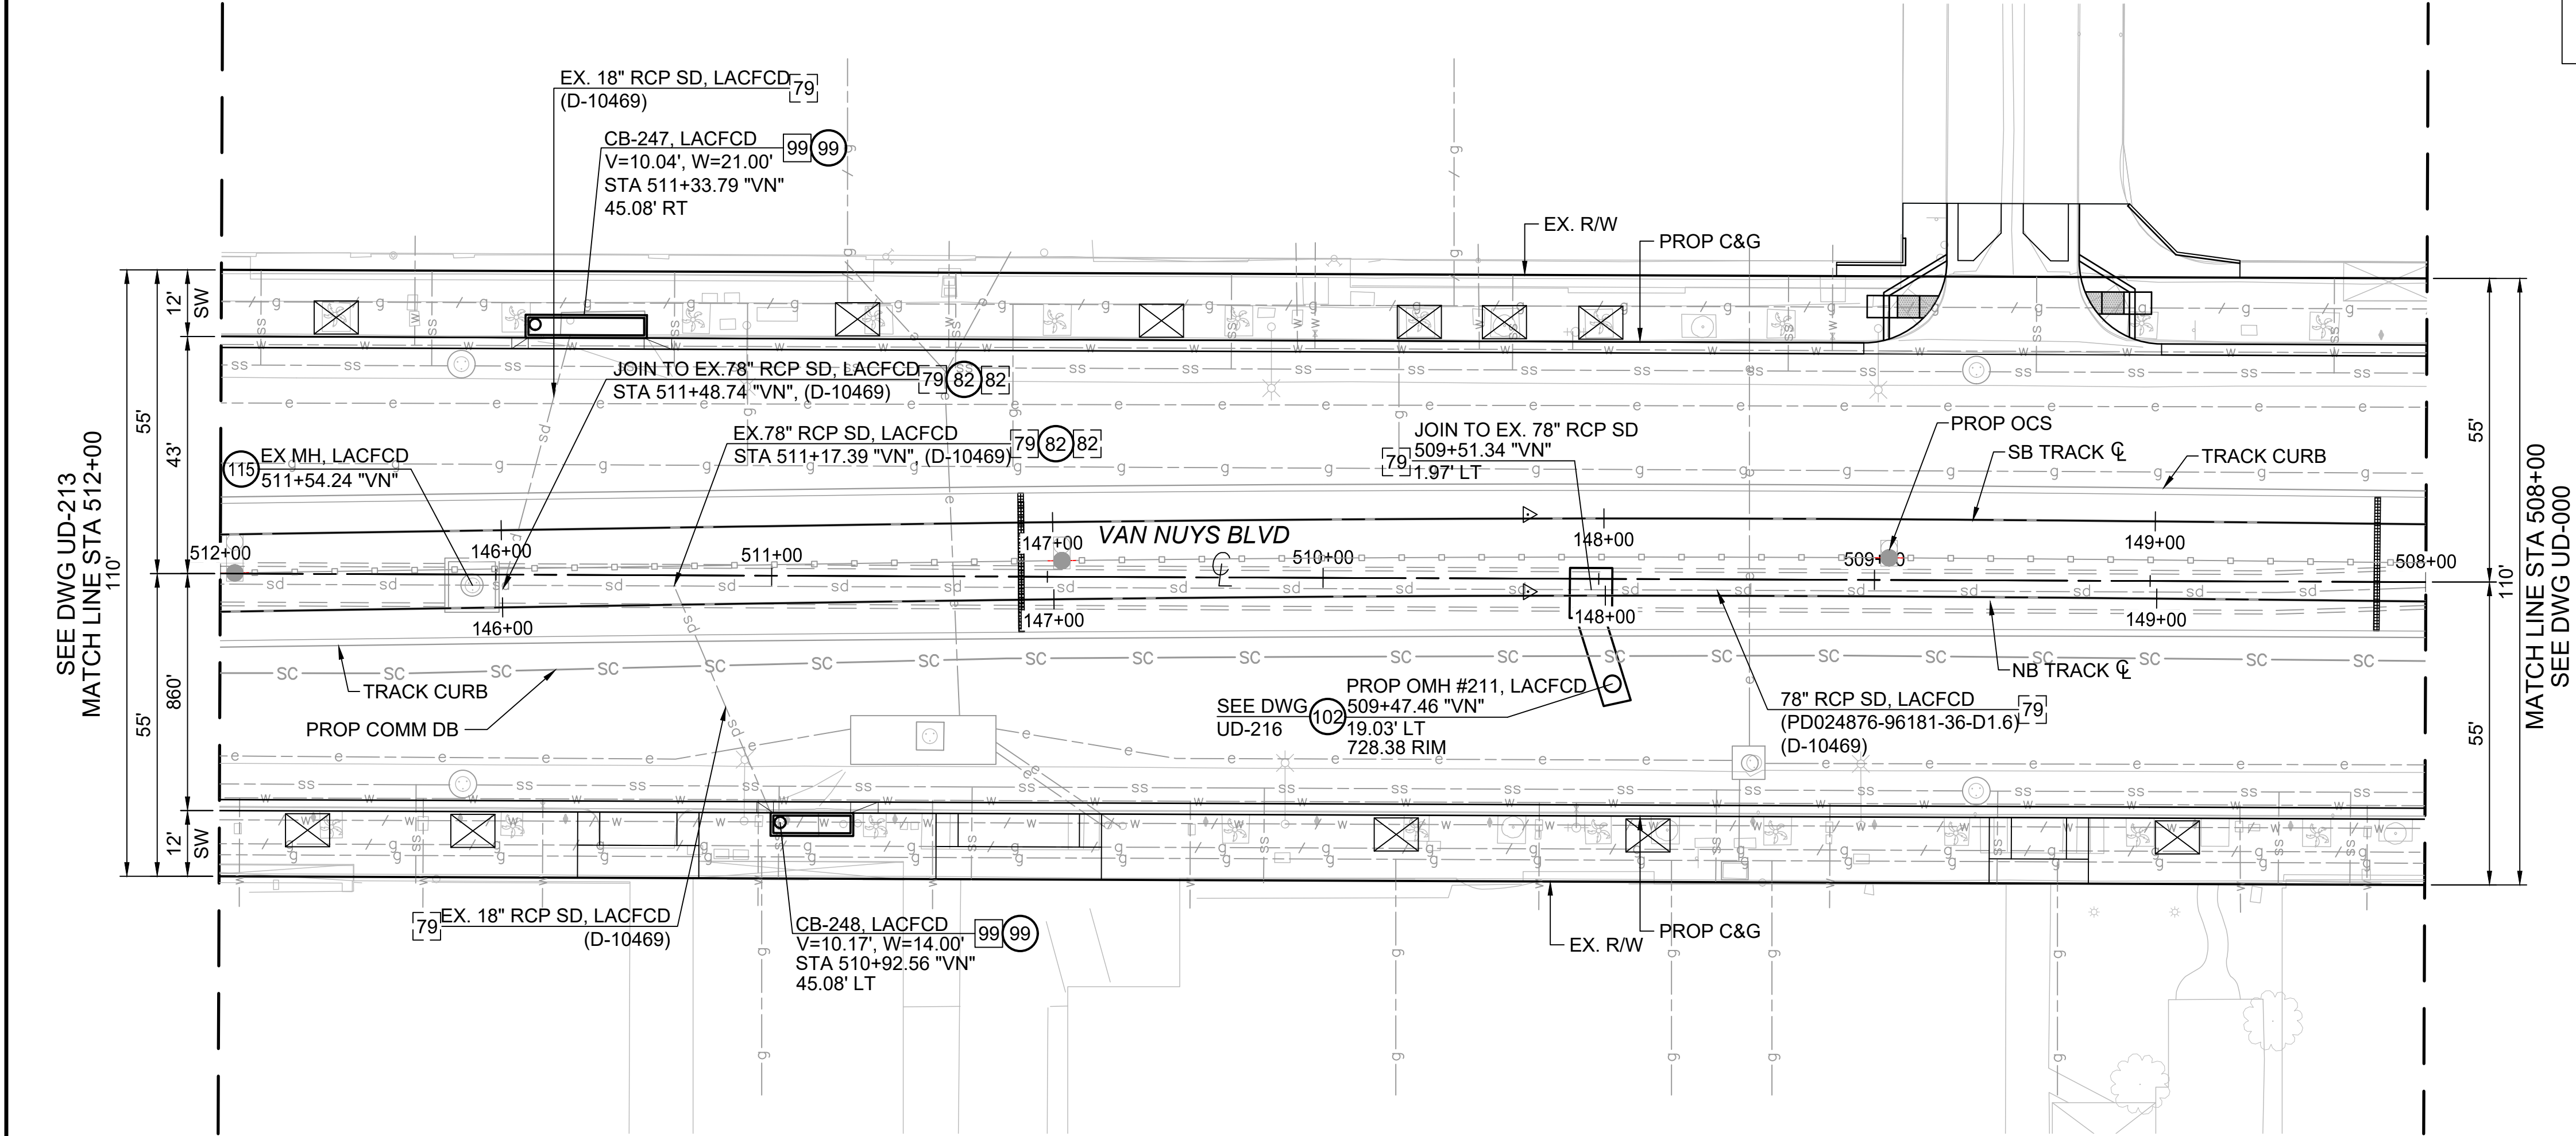

THE PREPARATION OF THIS DRAWING HAS BEEN FINANCED IN PART THROUGH A GRANT FROM THE U.S. DEPARTMENT OF TRANSPORTATION, FEDERAL TRANSIT ADMINISTRATION (FTA), UNDER THE FEDERAL TRANSIT ACT OF 1964, AS AMENDED, AND IN PART BY THE TAXES OF THE CITIZENS OF LOS ANGELES COUNTY AND OF THE STATE OF CALIFORNIA.									
REV	DATE	BY	APP	REG NO	EXPIRES	SEAL HOLDER	DESCRIPTION	DESIGNED BY N. SOTO	
								DRAWN BY R. VENEGAS	
C	12/15/25	NS	JR	C78082	09/30/27	J. RIMORIN	100% SUBMITTAL	CHECKED BY N. BUSCH	
B	08/18/25	AR	NB	C65608	09/30/27	N. BUSCH	85% SUBMITTAL	IN CHARGE N. BUSCH	
A	03/07/25	KM	JR	C78082	09/30/27	J. RIMORIN	60% SUBMITTAL	DATE 12/11/2025	

**LOS ANGELES COUNTY**
METROPOLITAN TRANSPORTATION AUTHORITY

**San Fernando Transit Constructors**

**AECOM**

14300 ARMINTA ST.
LOS ANGELES, CA 91402
TEL: 951.684.5360

100% SUBMITTAL - NOT FOR CONSTRUCTION

EAST SAN FERNANDO VALLEY LRT
DU06 - DRAINAGE SEGMENT A1
STORM DRAIN PLAN AND PROFILE
VAN NUYS BLVD STA 508+00 TO 512+00


CONTRACT NO
PS89616000

DRAWING NO
UD-214

SCALE
1" = 20'


SHEET NO

FILE PATH: \\0072457-ESFV-PH2\PROJECT FILES\900_CAD\20_SHEETS\DU06\09_UD_DRAINAGE\PS89616000-DU06-UD-214.DWG
PLOT DATE: 12/16/2025 - 4:23 PM USER: NEREDASOTO

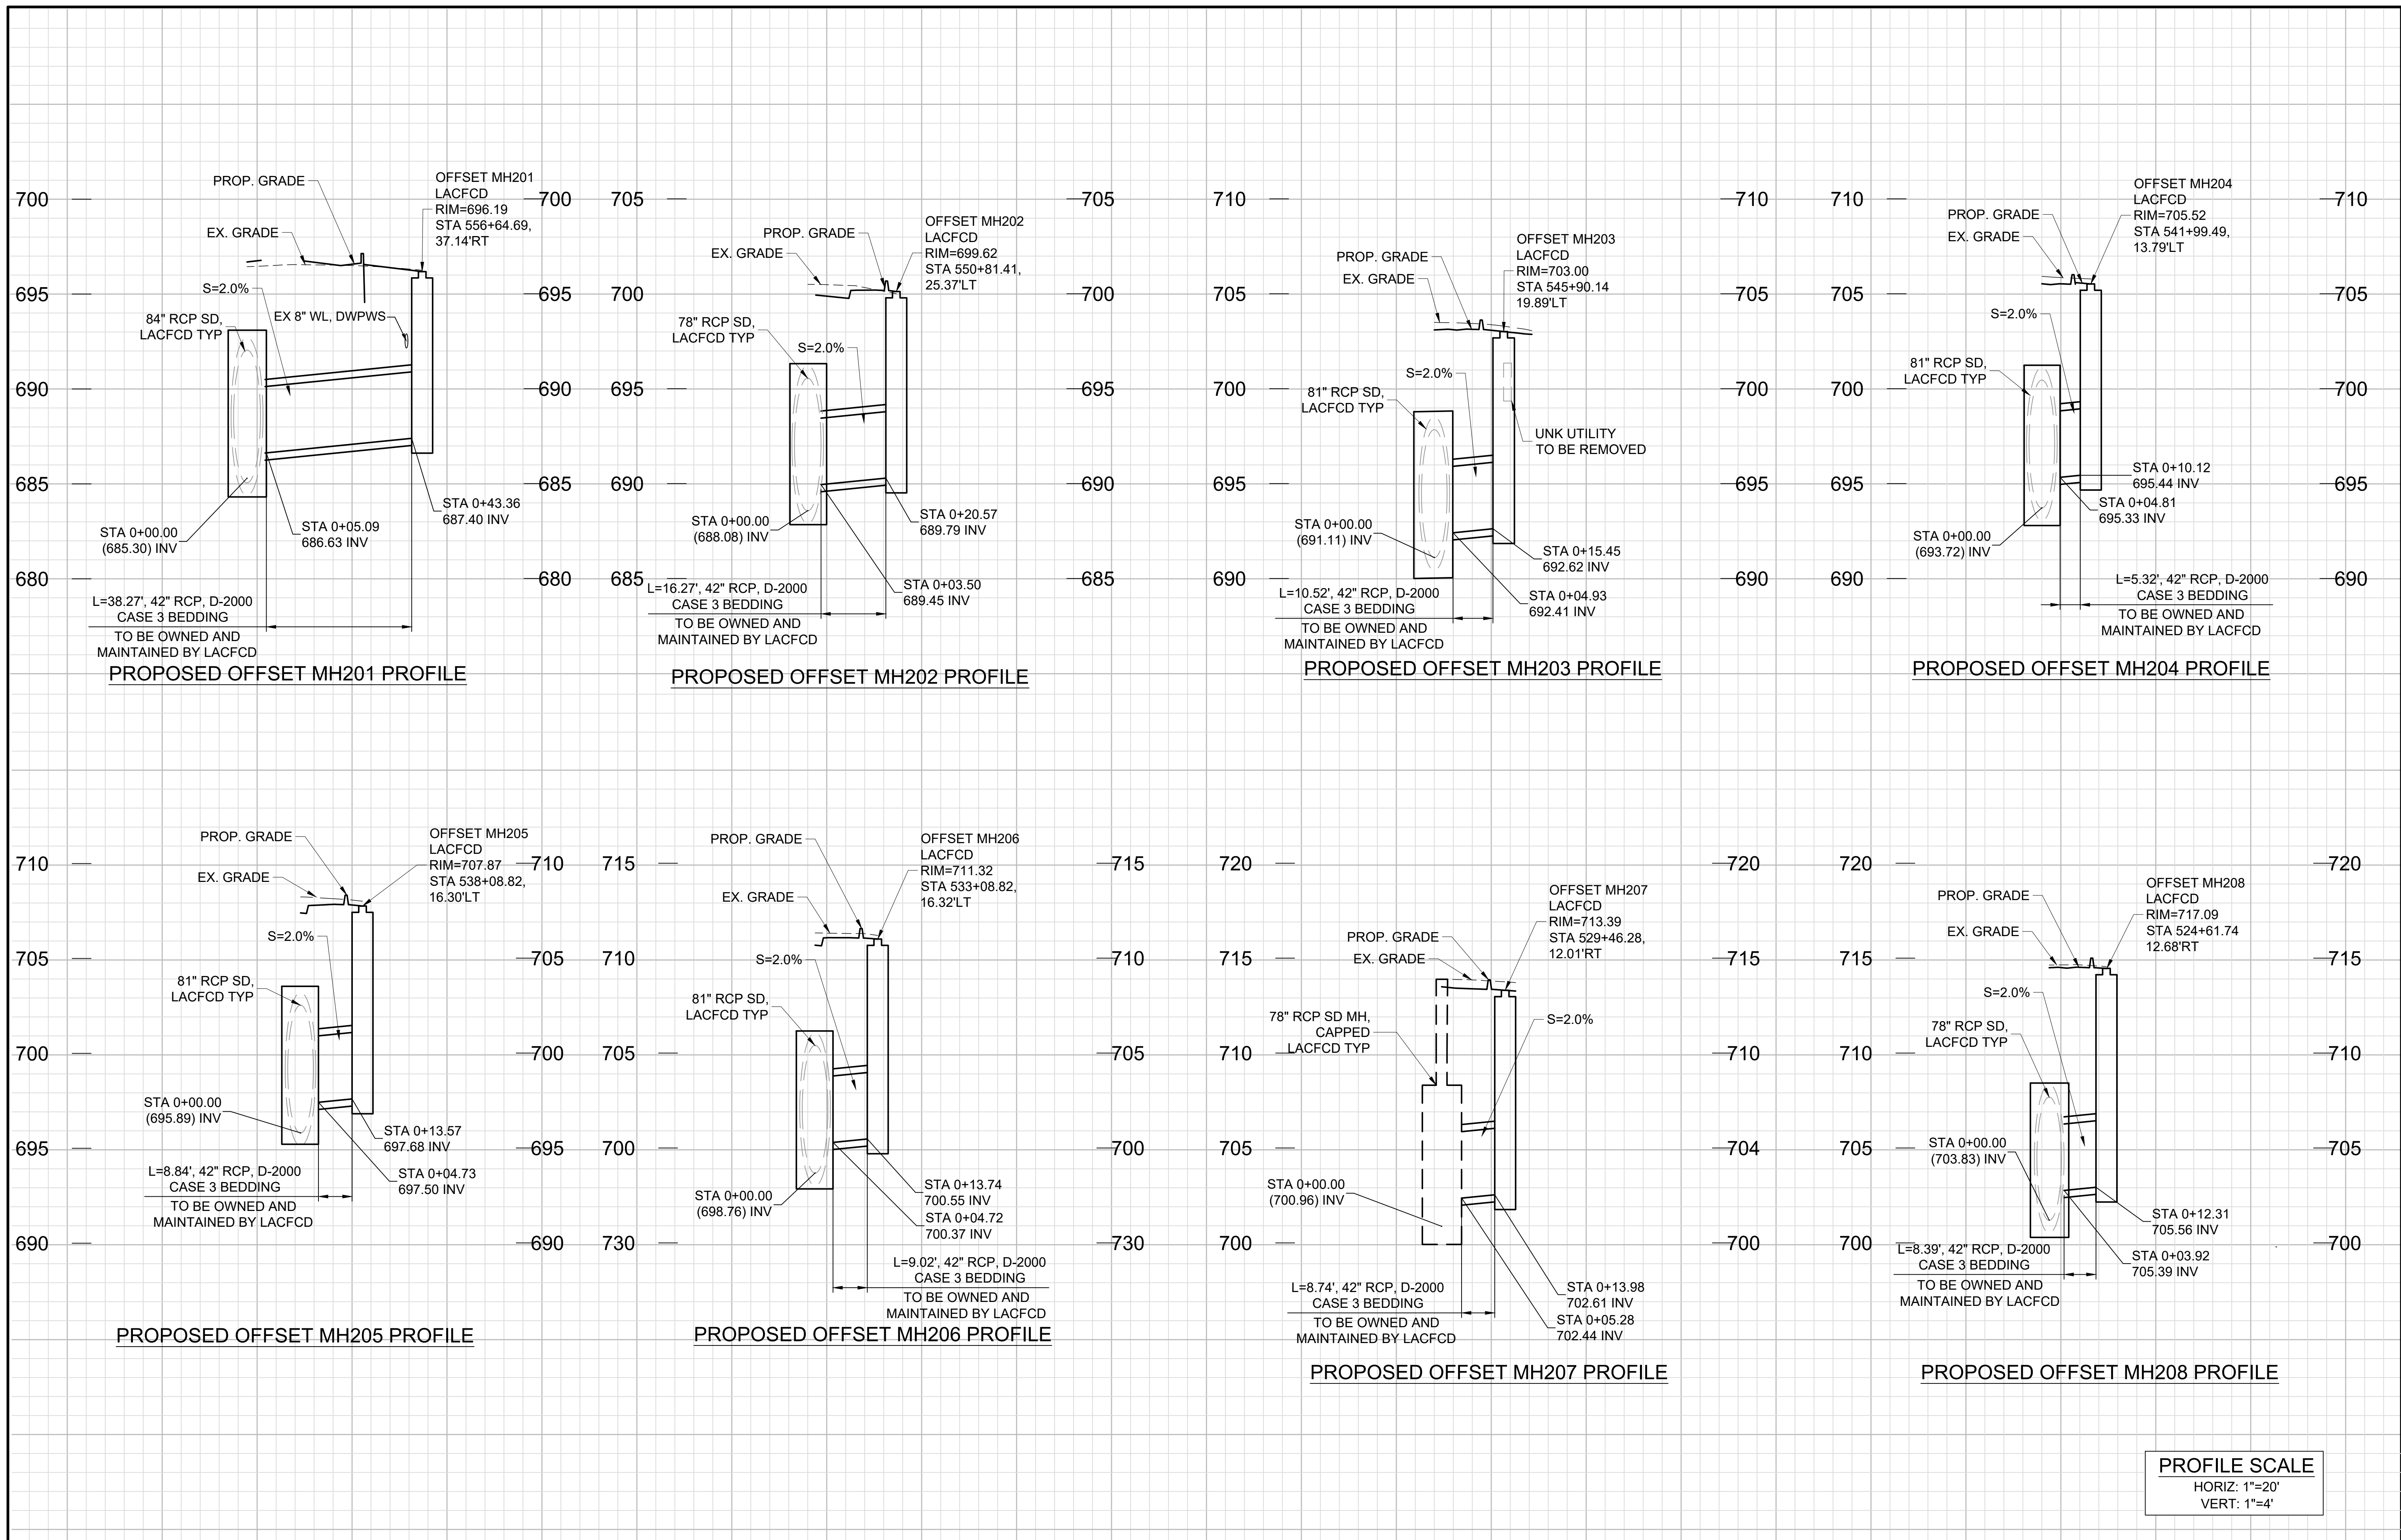







THE PREPARATION OF THIS DRAWING HAS BEEN FINANCED IN PART THROUGH A GRANT FROM THE U.S. DEPARTMENT OF TRANSPORTATION, FEDERAL TRANSIT ADMINISTRATION (FTA), UNDER THE FEDERAL TRANSIT ACT OF 1964, AS AMENDED, AND IN PART BY THE TAXES OF THE CITIZENS OF LOS ANGELES COUNTY AND OF THE STATE OF CALIFORNIA.								DESIGNED BY N. SOTO		A SIGNED & SEALED ORIGINAL OF REV 0 OF THIS DRAWING IS MAINTAINED BY METRO	 LOS ANGELES COUNTY METROPOLITAN TRANSPORTATION AUTHORITY				EAST SAN FERNANDO VALLEY LRT DU06 - CIVIL SEGMENT A1 STORM DRAIN PLAN OFFSET MANHOLE PROFILES SHEET 1 OF 2				CONTRACT NO PS89616000			
								DRAWN BY R. VENEGAS			 San Fernando Transit Constructors		 AECOM						DRAWING NO UD-215		REV	
								CHECKED BY N. BUSCH											100% SUBMITTAL - NOT FOR CONSTRUCTION			
								IN CHARGE N. BUSCH														
								DATE 12/15/2025														
C	12/15/25	NS	JR	C78082	09/30/27	J. RIMORIN	100% SUBMITTAL															
B	08/18/25	AR	NB	C65608	09/30/27	N.BUSCH	85% SUBMITTAL															
A	03/07/25	KM	JR	C78082	09/30/27	J. RIMORIN	60% SUBMITTAL															
REV	DATE	BY	APP	REG NO	EXPIRES	SEAL HOLDER	DESCRIPTION															

FILE PATH: \\S072457\ESV\PH2\PROJECT FILES\900_CAD\20_SHEETS\DU06\9_UD_DRAINAGE\PS89616000-DU06-UD-215-PR.DWG
PLOT DATE: 12/16/2025 - 12:16 PM USER: ROYSEJ

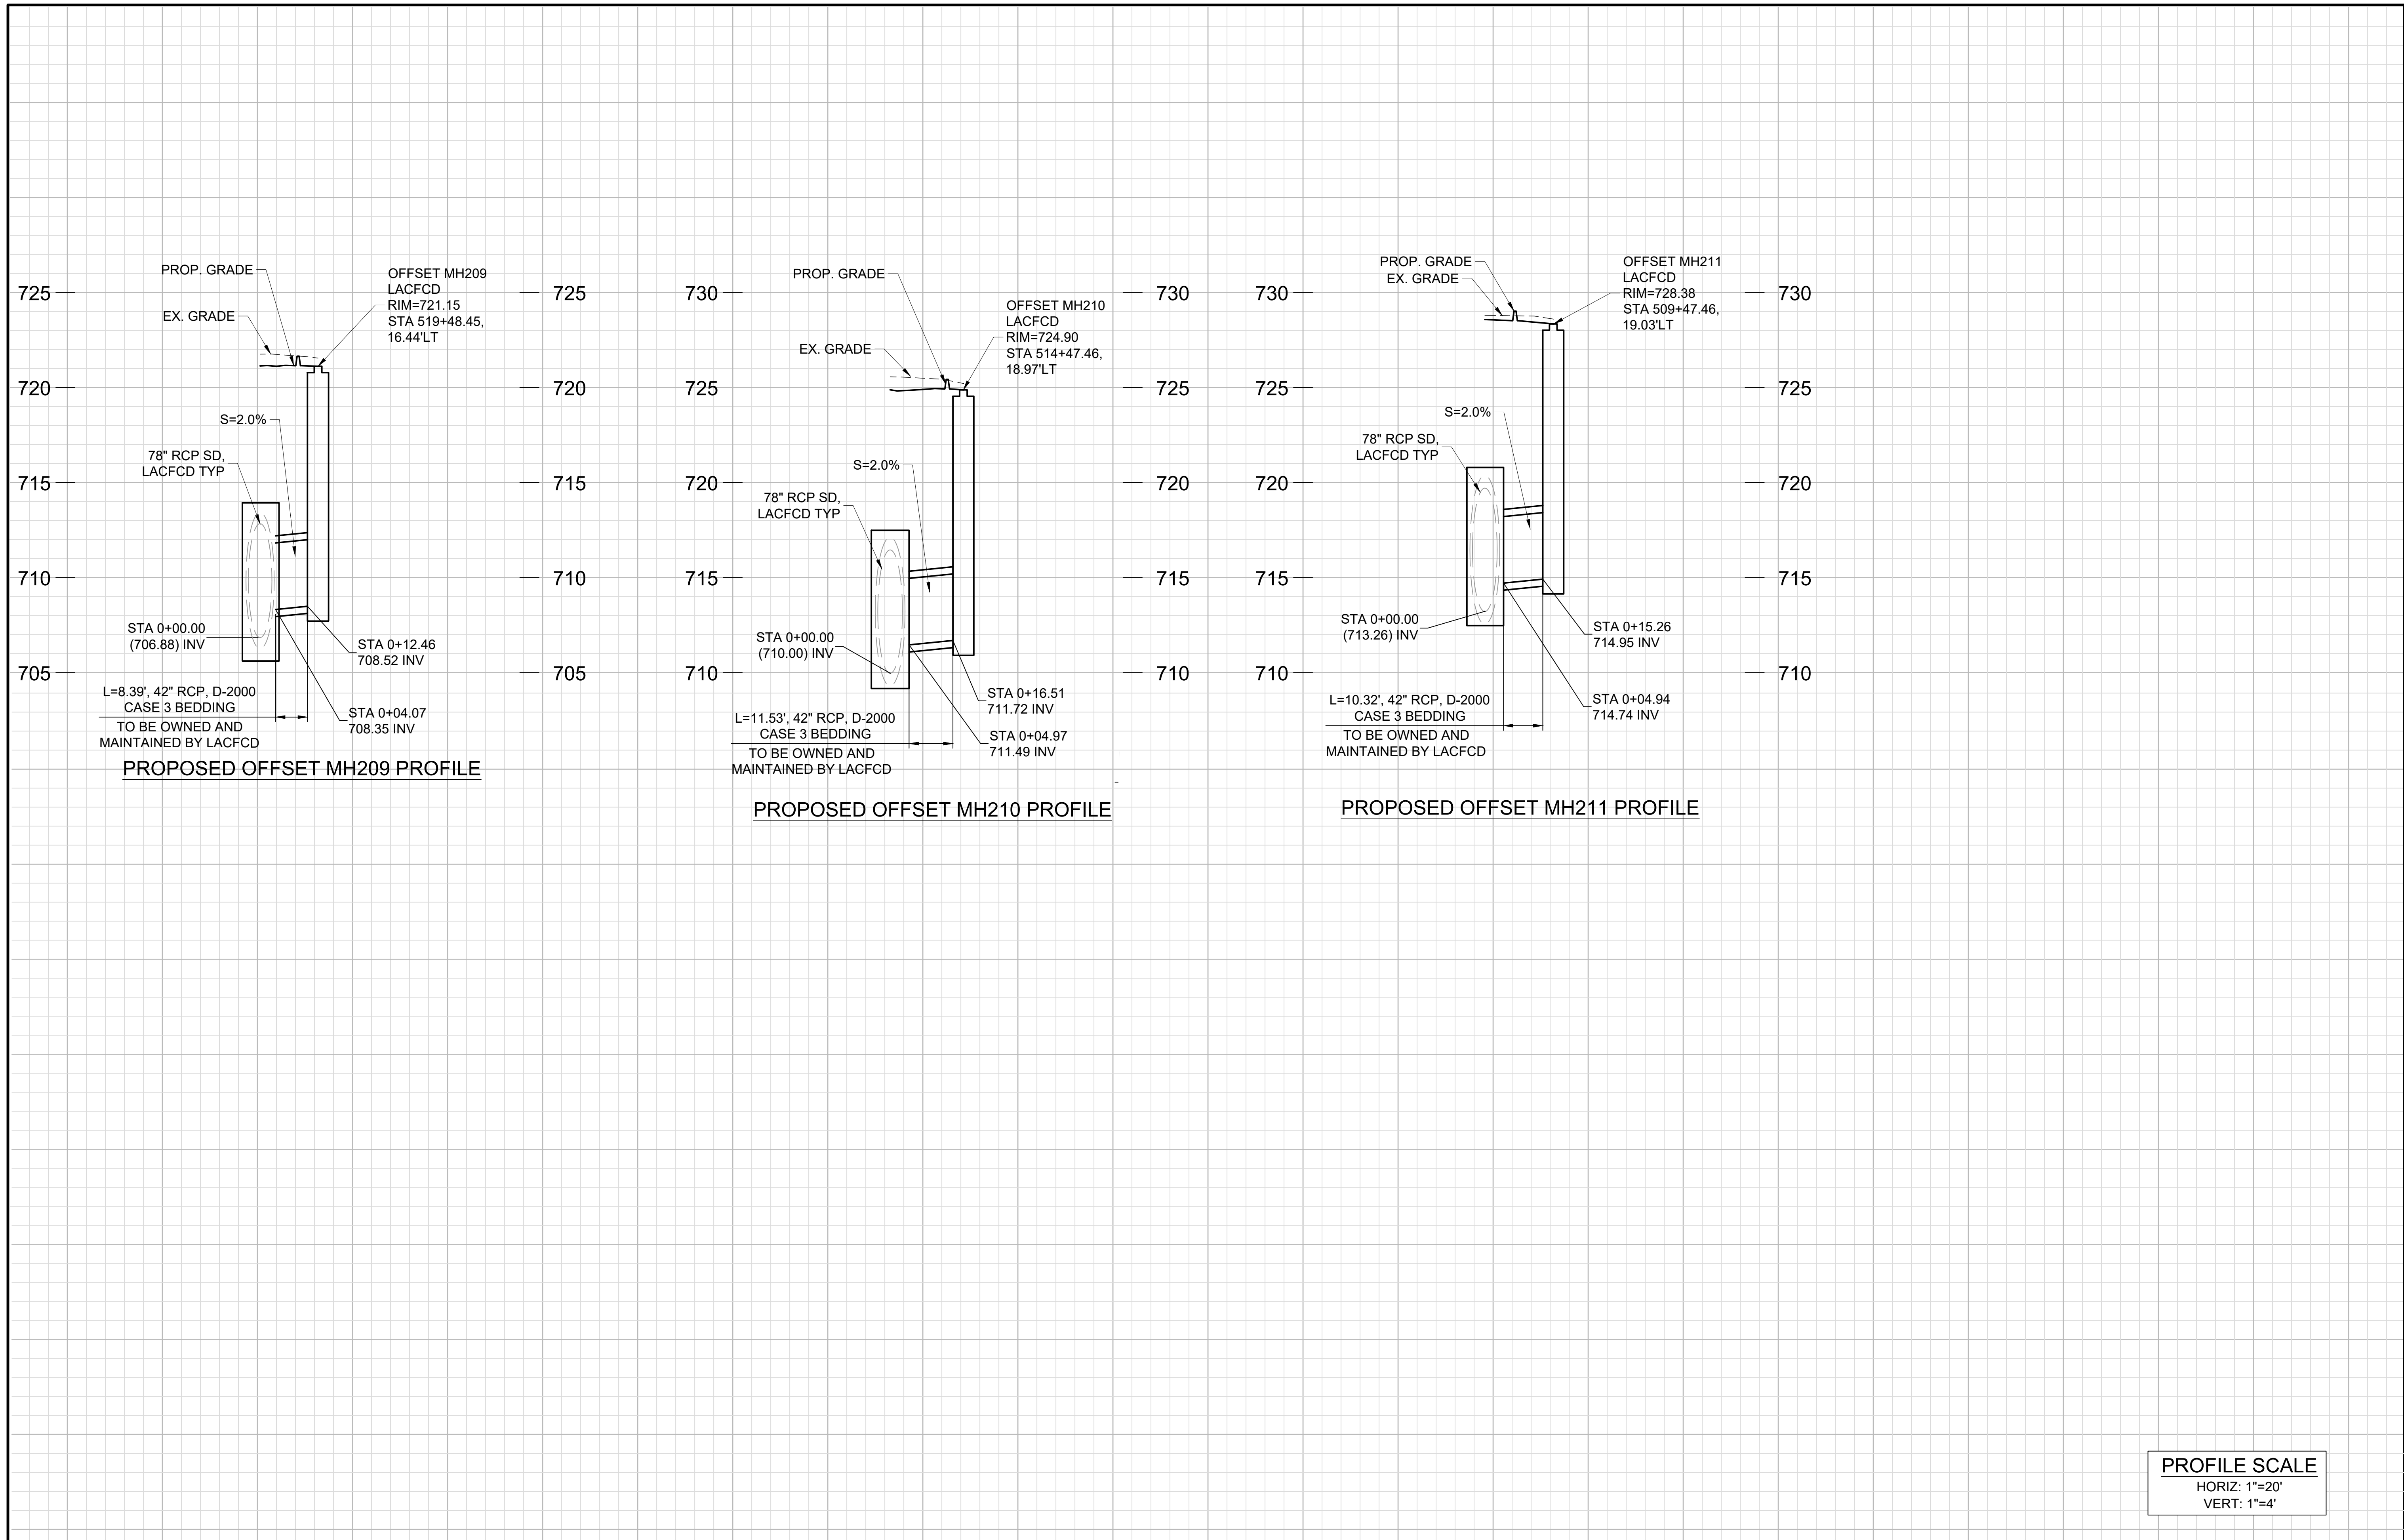

THE PREPARATION OF THIS DRAWING HAS BEEN FINANCED IN PART THROUGH A GRANT FROM THE U.S. DEPARTMENT OF TRANSPORTATION, FEDERAL TRANSIT ADMINISTRATION (FTA), UNDER THE FEDERAL TRANSIT ACT OF 1964, AS AMENDED, AND IN PART BY THE TAXES OF THE CITIZENS OF LOS ANGELES COUNTY AND OF THE STATE OF CALIFORNIA.								DESIGNED BY N. SOTO		A SIGNED & SEALED ORIGINAL OF REV 0 OF THIS DRAWING IS MAINTAINED BY METRO	LOS ANGELES COUNTY METROPOLITAN TRANSPORTATION AUTHORITY San Fernando Transit Constructors AECOM 14300 ARMINTA ST. LOS ANGELES, CA 91402 TEL: 951.684.5360 100% SUBMITTAL - NOT FOR CONSTRUCTION			EAST SAN FERNANDO VALLEY LRT DU06 - CIVIL SEGMENT A1 STORM DRAIN PLAN OFFSET MANHOLE PROFILES SHEET 2 OF 2		CONTRACT NO PS89616000	
								DRAWING NO UD-216								REV	
								SCALE AS SHOWN								SHEET NO	
C	12/15/25	NS	JR	C78082	09/30/27	J. RIMORIN	100% SUBMITTAL										
B	08/18/25	AR	NB	C65608	09/30/27	N.BUSCH	85% SUBMITTAL										
A	03/07/25	KM	JR	C78082	09/30/27	J. RIMORIN	60% SUBMITTAL										
REV	DATE	BY	APP	REG NO	EXPIRES	SEAL HOLDER	DESCRIPTION	DATE 12/15/2025									

FILE PATH: \\S072457-ESFV-PH2\PROJECT FILES\900_CAD\20_SHEETS\DU06\09_UD_DRAINAGE\PS89616000-DU06-UD-216-PR.DWG
PLOT DATE: 12/16/2025 - 12:20 PM USER: ROYSEJ

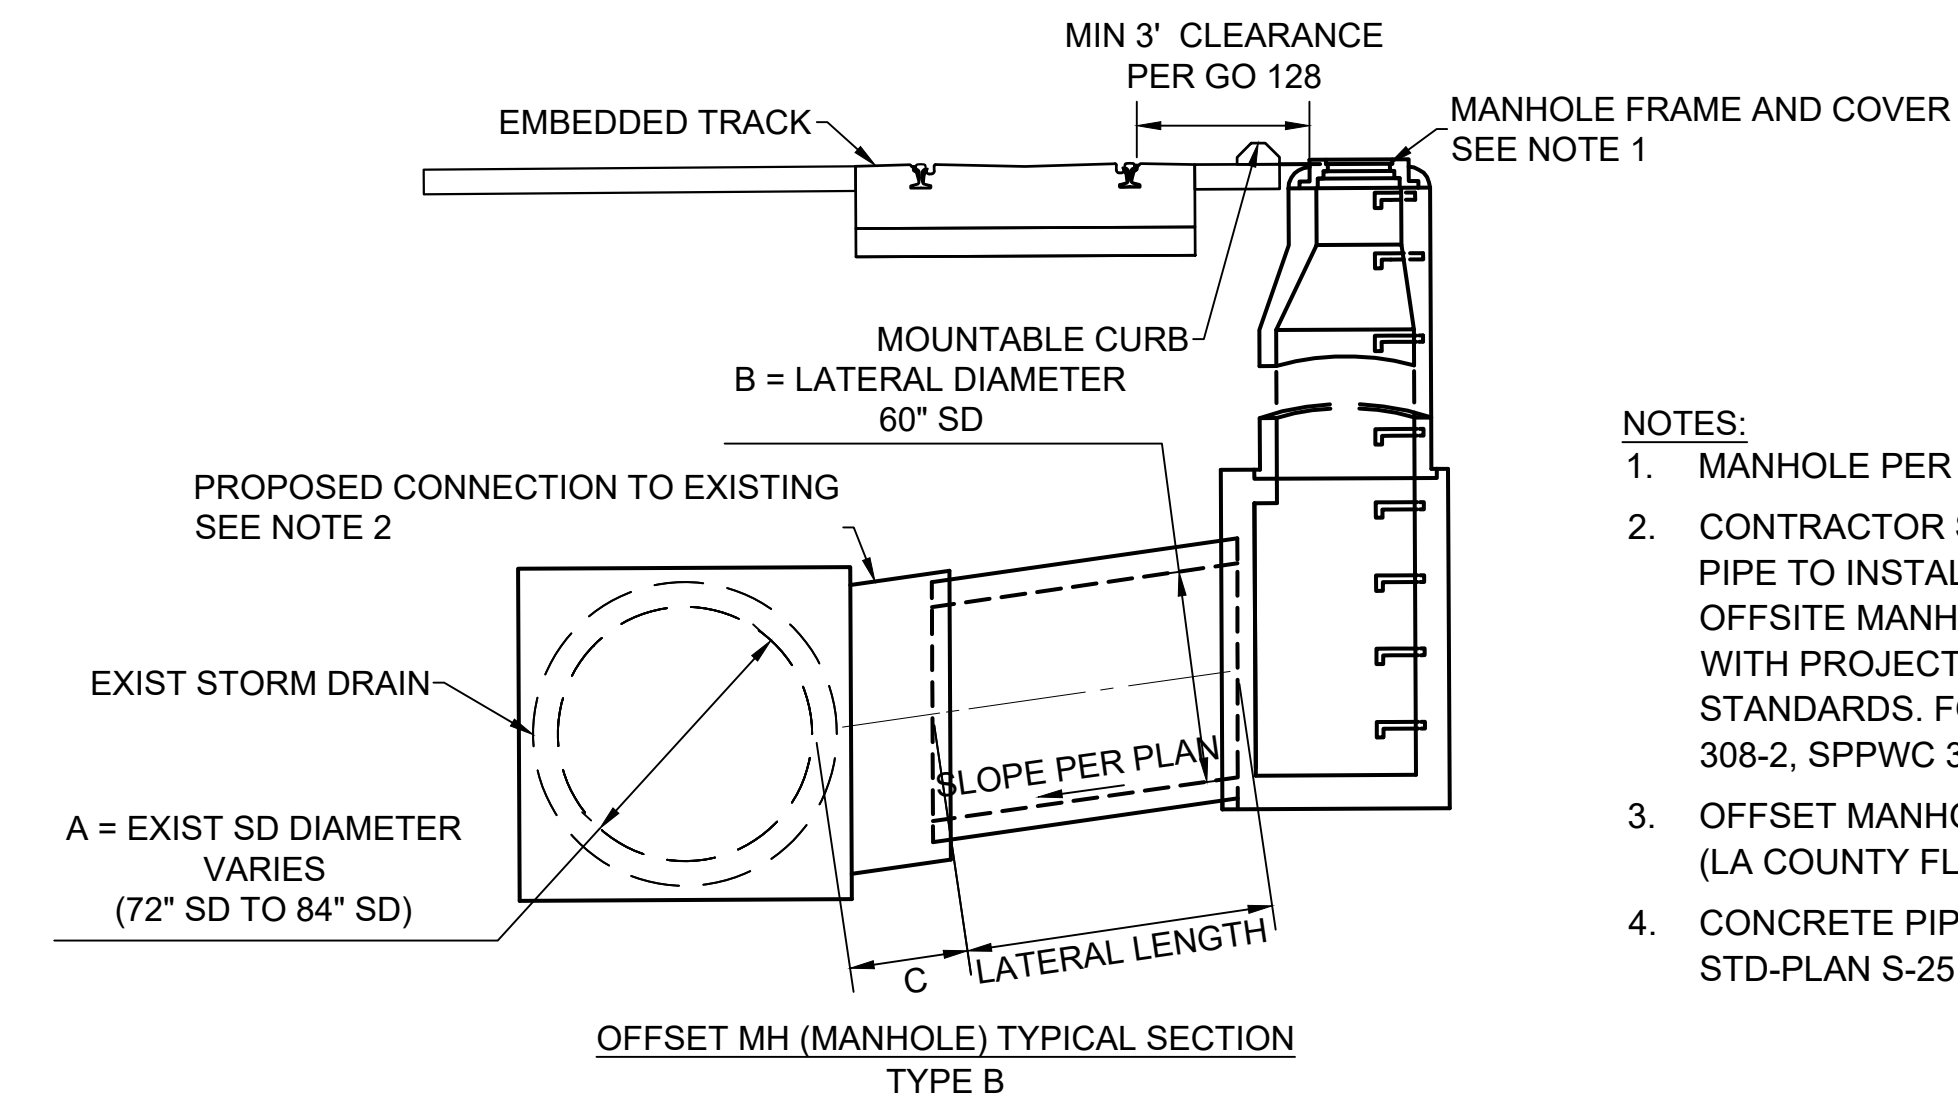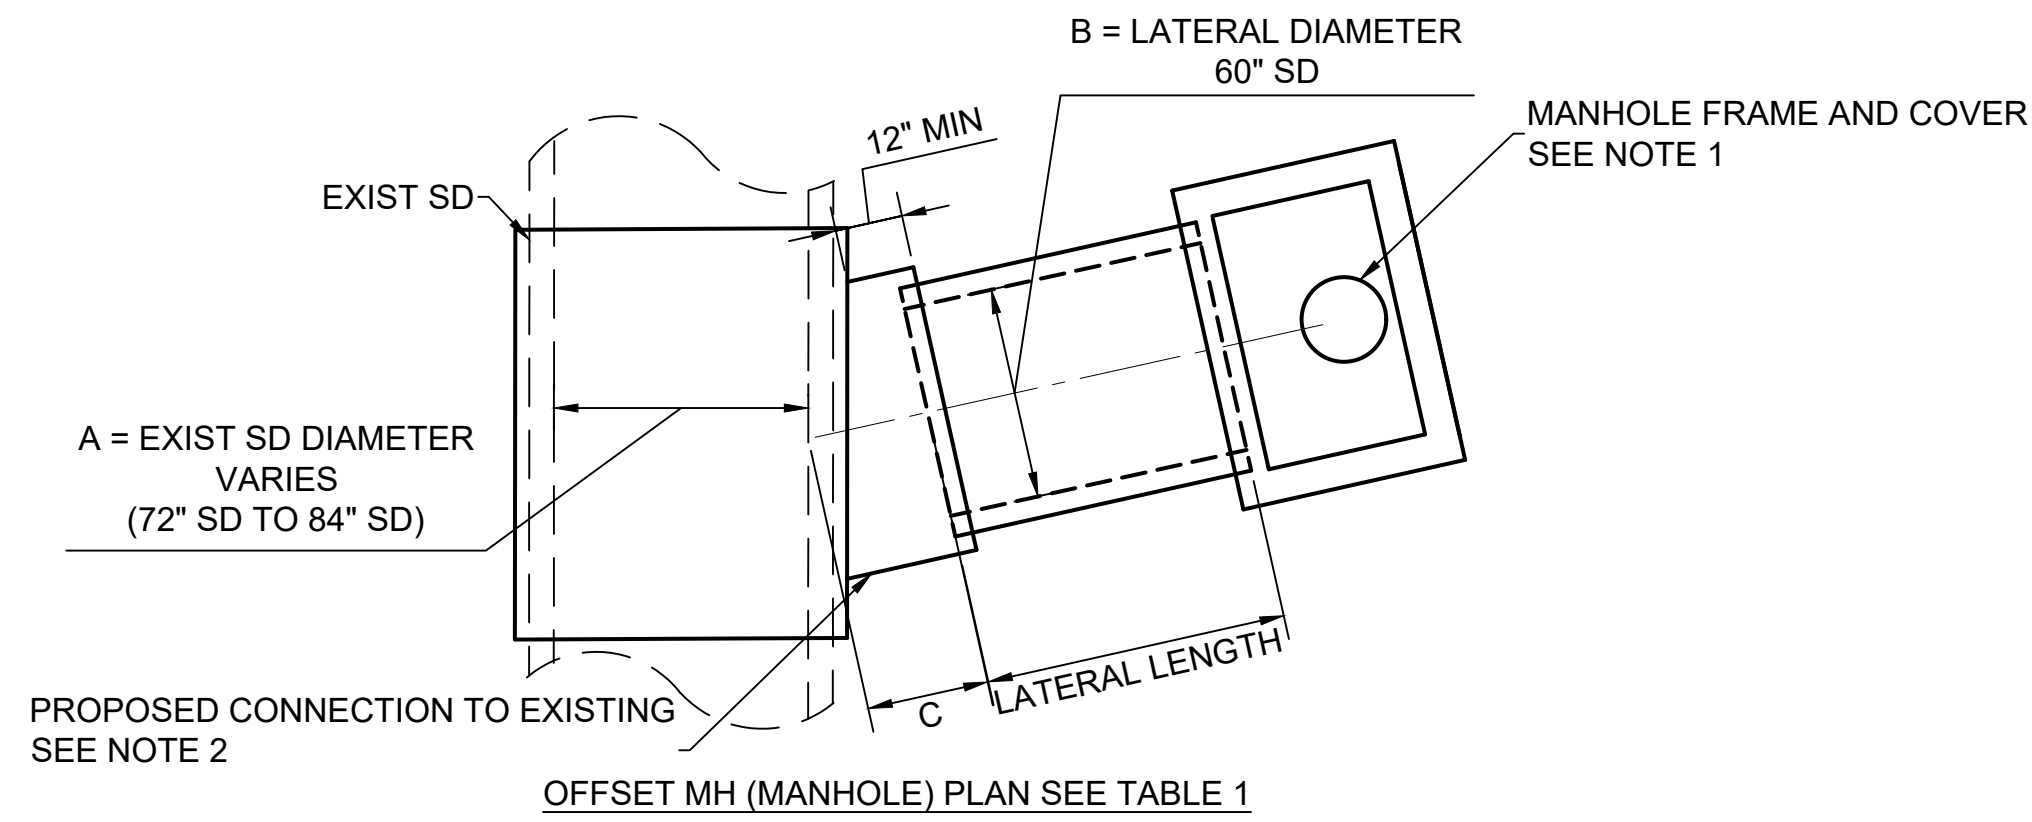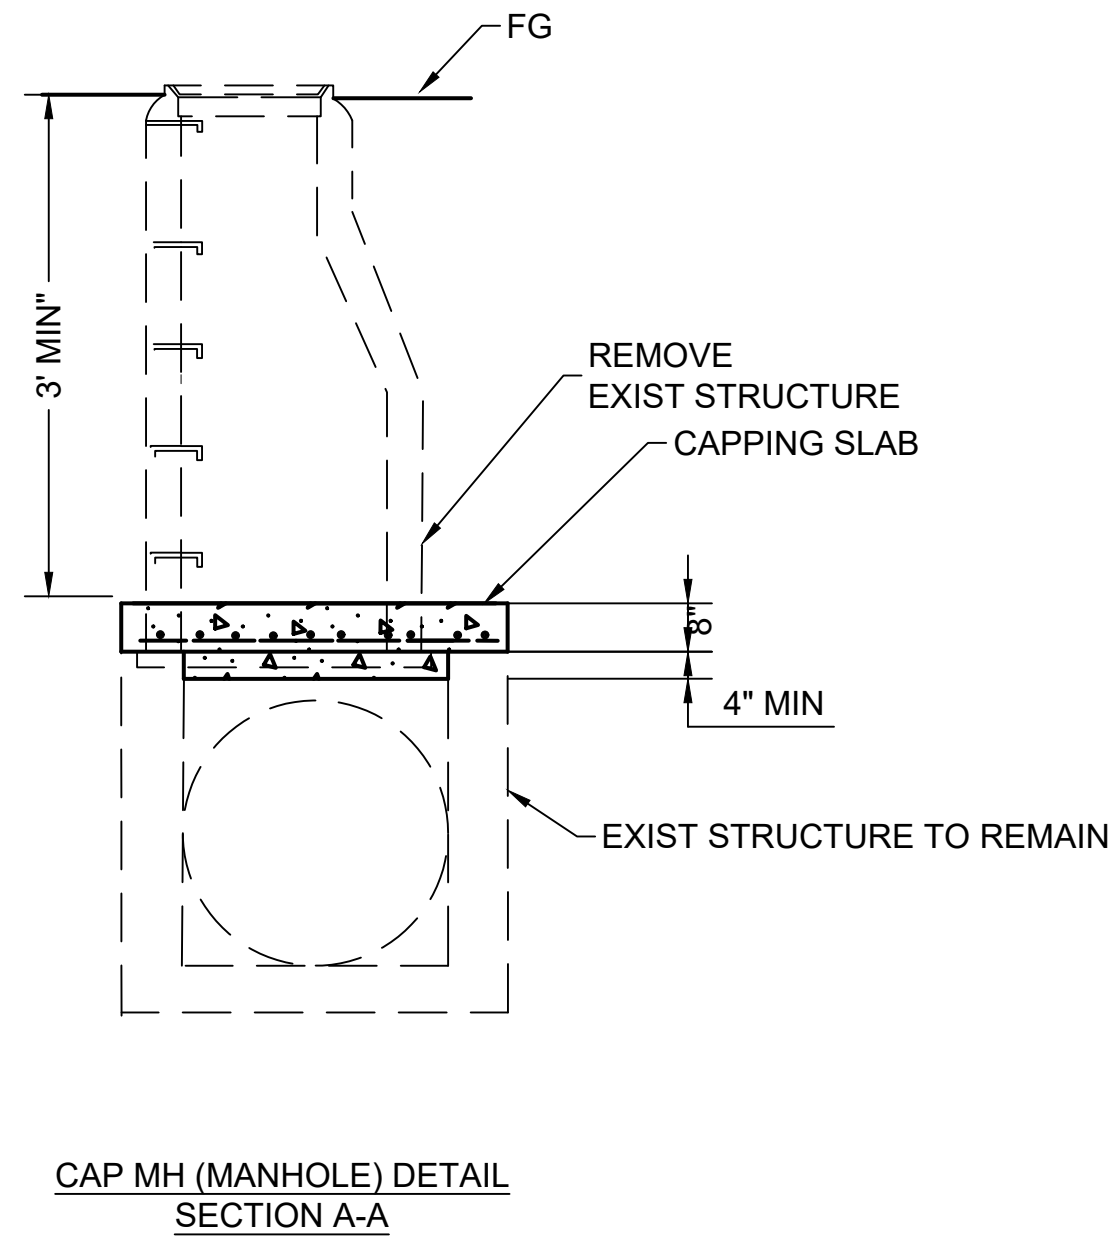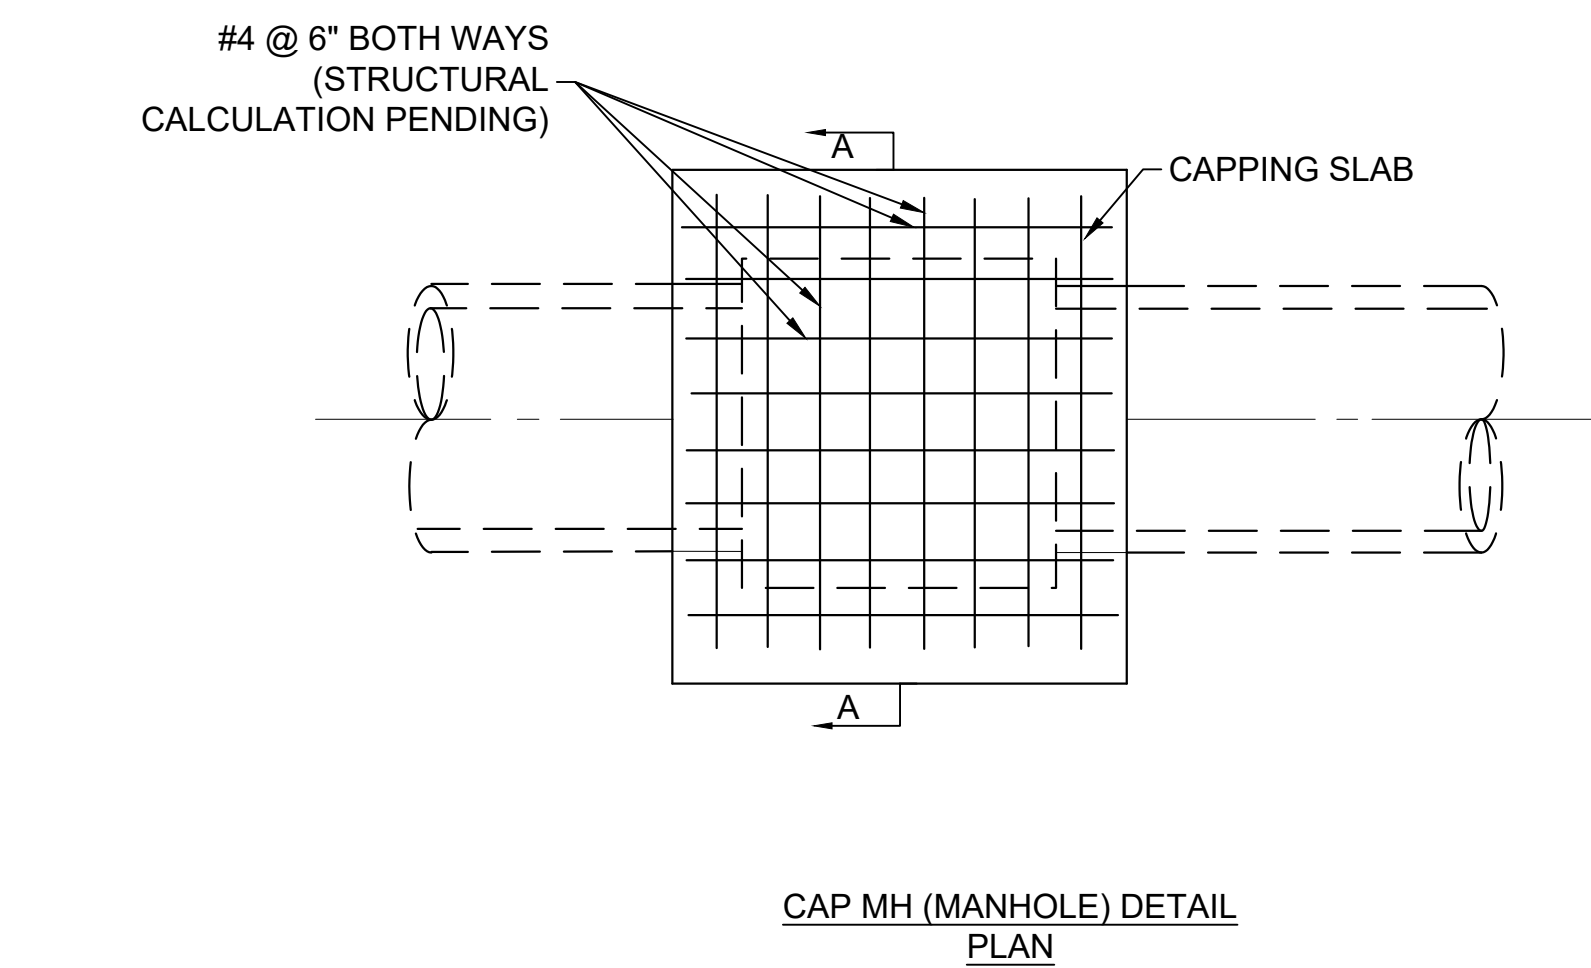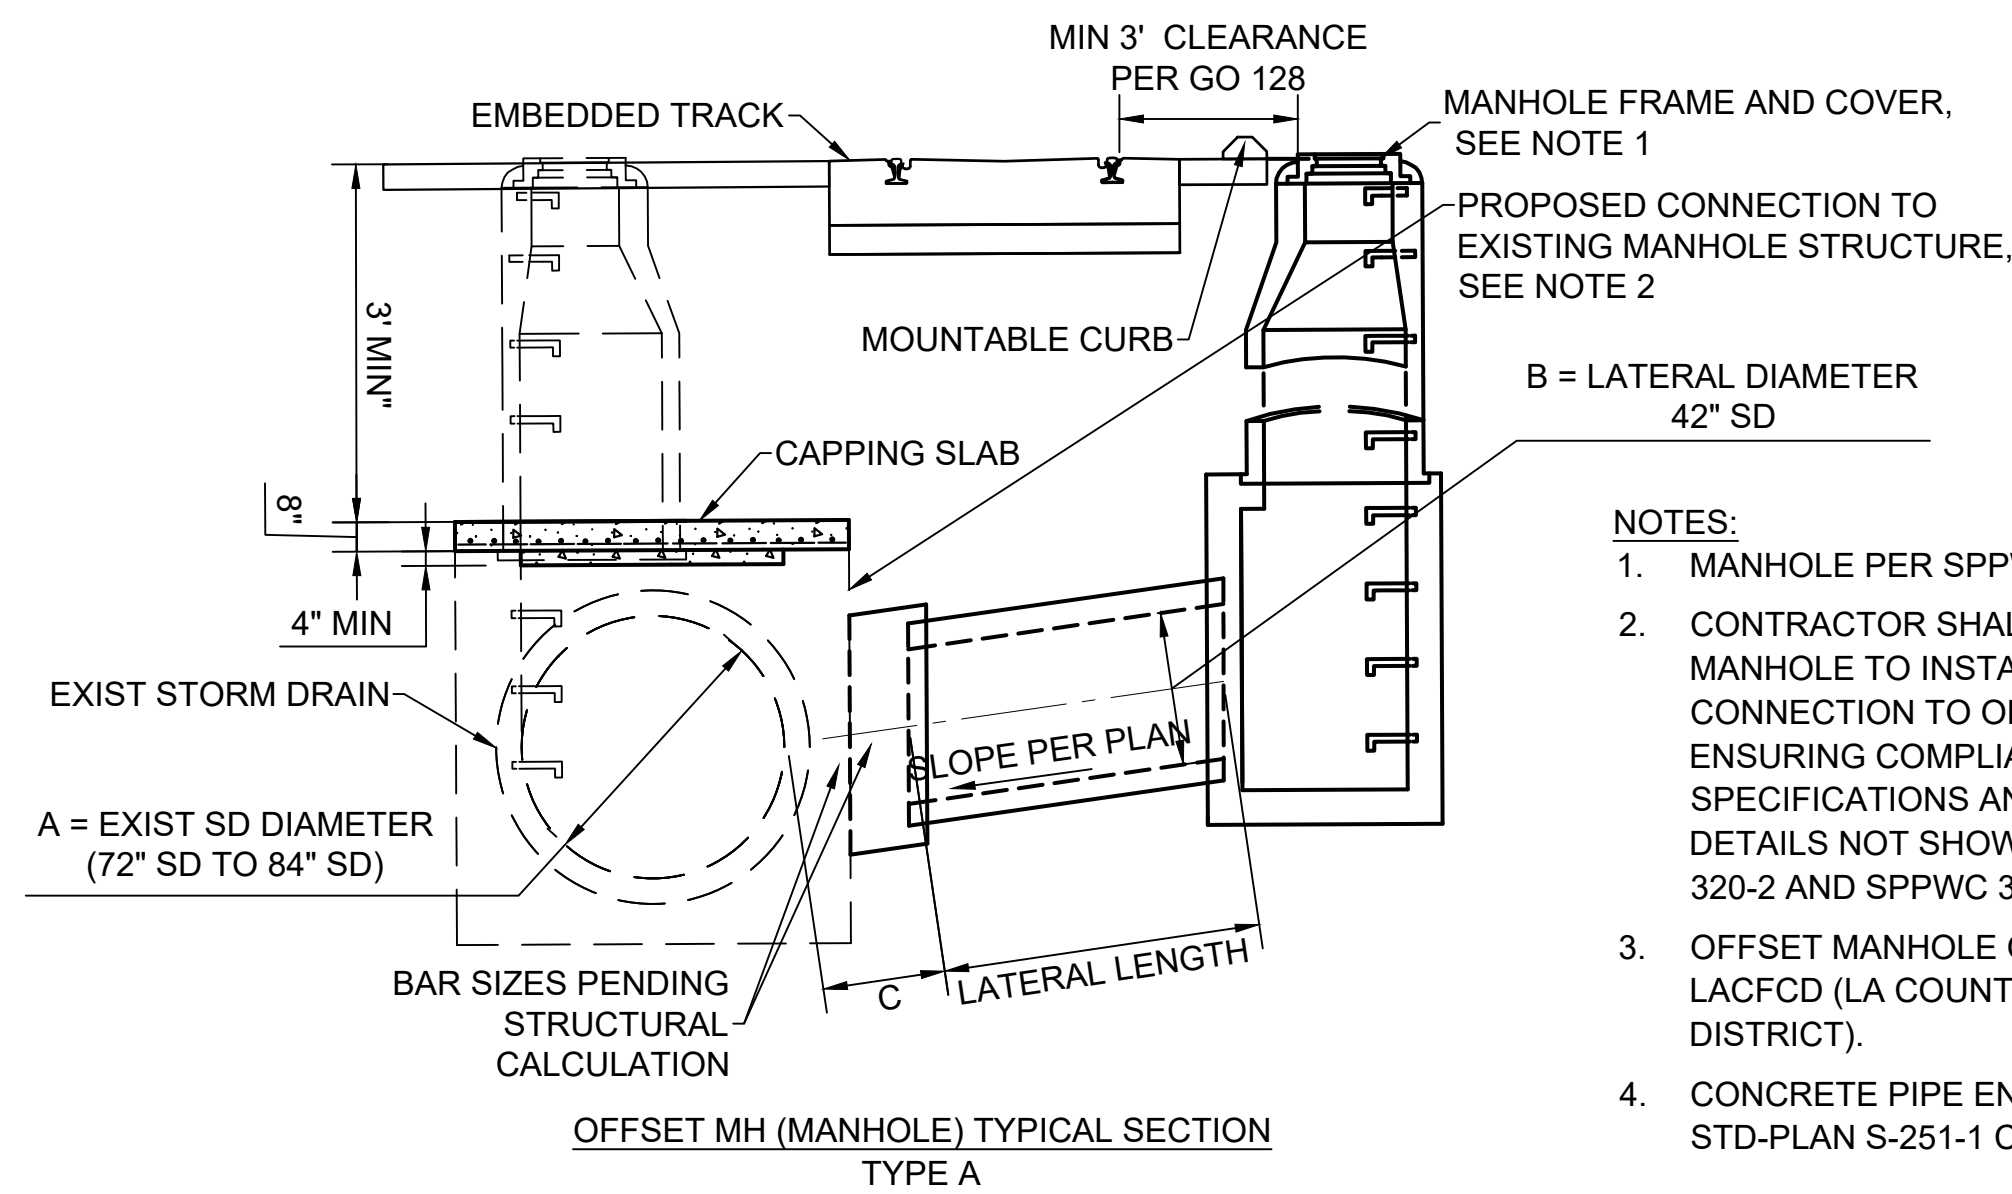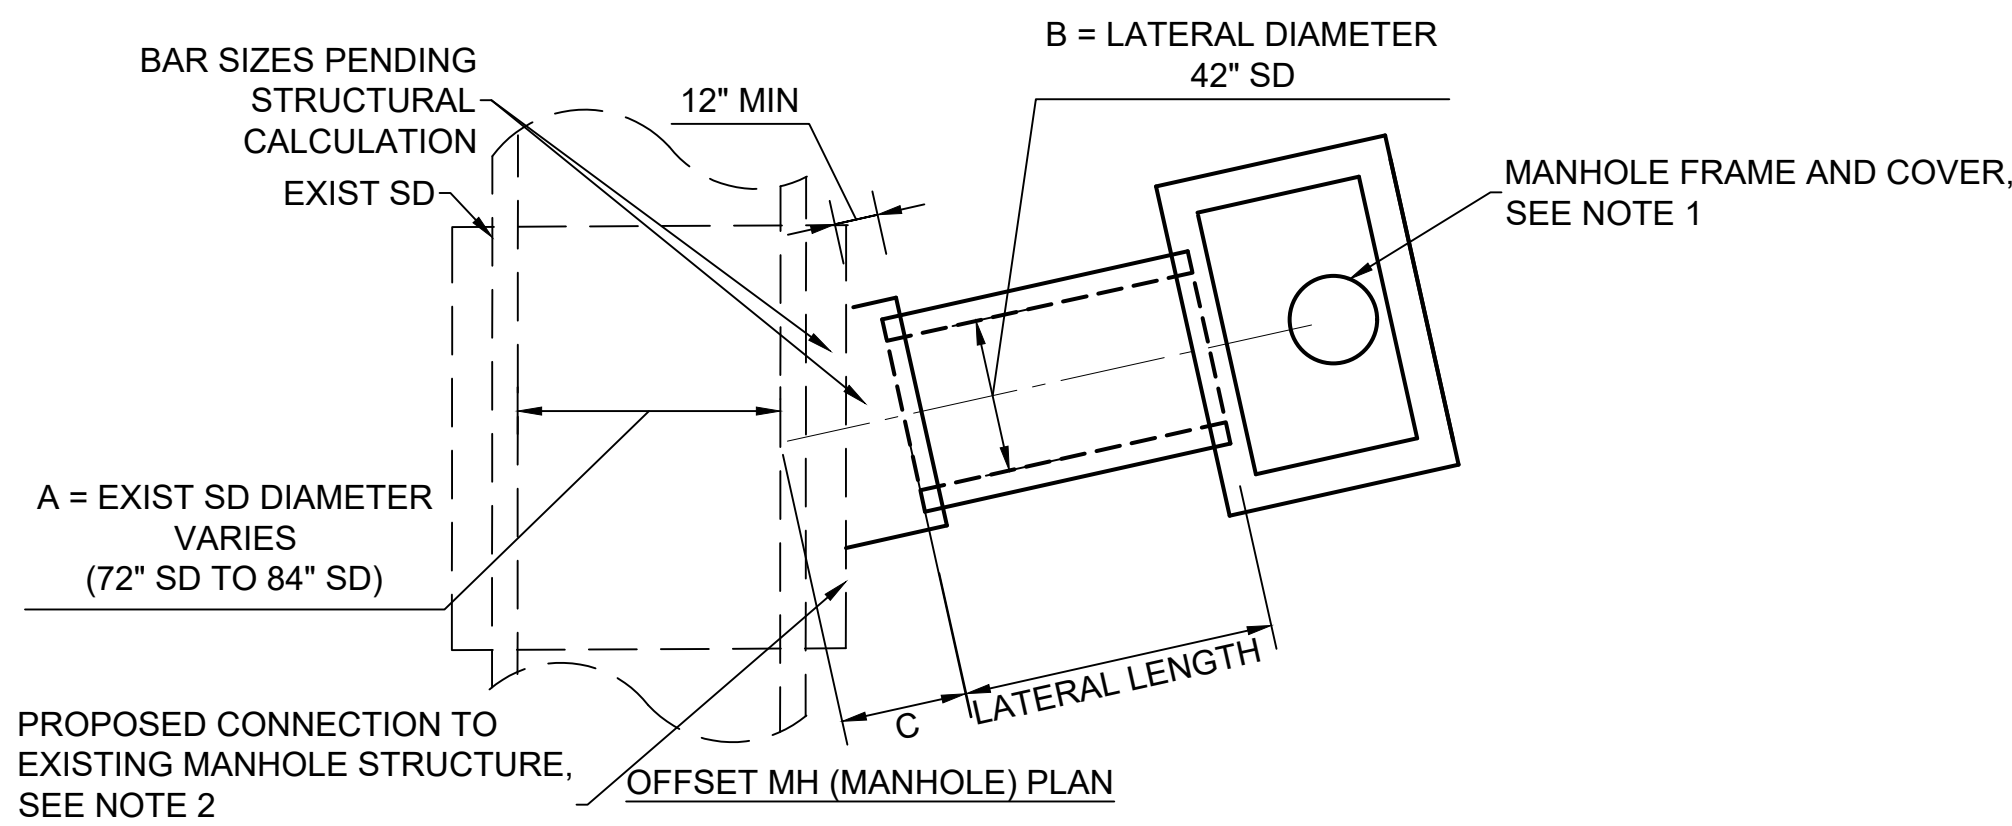

- NOTES:
1. MANHOLE PER SPPWC 320-2.
 2. CONTRACTOR SHALL MODIFY EXISTING STORM DRAIN PIPE TO INSTALL NEW LATERAL CONNECTION TO OFFSITE MANHOLE AS SHOWN, ENSURING COMPLIANCE WITH PROJECT SPECIFICATIONS AND SPPWC STANDARDS. FOR DETAILS NOW SHOWN SEE SPPWC 308-2, SPPWC 320-2 AND SPPWC 340-2.
 3. OFFSET MANHOLE OWNED AND MAINTAINED BY LACFCD (LA COUNTY FLOOD CONTROL DISTRICT).
 4. CONCRETE PIPE ENCASEMENT PER CITY OF LA STD-PLAN S-251-1 CASE 5 BEDDING.

THE PREPARATION OF THIS DRAWING HAS BEEN FINANCED IN PART THROUGH A GRANT FROM THE U.S. DEPARTMENT OF TRANSPORTATION, FEDERAL TRANSIT ADMINISTRATION (FTA), UNDER THE FEDERAL TRANSIT ACT OF 1964, AS AMENDED, AND IN PART BY THE TAXES OF THE CITIZENS OF LOS ANGELES COUNTY AND OF THE STATE OF CALIFORNIA.								DESIGNED BY N. SOTO			A SIGNED & SEALED ORIGINAL OF REV 0 OF THIS DRAWING IS MAINTAINED BY METRO	M Metro LOS ANGELES COUNTY METROPOLITAN TRANSPORTATION AUTHORITY				EAST SAN FERNANDO VALLEY LRT DU06 - CIVIL SEGMENT A1				CONTRACT NO PS89616000	
								DRAWN BY R. VENEGAS				DRAWING NO UD-201-D		REV							
								CHECKED BY N. BUSCH				SCALE NO SCALE		SHEET NO							
								IN CHARGE N. BUSCH													
								DATE 12/15/2025													
C	12/15/25	NS	JR	C78082	09/30/27	J. RIMORIN	100% SUBMITTAL	SFTC San Fernando Transit Constructors 14300 ARMINTA ST. LOS ANGELES, CA 91402 TEL: 951.684.5360 V&A V&A INC 1111 S. GRAND AVE. SUITE 103 LOS ANGELES, CA 90015 213.937.2700				100% SUBMITTAL - NOT FOR CONSTRUCTION									
B	08/18/25	AR	NB	C65608	09/30/27	N. BUSCH	85% SUBMITTAL														
A	03/07/25	KM	JR	C78082	09/30/27	J. RIMORIN	60% SUBMITTAL														
REV	DATE	BY	APP	REG NO	EXPIRES	SEAL HOLDER	DESCRIPTION														

FILE PATH: \\S072457-ESFV-PH2\PROJECT FILES\900_CAD\20_SHEETS\DU06\09_UD_DRAINAGE\PS89616000-DU06-UD-201-D.DWG
PLOT DATE: 12/16/2025 - 4:33 PM USER: ROYSEJ