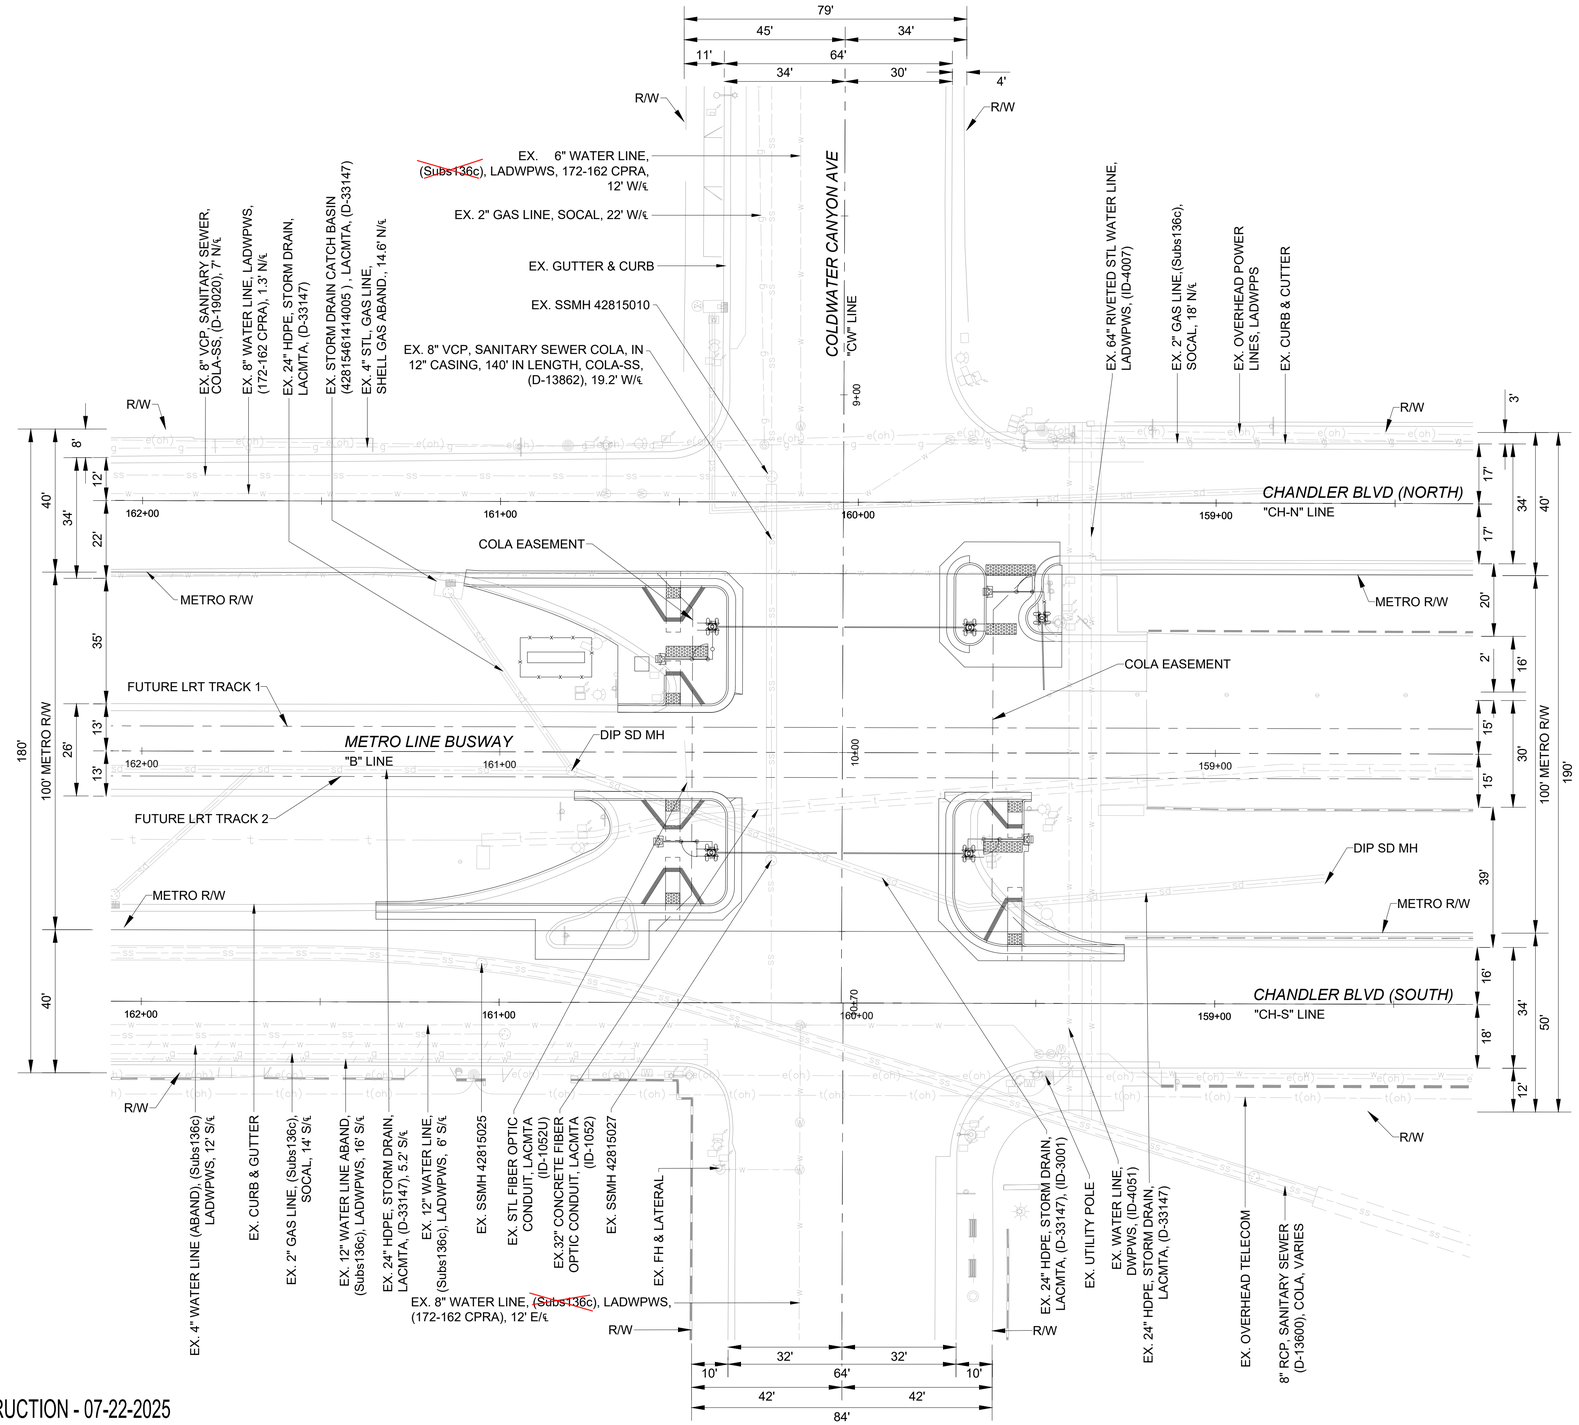

PROGRESS SET - NOT FOR CONSTRUCTION - 07-22-2025

REV	DATE	BY	APP	REG NO	EXPIRES	SEAL HOLDER	DESCRIPTION

REVISION DATES (DESIGN STAGE ONLY)

DESIGNED BY N. HURTADO
DRAWN BY N. NGUYEN
CHECKED BY N. YADAV
IN CHARGE N. YADAV
DATE 07/22/2025

FOR INFORMATION ONLY NOT FOR CONSTRUCTION

Metro
LOS ANGELES COUNTY METROPOLITAN TRANSPORTATION AUTHORITY
VALLEY TRANSIT PARTNERS
V&A INC 1111 S. GRAND AVE, SUITE 103 LOS ANGELES, CA 90015 213.972.9700
PROGRESS SET
FOR INFORMATION ONLY NOT FOR CONSTRUCTION

METRO G LINE BRT
GATED INTERSECTIONS DESIGN
UTILITY COMPOSITE PLAN
COLDWATER CANYON AVE & CHANDLER BLVD

CONTRACT NO PS85661000
DRAWING NO UC-006 REV
SCALE 1" = 20'
SHEET NO X OF XX

DRAWING NO. UC-006
SHEET X OF XX SHEETS

CITY OF LOS ANGELES DEPARTMENT OF PUBLIC WORKS BUREAU OF ENGINEERING

ENGINEERING
CITY OF LOS ANGELES

NO.	REVISIONS:	DATE	BY:
0			

WORK ACCEPTED
SERIAL NO.

B - PERMITS

INDEX NO.

BUREAU OF ENGINEERING APPROVAL:
SIGNATURE: DATE:

V&A, INC.
DESIGN GROUP
ENGINEER: N. HURTADO
DESIGNED BY: N. HURTADO
DRAWN BY: K. KGUYEN
CHECKED BY: N. YADAV
APPROVED BY: N. YADAV

VERTICAL CONTROL: BM # 07-00420, ELEVATION 711.051' NAVD88 2000 ADJ.
HORIZONTAL CONTROL: SEE PLAN SHEETS FOR CONTROL LINE REFERENCE

SHEET TITLE: UTILITY COMPOSITE PLAN
PROJECT: COLDWATER CANYON AVE & CHANDLER BLVD METRO G LINE BRT GATED INTERSECTIONS DESIGN
ADDRESS: COLDWATER CANYON BLVD LOS ANGELES, CA.

C:\Users\michaelbullock\DCACCDocs\V&A Inc\G-Line\Project Files\900_CAD\20_SHEETS\01_DU06-01_CIVIL\05_UTILITIES

Monday, August 04, 2025 10:32:01 AM

THE CITY OF LOS ANGELES OR ITS OFFICERS OR AGENTS SHALL NOT BE RESPONSIBLE FOR THE ACCURACY OR COMPLETENESS OF ELECTRONIC COPIES OF THIS PLAN SHEET.

Sheet Version 6.0 2-2015