


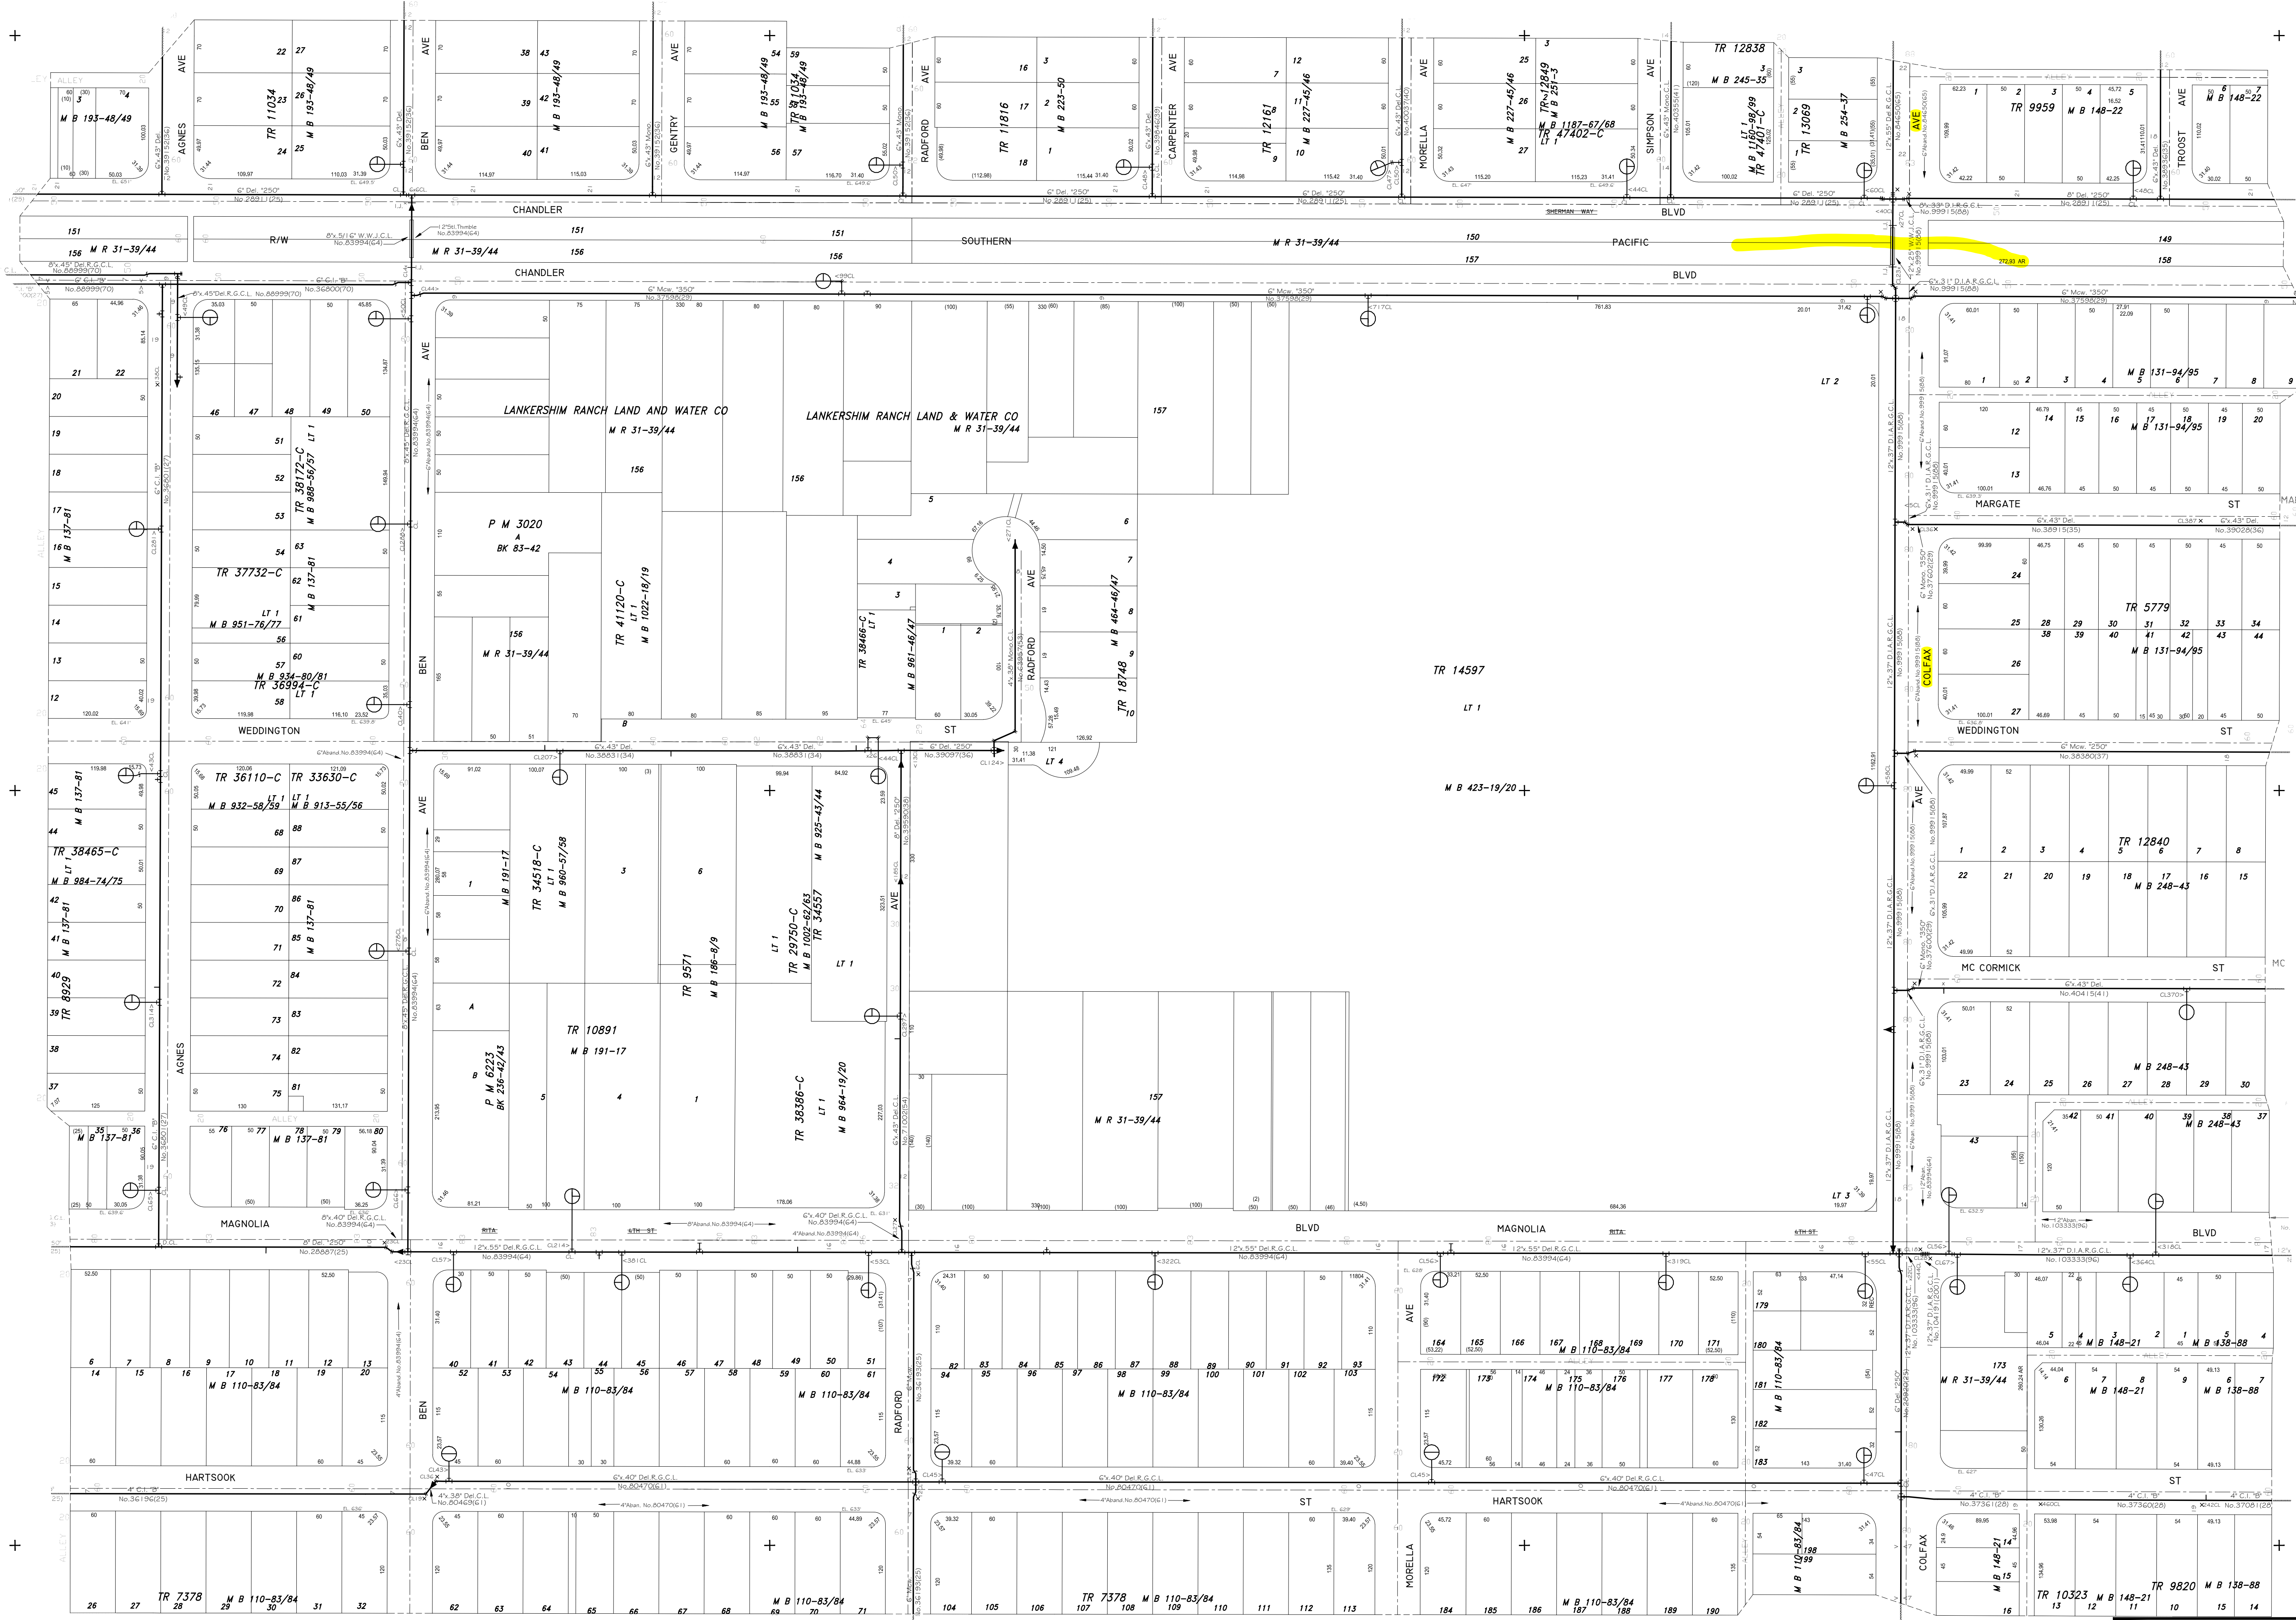

E.6.441.662

The Los Angeles Department of Water and Power (LADWP) assumes no responsibility for the accuracy of the substructure information herein provided. The user assumes responsibility for verifying substructure locations before excavation and assumes all liabilities for damage to LADWP facilities as a result of such excavation. Call Underground Service alert on 1-800-227-2600 two (2) days before excavating.

LEGEND MAP SCALE 1" = 1500'		SYMBOLS AND NOTATIONS		SCALE: 1" = 100'		PLOTTED	DATE	CHKD.	DATE	FIRE HYDRANTS		REFERENCES	
AS SHOWN		MAP		NAME		NAME	DATE	NAME	DATE	2 1/2" SINGLE		MAPS REPLACED	
		CONVERTED MAINS		T.CHEN		2105 NS, 2106 NS		2 1/2" S. BUILT UP		DATE BK.		170-168, 175-168	
		CONVERTED SERVICES		D.LEE		2120 NS, 2119 NS		2 1/2" DOUBLE		LANDBASE:		171B165, 171B169	
		MISC		NAME		NAME	DATE	4" SINGLE		SERVICE ZONE ELEVATION		DISTRICT: EAST VALLEY	
								4" S. BUILT UP		1700		172-168	
								4" DOUBLE		DATUM		NAD 1983 ZONE V	
								2 1/2" x 4" DOUBLE		LEVELS: U.S.G.S.			
				</									