


MATCH LINE SEE DWG U-063

MATCH LINE SEE DWG U-065

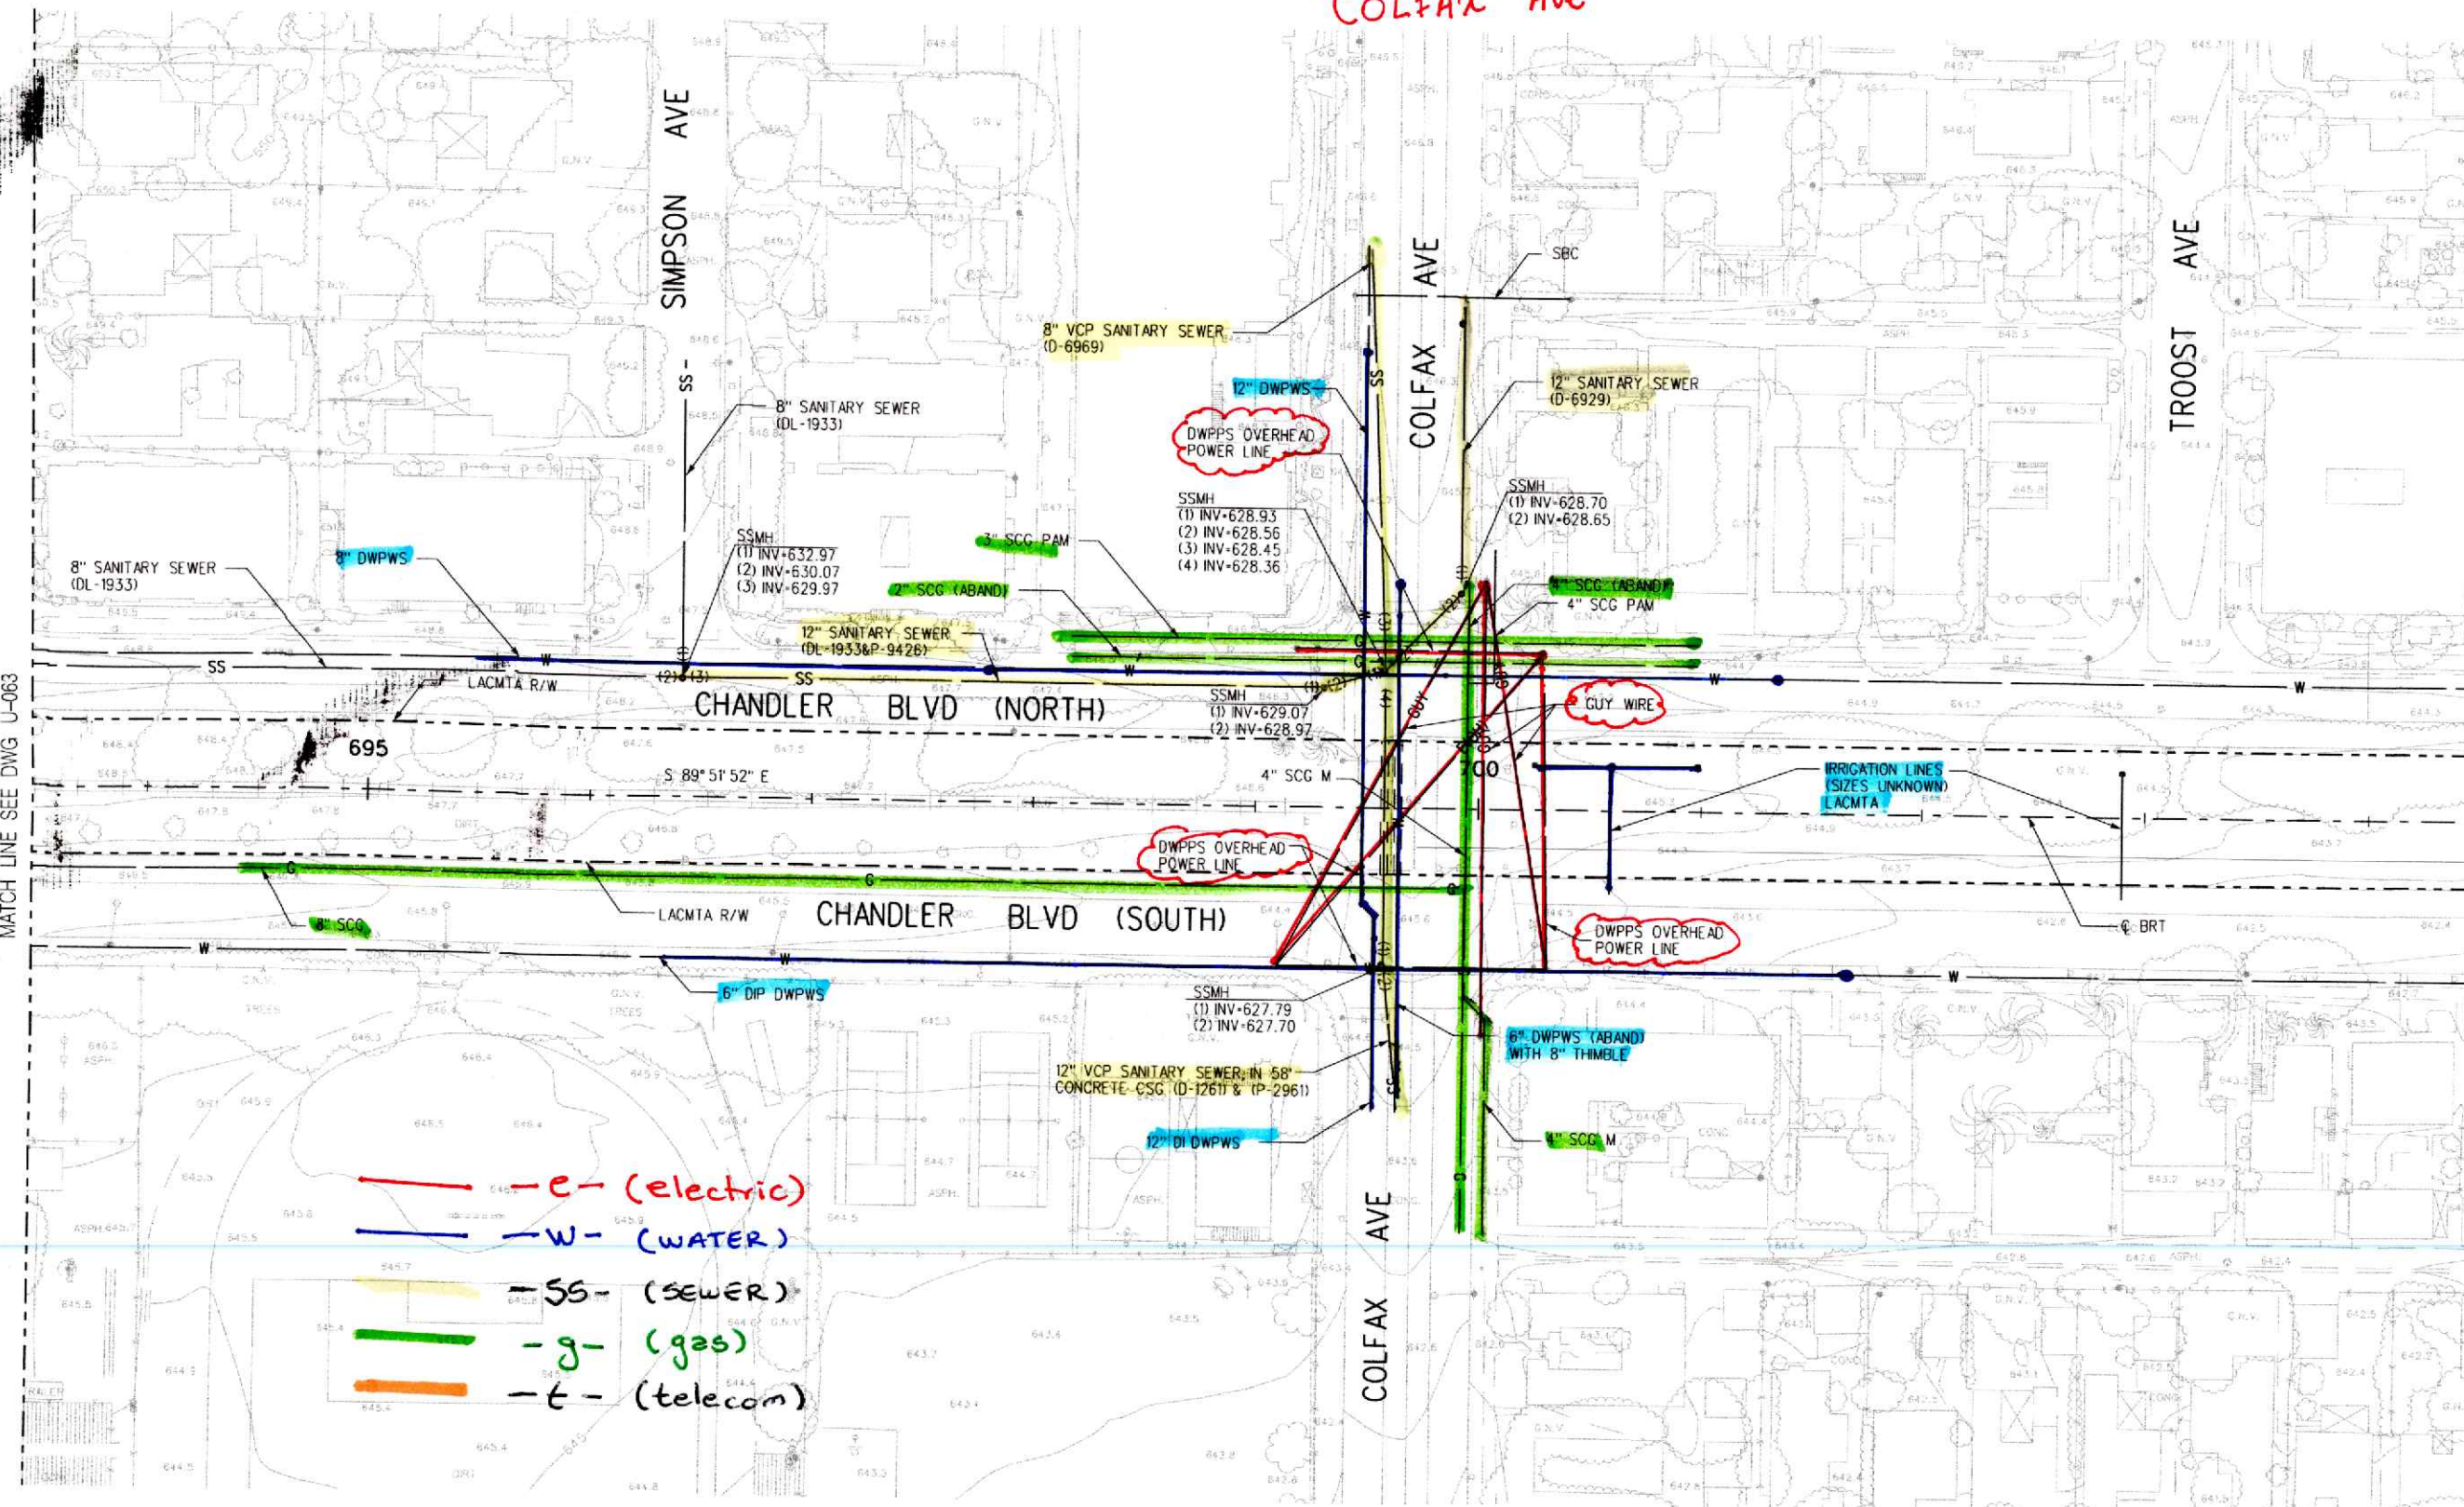


-e- (electric)
 -w- (water)
 -ss- (sewer)
 -g- (gas)
 -t- (telecom)



REV	DATE	BY	APP	REG NO	EXPIRES	SEAL HOLDER	DESCRIPTION
D	11/7/03	YX	BEJ	C59517	12/31/03	BRETT E. JONES	ISSUED FOR CONSTRUCTION

DESIGNED BY
S. KASSISIEH
 DRAWN BY
M. CUTTER
 CHECKED BY
S. YOUSEFIAN
 IN CHARGE
B. JONES
 DATE
11/07/03

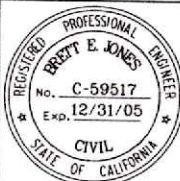

LOS ANGELES COUNTY METROPOLITAN TRANSPORTATION AUTHORITY
SAN FERNANDO VALLEY EAST-WEST BRT PROJECT

WASHINGTON GROUP INTERNATIONAL, INC.
5805 SEPULVEDA BLVD., SUITE 500
VAN NUYS, CA 91411

SHIMMICK
OBAYASHI, JV
5805 SEPULVEDA BLVD., SUITE 500
VAN NUYS, CA 91411

NORTH HOLLYWOOD TO
WARNER CENTER
 UTILITIES
 SHEET 61 OF 65

CONTRACT NO	C0675
DRAWING NO	U-064
SCALE	HORIZ. 1"=40'
SHEET NO	0