


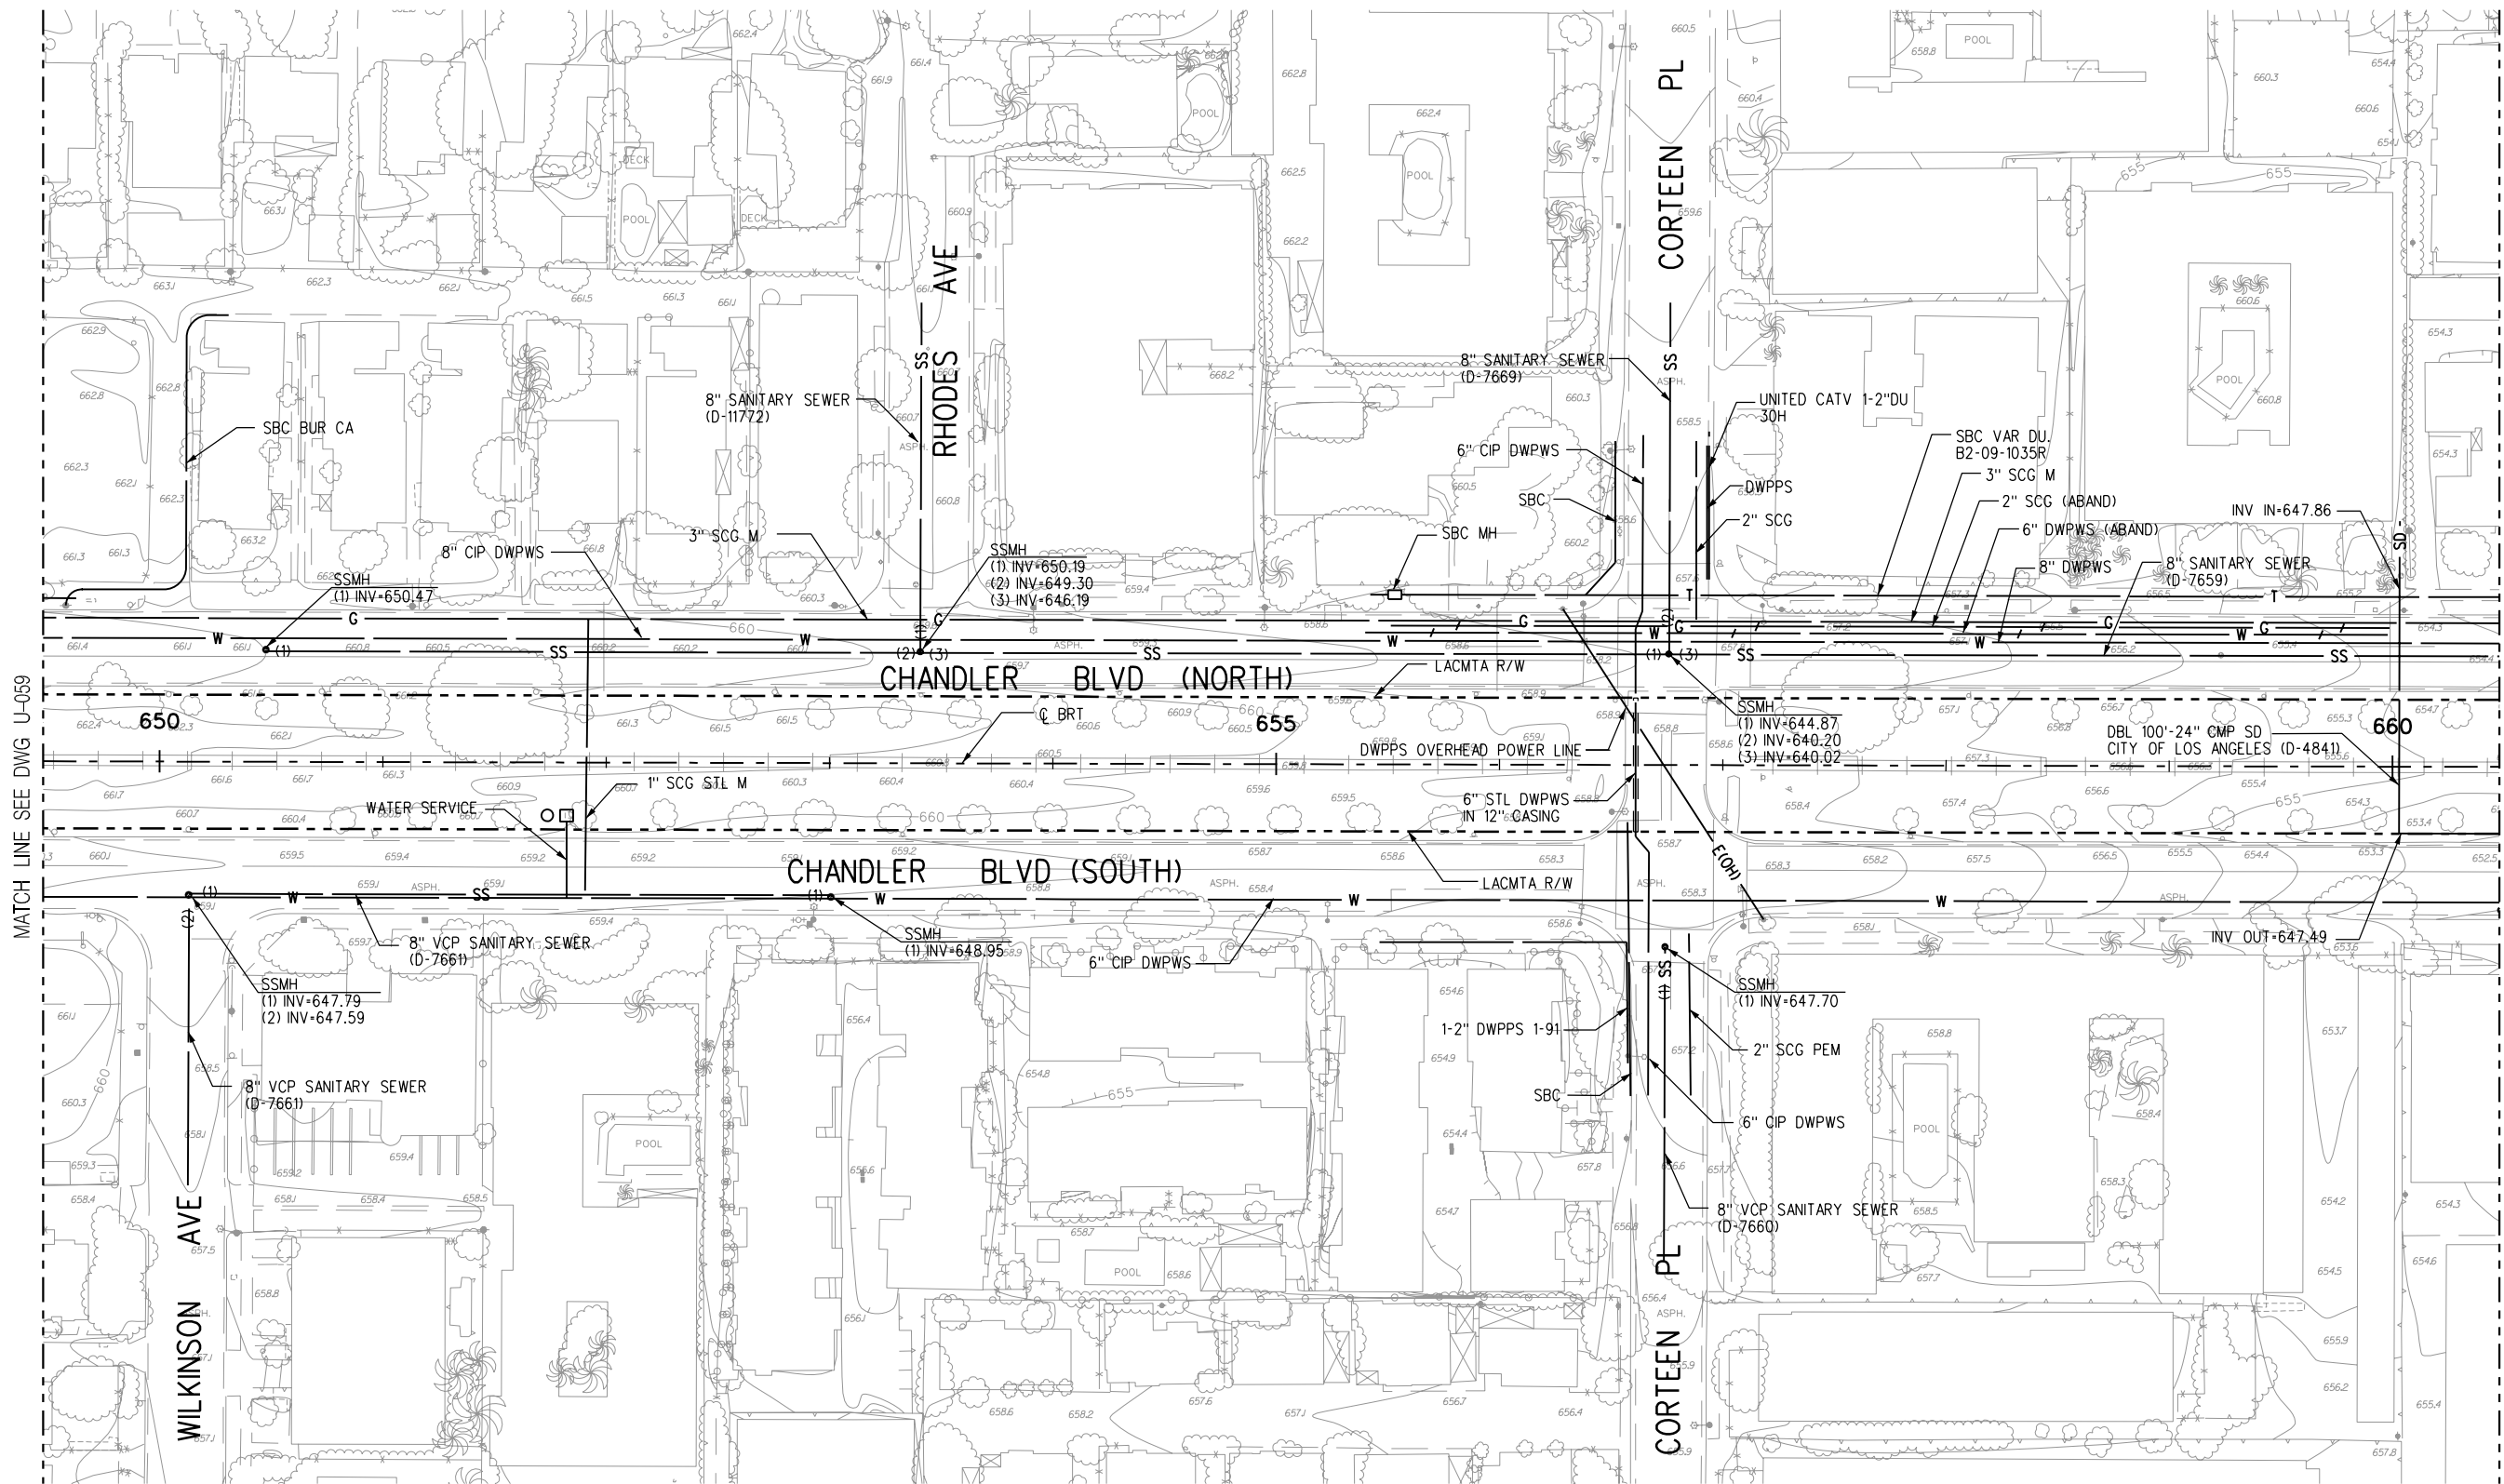


MATCH LINE SEE DWG U-059

MATCH LINE SEE DWG U-061



0	11/7/03	YX	BEJ	C59517	12/31/03	BRETT E. JONES	ISSUED FOR CONSTRUCTION
REV	DATE	BY	APP	REG NO	EXPIRES	SEAL HOLDER	DESCRIPTION

DESIGNED BY
S. KASSISIEH
DRAWN BY
M. CUTTER
CHECKED BY
S. YOUSEFIAN
IN CHARGE
B. JONES
DATE
11/07/03

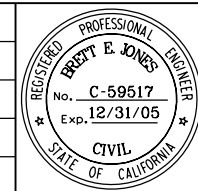

LOS ANGELES COUNTY METROPOLITAN TRANSPORTATION AUTHORITY
SAN FERNANDO VALLEY EAST-WEST BRT PROJECT

Washington Group International
WASHINGTON GROUP INTERNATIONAL, INC.
5805 SEPULVEDA BLVD., SUITE 500
VAN NUYS, CA 91411

**SHIMMICK
OBYASHI, JV**
5805 SEPULVEDA BLVD., SUITE 500
VAN NUYS, CA 91411

NORTH HOLLYWOOD TO
WARNER CENTER
UTILITIES
SHEET 57 OF 65

CONTRACT NO	C0675
DRAWING NO	U-060
SCALE	HORIZ. 1"=40'
SHEET NO	

m:\p\l\irvine\sheet\temp utilities\U-060.plg 07/21/2006 08:45:12 AM tim.gr.oorn