

90°
R=12 1/2'
L=19 1/2'

90°
R=10'
L=6'


49°
R=10'
L=9'

60°
R=12'
L=13'

90°
R=3'
L=5'

70°
R=12'
L=15'

CONDUIT CURVE DATA			
	ANGLE	RADIUS	LENGTH
△	90° 00' 00"	4'	6.28'
△	86° 03' 23"	9.50'	14.27'
△	0° 00' 0"	00'	00.00'

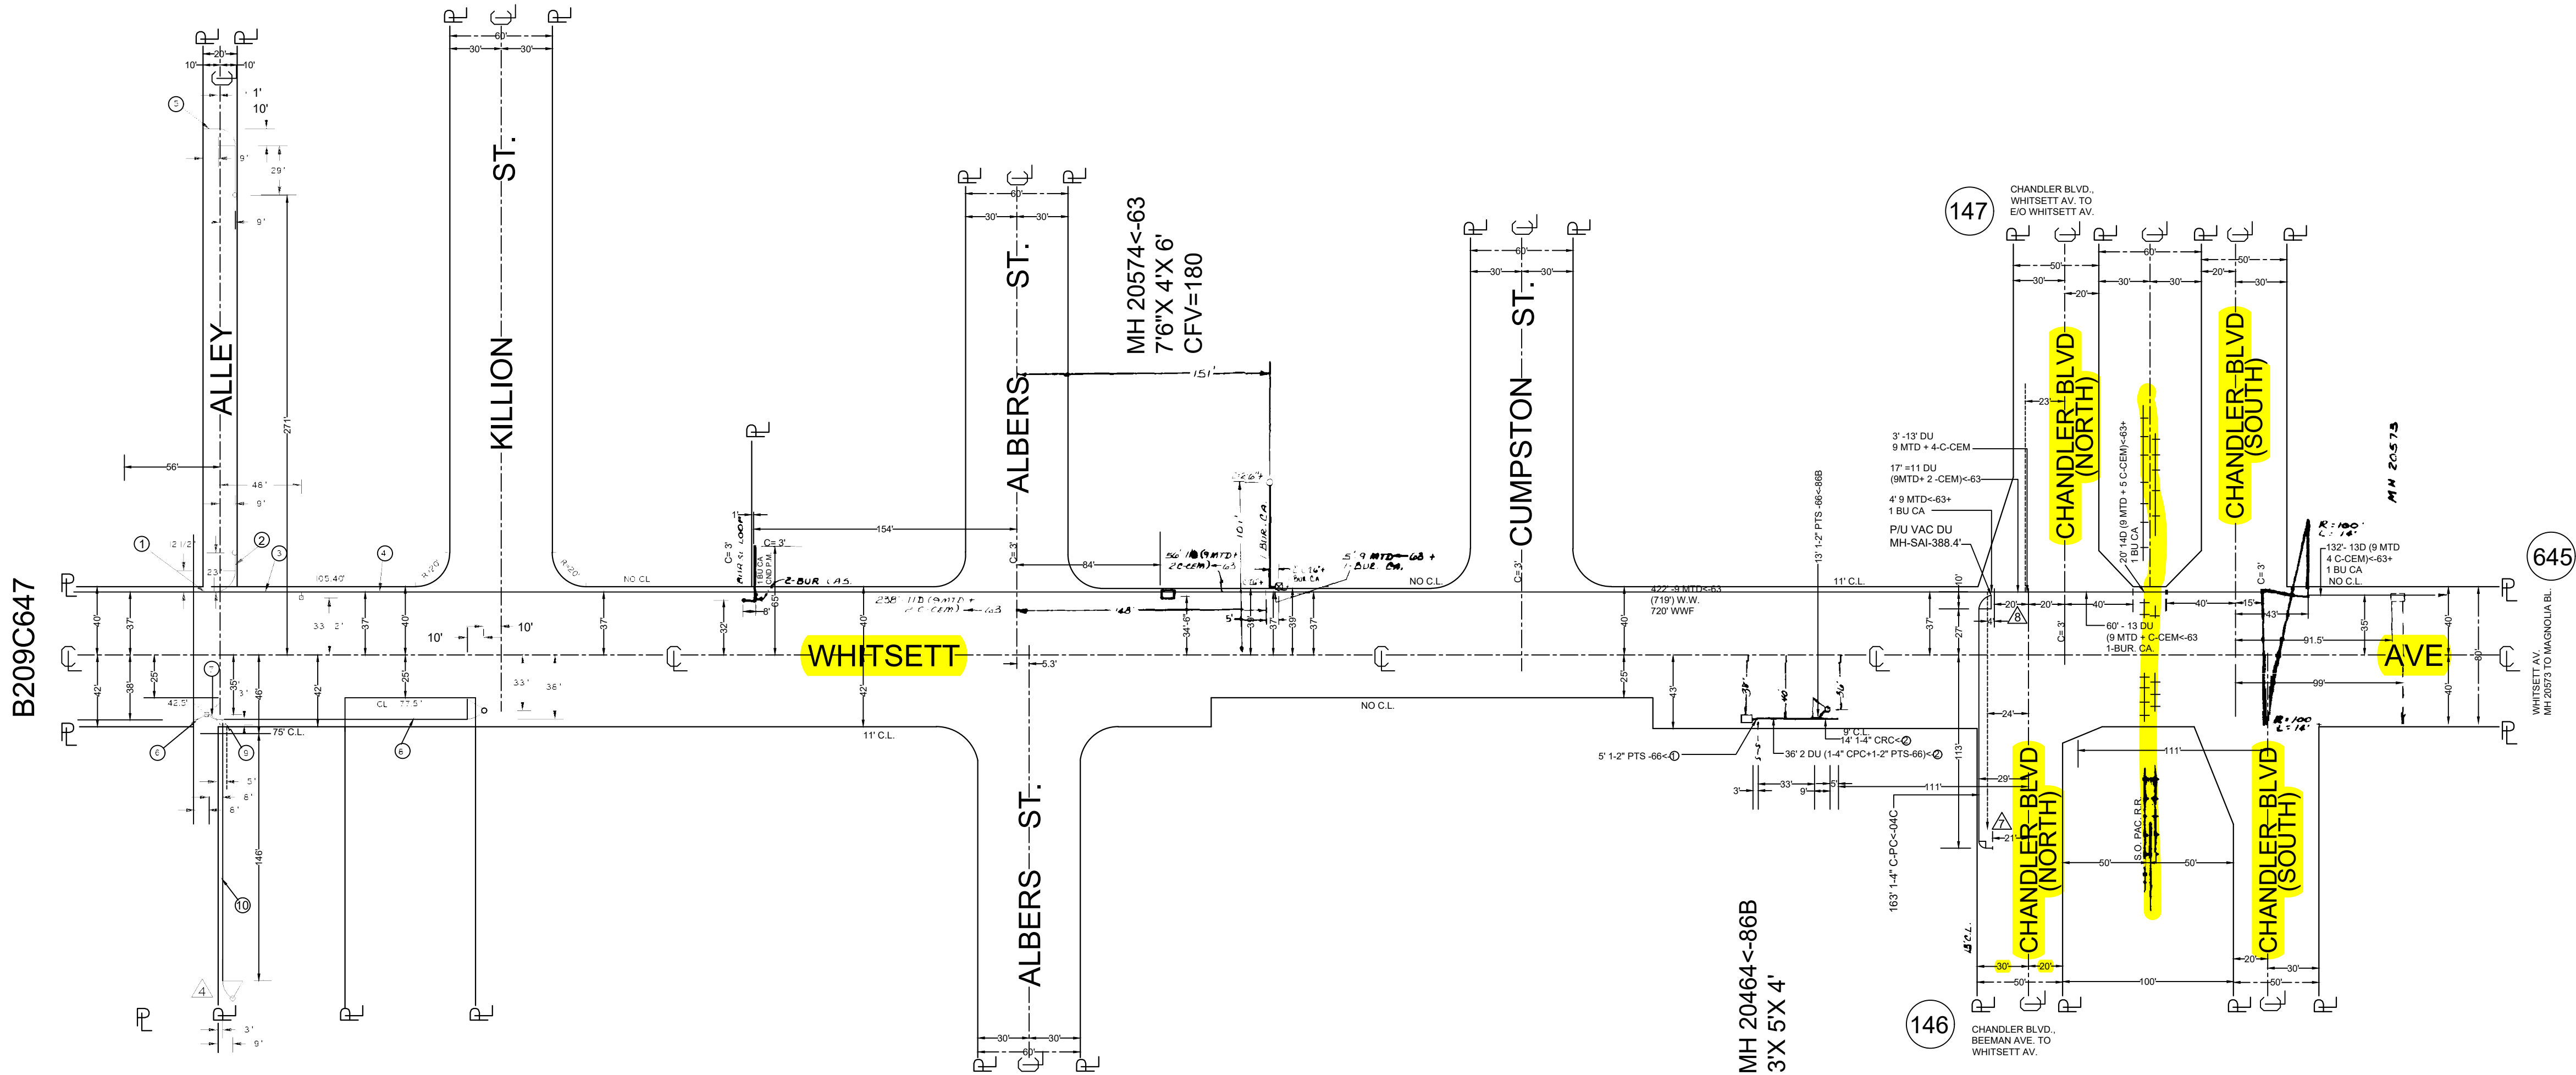


- ① 8" MTD=63+
2" C-CEM=63
- ② 3" 2" C-CEM=63
- ③ 5" 5" MTD=63+
BUR CA
- ④ 270" 8" MTD=63
62" WWF
- ⑤ 57" 1/4" C-PC=75+
BUR CA
- ⑥ 12" 5" 2" C-PC=75+
BUR CA
- ⑦ 1" 4" C-PC=75+
BUR CA
- ⑧ 62" 1/4" C-PC=75
- ⑨ 2" 2" PTS=66+
C-30
- ⑩ 70" 1/4" C-PC=75

1610-7482
1610-7482

IN EFFECT: 10-63

SUPERCEDES:

REVISION		
YEAR	PROJECT	ACT IDENT
6-69	88699	
12-31-69	INV	
11-71	88835	
	45C CONV	
10-78	8396R	
10-79	8537R	
5-80	7011T	
85A	8335W	
86B	8512W	
04C	5251001	

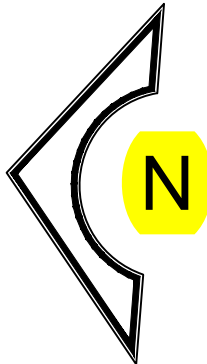

ISSUE DATE 3-24-2008

SEG NO. 1606-7490

R/C 4C EXCEPT AS NOTED



EXCHANGE NORTH HOLLYWOOD

C.O. AREA MAGNOLIA

GEO-CO CODE B2-09

LOCATION
WHITSETT AVE. A/N/O/ KILLION ST.
TO M.H. 20573

FILENAME
B209_NHWCA02_646.dwg

SCALE
1"=50'

RECORD NO.
B209_NHWCA02_646