


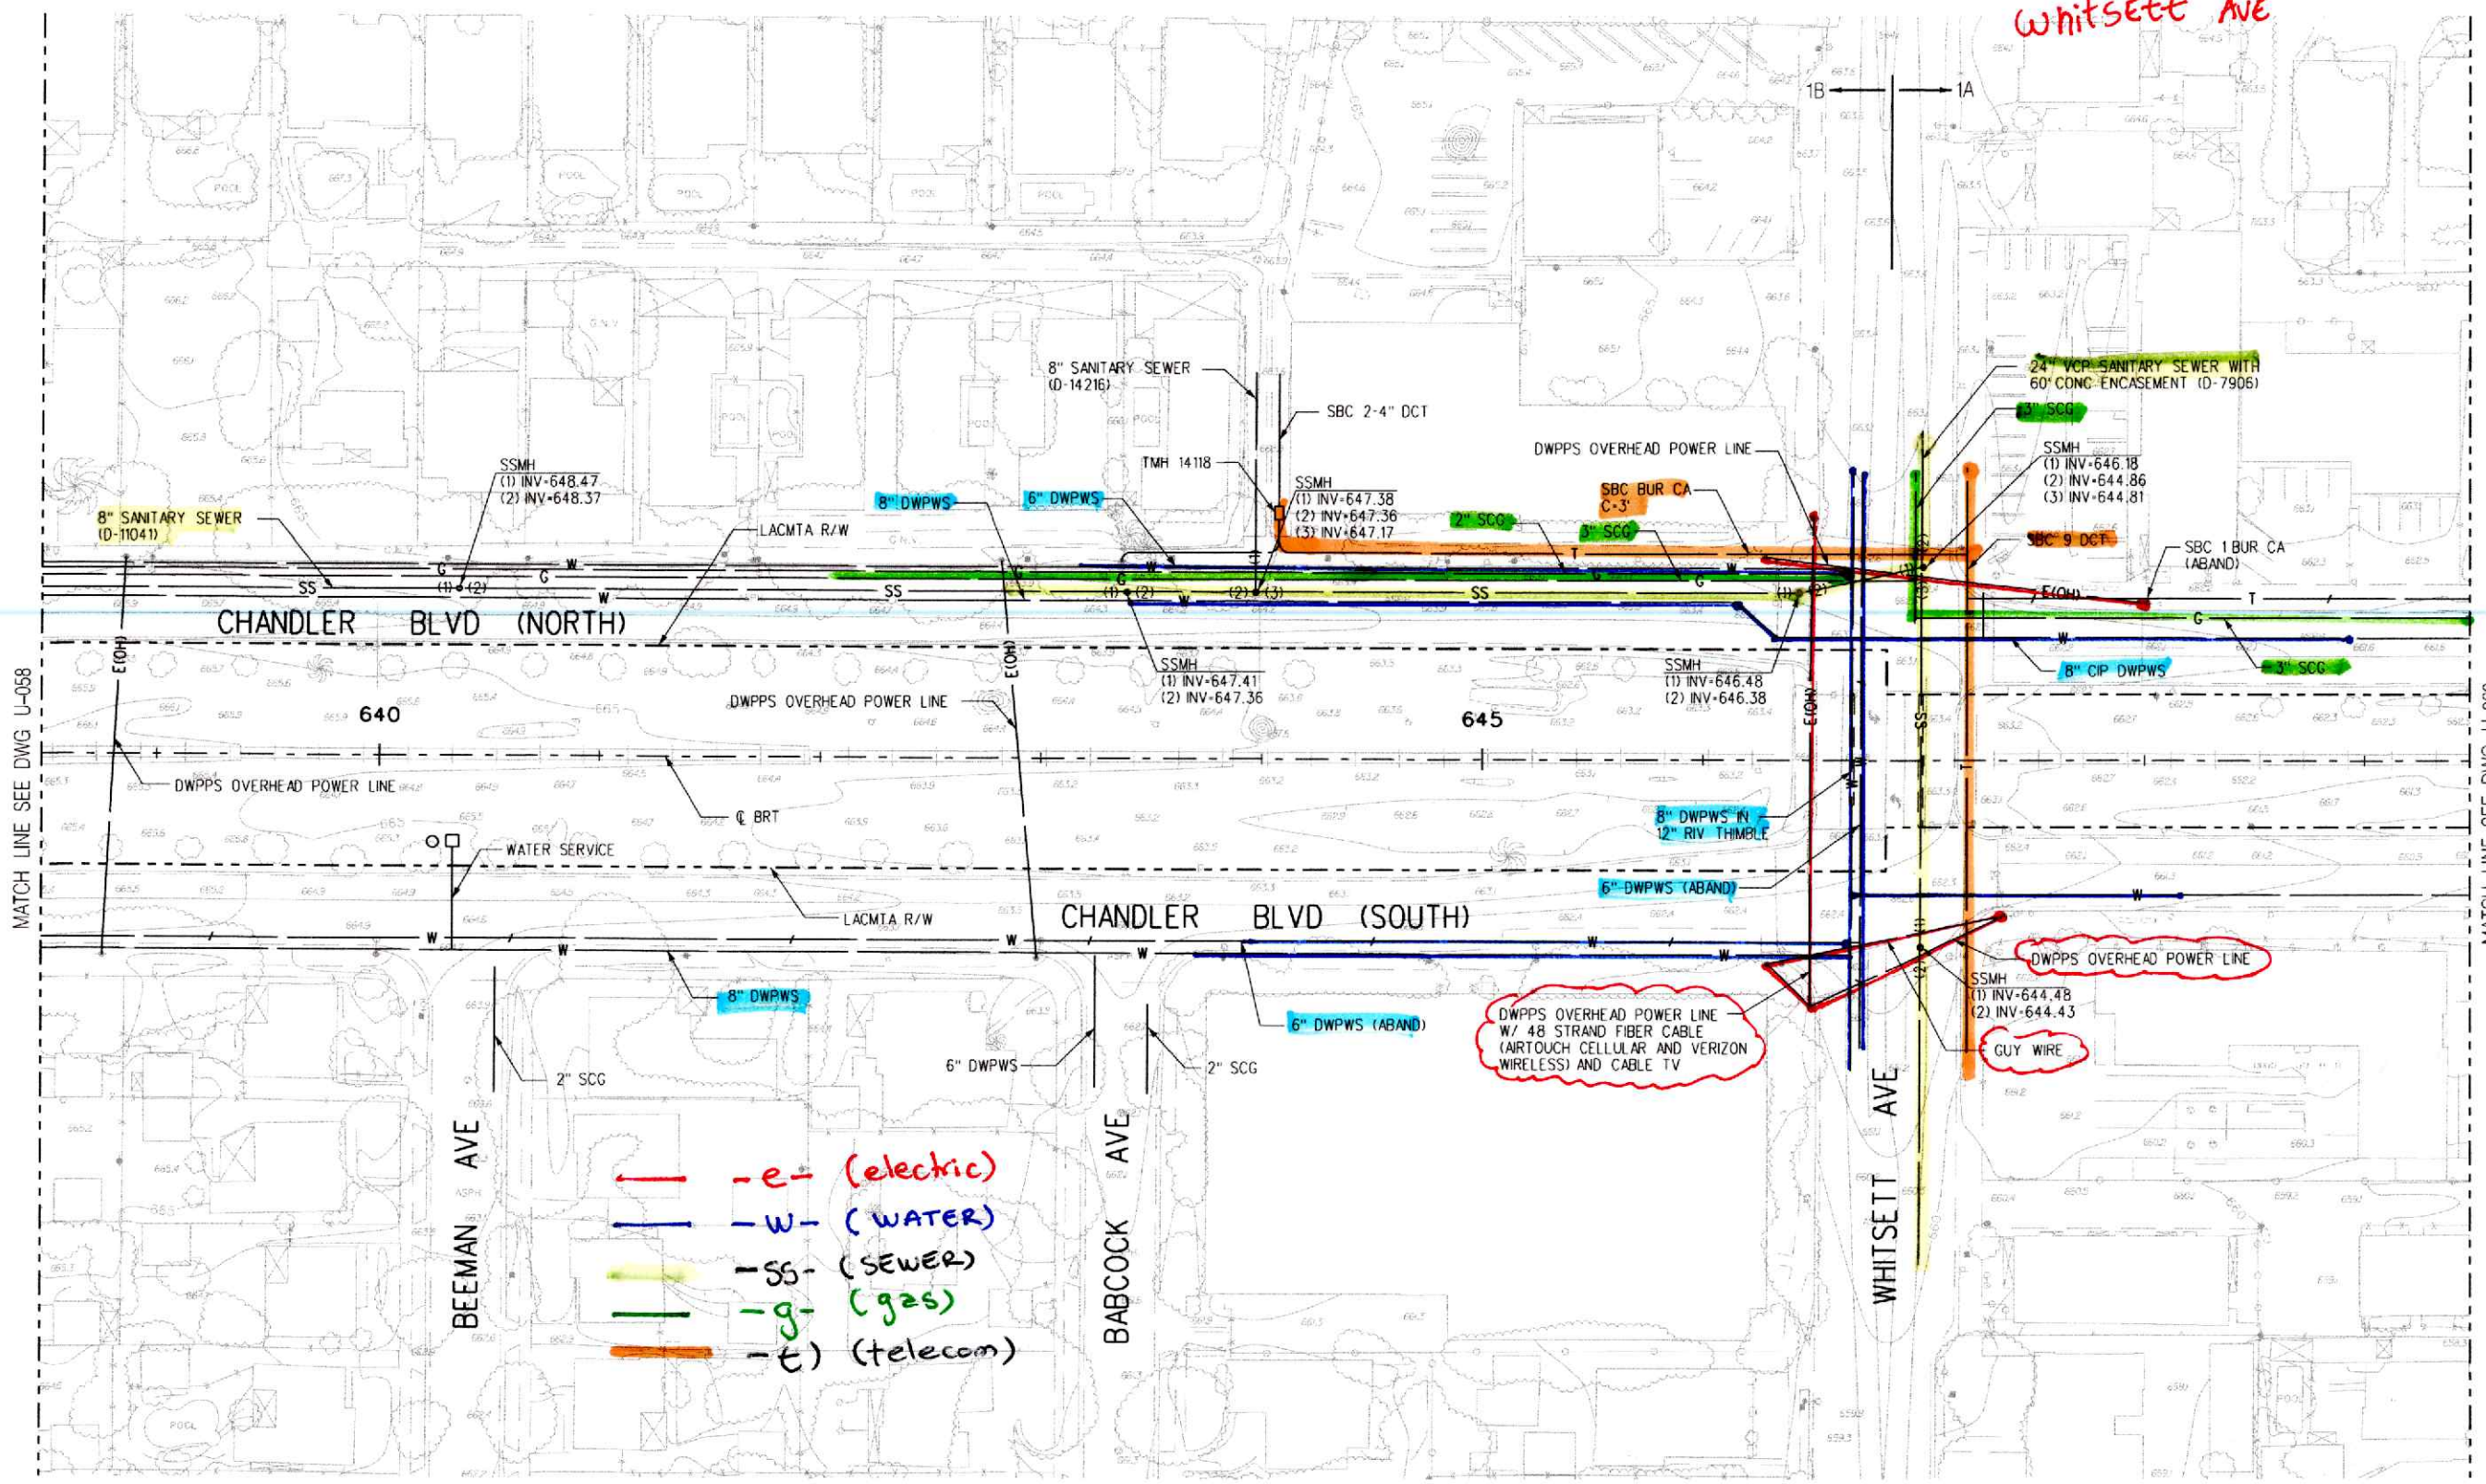

Whitsett Ave



							DESIGNED BY S. KASSISIEH		LOS ANGELES COUNTY METROPOLITAN TRANSPORTATION AUTHORITY SAN FERNANDO VALLEY EAST-WEST BRT PROJECT		 WASHINGTON GROUP INTERNATIONAL, INC. 5805 SEPULVEDA BLVD., SUITE 500 VAN NUTS, CA 91411	NORTH HOLLYWOOD TO WARNER CENTER UTILITIES SHEET 56 OF 65		CONTRACT NO C0675		
							DRAWN BY M. CUTTER					DRAWING NO U-059		REV 0		
							CHECKED BY S. YOUSEFIAN					SCALE HORIZ. 1"=40'		SHEET NO		
							IN CHARGE B. JONES									
0	11/7/03	YX	BEJ	C59517	12/31/03	BRETT E. JONES	ISSUED FOR CONSTRUCTION							07/21/2006 08:45:10 AM		
REV	DATE	BY	APP	REG NO	EXPIRES	SEAL HOLDER	DESCRIPTION									

tim.groom