



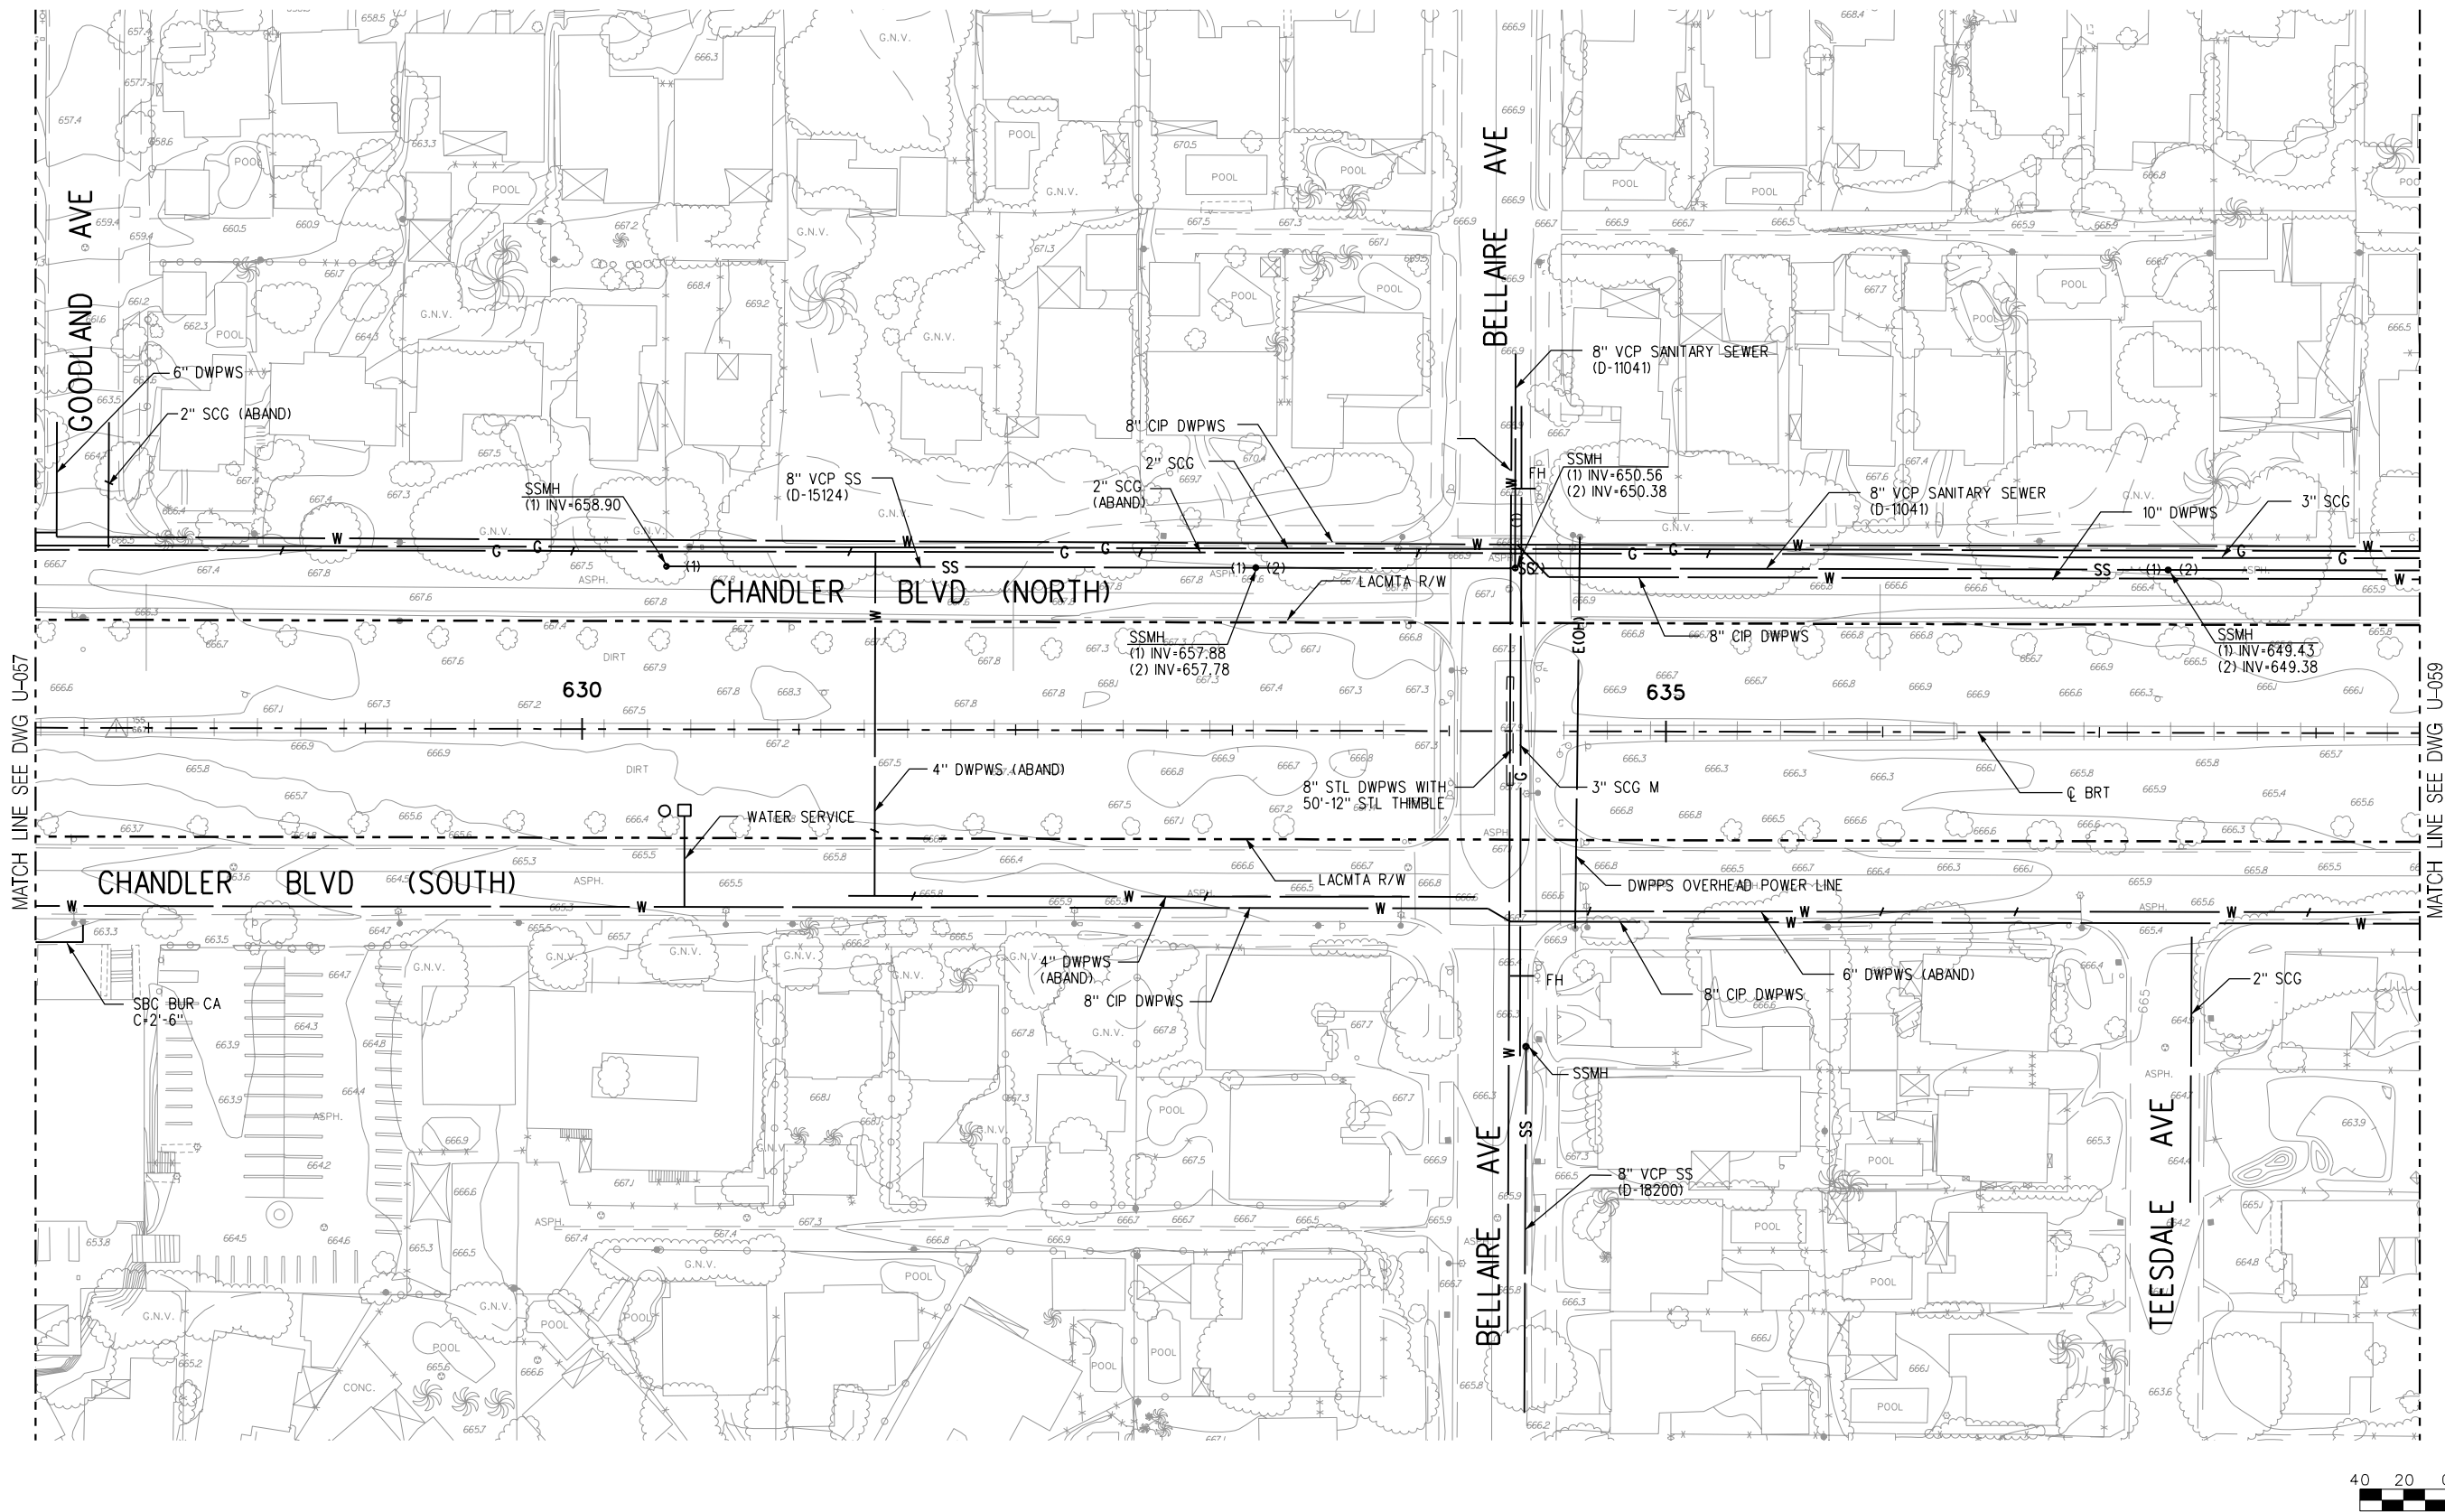

|     |         |    |     |        |          |                |                              |
|-----|---------|----|-----|--------|----------|----------------|------------------------------|
|     |         |    |     |        |          |                |                              |
|     |         |    |     |        |          |                |                              |
| 0   | 1/22/04 | YX | BEJ | C59517 | 12/31/03 | BRETT E. JONES | ISSUED FOR CONSTRUCTION - 1B |
| REV | DATE    | BY | APP | REG NO | EXPIRES  | SEAL HOLDER    | DESCRIPTION                  |

DESIGNED BY  
S. KASSISIEH  
DRAWN BY  
M. CUTTER  
CHECKED BY  
S. YOUSEFIAN  
IN CHARGE  
B. JONES  
DATE  
11/07/03

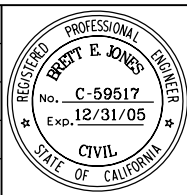



LOS ANGELES COUNTY METROPOLITAN TRANSPORTATION AUTHORITY  
SAN FERNANDO VALLEY EAST-WEST BRT PROJECT



Washington Group International  
WASHINGTON GROUP INTERNATIONAL, INC.  
5805 SEPULVEDA BLVD., SUITE 500  
VAN NUYS, CA 91411



SHIMMICK  
OBAYASHI, JV  
5805 SEPULVEDA BLVD., SUITE 500  
VAN NUYS, CA 91411

NORTH HOLLYWOOD TO  
WARNER CENTER  
UTILITIES  
SHEET 55 OF 65

|             |               |
|-------------|---------------|
| CONTRACT NO | C0675         |
| DRAWING NO  | U-058         |
| SCALE       | HORIZ. 1"=40' |
| SHEET NO    |               |