


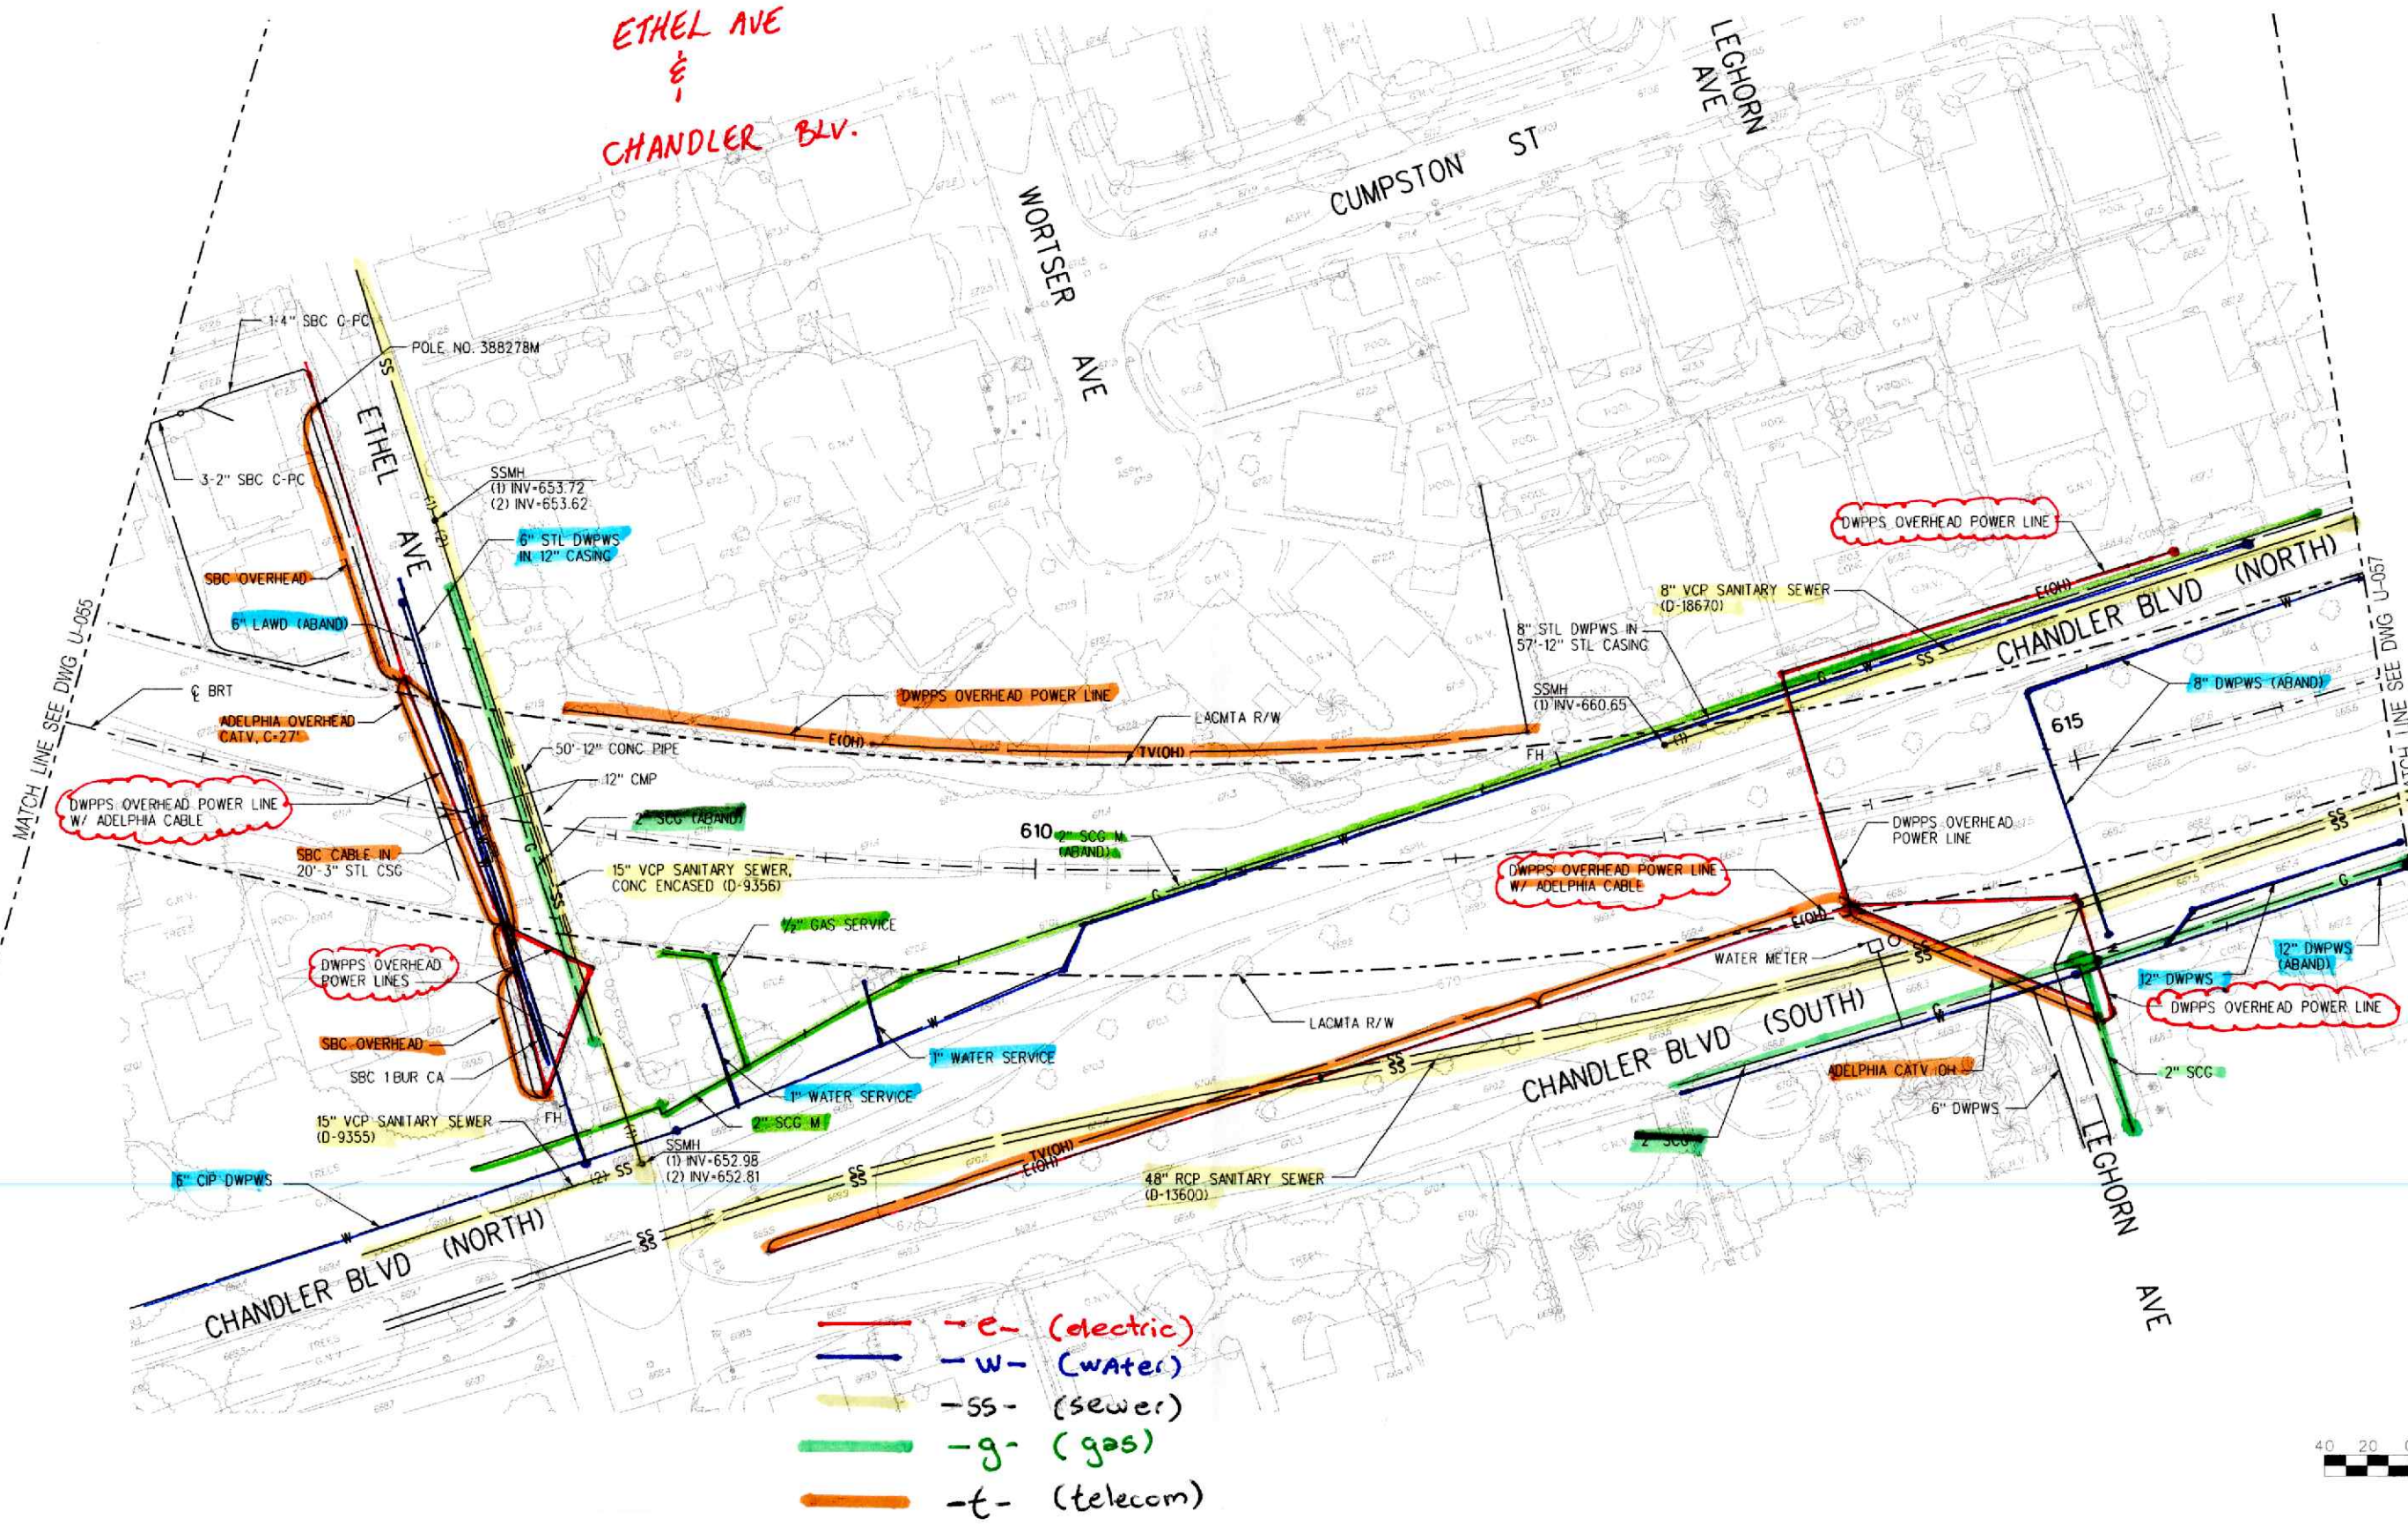


ETHEL AVE
&
CHANDLER BLV.



- E- (electric)
- W- (water)
- SS- (sewer)
- G- (gas)
- T- (telecom)

REV	DATE	BY	APP	REG NO	EXPIRES	SEAL HOLDER	DESCRIPTION
0	1/22/04	YX	BEJ	C59517	12/31/03	BRETT E. JONES	ISSUED FOR CONSTRUCTION - 1B

DESIGNED BY
S. KASSISIEH
DRAWN BY
M. CUTTER
CHECKED BY
S. YOUSEFIAN
IN CHARGE
B. JONES
DATE
11/07/03

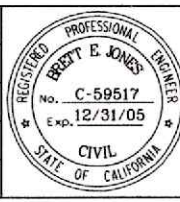

LOS ANGELES COUNTY METROPOLITAN TRANSPORTATION AUTHORITY
SAN FERNANDO VALLEY EAST-WEST BRT PROJECT

Washington Group International
WASHINGTON GROUP INTERNATIONAL, INC.
5805 SEPULVEDA BLVD., SUITE 500
VAN NUYS, CA 91411

SHIMMICK
OBAYASHI, JV
5805 SEPULVEDA BLVD., SUITE 500
VAN NUYS, CA 91411

NORTH HOLLYWOOD TO
WARNER CENTER
UTILITIES
SHEET 53 OF 65

CONTRACT NO	C0675
DRAWING NO	U-056
SCALE	HORIZ. 1"=40'
SHEET NO	0