


IN EFFECT 12-71	
REVISION	
AUTHORITY	DATE OF COMP.
18260	12-71
1111 6-30-72	
R/C 45 Rebuild	
12531	808

(CF0068 (4-78)
(REF: B5P 928-100-050 P1)

IN EFFECT		
SUPERSEDES		
REVISION		
VR	AUTH	ACT ID
98B	B47540T	

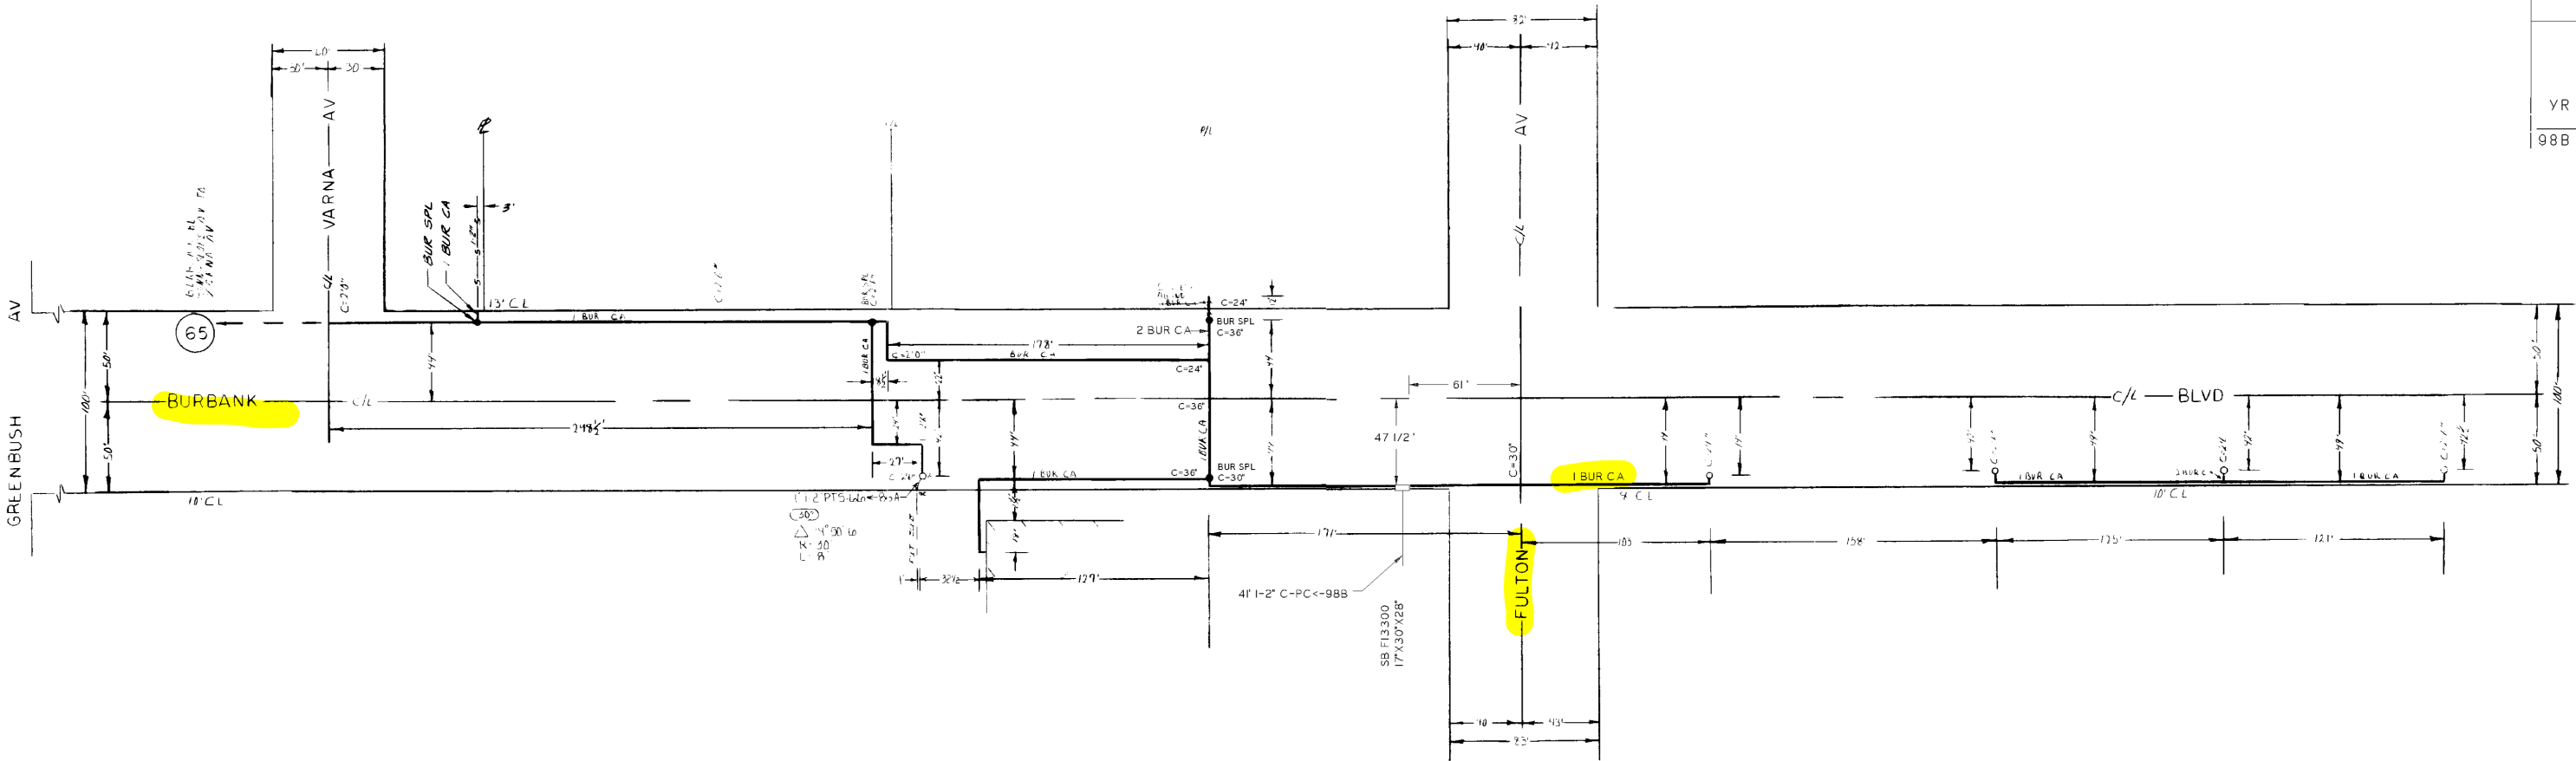

ISSUE DATE 11-05-98

SEGMENT NO. 1610-7476
R/C 45 EXCEPT AS NOTED

PACIFIC BELL

C.O.	CEDROS
EXCH	VAN NUYS
GEO-CO CODE	B4-02
BURBANK BLVD VARNA AV TO 502' E/O C/L/O FULTON AV	
TYPE OF RECORD :	
SCALE: 1" = 50'	RECORDS NO. B402C64