


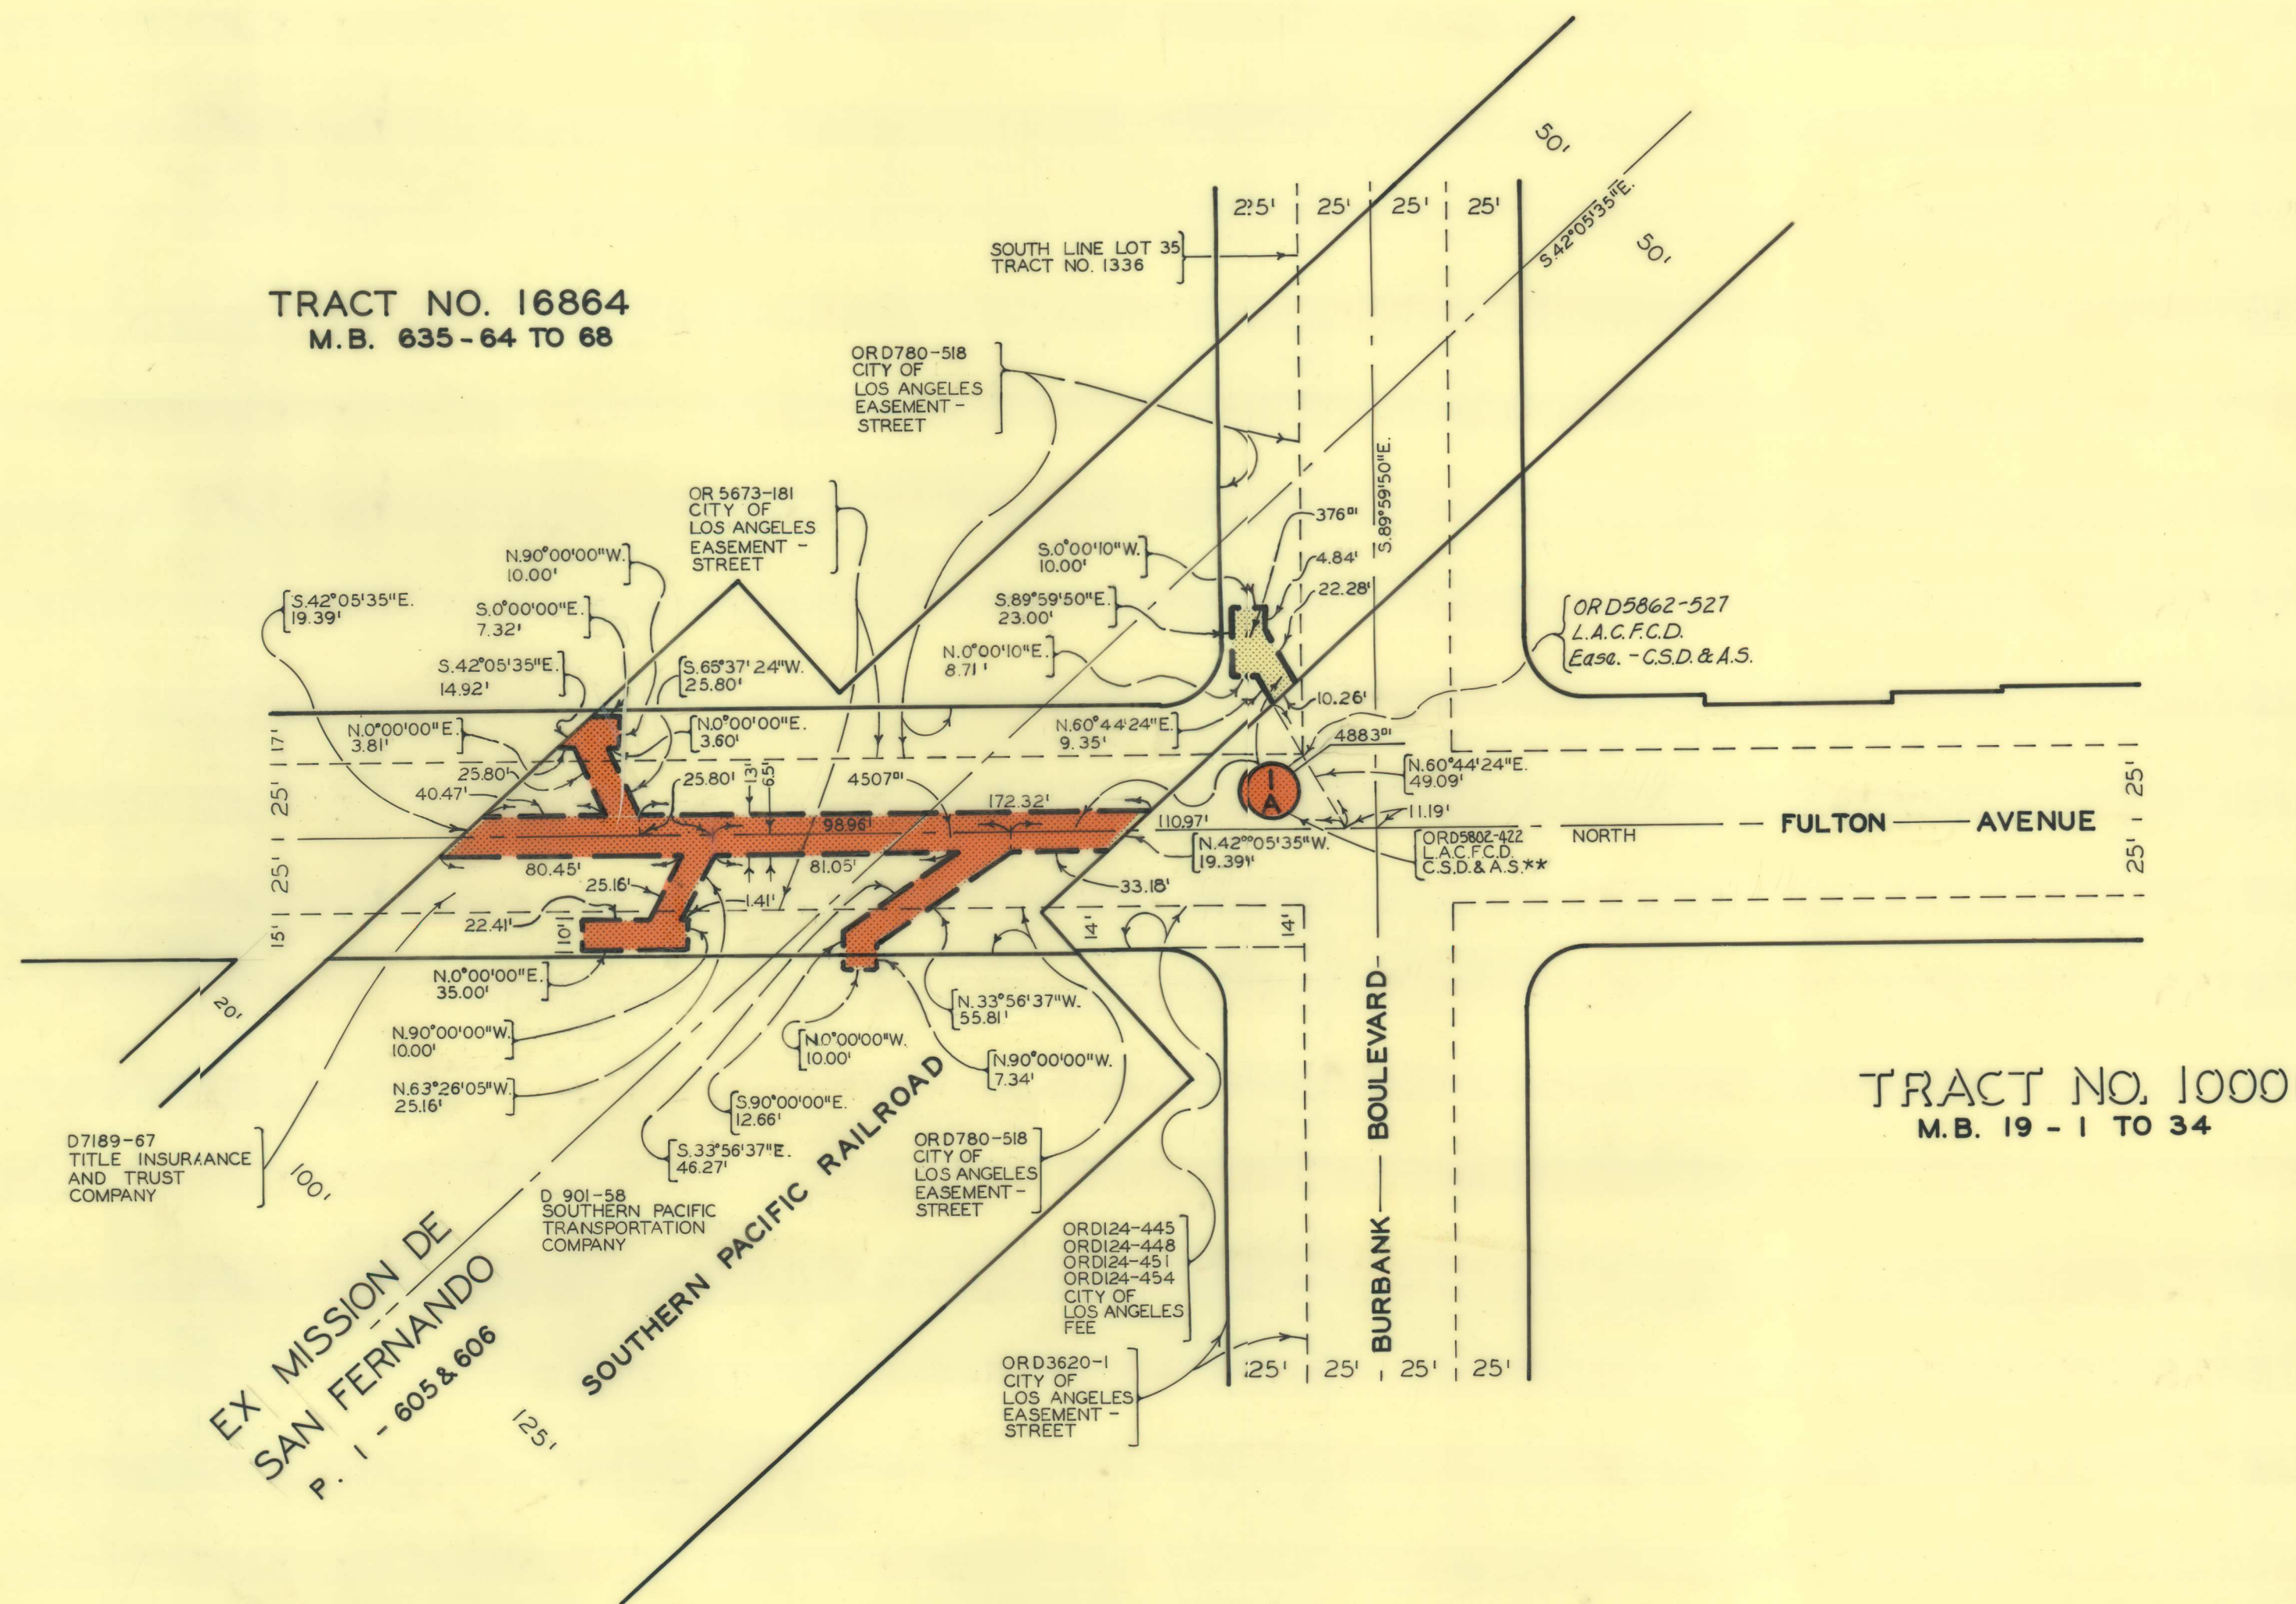

TRACT NO. 16864
M.B. 635-64 TO 68

TRACT NO. 1000
M.B. 19-1 TO 34

LEGEND

0000 = area of parcel.

Denotes square feet.

** C.S.D. & A.S. Denotes covered storm drain and appurtenant structures.

ALL IN THE CITY OF LOS ANGELES

LOS ANGELES COUNTY FLOOD CONTROL DISTRICT				
PROJECT 9204				
NORTH HOLLYWOOD				
BURBANK BOULEVARD AT FULTON AVENUE				
REVISED	REFERENCES	PREPARED BY	RECOMMENDED BY	DATE
	C.I. 54 (A-3) 470-9204-D3.1 TO .24	L. STONER T. MOSS		8-15-72
		CHECKED BY I. ITO	DIVISION ENGINEER, RIGHT OF WAY	SCALE AS SHOWN
		PROJECT ENGINEER	APPROVED BY	
		CHIEF ENGINEER	CIVIL ENGINEER NO. 8736	No. 470-9204-RW 2