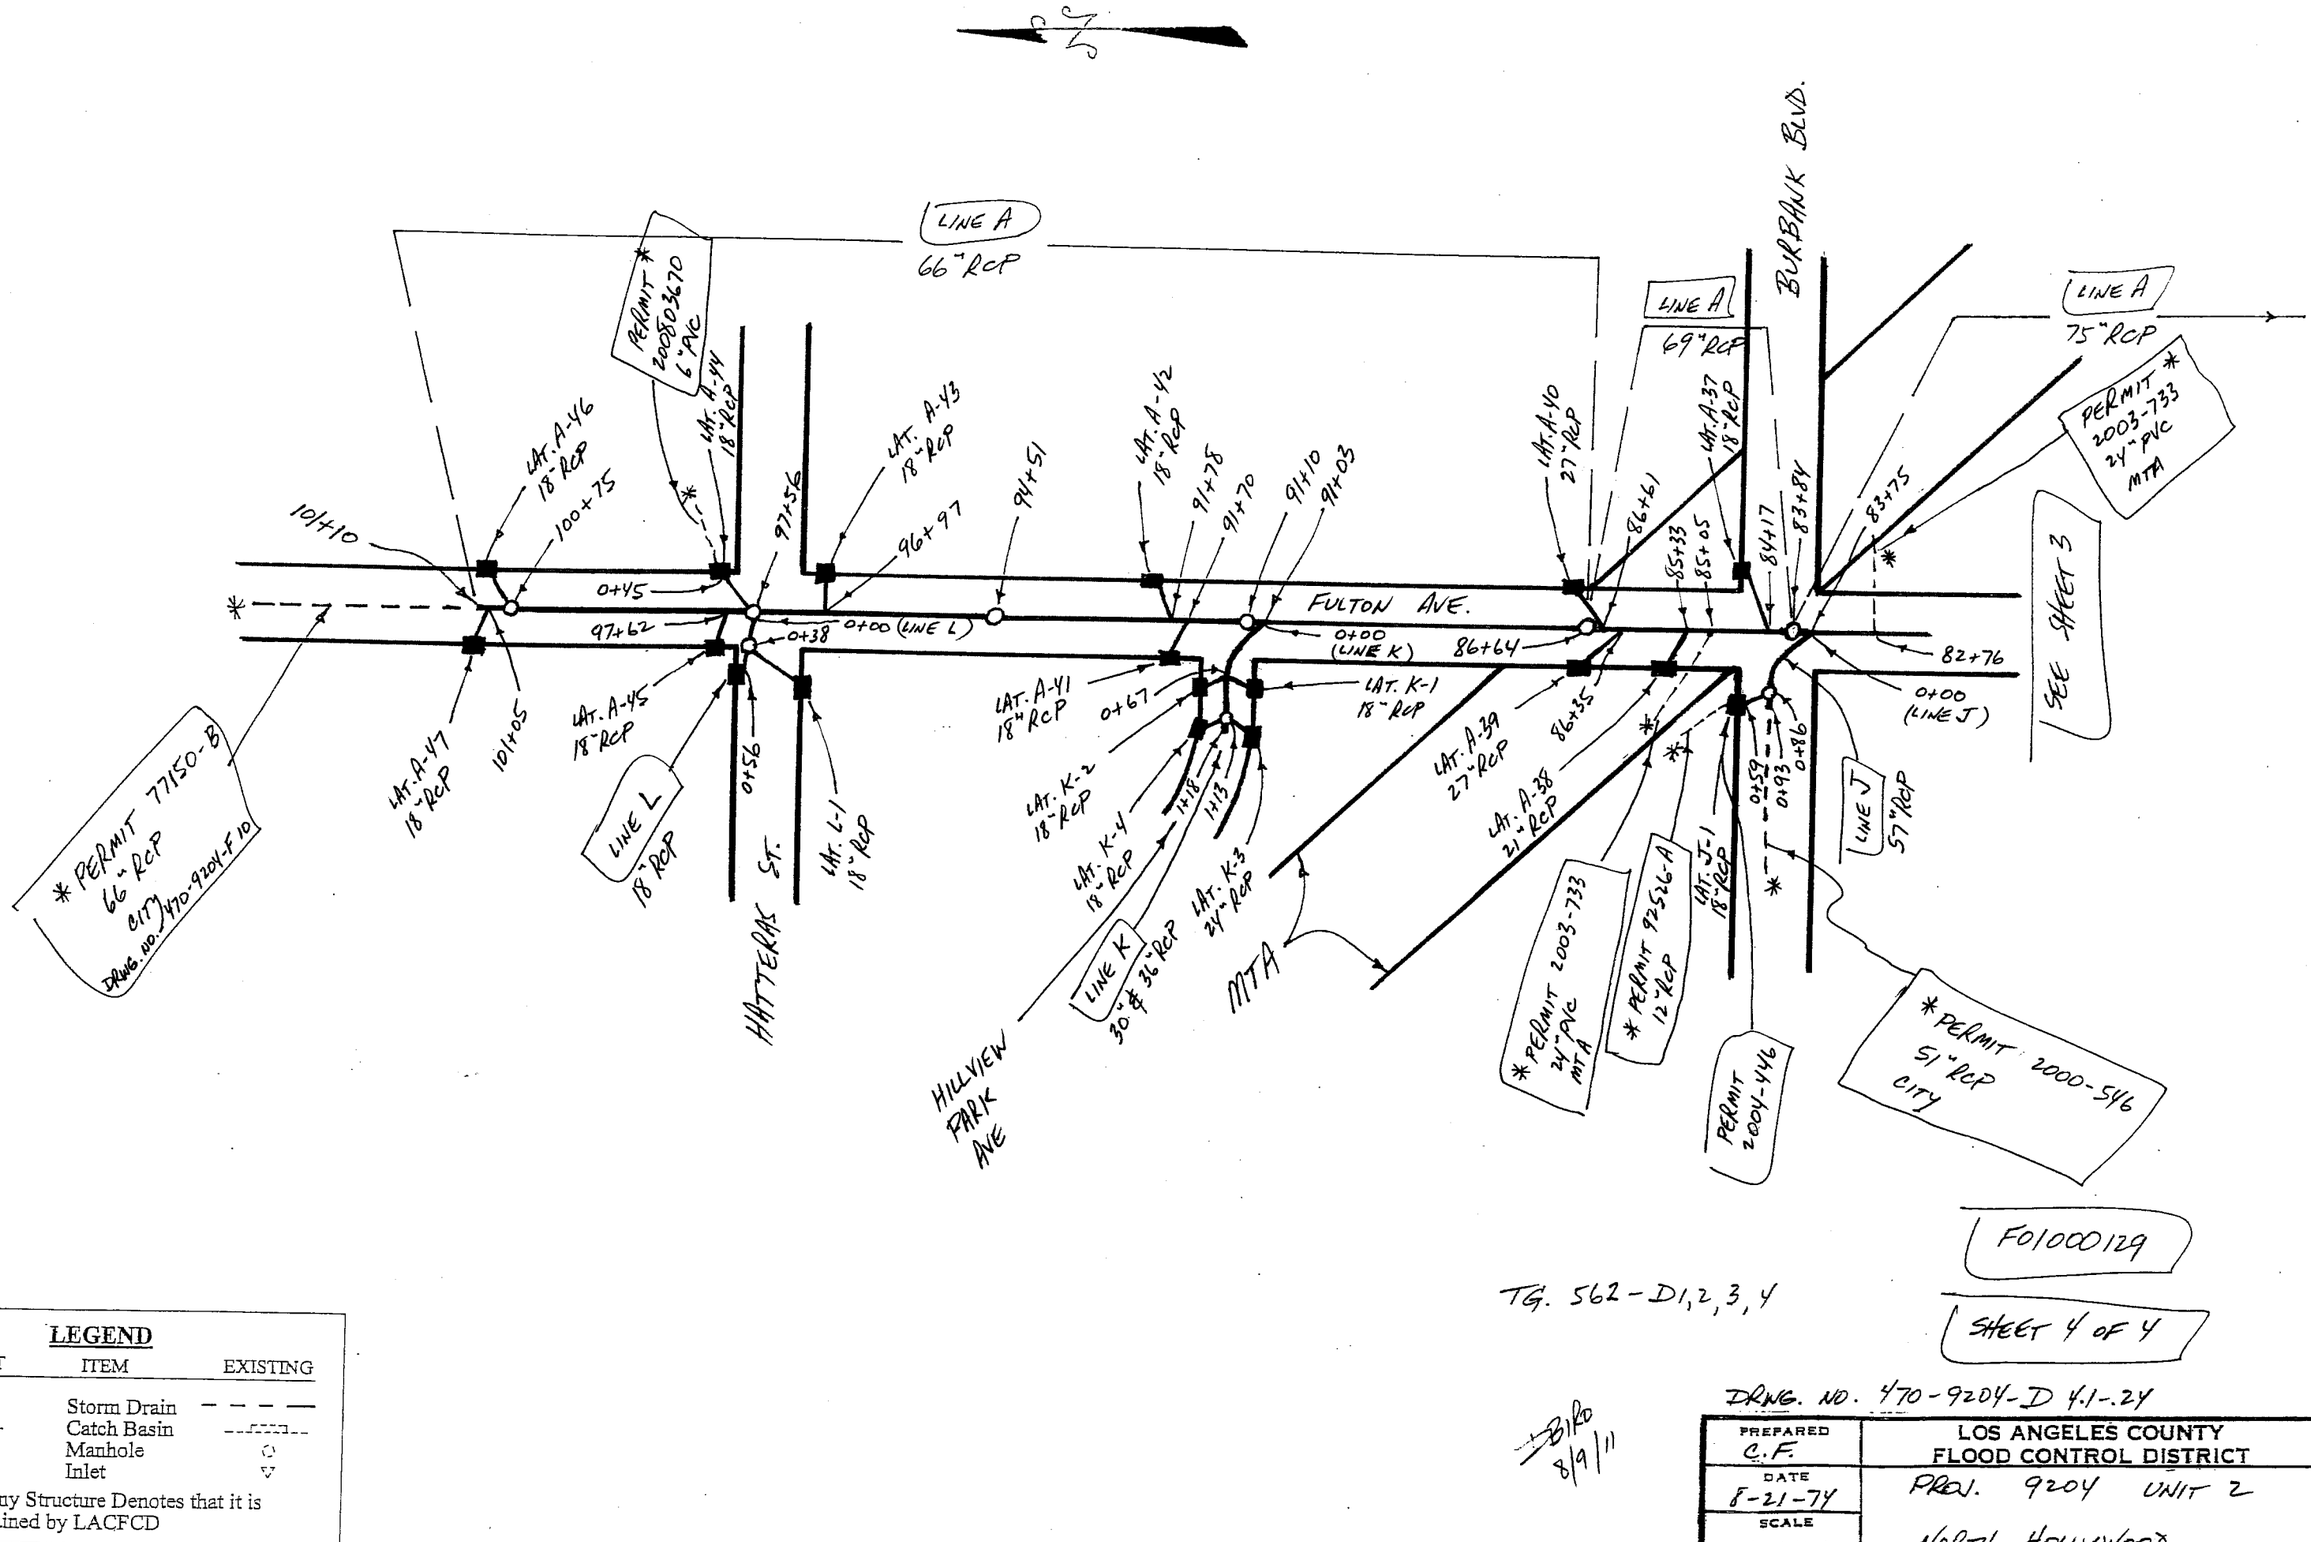

LEGEND

PROJECT	ITEM	EXISTING
———	Storm Drain	– – – —
═══	Catch Basin	---::::---
○	Manhole	○
▼	Inlet	▽

An * by any Structure Denotes that it is not Maintained by LACFCD

F01000129

TG. 562-D1,2,3,4

SHEET 4 OF 4

DRWG. NO. 470-9204-D 4.1-.24

PREPARED C.F.	LOS ANGELES COUNTY FLOOD CONTROL DISTRICT
DATE 8-21-74	PROJ. 9204 UNIT 2
SCALE NONE	NORTH HOLLYWOOD

8/9/11