


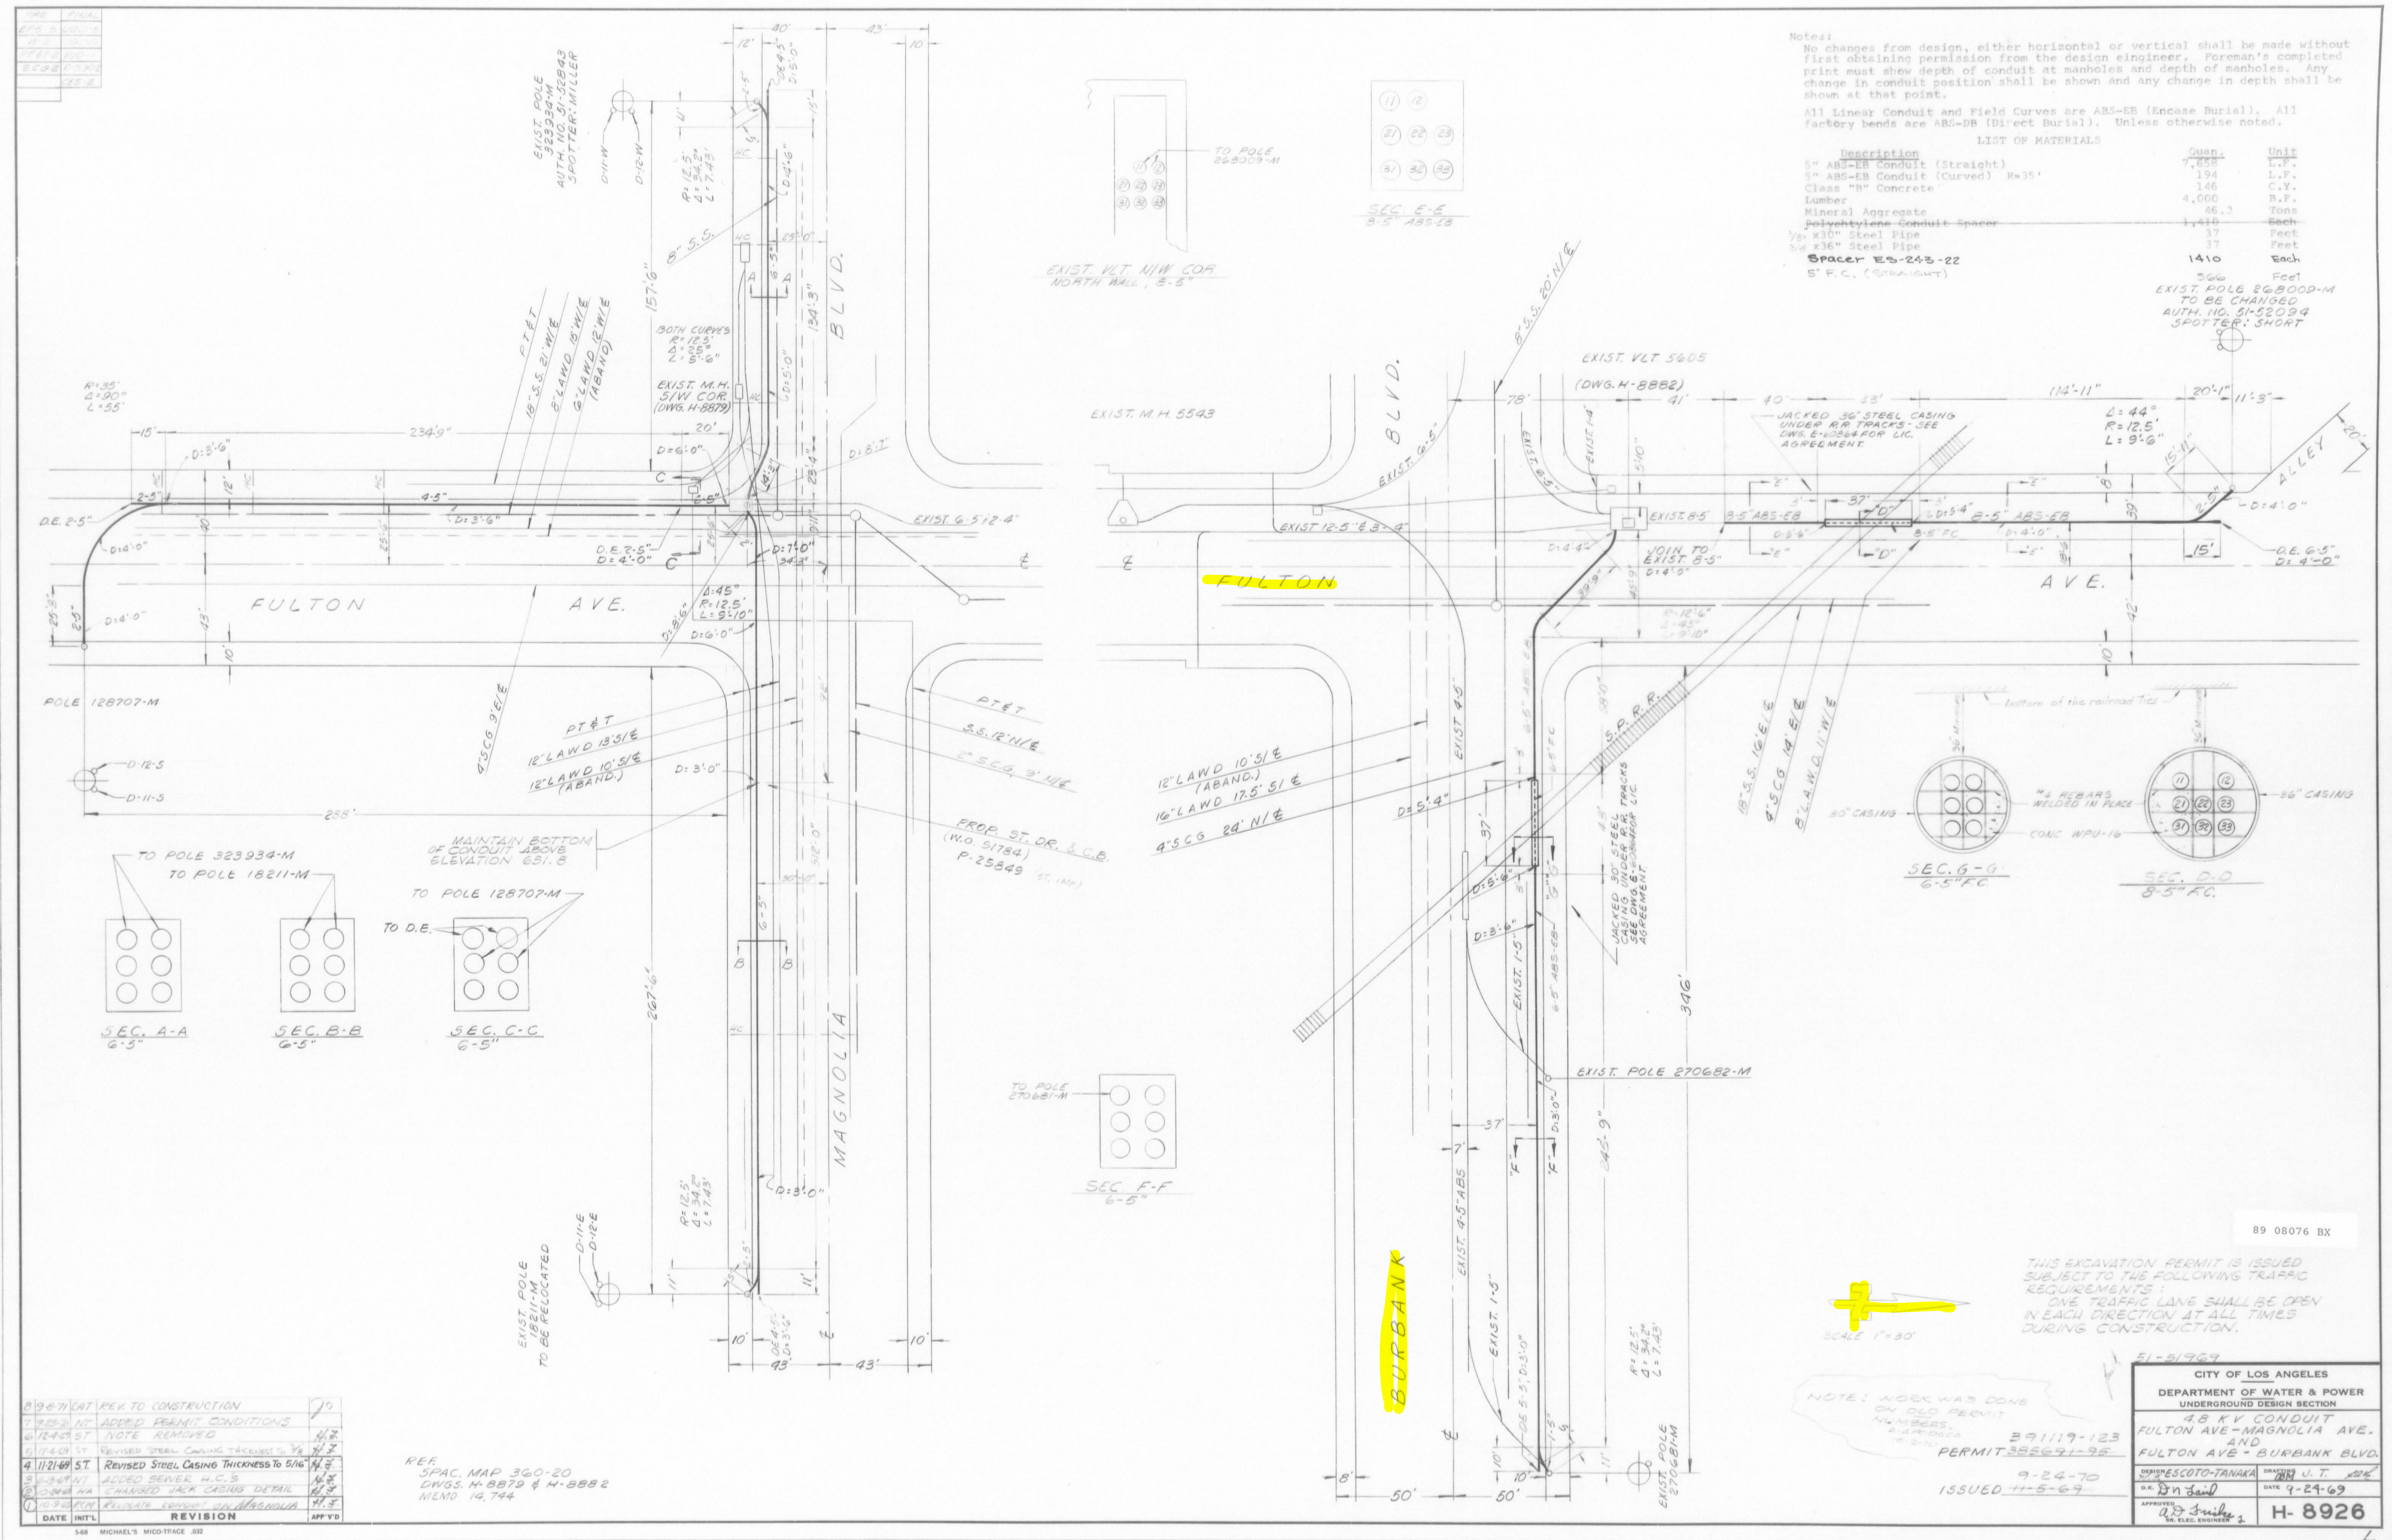

Notes:
No changes from design, either horizontal or vertical shall be made without first obtaining permission from the design engineer. Foreman's completed print must show depth of conduit at manholes and depth of manholes. Any change in conduit position shall be shown and any change in depth shall be shown at that point.
All Linear Conduit and Field Curves are ABS-EB (Encase Burial). All factory bends are ABS-DB (Direct Burial). Unless otherwise noted.

LIST OF MATERIALS

Description	Quan.	Unit
5" ABS-EB Conduit (Straight)	7,858	L.F.
5" ABS-EB Conduit (Curved) R=35'	194	L.F.
Class "B" Concrete	146	C.Y.
Lumber	4,000	B.F.
Mineral Aggregate	46.3	Tons
Polyethylene Conduit Spacer	1,410	Feet
7/8" x 3/8" Steel Pipe	37	Feet
3/4" x 3/8" Steel Pipe	37	Feet
SPACER ES-243-22	1410	Each
5" F.C. (STRAIGHT)		

EXIST. POLE 265009-M
TO BE CHANGED
AUTH. NO. 51-52094
SPOTTER SHORT

DATE	INITIAL	REVISION	APP'D
8/9/67	WAT	REV. TO CONSTRUCTION	
7/25/67	NT	ADDED PERMIT CONDITIONS	
6/14/67	ST	NOTE REMOVED	
6/14/67	ST	REVISED STEEL CASING THICKNESS TO 5/16"	
4/11/67	ST	REVISED STEEL CASING THICKNESS TO 5/16"	
3/13/67	NT	ADDED SEVERAL H.C.S.	
2/20/67	NT	CHANGED JACK CASING DETAIL	
1/23/67	NT	REVISED JOINT DETAIL	

REF.
SPAC. MAP 360-20
DWGS. H-8879 & H-8882
MEMO 14,744

89 08076 BX

THIS EXCAVATION PERMIT IS ISSUED SUBJECT TO THE FOLLOWING TRAFFIC REQUIREMENTS:
ONE TRAFFIC LANE SHALL BE OPEN IN EACH DIRECTION AT ALL TIMES DURING CONSTRUCTION.

SCALE 1"=30'

NOTE: WORK WAS DONE ON OLD PERMIT. NUMBERS 391119-123 PERMIT 385691-95 9-24-70 ISSUED 4-5-69

CITY OF LOS ANGELES	
DEPARTMENT OF WATER & POWER	
UNDERGROUND DESIGN SECTION	
48 KV CONDUIT	
FULTON AVE - MAGNOLIA AVE.	
AND	
FULTON AVE - BURBANK BLVD.	
DESIGNED BY SCOTO-TANAKA	DRAWN BY J. T. 224
CHECKED BY J. T. 224	DATE 9-24-69
APPROVED BY J. T. 224	DATE 9-24-69
EL. ENG. 1	H-8926

CERTIFICATE OF AUTHENTICITY

THIS IS TO CERTIFY that this microimage is a true and complete reproduction of the City of Los Angeles, Department of Water and Power records as delivered during the normal course of business. The photographic process used for the microimaging of this document was accomplished in a manner and on microfilm which meets the City of Los Angeles Records Management Program requirements for permanent micrographic reproduction and was accomplished under my direction and control.

Bechtel Corporation Company Name	Don R. Walker Signature
June 28, 1989 Date	Don R. Walker Typed Name
Norwalk, California (City) (State)	Micrographics Operations Supervisor Title

CITY OF LOS ANGELES DEPARTMENT OF WATER AND POWER

DECLARATION OF INTENT AND PURPOSE

The document appearing in this microimage is an actual record of the Power System Service Division, Los Angeles Department of Water and Power. Filing of this document is in accordance with City Administrative Code, Division 12, "Records", and is part of a planned program of records retention.

Don R. Walker
Signature
Thomas H. McElroy
Typed Name
Assistant Engineer of System Services
Title

3/16/69
Date
Los Angeles, California
Place