



PRE	FINAL
EP-5-2	UGD-4
WED-2	UGC-10
PMT-2	WUD-2
SCG-2	D30-5-3
VUD-1	
COORD-1	

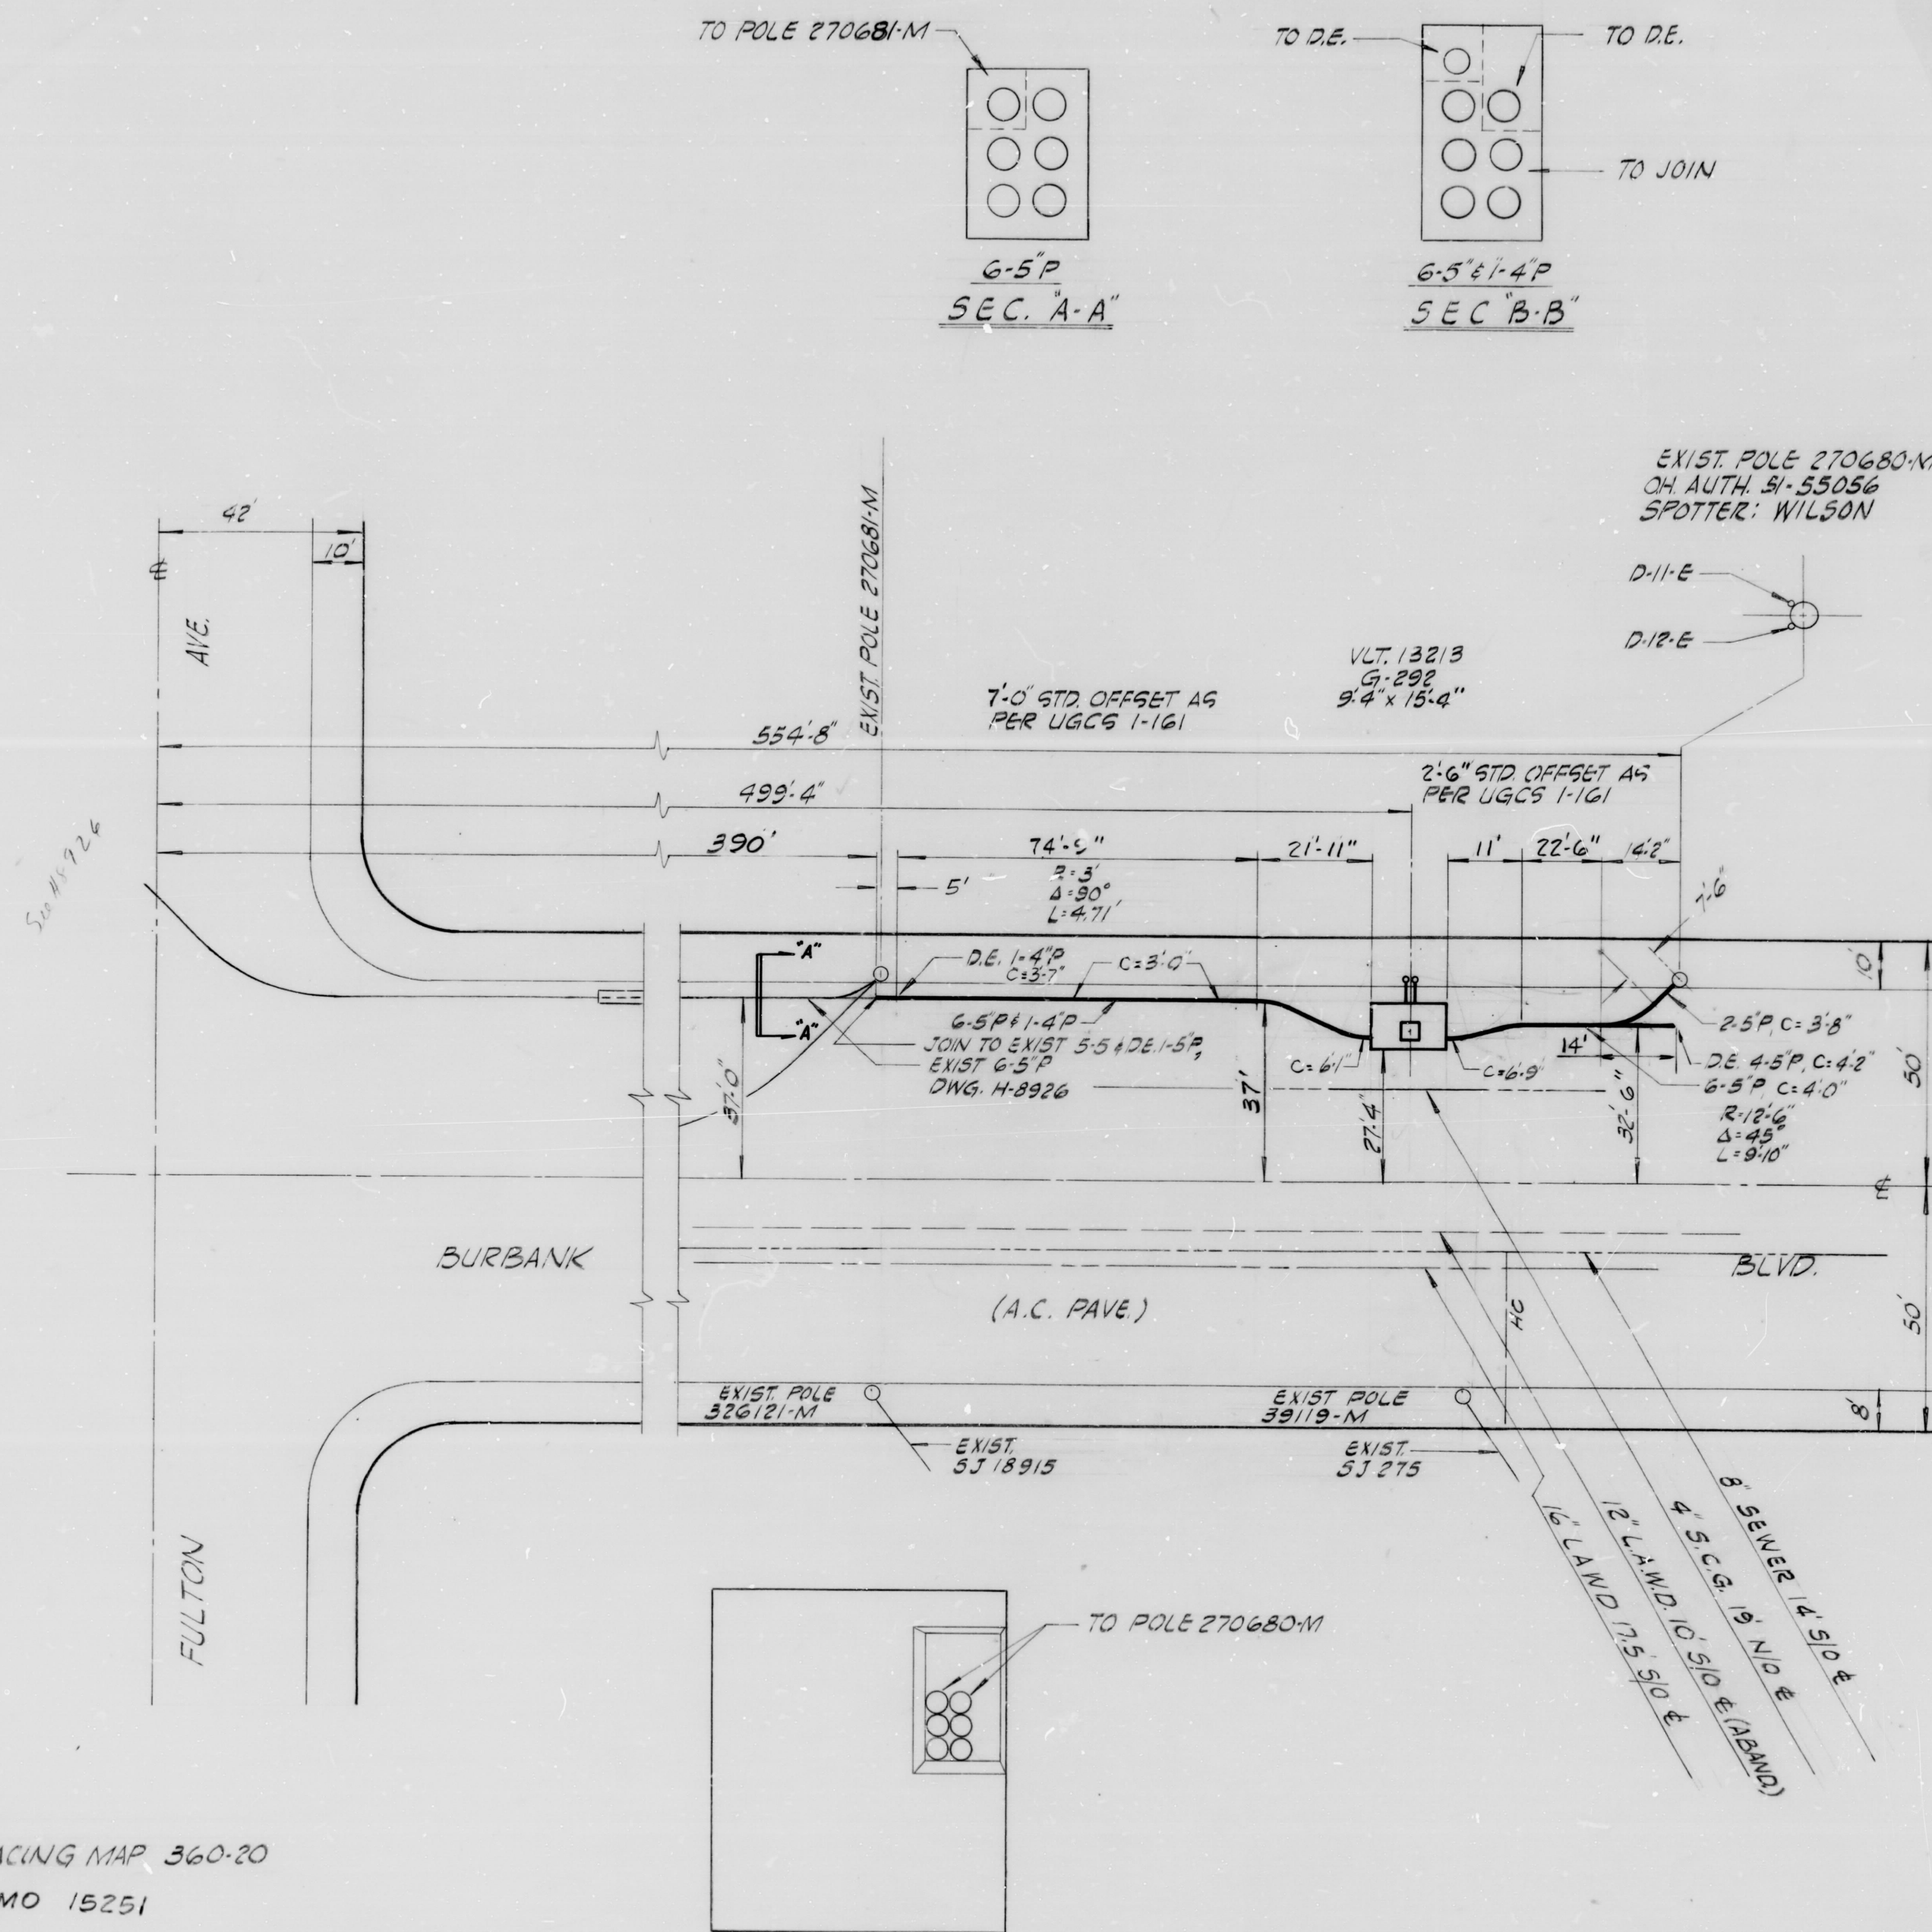

Notes:
 Cable and transformer installation drawing to follow.
 No changes from design, either horizontal or vertical shall be made without first obtaining permission from the design engineer. Foreman's completed print must show depth of conduit at manholes and depth of manholes. Any change in conduit position shall be shown and any change in depth shall be shown at that point.
 Cover over all conduit to be 30".
 Avoid existing mainline sewer and sewer house connections by 3' horizontally.

Description	Quantity	Unit
Precast Vault G-292 (Complete) W/OPT. KD #3	1	Each
5" ABS-EB Conduit (Straight)	910	L.F.
5" ABS-DB Conduit (Curved) R=12.5'	4	Each
5" ABS-DB Conduit (Curved) R=5'	2	Each
5" Galvanized Conduit Nipple, 2' long	2	Each
5" Adaptor Coupling, Fiber to G.C.	2	Each
Class Concrete, DWP-13U	22	C.Y.
Lumber	1,800	B.F.
Mineral Aggregate	9	Tons
Aggregate Base Material	15	Tons
Conduit Spacers: ES-234 (2DM)	104	Each

THIS EXCAVATION PERMIT IS ISSUED SUBJECT TO THE FOLLOWING CONDITIONS: There shall be two traffic lanes open in each direction between the hours of 7 a.m. and 9 a.m. and between 4 p.m. and 7 p.m., and one traffic lane in each direction at all other times.

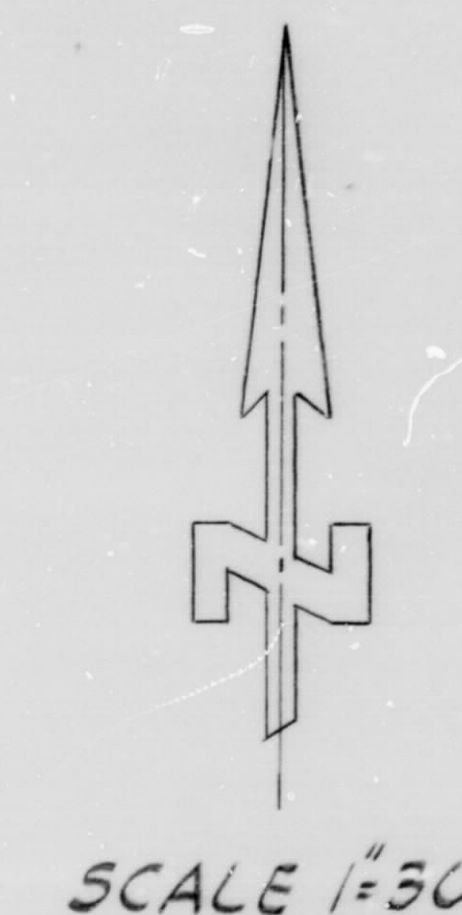

REF.
 SPACING MAP 360-20
 MEMO 15251

VLT/13219
 EAST WALL
 G-5-P

PERMIT 398736
 ISSUED 12-14-71

②	8-15-72	CWN.	REVISED TO CONSTRUCTION	JA
①	12-7-71	CWN.	ADDED 1-4" SERV. COND.	H.F.
	DATE	INIT'L	REVISION	APP'VD

51-55327 89 13790 BX

CITY OF LOS ANGELES DEPARTMENT OF WATER & POWER UNDERGROUND DESIGN SECTION	
4.8KV CONDUIT BURBANK BLVD. 3870 TO 5540 N/O FULTON AVE	
DESIGN PIZZO GAI	DRAWING NEALY
DATE 11-29-71	APPROVED G-9779
SR. ELEC. ENGINEER	

THIS IS TO CERTIFY that this microimage is a true and complete reproduction of the City of Los Angeles, Department of Water and Power records as delivered during the normal course of business. The photographic process used for the microfilming of this document was accomplished in a manner and on microfilm which meets the City of Los Angeles Records Management Program requirements for permanent micrographic reproductions and was accomplished under my direction and control.

Bechtel Corporation Company Name	Don R. Walker Signature
July 10, 1989 Date	Don R. Walker Typed Name
Norwalk, California (City) (State)	Micrographics Operations Supervisor Title

CITY OF LOS ANGELES DEPARTMENT OF WATER AND POWER
 DECLARATION OF INTENT AND PURPOSE

The document appearing in this microimage is an actual record of the Power System Services Division, Los Angeles Department of Water and Power. Filing of this document is in accordance with City Administrative Code, Division 12, "Records", and is part of a planned program of records retention.

Don R. Walker Bechtel Corporation	is authorized to photographically reproduce records for the City of Los Angeles Department of Water and Power.
Thomas H. McGuinness Signature	9/16/89 Date
Thomas H. McGuinness Typed Name	Los Angeles, California Place
Assistant Engineer of System Services Title	