


OTAT	8
IGD	5
IGC	8
HD	
T	
UD	1
30S	3
JOED	1
SAMUEL	1

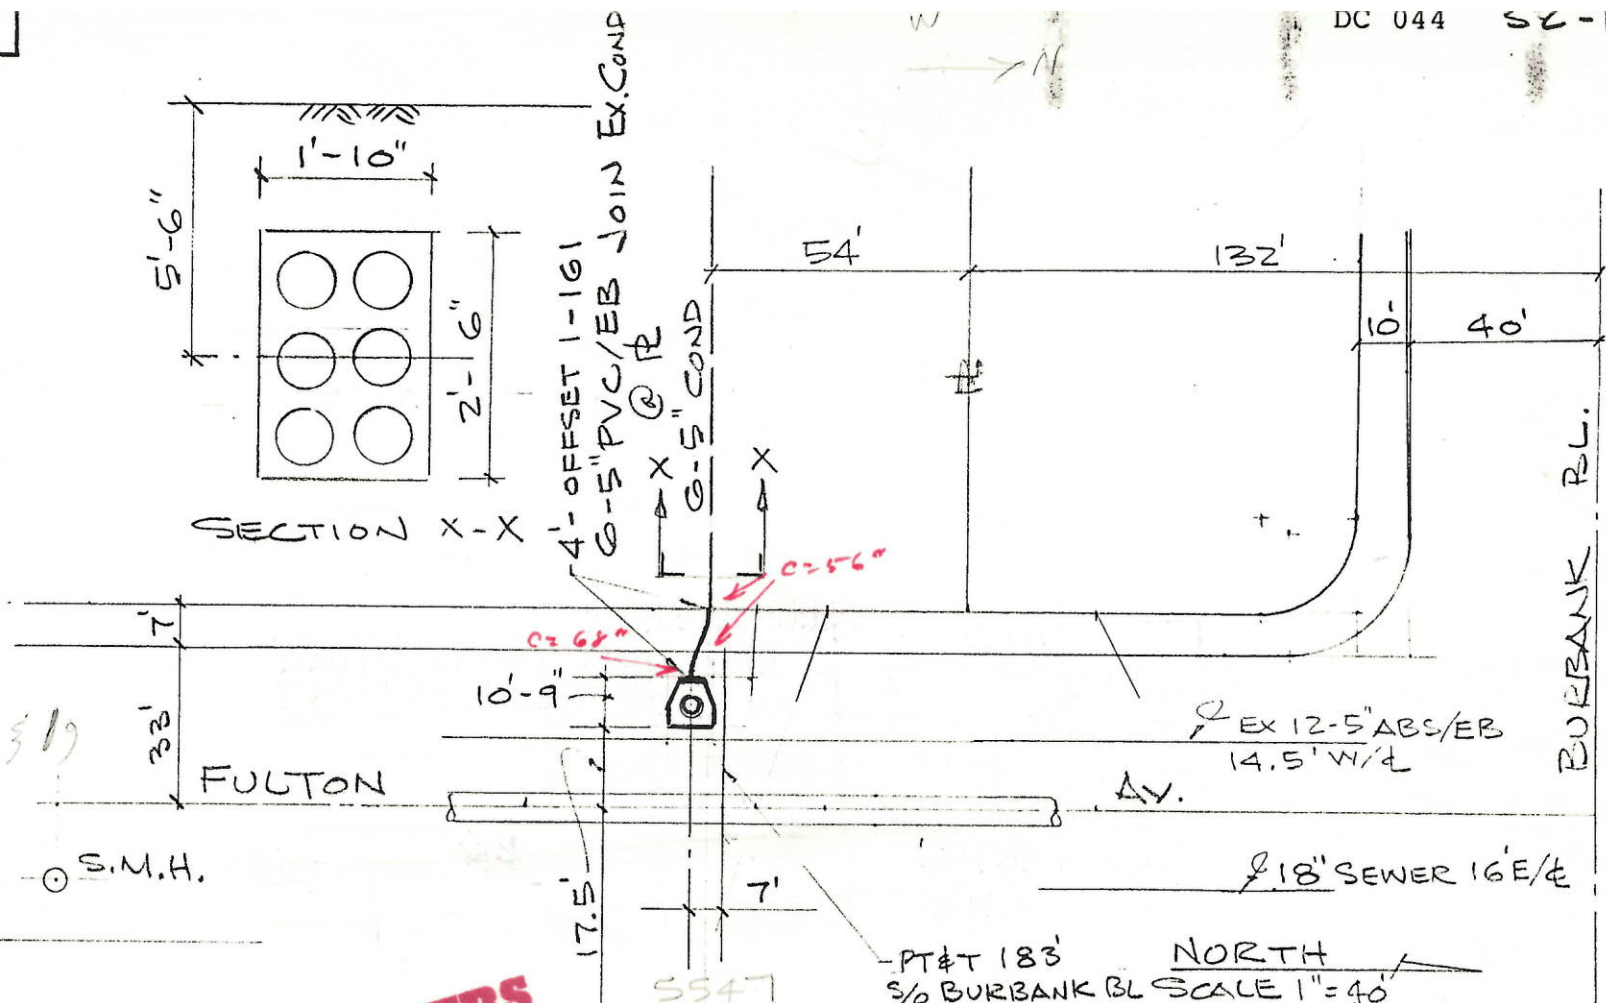

71-1, 5, 17, 319

S.M.H.

ENGINEERS COPY

MH 5541 1/2
G-328
(9'-10") x (9'-10")
SET 7-10-84
LEMS 3-11'3"

PT & T 183
S/O BURBANK BL
NORTH
SCALE 1" = 40'

FOREMAN'S PRINT

KAR 20 (REM 22) QAUT 6 PERMIT 362230

COMPLETED
DATE 7-12-84
BY Lemos

51- ISSUED 9-7-83	
CITY OF LOS ANGELES DEPARTMENT OF WATER & POWER UNDERGROUND DESIGN SECTION	
4.8KV MANHOLE 5541 1/2 FULTON AV.	
DESIGN TANAKA	DATE 8-9-83
O.K. C.P. Masuo	A.J. N° 18354
APPROVED A.R. Shockey SR. ELEC. ENGINEER	

DATE	INIT'L	REVISION	APP'V'D.
CONDUIT	COMP. DATE	BY	SPLICING
ABLE	COMP. DATE	BY	

SYSTEM MAP 300-20P
PRIMARY CIRCUIT
COMMERCIAL

NOV 20 1984