


MATCH LINE - SEE SHEET UE-6 -
STA 375+00

MATCH LINE - SEE ABOVE RIGHT -
STA 390+00

MATCH LINE - SEE BELOW LEFT - STA 390+00

MATCH LINE - SEE SHEET UE-9 -
STA 405+00

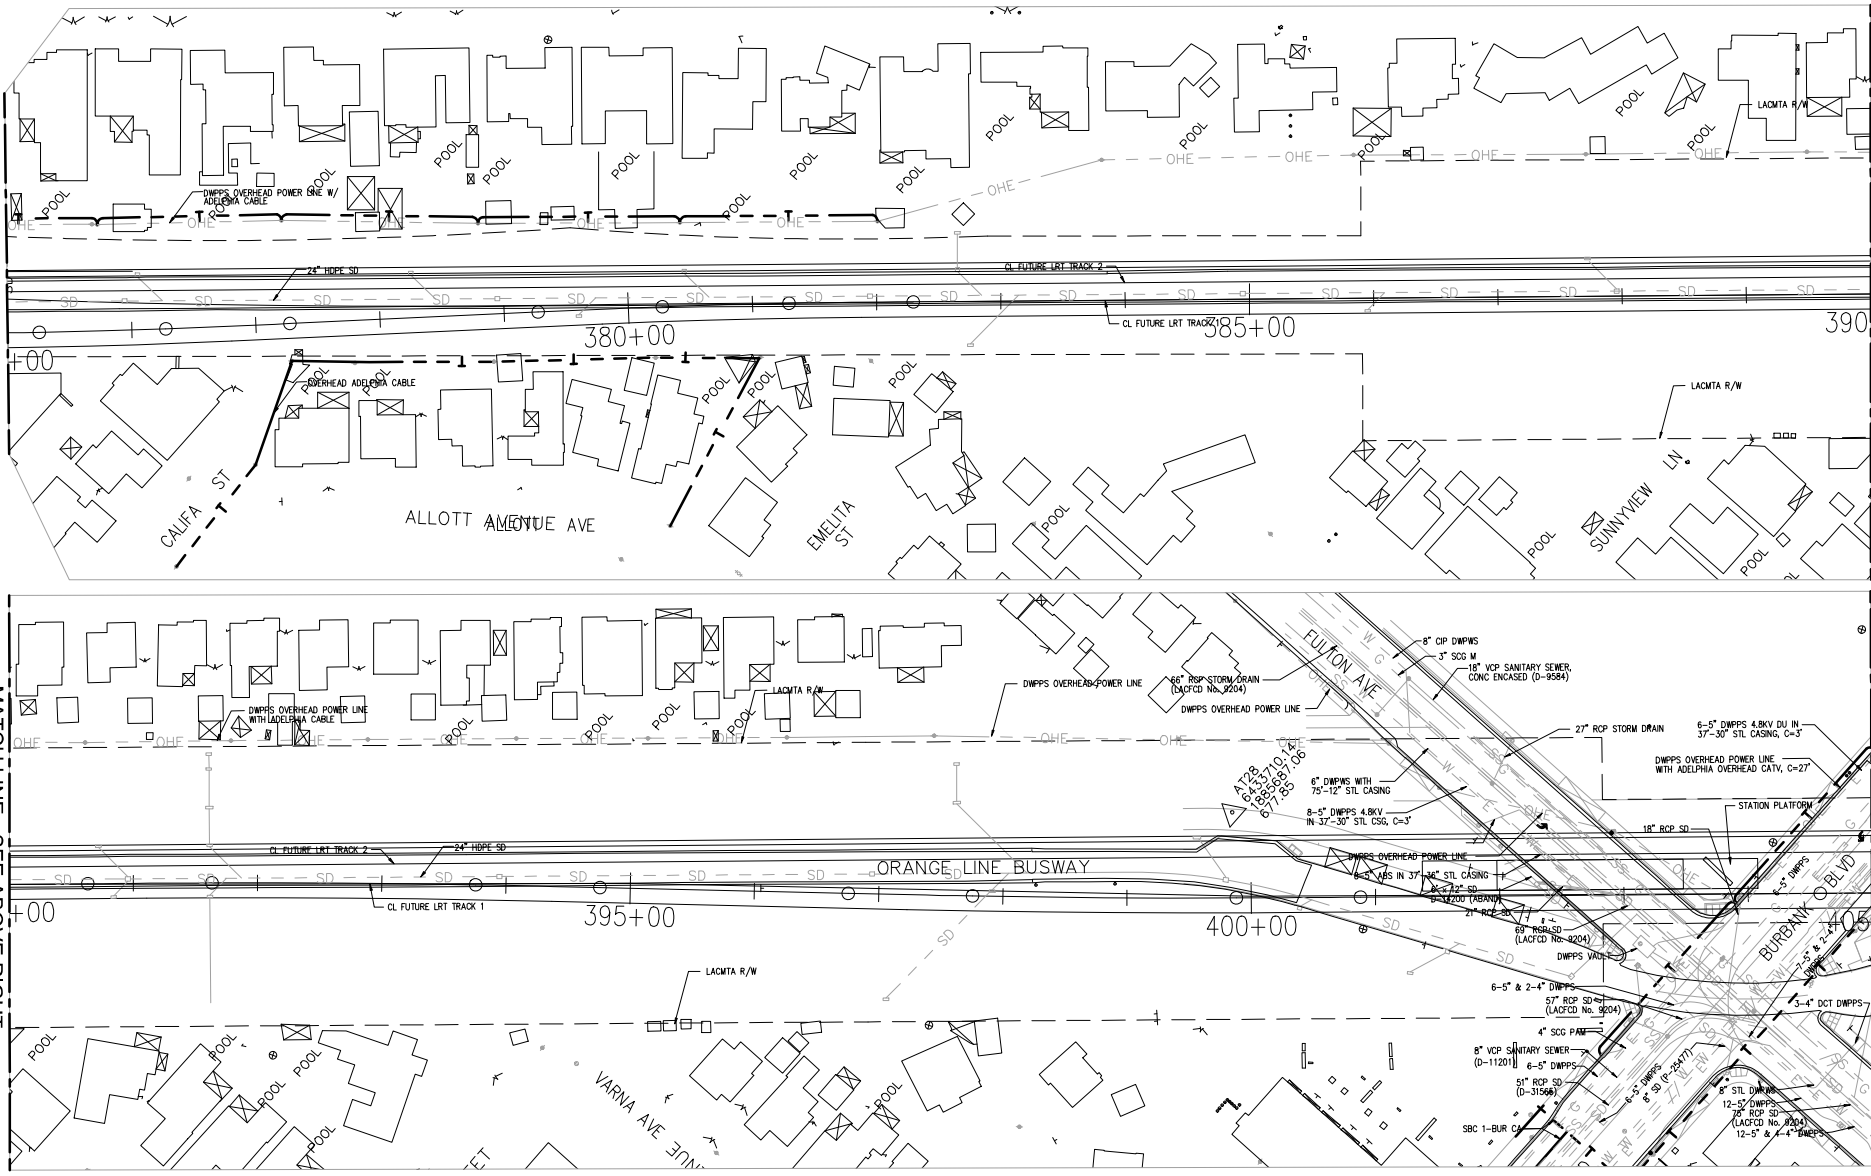

SCALE	1" = 50'
DATE	03/22/2018
PROJECT	UE-8
DESCRIPTION	EXISTING TELECOMMUNICATION LACMTA R/W LACMTA ORANGE LINE ALIGNMENT


Metro

LOS ANGELES COUNTY
METROPOLITAN TRANSPORTATION AUTHORITY

MOTT
MACDONALD




BA INC

DESIGNED BY
 10000 W. 10TH AVE., SUITE 1000, DENVER, CO 80202
 (303) 733-1000

METRO ORANGE LINE GRADE SEPARATIONS PROJECT
 EXISTING TELECOMMUNICATION EXHIBIT
 AT&T
 STA 375+00 TO 405+00

GRAPHIC SCALE
 0 25 50 100
 SCALE: 1"=50'