


MATCH LINE - SEE SHEET UE-6 -
STA 375+00

MATCH LINE - SEE ABOVE RIGHT -
STA 390+00

MATCH LINE - SEE BELOW LEFT - STA 390+00

MATCH LINE - SEE SHEET UE-9 -
STA 405+00

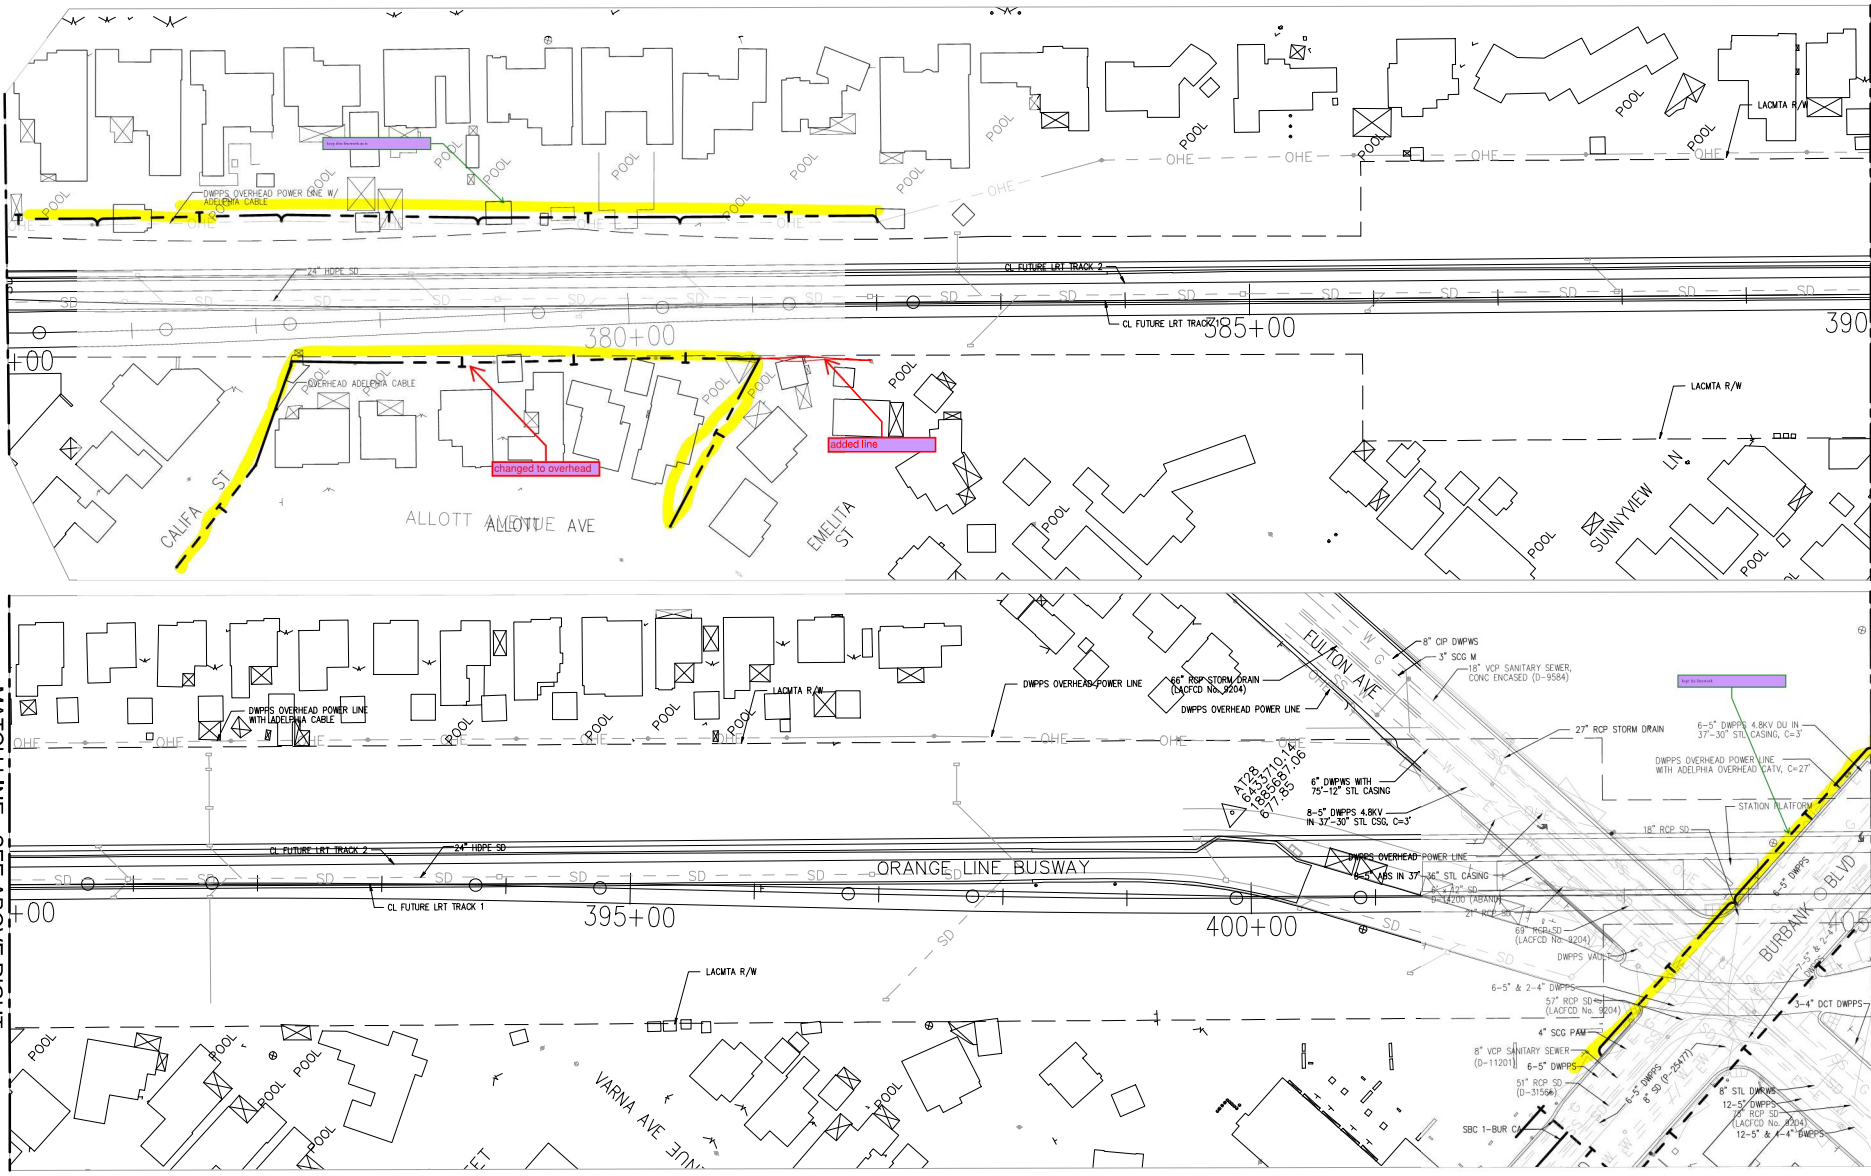

SCALE	1" = 50'
DATE	03/22/2018
LEGEND	
---	EXISTING TELECOMMUNICATION
- - -	LACMTA R/W
- - -	LACMTA ORANGE LINE ALIGNMENT



LOS ANGELES COUNTY
METROPOLITAN TRANSPORTATION AUTHORITY

MOTT
MACDONALD

M
M



BA INC

METRO ORANGE LINE GRADE SEPARATIONS PROJECT
EXISTING TELECOMMUNICATION EXHIBIT
CHARTER
STA 375+00 TO 405+00

