


MATCH LINE - SEE SHEET UE-6 -
STA 375+00

MATCH LINE - SEE ABOVE RIGHT -
STA 390+00

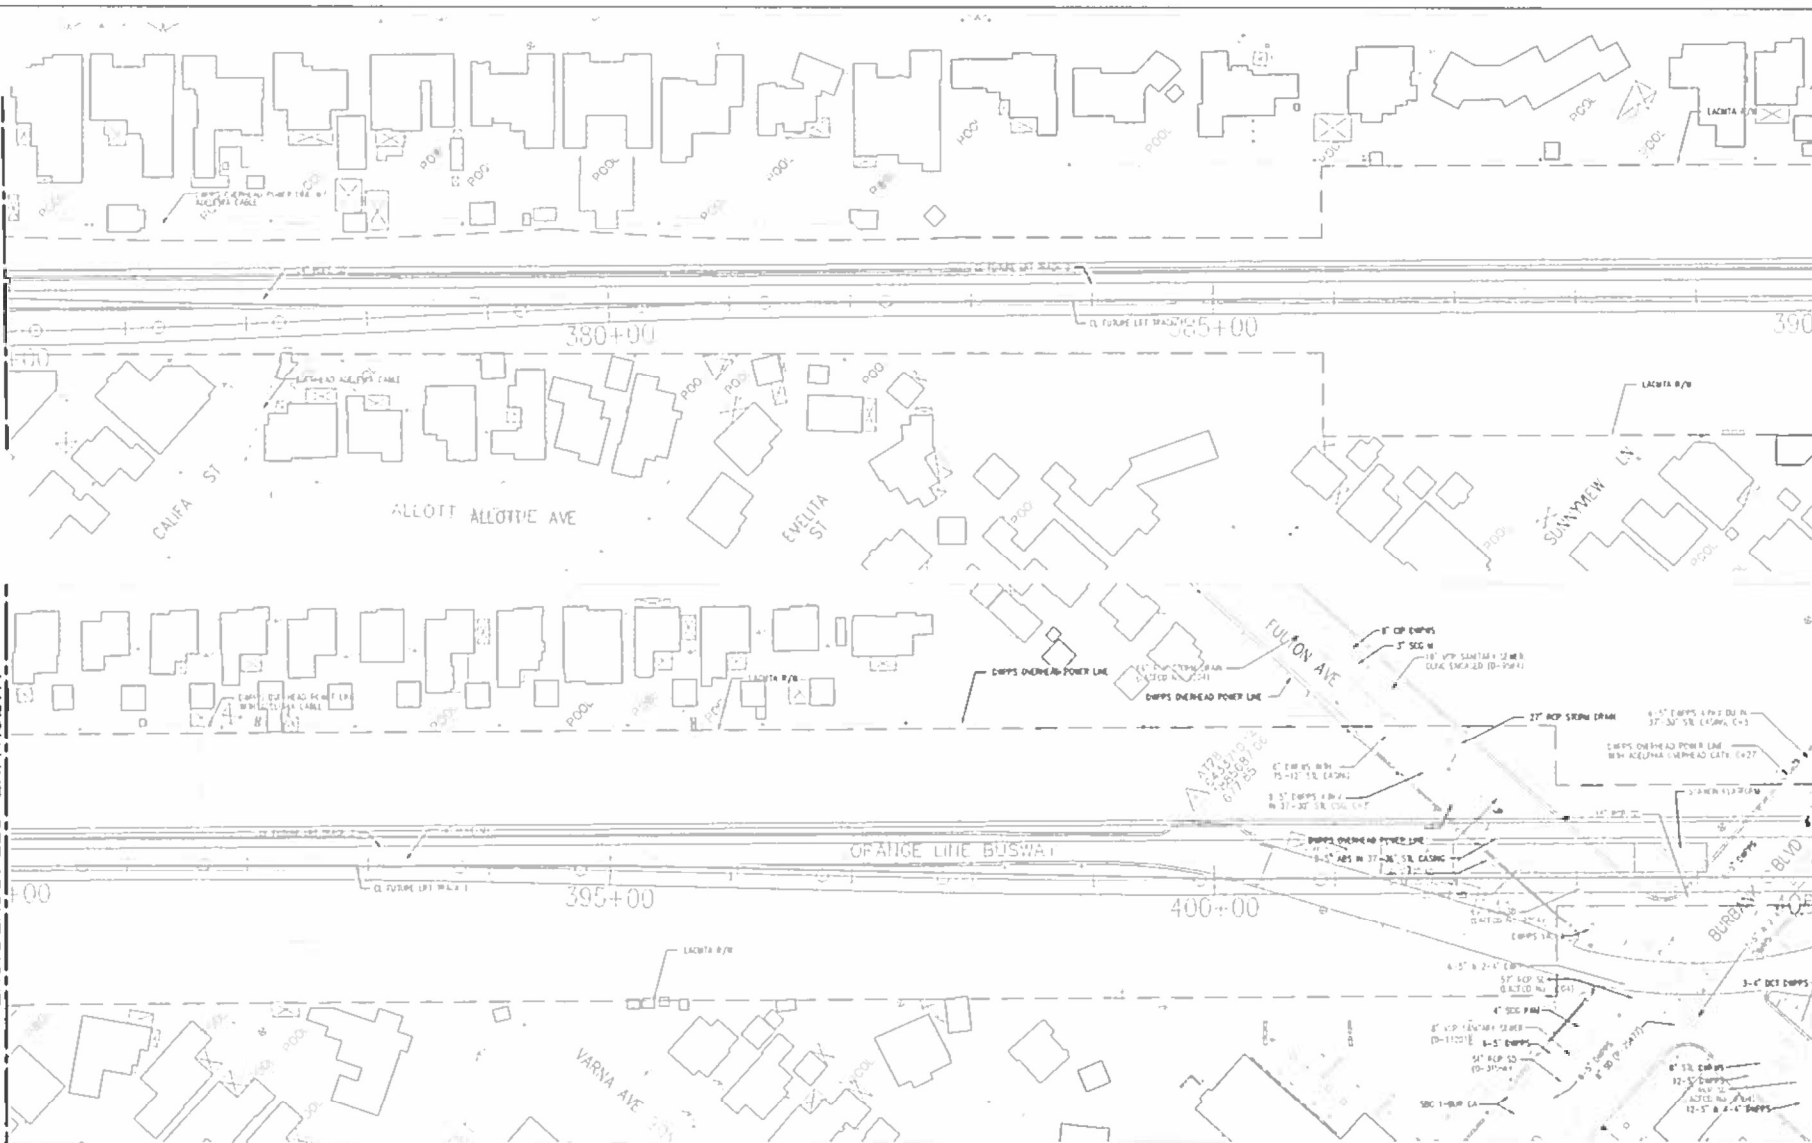

MATCH LINE - SEE BELOW LEFT- STA 390+00

MATCH LINE - SEE SHEET UE-9 -
STA 405+00

1" = 50' UE-8 03/22/2018	LEGEND --- EXISTING OIL --- LACMTA R/W --- LACMTA ORANGE LINE ALIGNMENT	LOS ANGELES COUNTY Metro METROPOLITAN TRANSPORTATION AUTHORITY	MOTT MACDONALD M M	BA INC	METRO ORANGE LINE GRADE SEPARATIONS PROJECT EXISTING OIL EXHIBIT CHEVRON STA 375+00 TO 405+00	GRAPHIC SCALE 0 10 20 30 40 50 60 70 80 90 100 SCALE: 1"=50'
---	--	--	--	----------------------	---	--