


MATCH LINE - SEE SHEET UE-6 -
STA 375+00

MATCH LINE - SEE ABOVE RIGHT -
STA 390+00

MATCH LINE - SEE BELOW LEFT- STA 390+00

MATCH LINE - SEE SHEET UE-9 -
STA 405+00

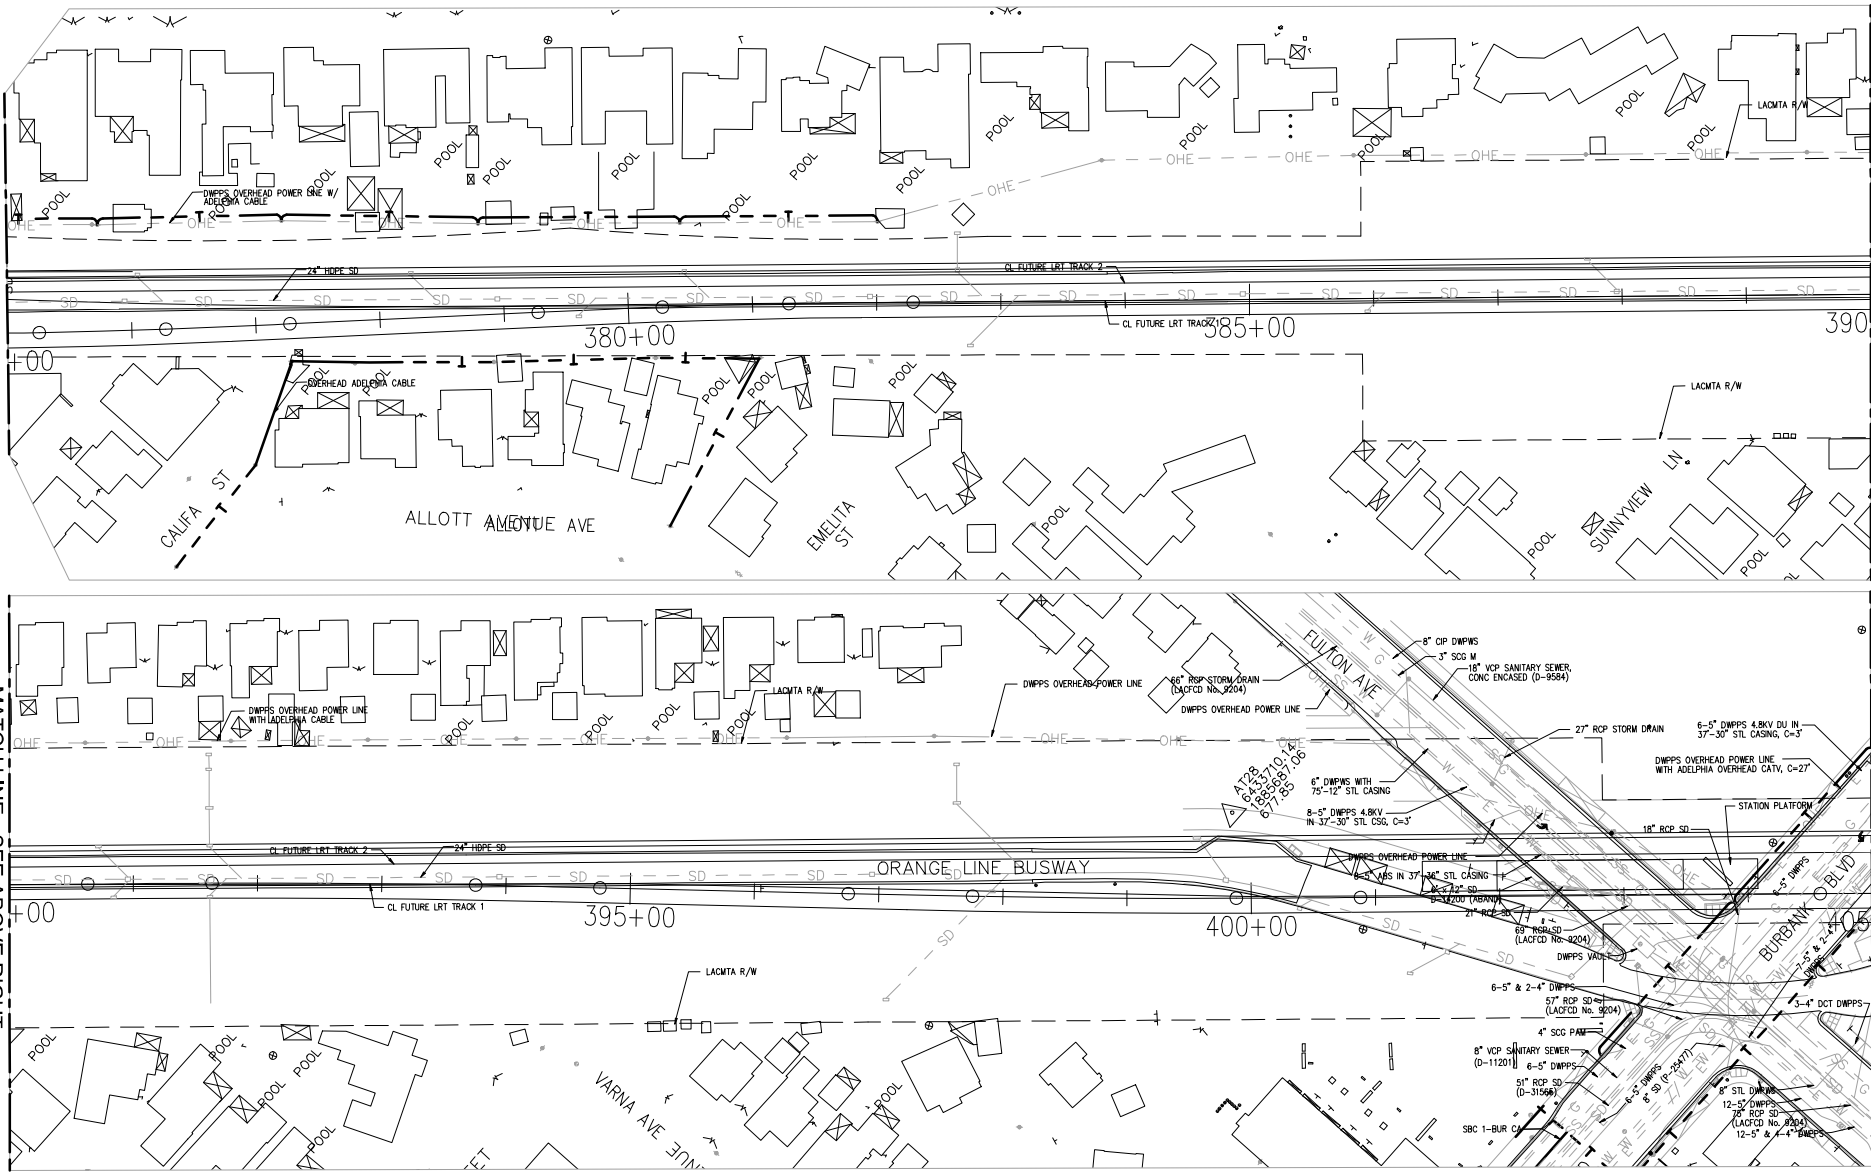

SCALE	1" = 50'
DATE	03/22/2018
PROJECT	UE-8
LEGEND	
---	EXISTING TELECOMMUNICATION
- - -	LACMTA R/W
- - -	LACMTA ORANGE LINE ALIGNMENT

**Metro**

LOS ANGELES COUNTY
METROPOLITAN TRANSPORTATION AUTHORITY

MOTT
MACDONALD



**BA INC**

INCORPORATED
1000 WEST 10TH STREET, SUITE 200, LOS ANGELES, CA 90057
PH: (213) 621-1111 FAX: (213) 621-1112

METRO ORANGE LINE GRADE SEPARATIONS PROJECT
EXISTING TELECOMMUNICATION EXHIBIT
NEXT GLAVEN (CROWN CASTLE)
STA 375+00 TO 405+00

GRAPHIC SCALE
0 25 50 100
SCALE: 1"=50'