



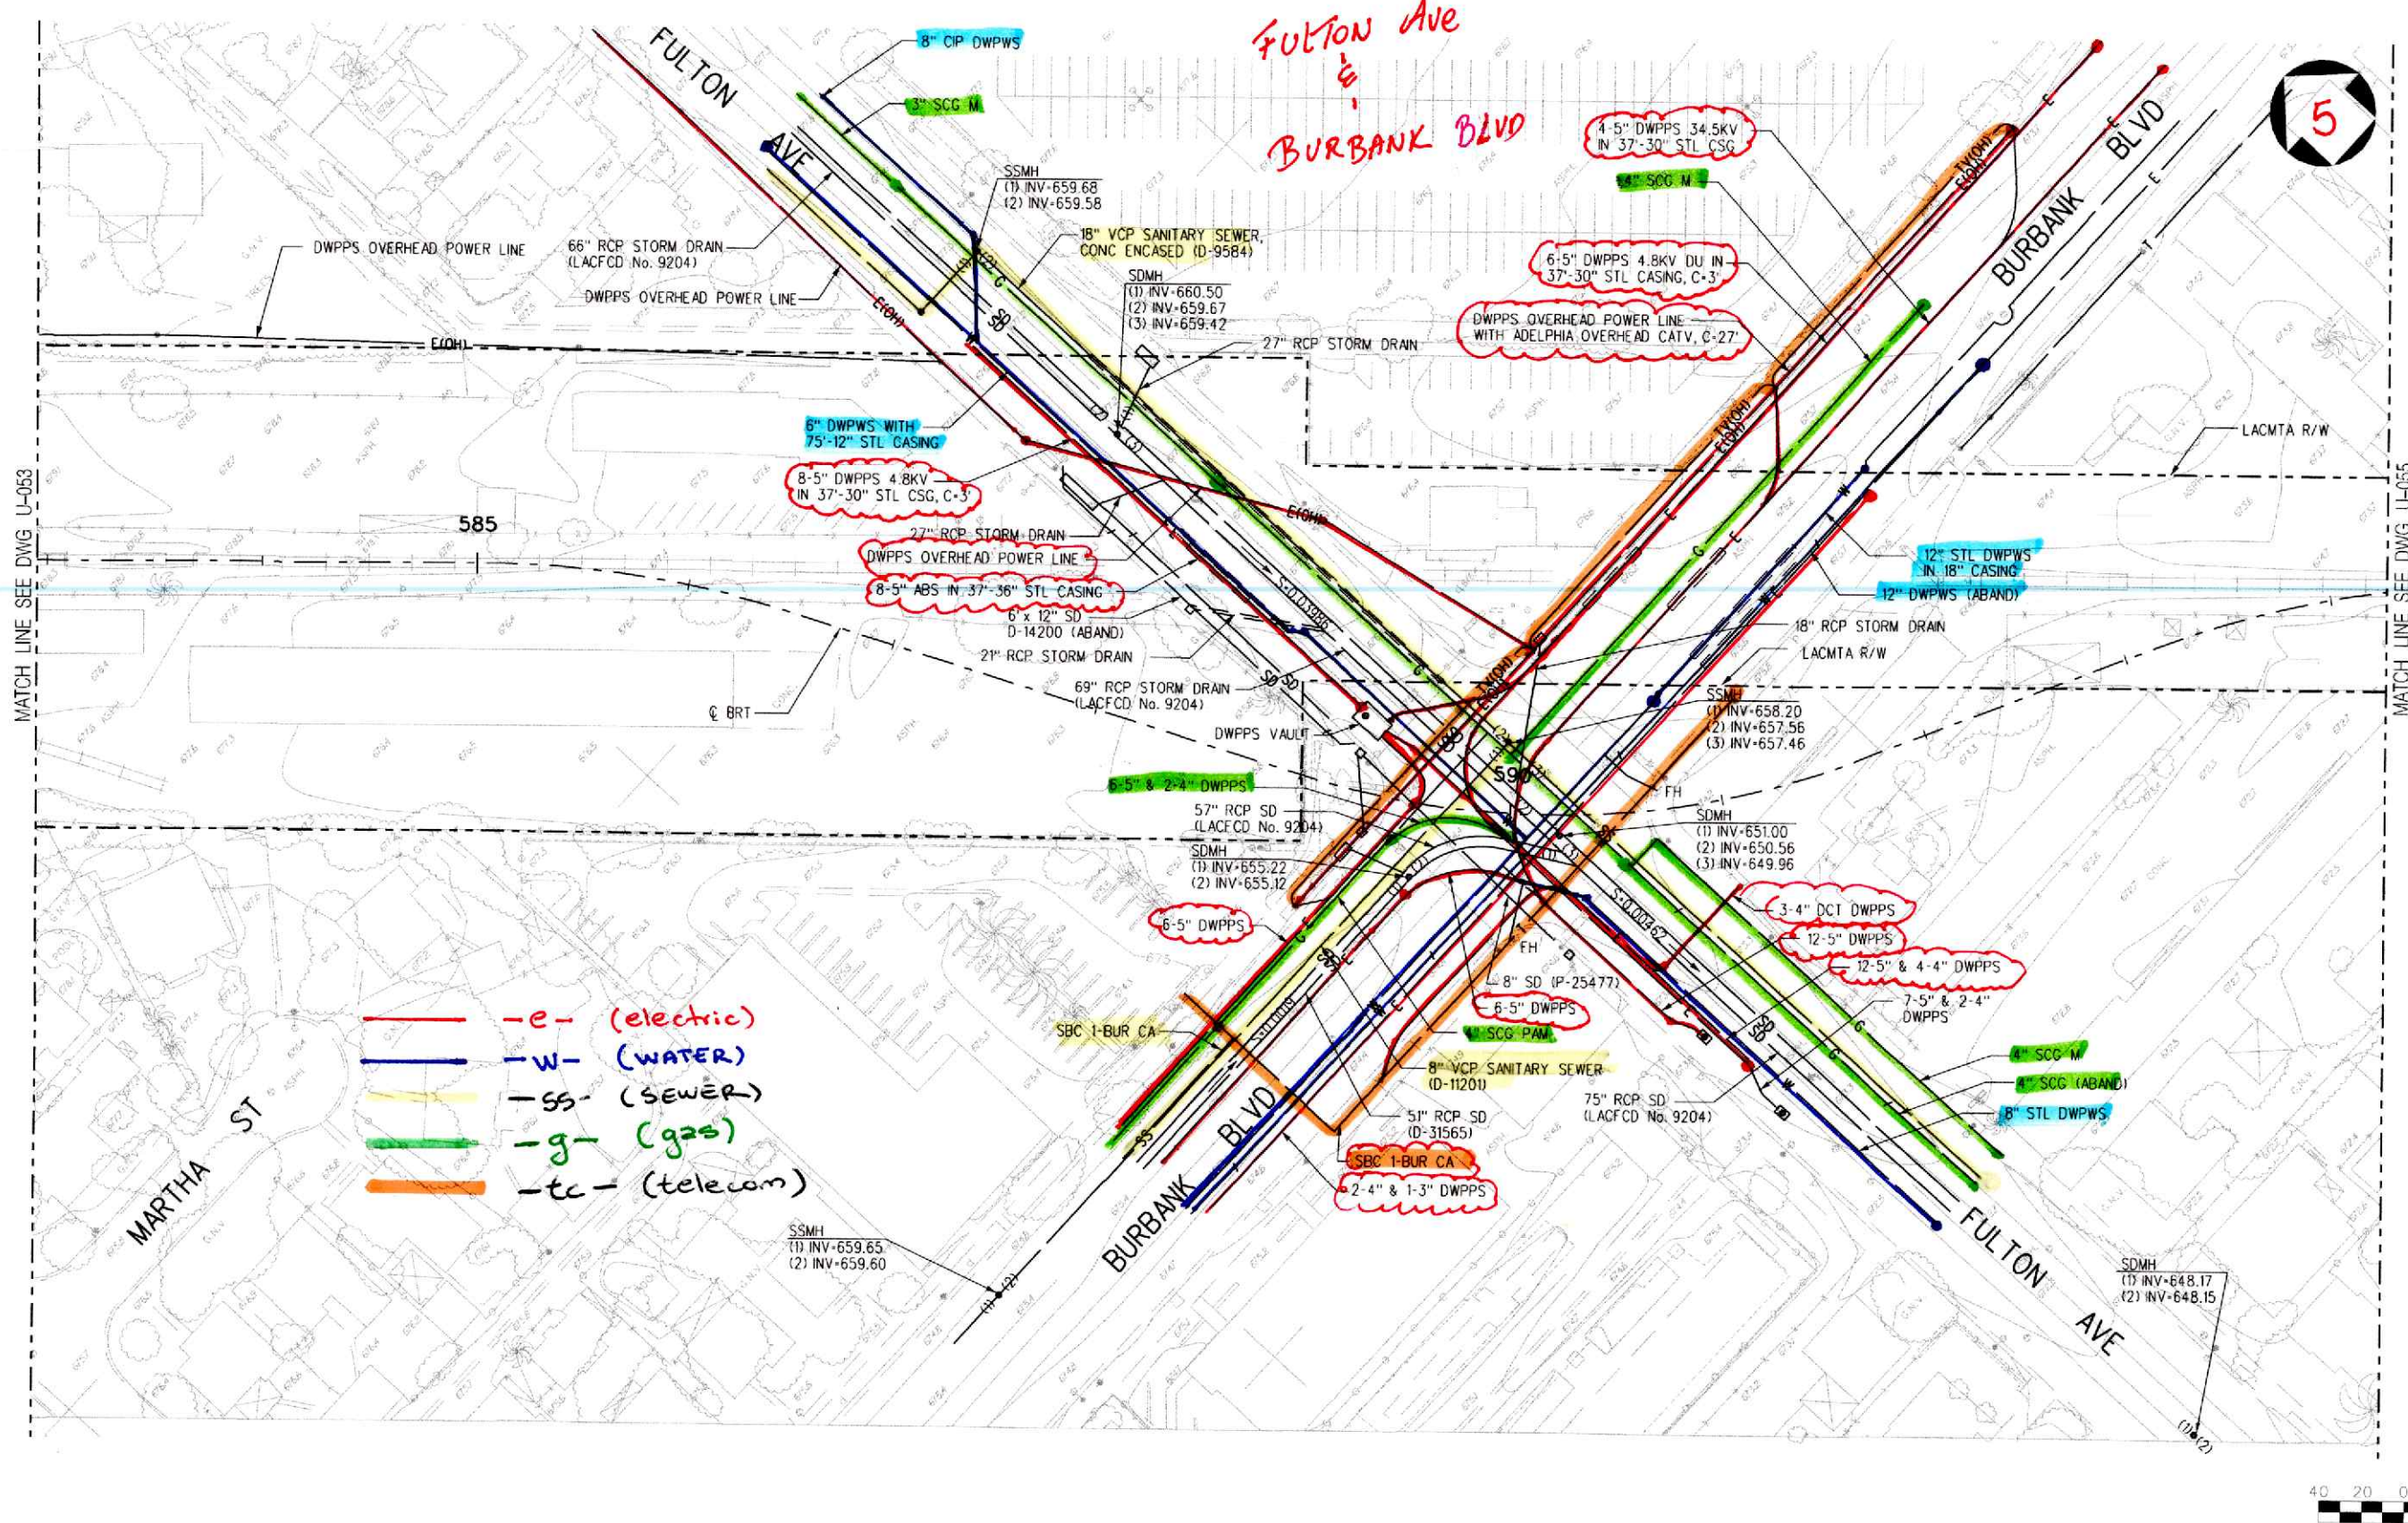

REV	DATE	BY	APP	REC NO	EXPIRES	SEAL HOLDER	DESCRIPTION
0	1/22/04	YX	BEJ	C59517	12/31/03	BRETT E. JONES	ISSUED FOR CONSTRUCTION - 1B

DESIGNED BY
S. KASSISIEH
DRAWN BY
M. CUTTER
CHECKED BY
S. YOUSEFIAN
IN CHARGE
B. JONES
DATE
11/07/03

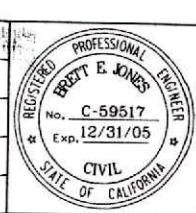

LOS ANGELES COUNTY METROPOLITAN TRANSPORTATION AUTHORITY
SAN FERNANDO VALLEY EAST-WEST BRT PROJECT

Washington Group International
 WASHINGTON GROUP INTERNATIONAL, INC.
 5805 SEPULVEDA BLVD., SUITE 500
 VAN NUYS, CA 91411

SHIMMICK
 OBAYASHI, JV
 5805 SEPULVEDA BLVD., SUITE 500
 VAN NUYS, CA 91411

NORTH HOLLYWOOD TO
 WARNER CENTER
 UTILITIES
 SHEET 51 OF 65

CONTRACT NO	C0675
DRAWING NO	U-054
SCALE	HORIZ. 1"=40'
SHEET NO	0

m:\bri\irvine\sheet\temp\utilities\U-054.pig 07/21/2006 08:44:59 AM