

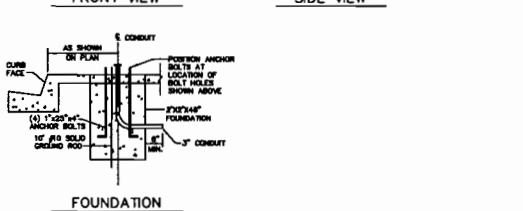
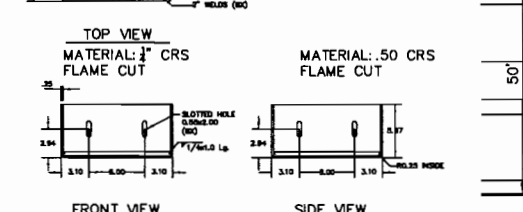


SIGNAL STANDARD SCHEDULE					
No.	TYPE	FOUND. TYPE	PED. PUSH BUTN TYPE	PHASE	REMARKS
(1)	CD954	F-2			20' M.A.
(2)	CD953C*	F-2	6"	3	15' M.A.
(3)	CD953C-7	F-2	6"	3	15' M.A.
(4)	9	F-1			
(5)	CD953C*	F-2			15' M.A.
(6)	CD953C*	F-2			15' M.A.
(7)	CD954	F-2			15' M.A.
(8)	1	F-1			
(9)	CD954	F-2			20' M.A.
(10)	1A	F-1			PHOTO ENFORCEMENT AUXILIARY FLASH UNIT
(11)	CD954	F-2			15' M.A.
(12)	1	F-1			
(13)	C-2	CIDH***			VIDEO CAMERA W/ 6' CAMERA ARM & CUSTOM 12' M.A.
(14)	1A	F-1			PHOTO ENFORCEMENT AUXILIARY FLASH UNIT
(15)	CD954	F-2			15' M.A.
(16)	CD953C*	F-2			15' M.A.
(17)	CAMERA POLE**				PHOTO ENFORCEMENT CAMERA POLE
(18)	CAMERA POLE**				PHOTO ENFORCEMENT CAMERA POLE

* For reference only, see separate Street Lighting sheet
 ** See Detail "E"
 *** CIDH PILE Foundation as per LADOT Std. Dwg. No. S-52.1-4B.

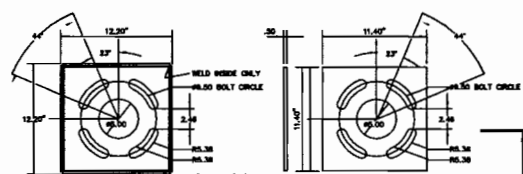

DETAIL "E"
NOT TO SCALE

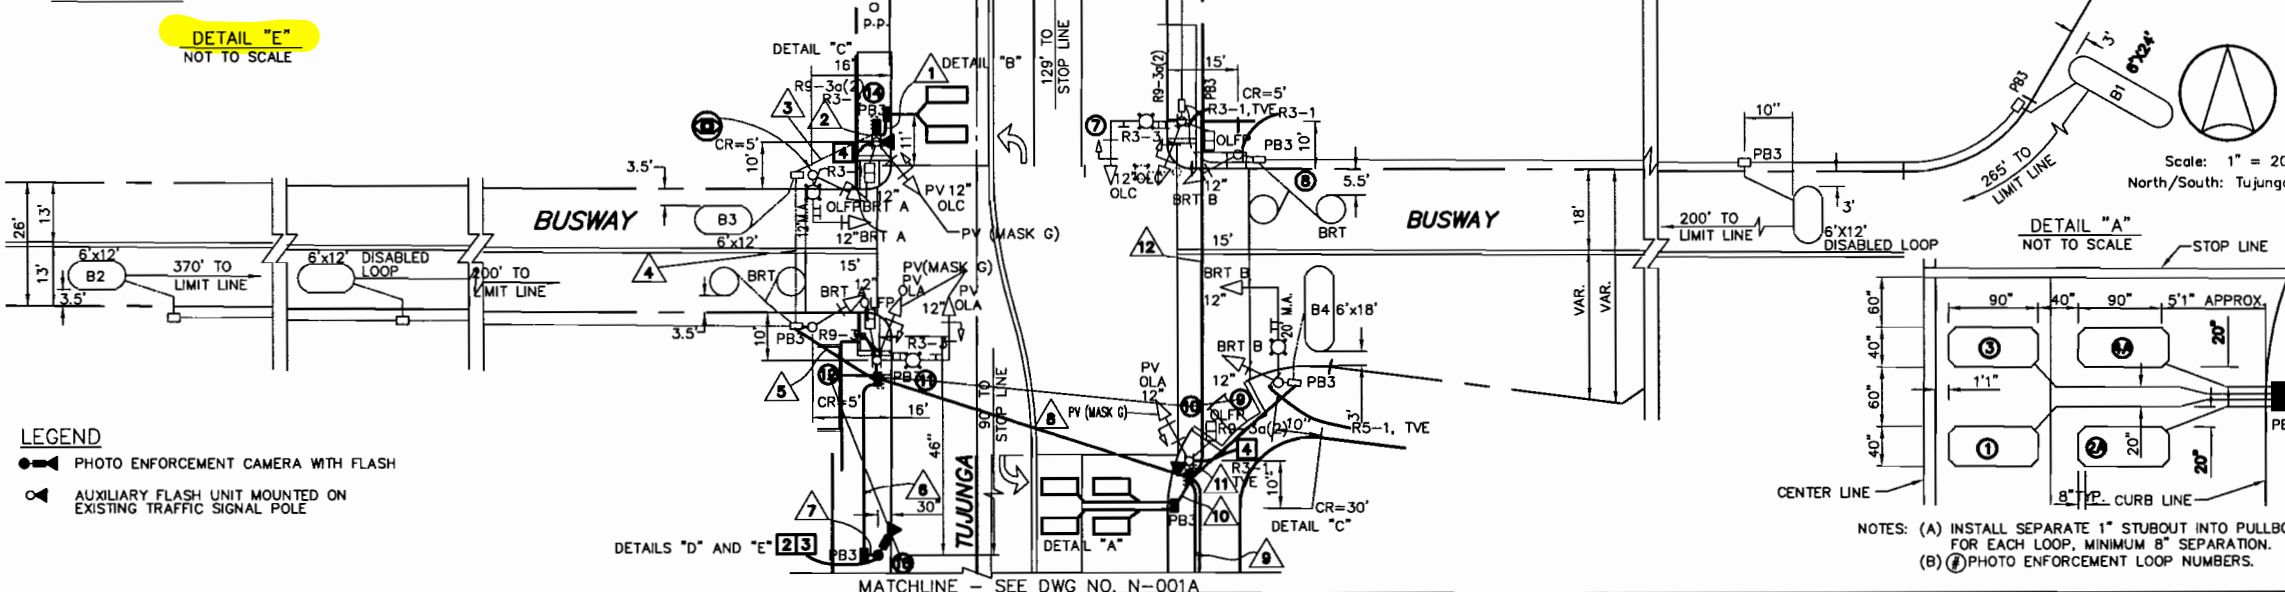

LEGEND

● PHOTO ENFORCEMENT CAMERA WITH FLASH

○ AUXILIARY FLASH UNIT MOUNTED ON EXISTING TRAFFIC SIGNAL POLE

 KI HYUK KIM No. NO. TR2255 Exp. 06-30-06 TRAFFIC STATE OF CALIFORNIA								DESIGNED BY K. KIM	 JAMES P. CURRY No. NO. 22336 Exp. 09-30-2007 CIVIL STATE OF CALIFORNIA
								DRAWN BY D. BARRAZA	
								CHECKED BY J. CURRY	
								IN CHARGE J. CURRY	
								DATE	
REV	DATE	BY	APP	REG NO	EXPIRES	SEAL HOLDER	DESCRIPTION		

LOS ANGELES COUNTY METROPOLITAN TRANSPORTATION AUTHORITY
 SAN FERNANDO VALLEY EAST-WEST BRT PROJECT

ACS GOVERNMENT SOLUTIONS

PB PREPARED BY
 PB FARRADYNE
 444 S. FARRADYNE
 LOS ANGELES, CA 90071
 TEL: (213) 223-2222
 FAX: (213) 223-2222

REVIEWED BY: _____

CONDUCTOR SCHEDULE											
SIZE No.	CABLE / WIRE	RUN									
3C12	PHOTO ENFORCEMENT SERVICE										
5C14	PHOTO ENFORCEMENT ENFORCED RED AND YELLOW										
2C12	PHOTO ENFORCEMENT DLC	2	2	2	2	2	2	4	4	4	4
5C14	PHOTO ENFORCEMENT AUXILIARY FLASH	1	1	1	1	1	1	1	1	1	1
CONDUIT SIZE		2"	5"	5"	3"	2"	3"	3"	5"	5"	3"
NEW/EXISTING		N	E	E	E	N	E	N	E	E	N

(*) IMSA 50-2
 (**) IMSA 40-2

NOTICE TO CONTRACTOR
 SEE DWG. NO. N-001A

- NOTES:
- SEMI-ACTUATED OPERATION (ATSAC 2070 CONTROLLER WITH TRANSIT PRIORITY IN 332 CABINET)
 - TUJUNGA AVE. SB & W/S PED. XING (AT CHANDLER BLVD NORTH RDWY)
 - CHANDLER BLVD (NORTH RDWY) WB, WB LT & N/S PED XING (EXCLUSIVE PHASE)
 - TUJUNGA AVE ES PED XING (AT CHANDLER BLVD NORTH RDWY)
 - TUJUNGA AVE NB & E/S PED XING (AT CHANDLER BLVD SOUTH RDWY)
 - CHANDLER BLVD (SOUTH RDWY) EB & S/S PED XING
 - CHANDLER BLVD (SOUTH RDWY) WB RT, WB LT & WS PED XING
 - OLA - (#2 & #3) TUJUNGA AVE SB AT BRT
 - OLB - (#2 & #3) TUJUNGA AVE SB (AT CHANDLER BLVD SOUTH RDWY)
 - OLC - (#4 & #6) TUJUNGA AVE NB AT BRT
 - OLD - (#4 & #6) TUJUNGA AVE NB (AT CHANDLER BLVD NORTH RDWY)
 - OLE - (#7) CHANDLER BLVD (SOUTH RDWY) EB LT
 - OLF - (#3 & #4 & #6) TUJUNGA AVE E/S & W/S PED XING AT BRT
 - BRT A - BUSWAY WB
 - BRT B - BUSWAY EB
 - DIRECT WIRE (CABLE) INTERCONNECT VENTURA 2B ATSAC SYSTEM
 - CONTRACTOR TO INSTALL PHOTO ENFORCEMENT CAMERA POLE, FURNISHED BY ACS, ON FOUNDATION PER DETAIL "E". CONNECT CAMERA SERVICE, BRT RED AND YELLOW SENSE WIRES, AUXILIARY FLASH POWER AND TRIGGER CONDUCTORS, DETECTOR LEAD-IN CABLES, AND GROUND AT CAMERA POLE TERMINAL BLOCK.
 - CONTRACTOR TO INSTALL GROUND ROD AND CONNECT 10AWG SOLID GROUND WIRE TO PHOTO ENFORCEMENT CAMERA POLE TERMINAL BLOCK GROUND LUG.
 - CONTRACTOR TO FURNISH AND INSTALL FLASH UNIT MOUNTING ARM ON EXISTING LADOT TYPE 1A TRAFFIC SIGNAL POLE AT MINIMUM 10'-0" ABOVE SIDEWALK GRADE, AND INSTALL AUXILIARY FLASH UNIT FURNISHED BY ACS. ADJUST EXISTING SIGNS ATTACHED TO TRAFFIC SIGNAL POLE, AS NEEDED, TO ALLOW FOR FLASH UNIT INSTALLATION. MAKE CONNECTIONS AT FLASH UNIT TERMINAL BLOCK FOR FLASH UNIT POWER AND TRIGGER CONDUCTORS.
 - CONTRACTOR TO INSTALL ACS-FURNISHED PHOTO ENFORCEMENT WARNING SIGN AND SIGN POLE, PRIOR TO ACTIVATION OF SYSTEM.
 - CONTRACTOR TO PROTECT IN PLACE EXISTING TRAFFIC SIGNAL PULLBOXES, CONDUITS, AND CONDUCTORS DURING CONSTRUCTION. REPLACE ANY PULLBOX LIDS, PULLBOXES, CONDUITS, OR CONDUCTORS DAMAGED DURING CONSTRUCTION AT CONTRACTOR'S SOLE EXPENSE.
 - PHOTO ENFORCEMENT LOOPS SHALL BE 3 TURNS IMSA 51-7 14AWG WIRE IN MAXIMUM 2" DEEP, 1/4-INCH WIDE SAWCUT. LOOP LEAD-IN WIRES TO BE TWISTED MINIMUM FOUR TURNS PER FOOT.
 - CONTRACTOR TO SPlice LOOP WIRES TO DLC AT PULLBOX BY CRIMPING THEN SOLDERING COMPRESSION FITTING TO CONDUCTOR ENDS, THEN ENCASE IN COMPRESSION FITTING AND CONDUCTOR ENDS WITH HEAT SHRINK TUBING AND VINYL ELECTRICAL TAPE.
 - CONTRACTOR TO CONTACT RAY MAY AT (619) 247-1252 FOR ACS-FURNISHED CAMERA POLE AND AUXILIARY FLASH UNIT INSTALLATION AND CONDUCTOR TERMINATION DETAILS.
 - CONTRACTOR TO CONTACT TODD REDMOND AT (213) 439-6219 FOR PICK-UP OF ACS-FURNISHED EQUIPMENT FIVE (5) WORKING DAYS PRIOR TO PICK-UP DATE.

THIS PLAN SUPERSEDES PLAN
 SIGNED ON MARCH 19, 2006

MTA - SAN FERNANDO VALLEY RAPID BUS SYSTEM (PHOTO ENFORCEMENT)

REVIEWED	20	RECOMMENDED	20	ACCEPTED	
Transportation Engineer		Senior Transportation Engineer		Principal Transportation Engineer	

CITY OF LOS ANGELES
 DEPARTMENT OF TRANSPORTATION
 GLORIA JEFF, GENERAL MANAGER

TITLE
CHANDLER BLVD., TUJUNGA AVE. & BUSWAY

Condition As Of:
 LADOT Engineer:
 District: EAST VALLEY
 Thomas Guide: 562-J2

References

File Name	32810-R2.DWG	Intersection No.	32810	Project No.	74720
-----------	--------------	------------------	-------	-------------	-------

NOTICE: IF PLAN HAS NOT BEEN IMPLEMENTED WITHIN TWO (2) YEARS OF THE ACCEPTANCE DATE, IT MUST BE RE-SUBMITTED TO LADOT SIGNAL DESIGN SECTION FOR REVIEW AND APPROVAL.

METRO ORANGE LINE PHOTO ENFORCEMENT SYSTEM
 INSTALLATION PLAN
 CHANDLER BLVD., TUJUNGA AVE. AND BUSWAY

SEGMENT NO

DRAWING NO
 N-001B

SCALE
 1" = 20'

SHEET NO