



EP-5 UGC-8 CES-2 UTD-3
UGD-6 UTL-6 VUD-1

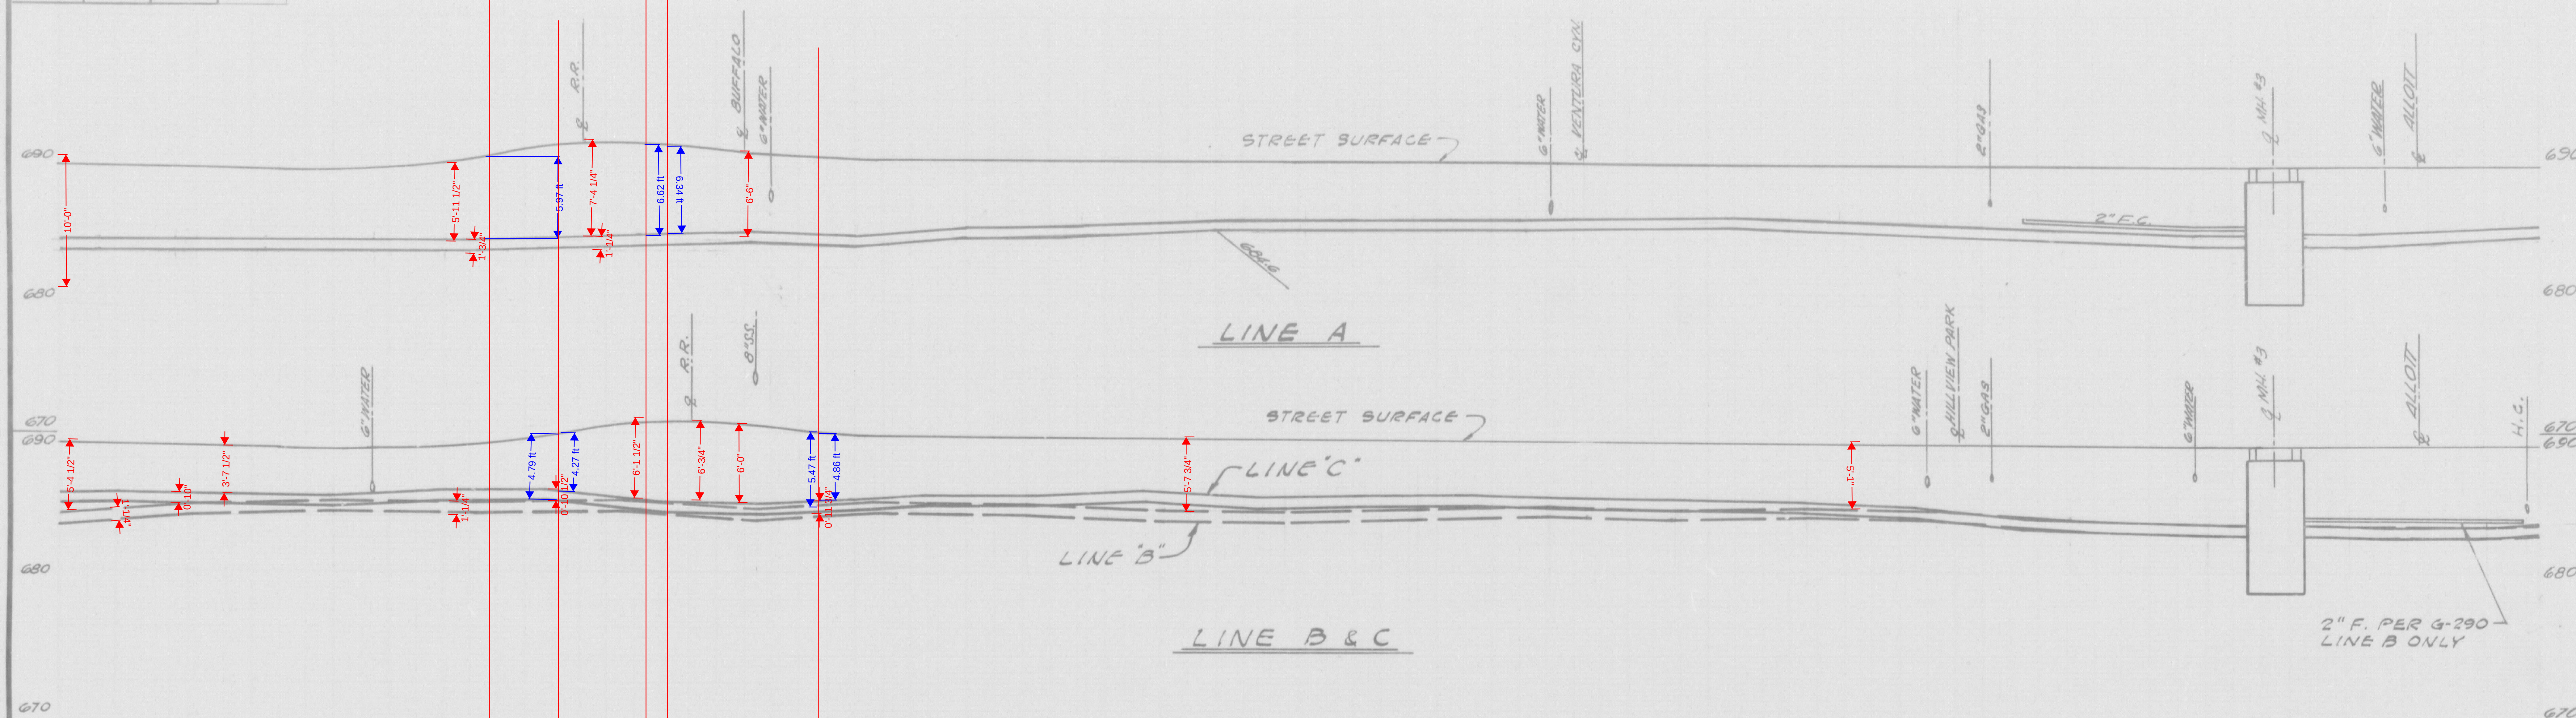

SCALE:
HOR. 1" = 40'
VERT. 1" = 8'

NOTE:
NO EXCAVATION WITHIN
10' OF RAILROAD LICENSE
AGREEMENT E-60548

INSTALL THERMOCOUPLE
AND POTENTIAL LEADS
AS PER DWG. G-277.

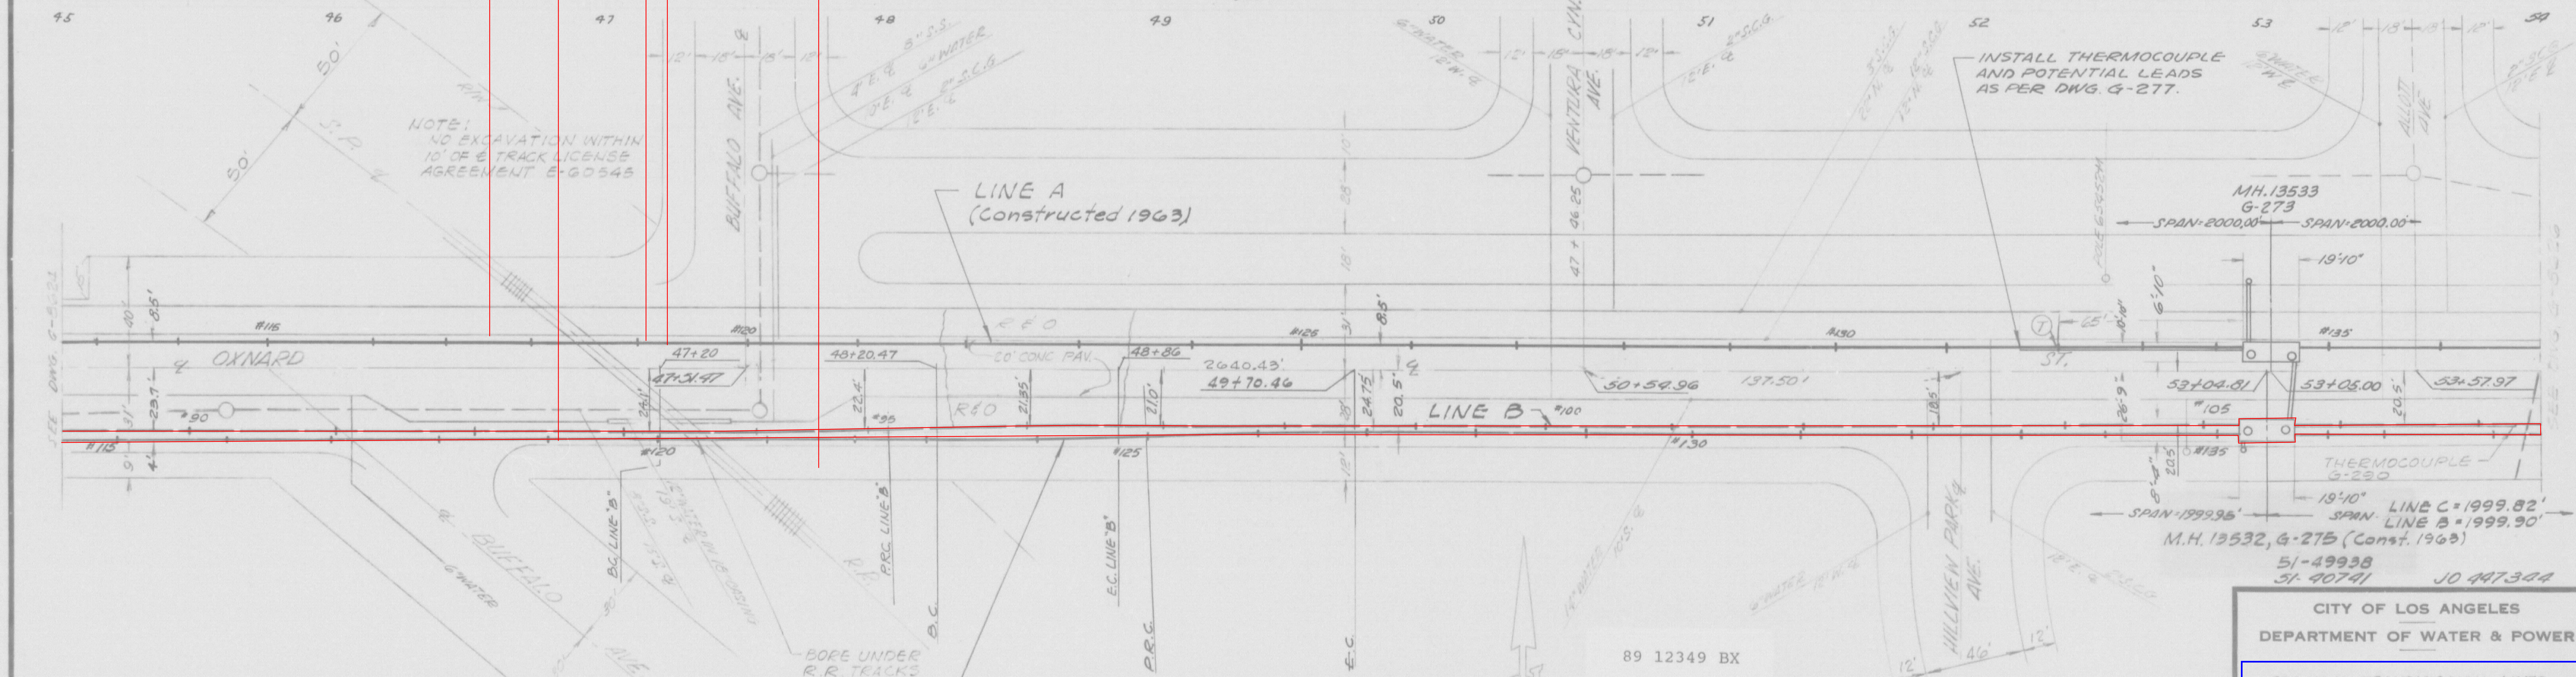

DATE	INITIAL	REVISION	APPROVED
1/1/68	MG	REVISED TO CONST.	
1/1/68	JO	LINE B AUTHORIZED	
1/1/68	MG	REVISED TO CONSTRUCTION	LHC
1/1/68	MG	STATIONING AND ALONG CONDUIT LINE	
1/1/68	U.O.	ADDED THERMOCOUPLE W/O M.H.'S	

F.B. 1367 FOR PIPE JOINTS LINE A
F.B. 1380 " " " LINE C
F.B. 1456 " " " LINE B

LINE B
PERMIT 376523
ISSUED 8-1-68

LINE A & C
PERMIT NO. 328390-92
ISSUED 9-12-62

CITY OF LOS ANGELES DEPARTMENT OF WATER & POWER	
230 KV. LIG. TRANSMISSION LINES OXNARD ST. BUFFALO AVE TO HILLVIEW PARK AVE	
DESIGNED BY: M.H. FOOTE	DRAWN BY: TAYLOR
DATE: APR 22 1968	O.K. [Signature]
APPROVED: [Signature]	G-8625

CERTIFICATE OF AUTHENTICITY

THIS IS TO CERTIFY that this microimage is a true and complete reproduction of the City of Los Angeles, Department of Water and Power records as delivered during the normal course of business. The photographic process used for the microfilming of this document was accomplished in a manner and on microfilm which meets the City of Los Angeles Records Management Program requirements for permanent micrographic reproductions and was accomplished under my direction and control.

Bechtel Corporation

Don R. Walker

CITY OF LOS ANGELES DEPARTMENT OF WATER AND POWER DECLARATION OF INTENT AND PURPOSE

The document appearing in this microimage is an actual record of the Power System Services Division, Los Angeles Department of Water and Power. Filming of this document is in accordance with City Administrative Code, Division 12, "Records", and is part of a planned program of records retention.

Don R. Walker, Bechtel Corporation, is authorized to photographically reproduce records for the City of Los Angeles Department of Water and Power.

Thomas W. [Signature]

3/16/89

LISTED
8625