





MATCH LINE - SEE SHEET UE-6 - STA 345+00

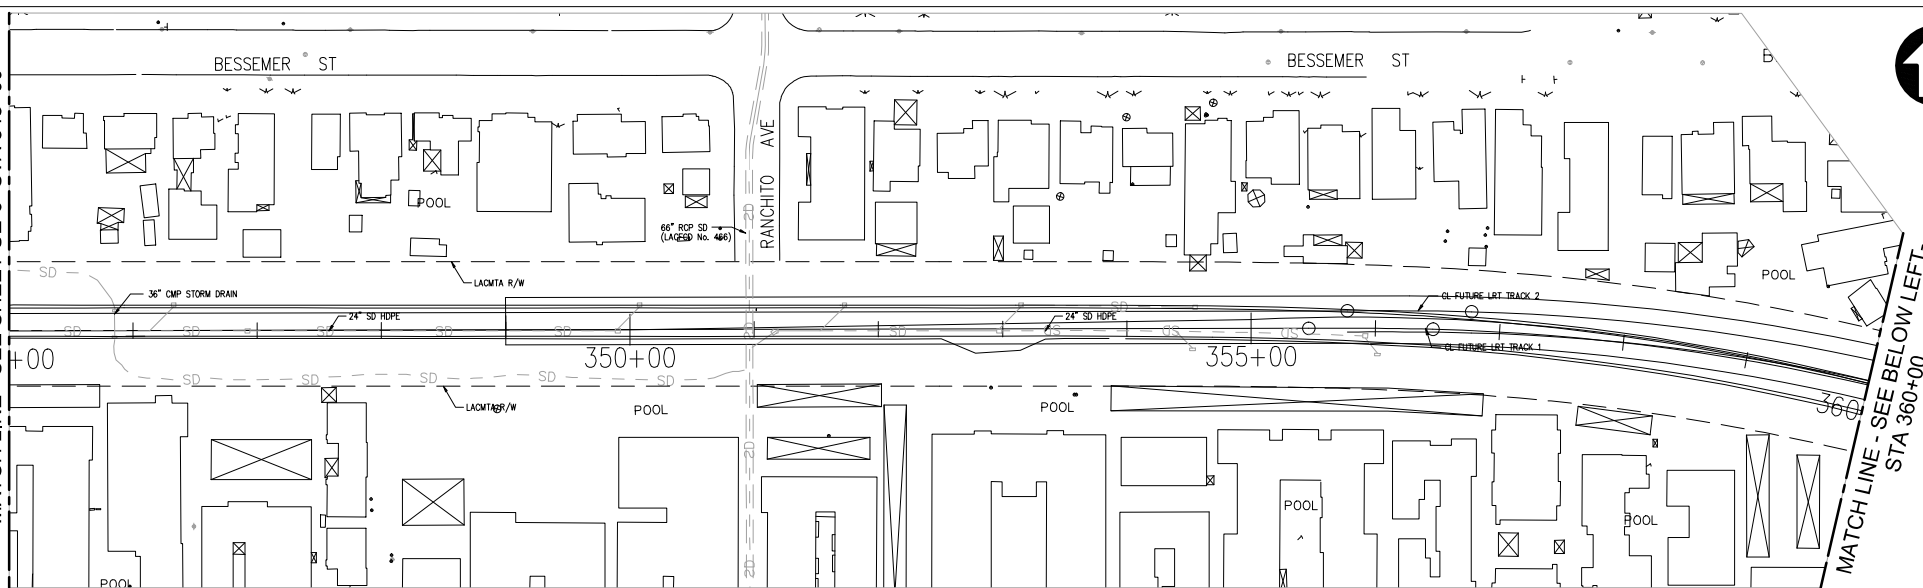

MATCH LINE - SEE BELOW LEFT - STA 360+00

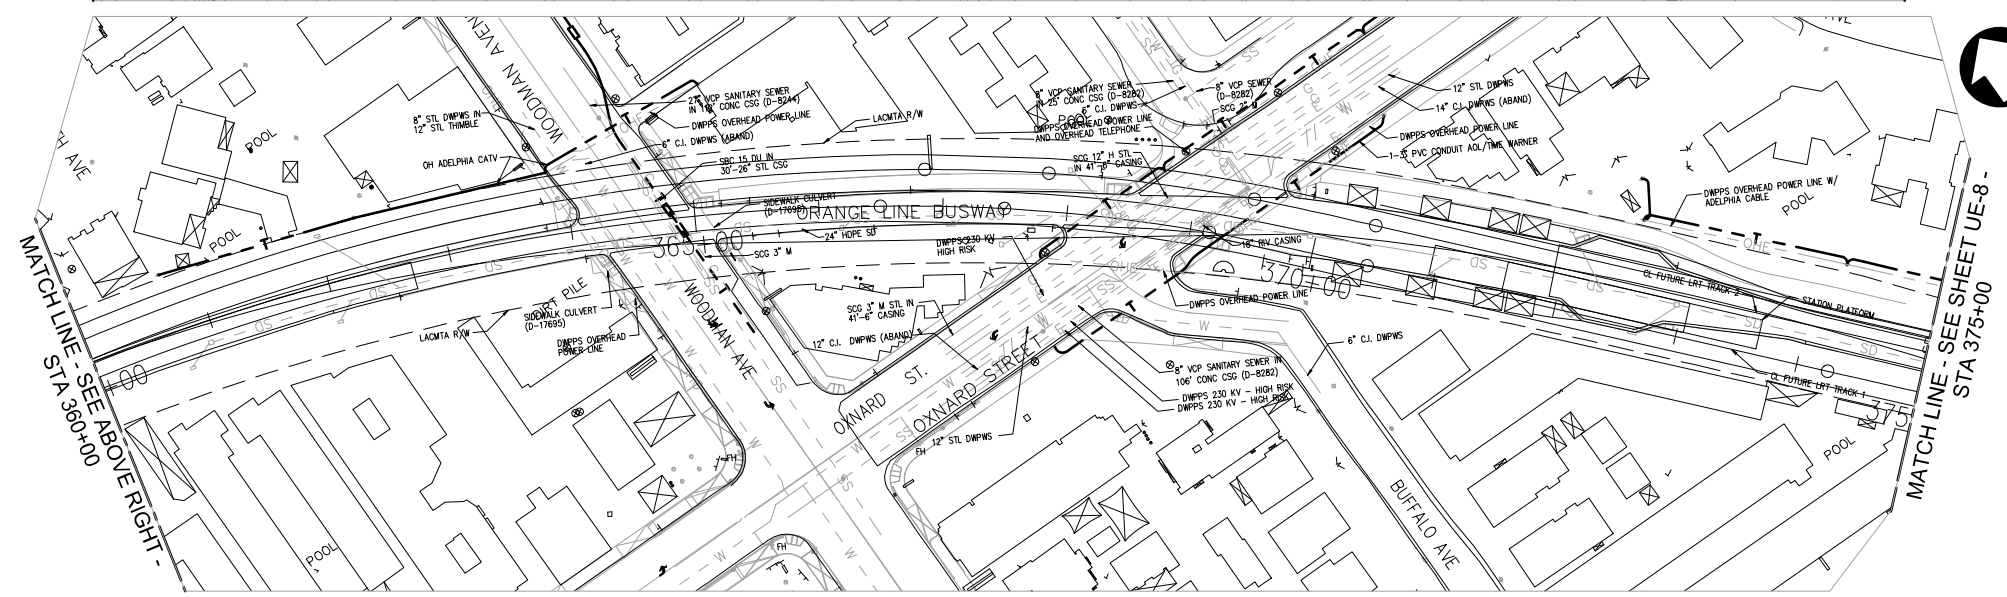

MATCH LINE - SEE SHEET UE-8 - STA 375+00

SCALE	1" - 50'
SHEET NO	UE-7
DATE	03/22/2018

LEGEND	
	EXISTING TELECOMMUNICATION
	LACMTA R/W
	LACMTA ORANGE LINE ALIGNMENT

**Metro**

**LOS ANGELES COUNTY
METROPOLITAN TRANSPORTATION AUTHORITY**

**MOTT
MACDONALD**

M M

**BA INC**

DESIGNED BY
ENGINEERED BY
CHECKED BY
APPROVED BY
DATE: 03/22/2018

METRO ORANGE LINE GRADE SEPARATIONS PROJECT

EXISTING TELECOMMUNICATION EXHIBIT

AT&T

STA 345+00 TO 375+00

