



MATCH LINE - SEE SHEET UE-6 - STA 345+00

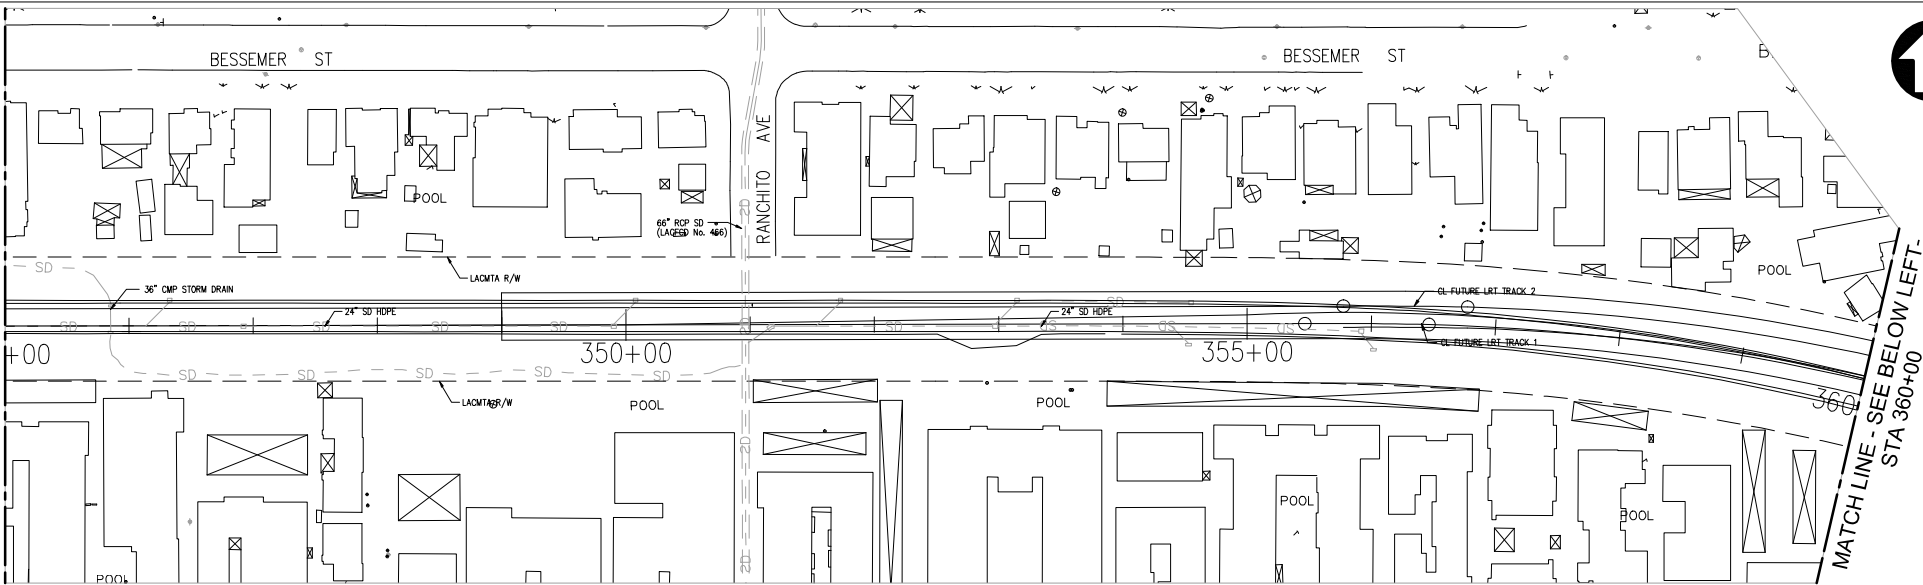

MATCH LINE - SEE BELOW LEFT - STA 360+00

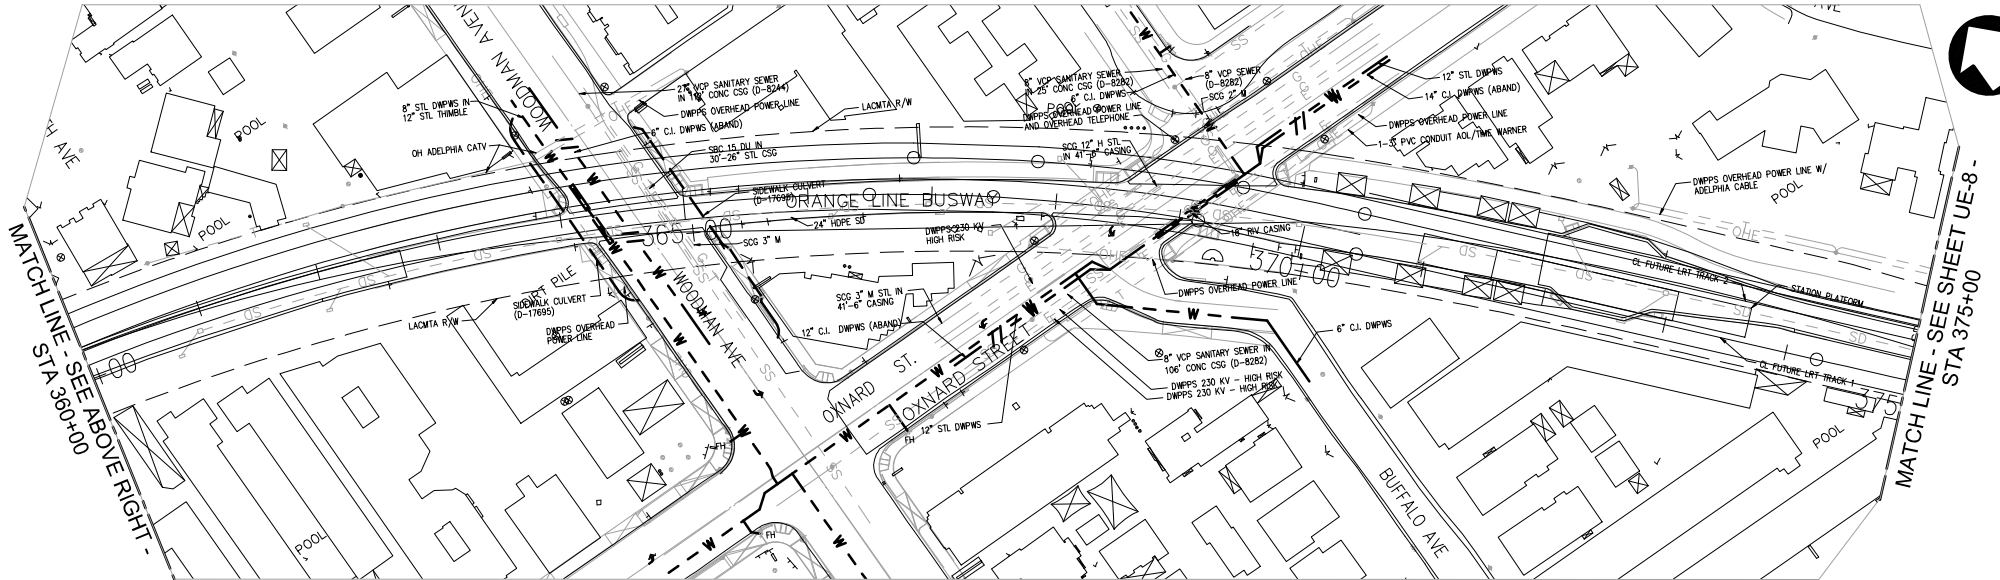

MATCH LINE - SEE SHEET UE-8 - STA 375+00

SCALE	1" = 50'
PROJECT	UE-7
DATE	03/22/2018
LEGEND	
---	EXISTING WATER
- - - -	LACMTA R/W
- . - . -	LACMTA ORANGE LINE ALIGNMENT

 **LOS ANGELES COUNTY**
METROPOLITAN TRANSPORTATION AUTHORITY

 **MOTT**
MACDONALD

 **BA INC**

METRO ORANGE LINE GRADE SEPARATIONS PROJECT
EXISTING WATER EXHIBIT
LADWP-WS
STA 345+00 TO 375+00

GRAPHIC SCALE
0 25 50 100
SCALE: 1"=50'