


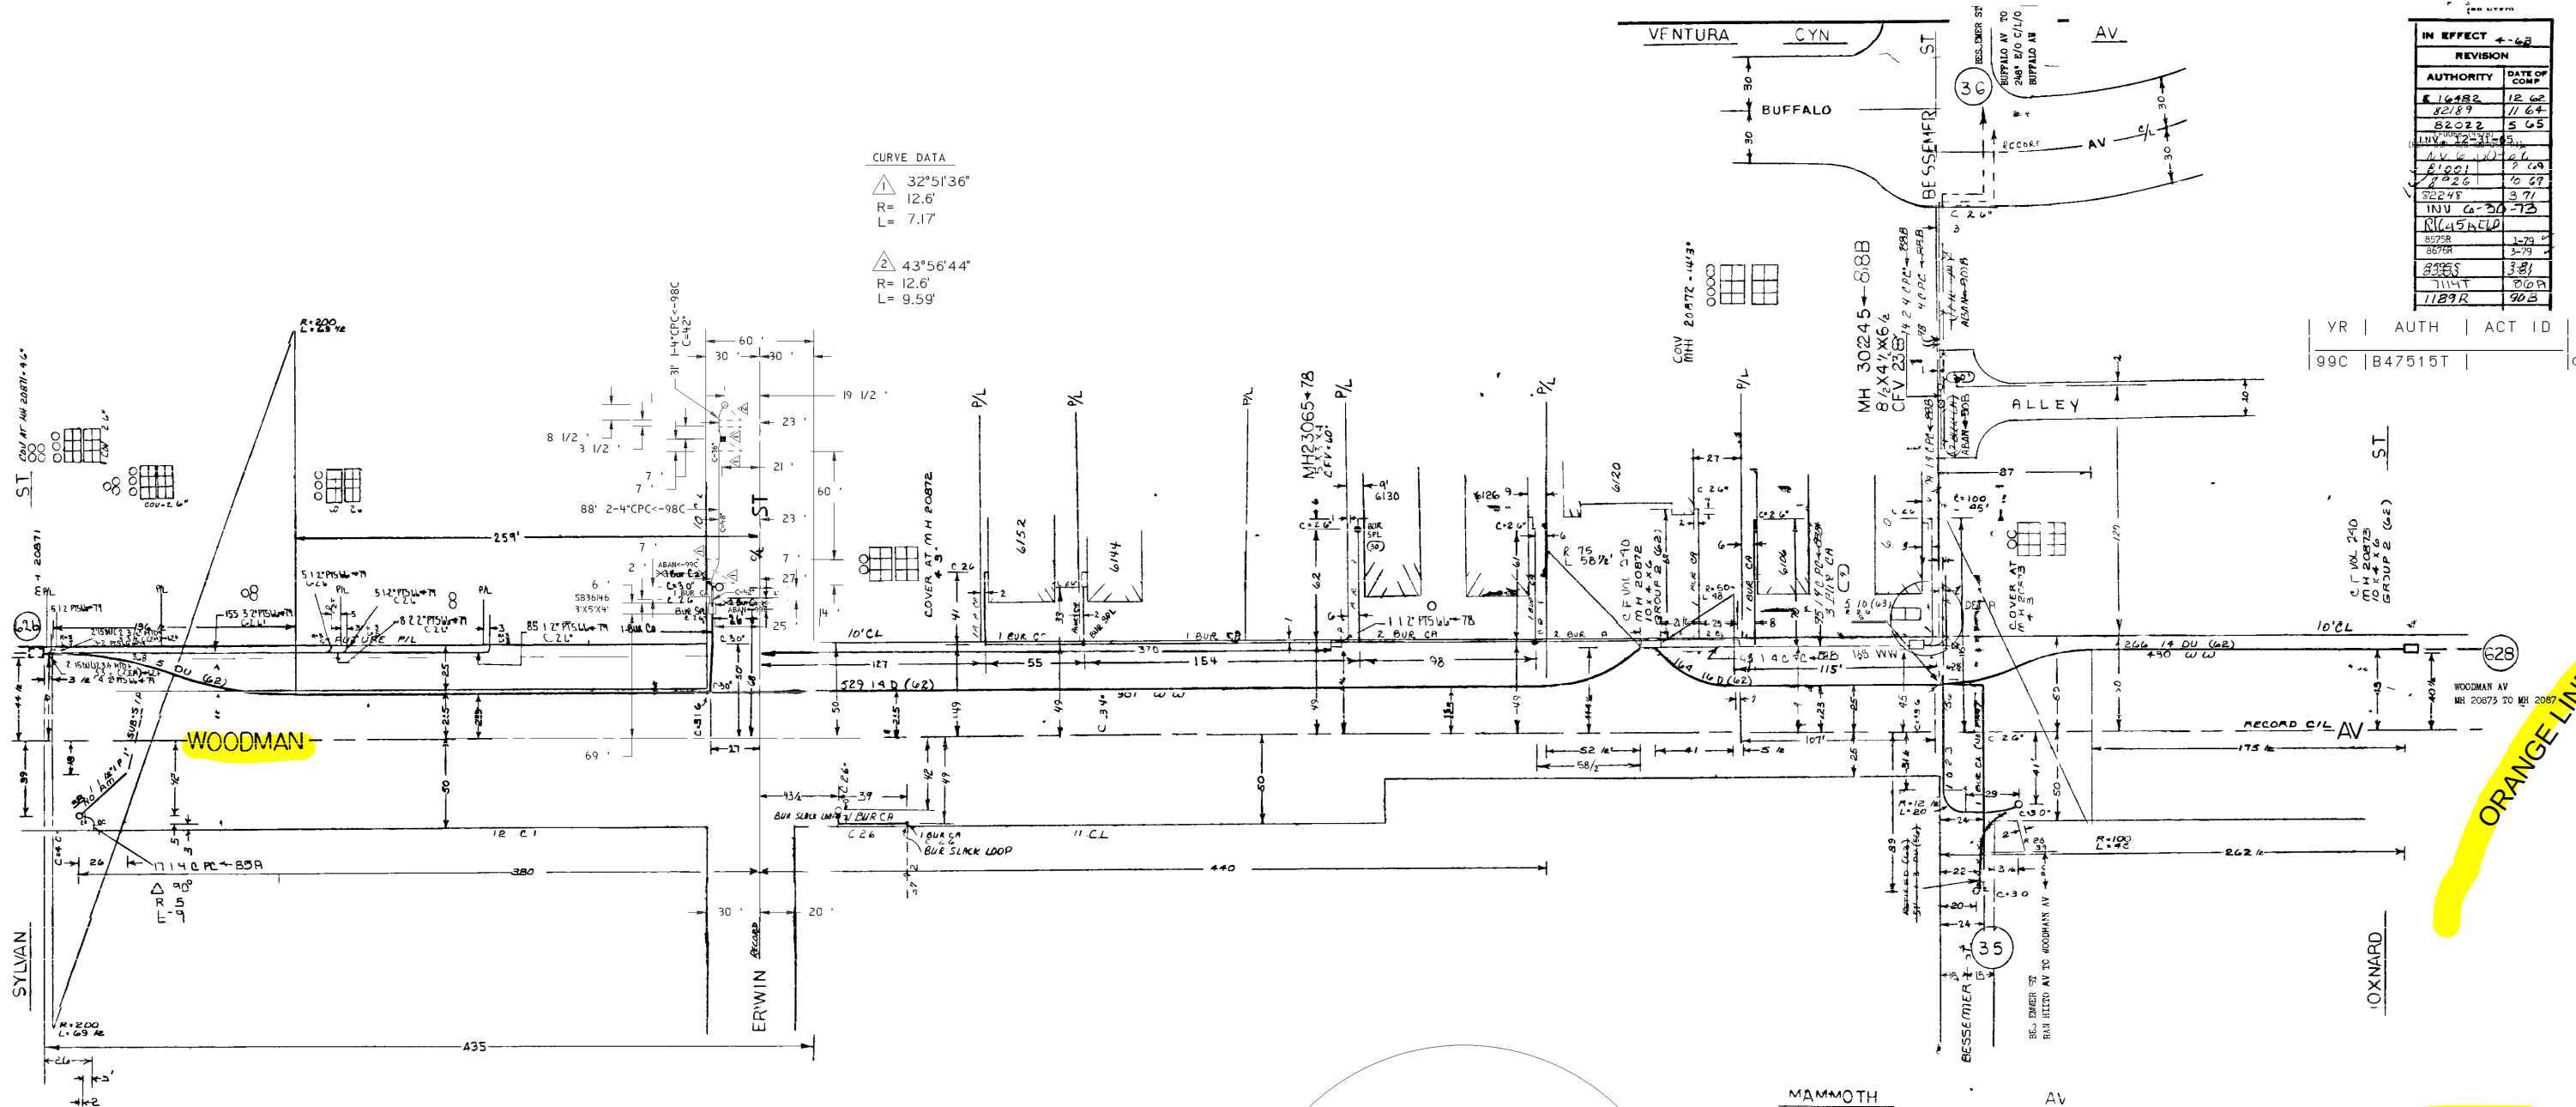


CURVE DATA
32°51'36"
R= 12.6'
L= 7.17'
43°56'44"
R= 12.6'
L= 9.59'

IN EFFECT 4-68	
REVISION	
AUTHORITY	DATE OF COMP.
816482	12 62
82189	11 64
82022	5 65
INV 4-23-65	
AV 6-10-65	6 65
81001	7 65
82026	10 67
82248	3 71
INV 6-30-73	
RL 4-5-73	
8575R	2-79
8675R	3-79
8855	3-81
7114T	8-05
1189R	9-05

YR	AUTH	ACT ID	CL
99C	B47515T		

ORANGE LINE BRT

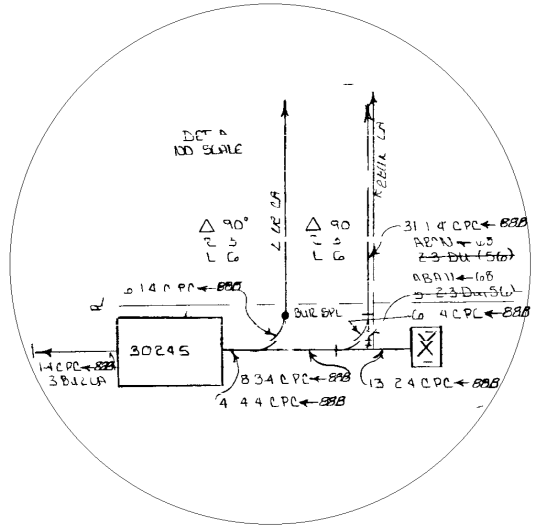

L.A. CITY (EAST)
L.A. VALLEY
L.A.F.A.
VITRIFIED CLAY DUCT
TRANSITE DUCT
I.P. - IRON PIPE

ISSUE DATE 10-16-00

SEGMENT NO. 1618-7468
R/C 4 EXCEPT AS NOTED

PACIFIC BELL

C.O. CEDROS
EXCH VAN NUYS
GEO-CO CODE B4-02
WOODMAN AVENUE MH 20871 TO MH 20873
TYPE OF RECORD:
SCALE: 1" = 50'
RECORDS NO. B402C627