

INDEX OF SHEETS

SHEET NO. 1.....TITLE SHEET AND MISCELLANEOUS DETAILS
SHEET NO. 2.....WOODMAN AVENUE FROM 320 FEET NORTH OF OXNARD STREET TO 87 FEET NORTH OF OXNARD STREET

- STANDARD PLANS: The following Standard Plans, listed by number and title, are included in this made a part of these plans.
- 1. Standard Culvert.....DL-2327
 - 2. Catch Basin Inlet and Top Slab.....B-3651, B-3654
 - 3. Manhole Frame and Cover.....B-2189
 - 4. Manhole Cover Locking Device.....B-3233
 - 5. Types of Curb and Gutter.....B-3682
 - 6. Keyed Sidewalk and Curb.....B-3675
 - 7. Standard Driveways.....D-14817

GENERAL NOTES

1. Stationing Shown on Profile is along Street &
2. Inlet and Outlets for Culverts Shall be Modified per Std. Plan B-3651 and/or B-3654 (The Opening used to be Optional with the Contractor). The Protection Bar Shall be Located as Follows: 5 inches back of Curb Line and 5 1/2 inches below top of Curb for 10 inch Curb Faces and 5 inches back of Curb Line and 7 1/2 inches below top of Curb for 12 inch Curb Faces. Omit protection bar on all Outlets.
3. All Manhole Frames and Covers Shall be Installed Per Std. Plan B-2189.
4. Install Locking Device on all Manhole Covers Per Std. Plan B-3233.
5. Sidewalk Constructed Adjacent to Curb Shall be Provided with a Key Per Std. Plan B-3675.
6. Floor of Culvert Shall be Warped in 3 feet to Conform to flow Line of Gutter at all Outlets.

PLAN AND PROFILE OF STORM DRAIN IN WOODMAN AVENUE FROM 320 FEET NORTH OF OXNARD STREET TO 87 FEET NORTH OF OXNARD STREET

CITY OF LOS ANGELES
LYALL A. PARDEE CITY ENGINEER

DATUM NOTE
U. S. G. S. DATUM EFFECTIVE JULY 1, 1925 ORDINANCE NO. 5222 DEDUCT 5.75 FEET TO ADJUST TO DATUM PLANE IN USE PRIOR TO SAID DATE

REFERENCES

FIELD BOOK NO. 73823-52
DATE OF SURVEY.....
DISTRICT MAP NO. 7422, 7423 & W. MAP NO. 102, 303
ASSESSMENT MAP NO. 428
DRAINAGE MAP NO. 428
SUPERSEDES PROFILE NO.

NOTICE TO CONTRACTORS

THIS IMPROVEMENT ALSO INCLUDES WORK CALLED FOR ON THE FOLLOWING SPECIAL PLANS AND PROFILES
STREET IMP. PROFILE.....P. 20822
SEWER PLANS.....NONE
STORM DRAIN PLANS.....NONE
STRUCTURAL PLANS.....NONE
ORNAMENTAL LIGHTING PLANS.....P. 20822
EXISTING MANHOLES (TOTAL) STORM DRAIN.....0 SEWER.....0

SPECIFICATIONS-All work detailed on these plans to be performed under contract shall, except as otherwise stated or provided for herein, be constructed in accordance with Standard Specifications No. 150, as amended by Amendment No. 1.


SUPPLEMENTAL NOTES-The following notes shall supplement the applicable Standard Plans or Specifications on the Standard Specifications.

CLASSES OF CONCRETE-Superior concrete shall be used for all concrete work on this project. The concrete shall be of the same quality as that used in the construction of the existing storm drain and sewer lines in the City of Los Angeles.

PAVEMENT-CONCRETE CURBS SHALL BE CONSTRUCTED WITH A 4" MINIMUM THICKNESS. THE CURBS SHALL BE SET IN A 6" MINIMUM THICKNESS OF CONCRETE. THE CURBS SHALL BE SET IN A 6" MINIMUM THICKNESS OF CONCRETE.

Traffic lanes shall have a minimum width of ten (10) feet and clearance of two (2) feet to curbs, barriers, or other vertical obstructions, and five (5) feet to any open excavation.


The Department of Traffic of the City of Los Angeles will issue "Temporary No Parking" signs along the project area. The signs shall be placed on the State Highway side of the project area. The signs shall be placed on the State Highway side of the project area.

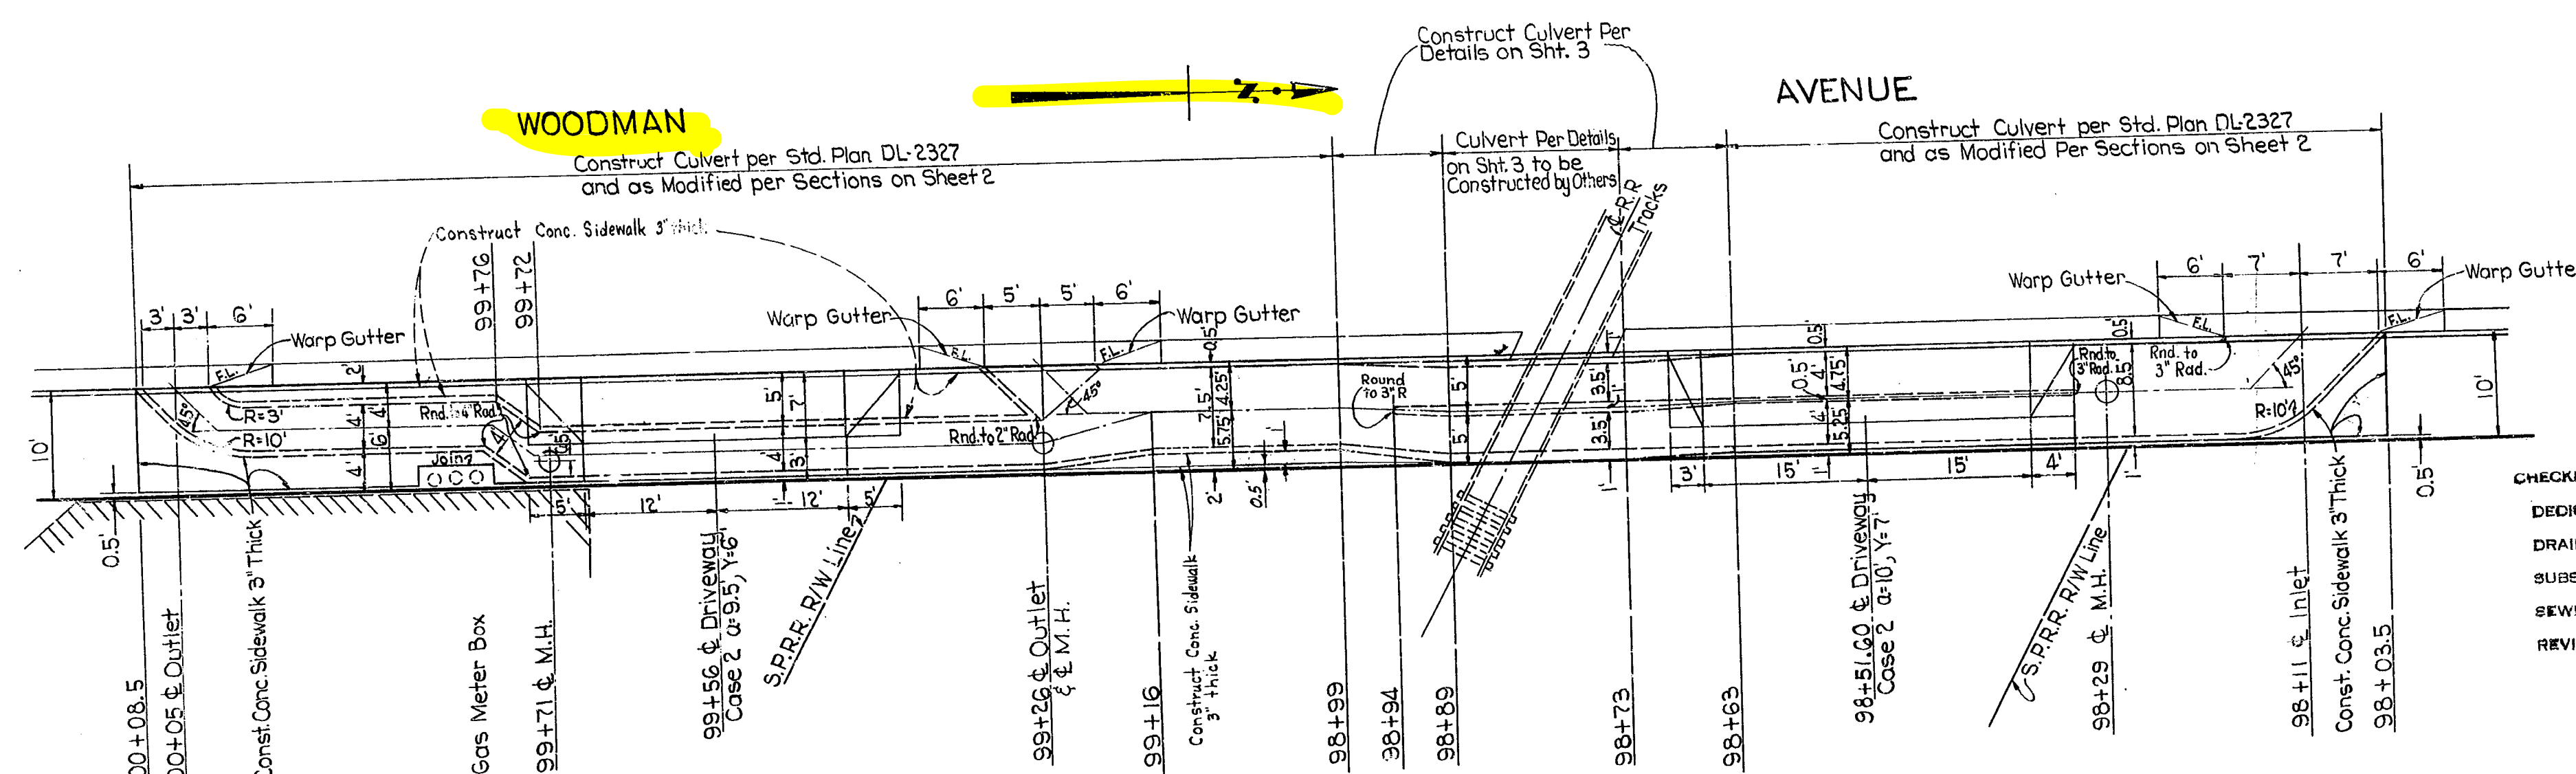


CHECKED FOR:

DEDICATION.....
DRAINAGE.....
SUBSTRUCTURE.....
SEWER.....
REVIEWED.....

DETAIL OF CULVERT WOODMAN AVENUE (EAST SIDE) Scale: 1"=10'

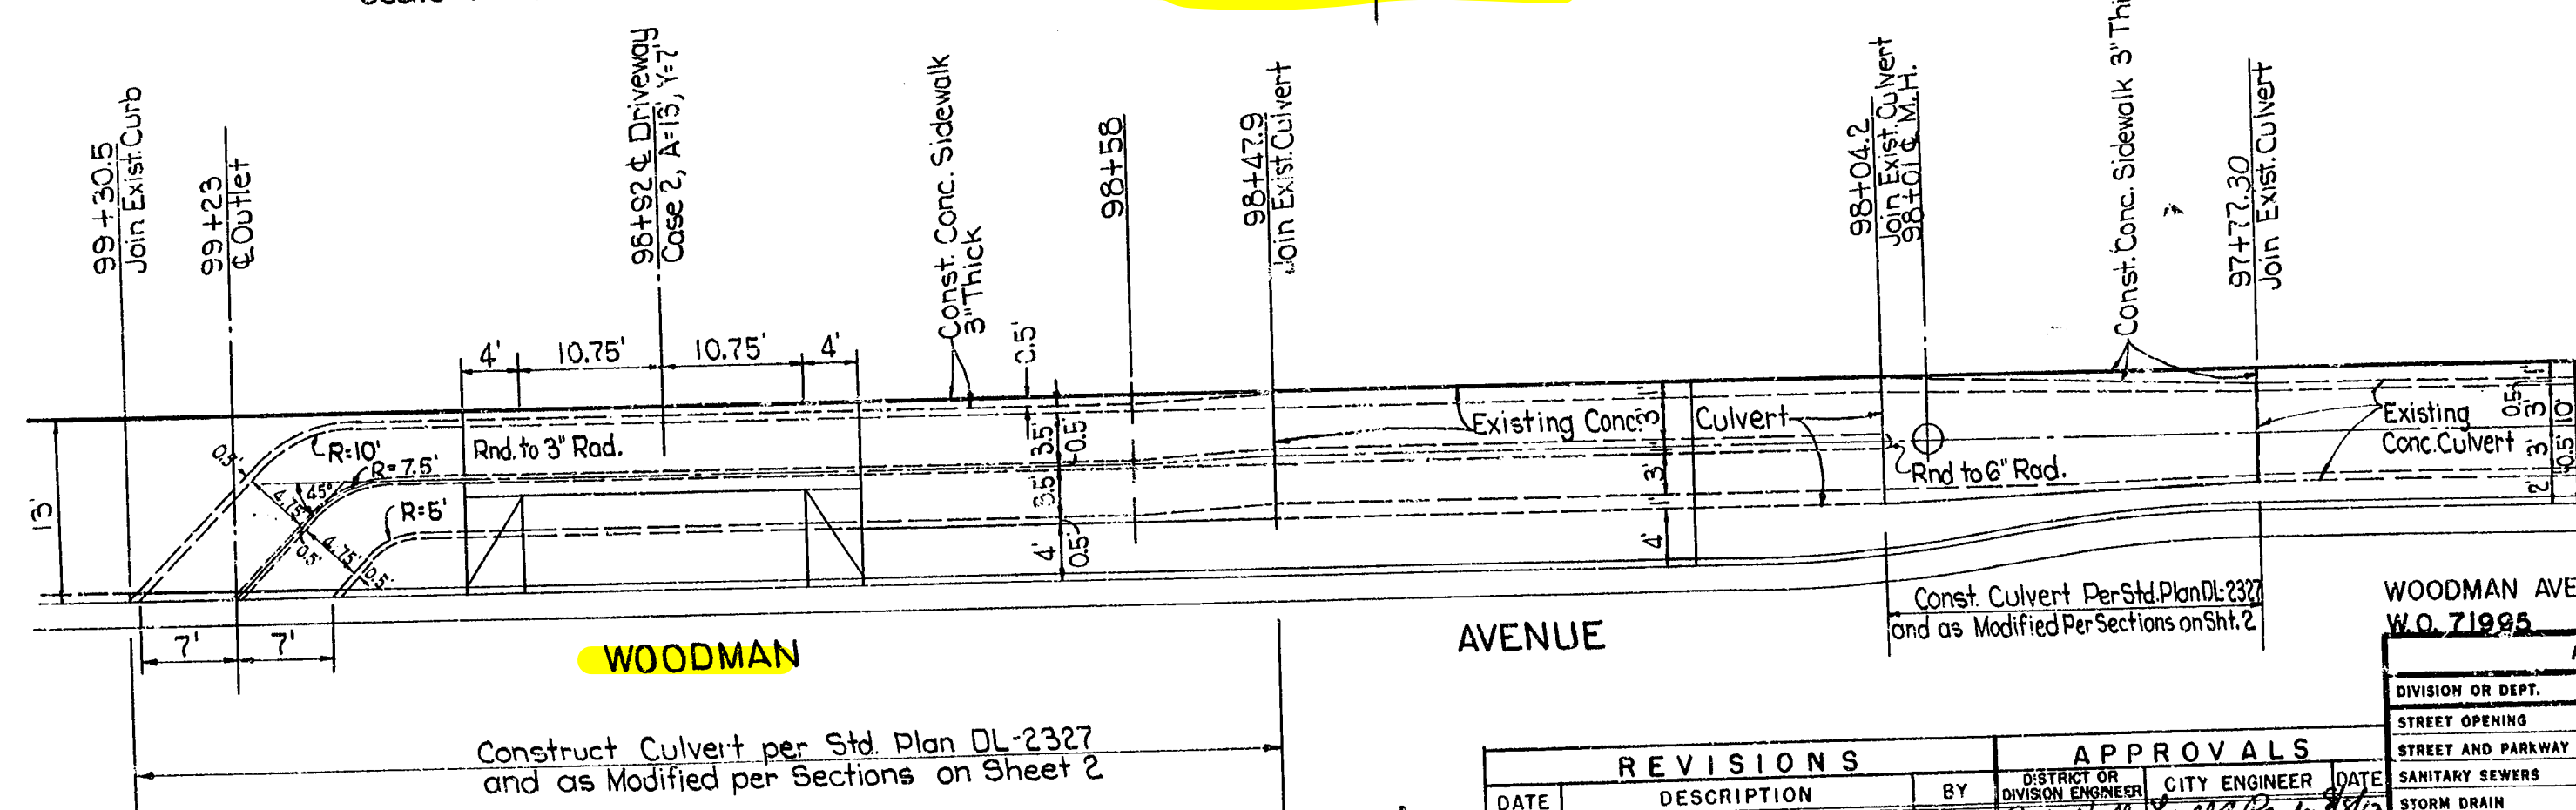

DETAIL OF CULVERT WOODMAN AVENUE (WEST SIDE) Scale: 1"=10'

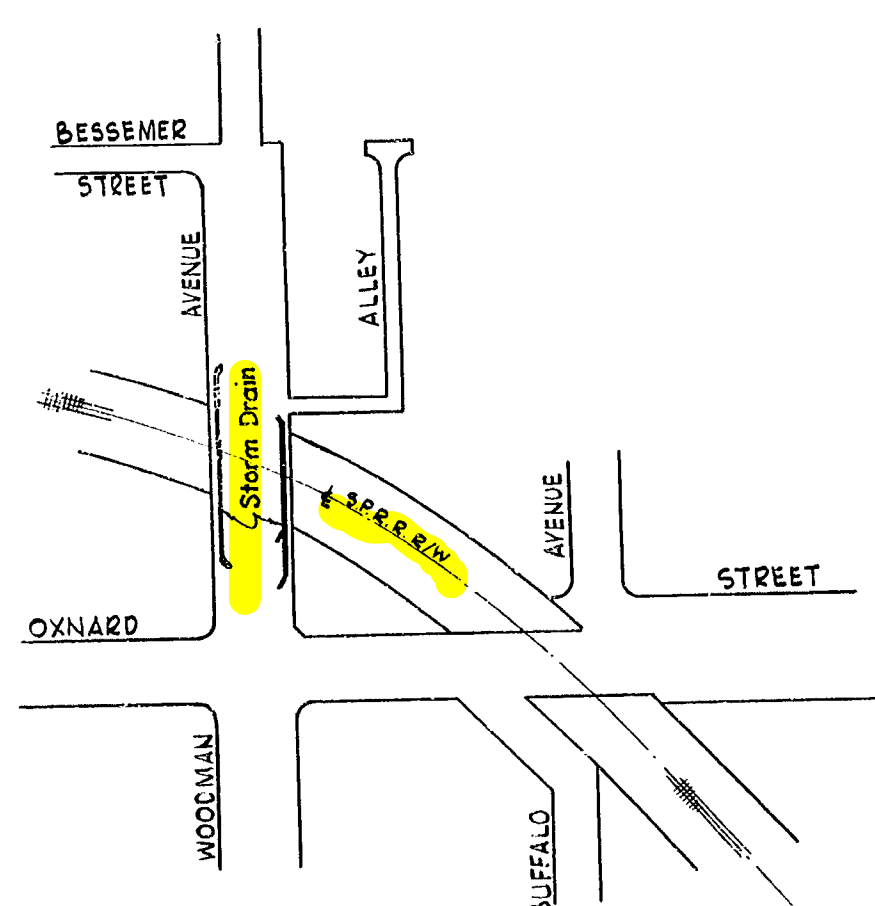



KEY MAP SCALE: 1"=200'

WOODMAN AVENUE & OXNARD STREET I.D. W.O. 71995


APPROVALS		
DIVISION OR DEPT.	ENGINEER	DATE
STREET OPENING		
STREET AND PARKWAY		
SANITARY SEWERS		
STORM DRAIN		
WIDEN DESIGN		
STREET LIGHTS J.M.		
WATER DEPARTMENT		
TRAFFIC DEPT.		

SHEET NO. 1 OF 3 SHEETS D-17695


D 17695

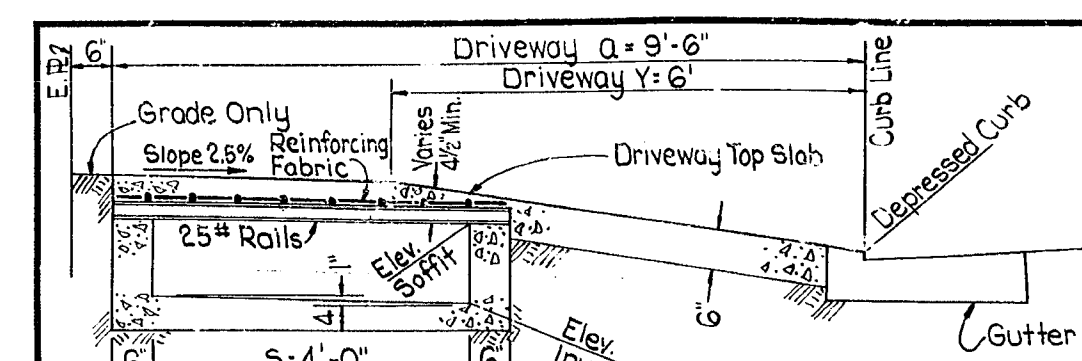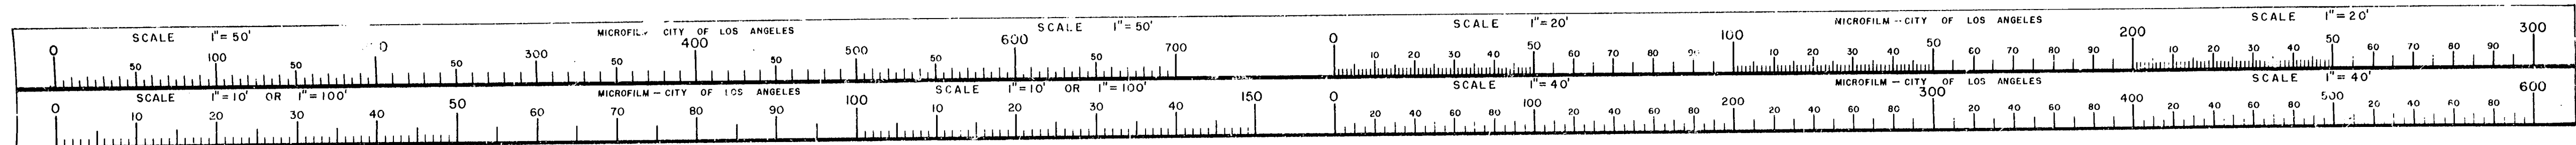


SECTION F-F
FROM STA. 99+39 TO STA. 99+72

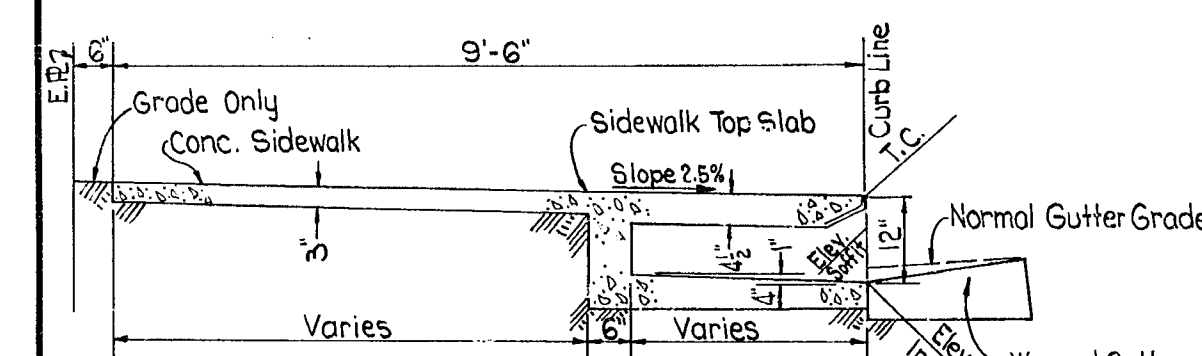

SECTION G-G
FROM STA. 100+02 TO STA. 100+08

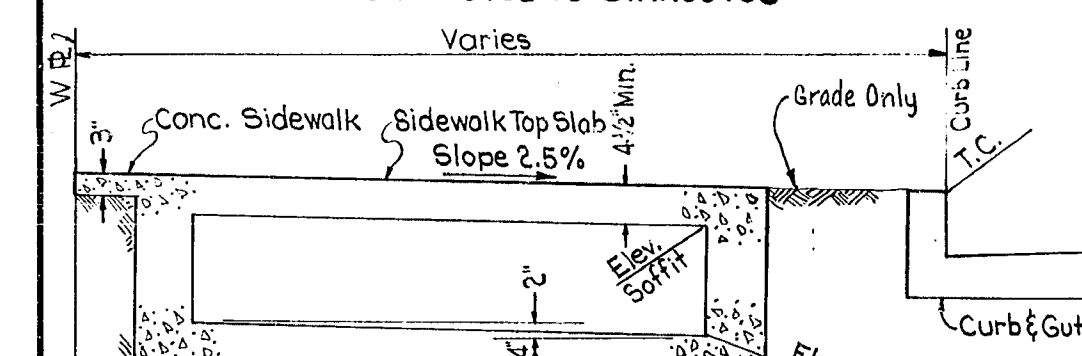

SECTION H-H
FROM STA. 97+77.3 TO STA. 98+04.2

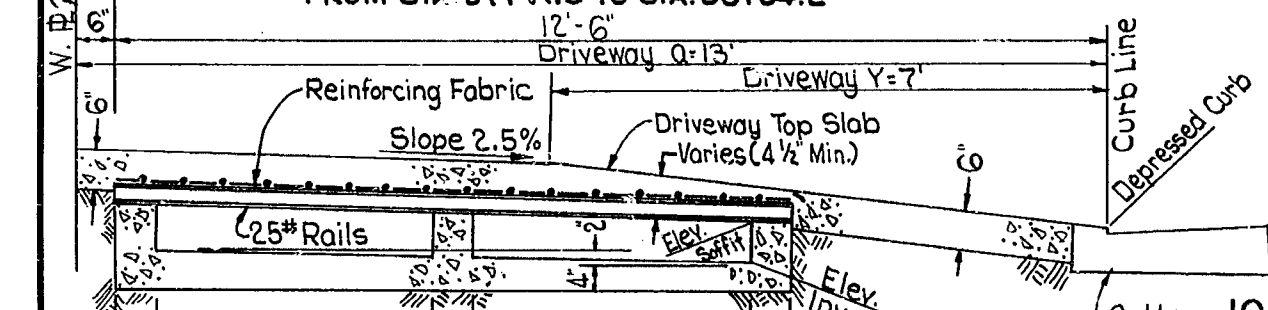

SECTION J-J
FROM STA. 98+77.25 TO STA. 99+00.75


NO SCALE

STREET



OXNARD

BENCH MARK:
Sta. trav. mon. 10-L-2 & Inters.
Oxnard St. & Woodman Ave.
F.B. 23823-53 Elev. 689.01 (1950 Adj.)


SCALE: 1"=20'

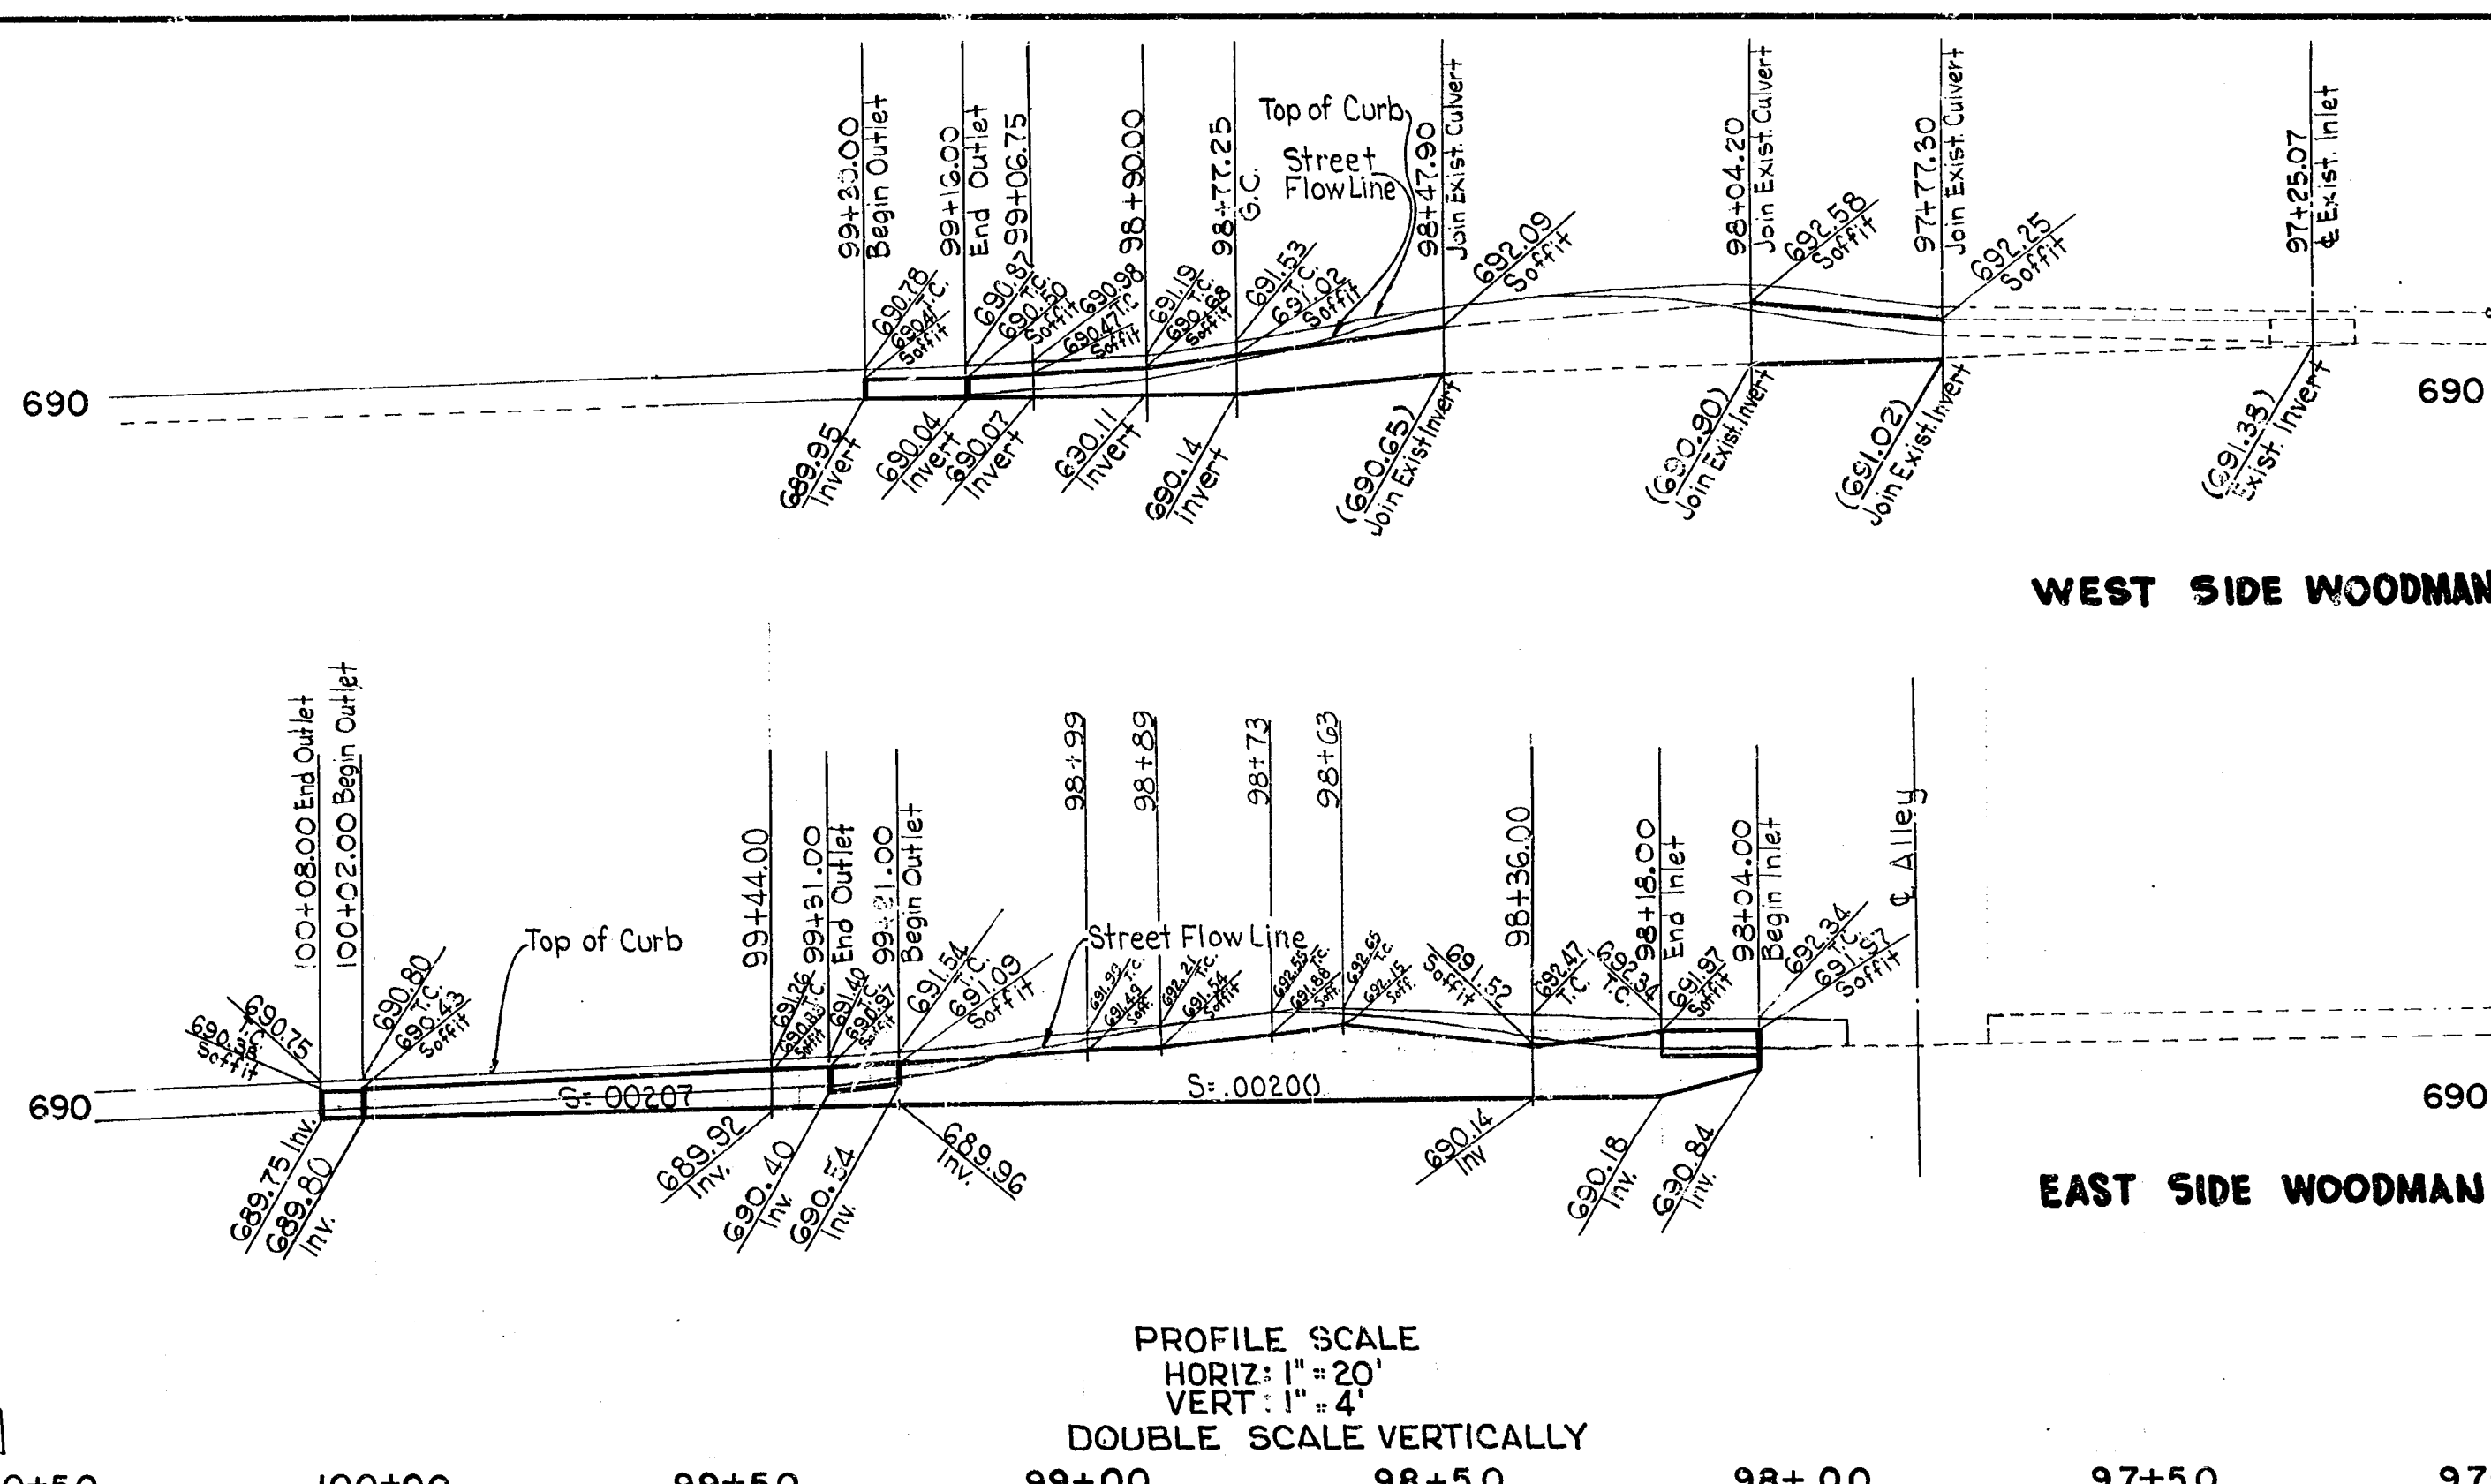


PROFILE SCALE
HORIZ: 1"=20'
VERT: 1"=4'
DOUBLE SCALE VERTICALLY

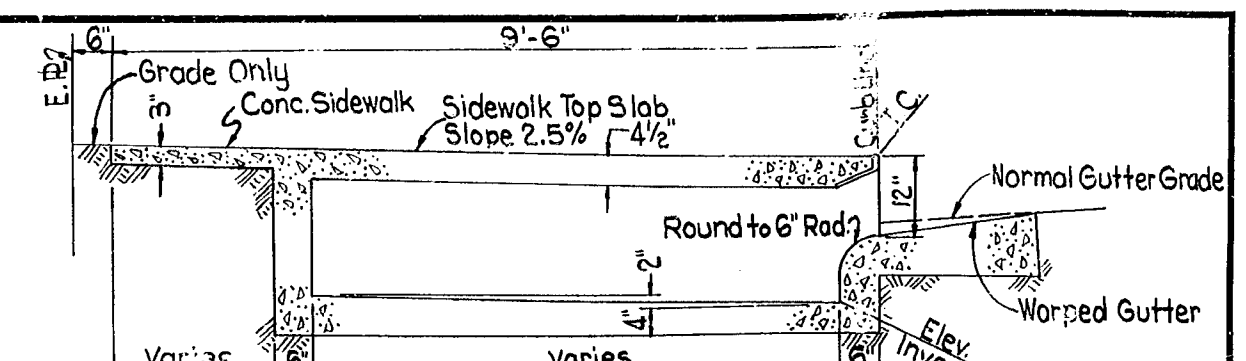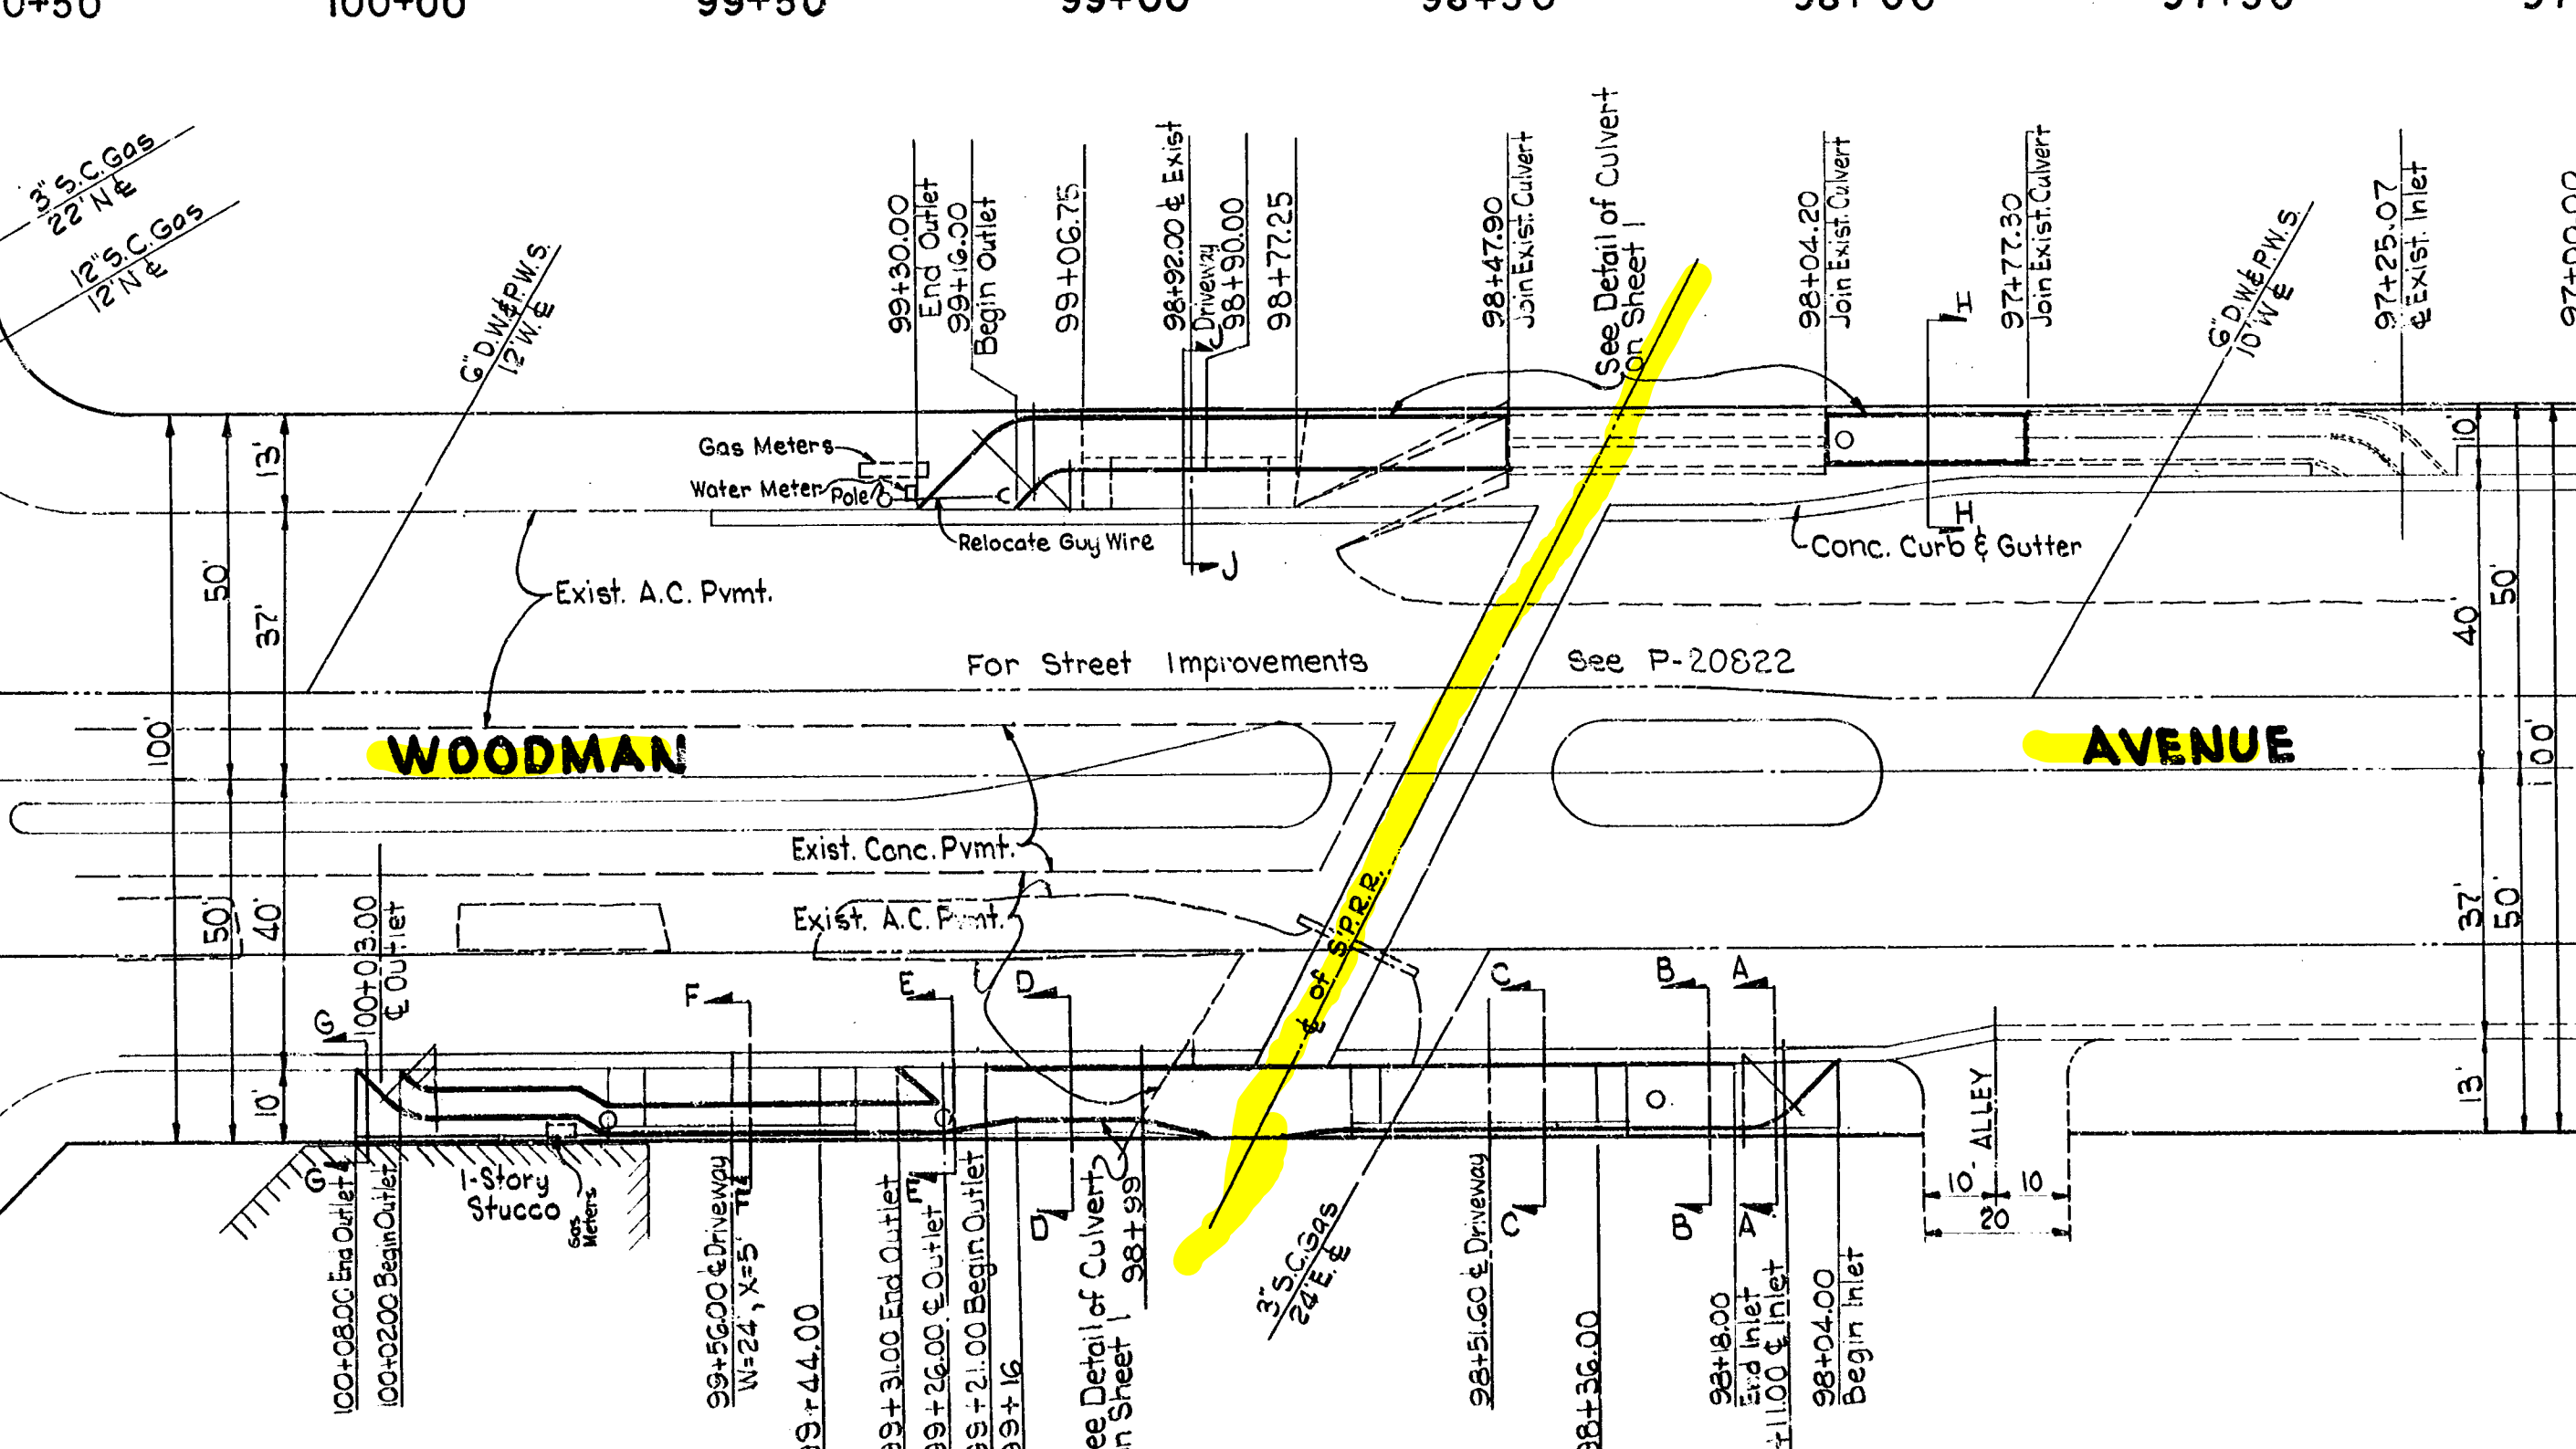


SECTION A-A
FROM STA. 98+04 TO STA. 98+18

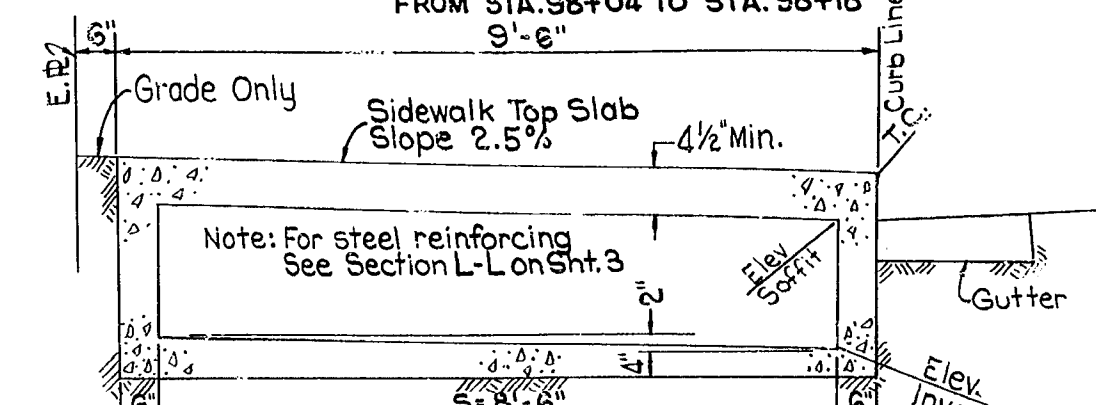


SECTION B-B
FROM STA. 98+18 TO STA. 98+32.60

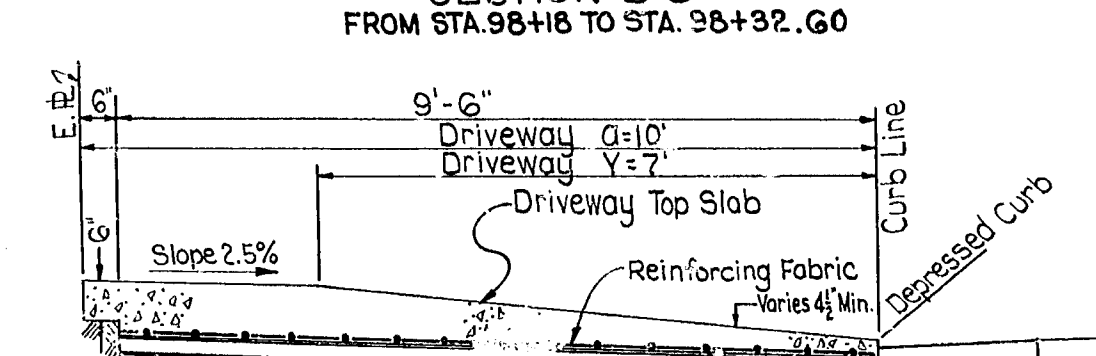

SECTION C-C
FROM STA. 98+04 TO STA. 98+08

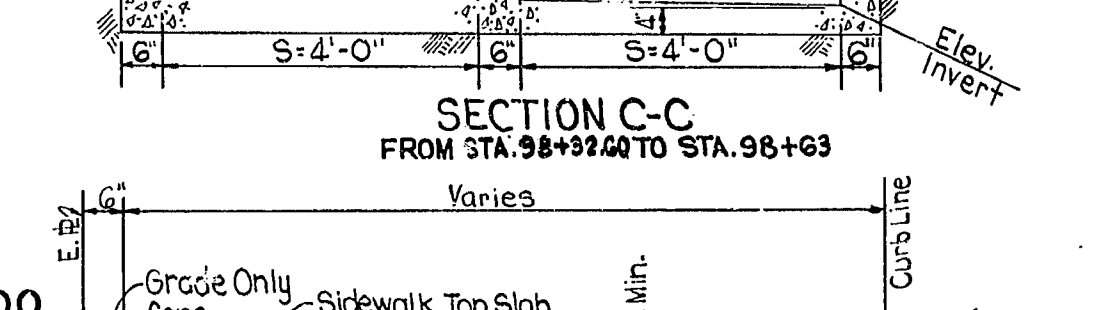

SECTION D-D
FROM STA. 98+00 TO STA. 98+04

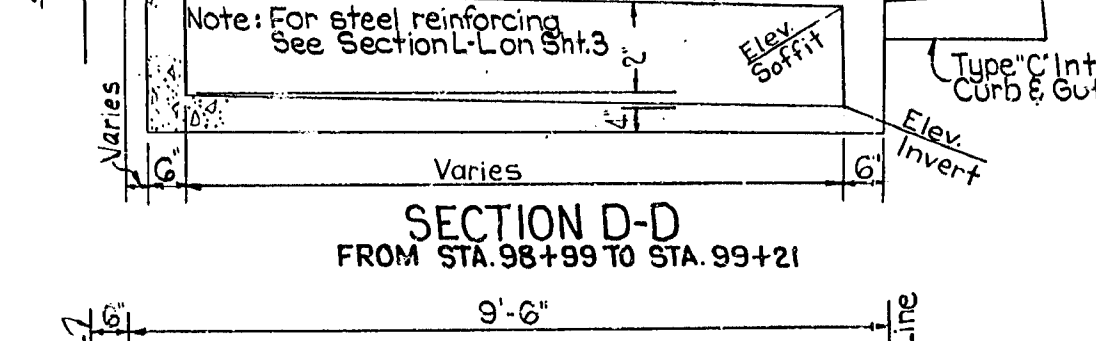

SECTION E-E
FROM STA. 98+00 TO STA. 98+04

NO SCALE

WOODMAN AVENUE & OXNARD STREET I.D.

SUBMITTED 10-10-63 Herschel B. Brown DIVISION OF DISTRICT ENGINEER	APPROVED 11-1-63 Lyall A. Pardee CITY ENGINEER
CITY OF LOS ANGELES LYALL A. PARDEE CITY ENGINEER PLAN AND PROFILE OF STORM DRAIN IN WOODMAN AVENUE FROM 320 FT. N/O OXNARD ST. TO 87 FT. N/O OXNARD ST.	
SHEET NO. 2 OF 3 SHEETS	D-17695

D 17695