


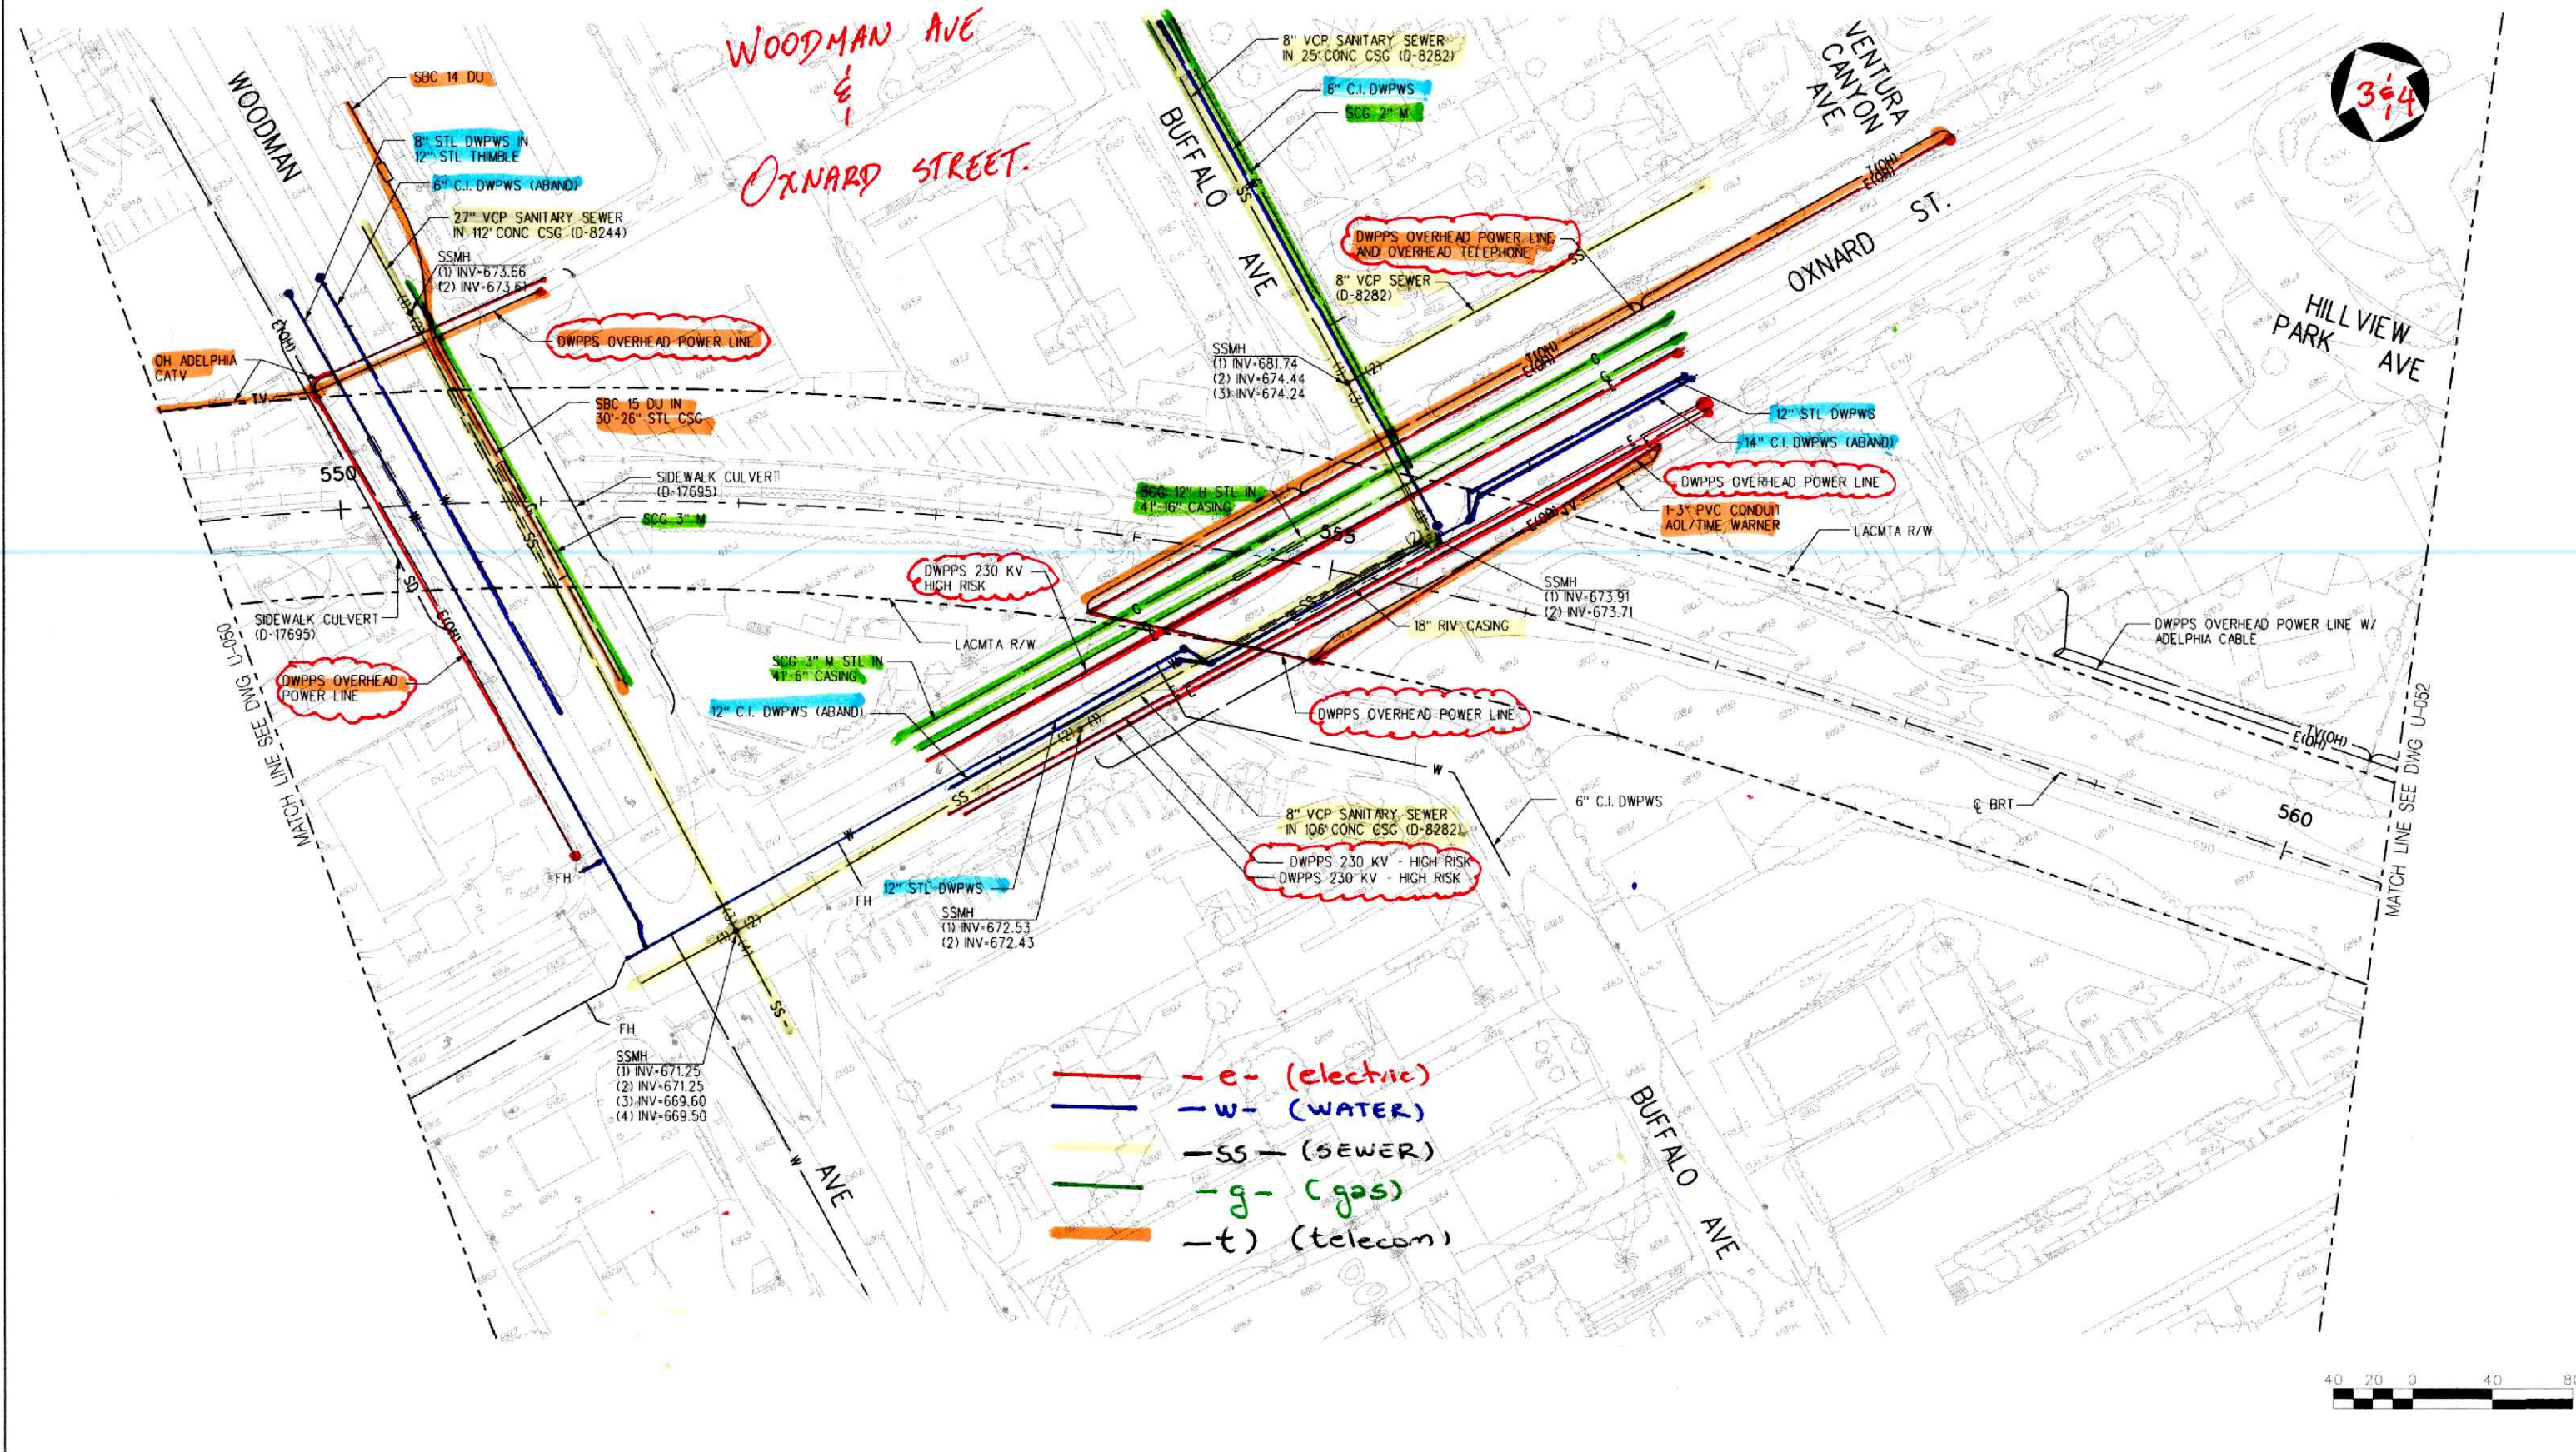

<table border="1"><tr><td>REV</td><td>DATE</td><td>BY</td><td>APP</td><td>REG NO</td><td>EXPIRES</td><td>SEAL HOLDER</td><td>DESCRIPTION</td></tr><tr><td>0</td><td>1/22/04</td><td>YX</td><td>BEJ</td><td>C59517</td><td>12/31/03</td><td>BRETT E. JONES</td><td>ISSUED FOR CONSTRUCTION - 1B</td></tr></table>						REV	DATE	BY	APP	REG NO	EXPIRES	SEAL HOLDER	DESCRIPTION	0	1/22/04	YX	BEJ	C59517	12/31/03	BRETT E. JONES	ISSUED FOR CONSTRUCTION - 1B	DESIGNED BY S. KASSISIEH DRAWN BY M. CUTTER CHECKED BY S. YOUSEFIAN IN CHARGE B. JONES DATE 11/07/03			LOS ANGELES COUNTY METROPOLITAN TRANSPORTATION AUTHORITY SAN FERNANDO VALLEY EAST-WEST BRT PROJECT Washington Group International WASHINGTON GROUP INTERNATIONAL, INC. 5805 SEPULVEDA BLVD., SUITE 500 VAN NUYS, CA 91411	SHIMMICK OBAYASHI, JV 5805 SEPULVEDA BLVD., SUITE 500 VAN NUYS, CA 91411	NORTH HOLLYWOOD TO WARNER CENTER UTILITIES SHEET 48 OF 65	CONTRACT NO C0675 DRAWING NO U-051 SCALE HORIZ. 1"=40' SHEET NO
REV	DATE	BY	APP	REG NO	EXPIRES	SEAL HOLDER	DESCRIPTION																					
0	1/22/04	YX	BEJ	C59517	12/31/03	BRETT E. JONES	ISSUED FOR CONSTRUCTION - 1B																					

07/21/2006 08:44:53 AM m:\bri\p\vine\sheet\temp\utilities-u-051.dwg