


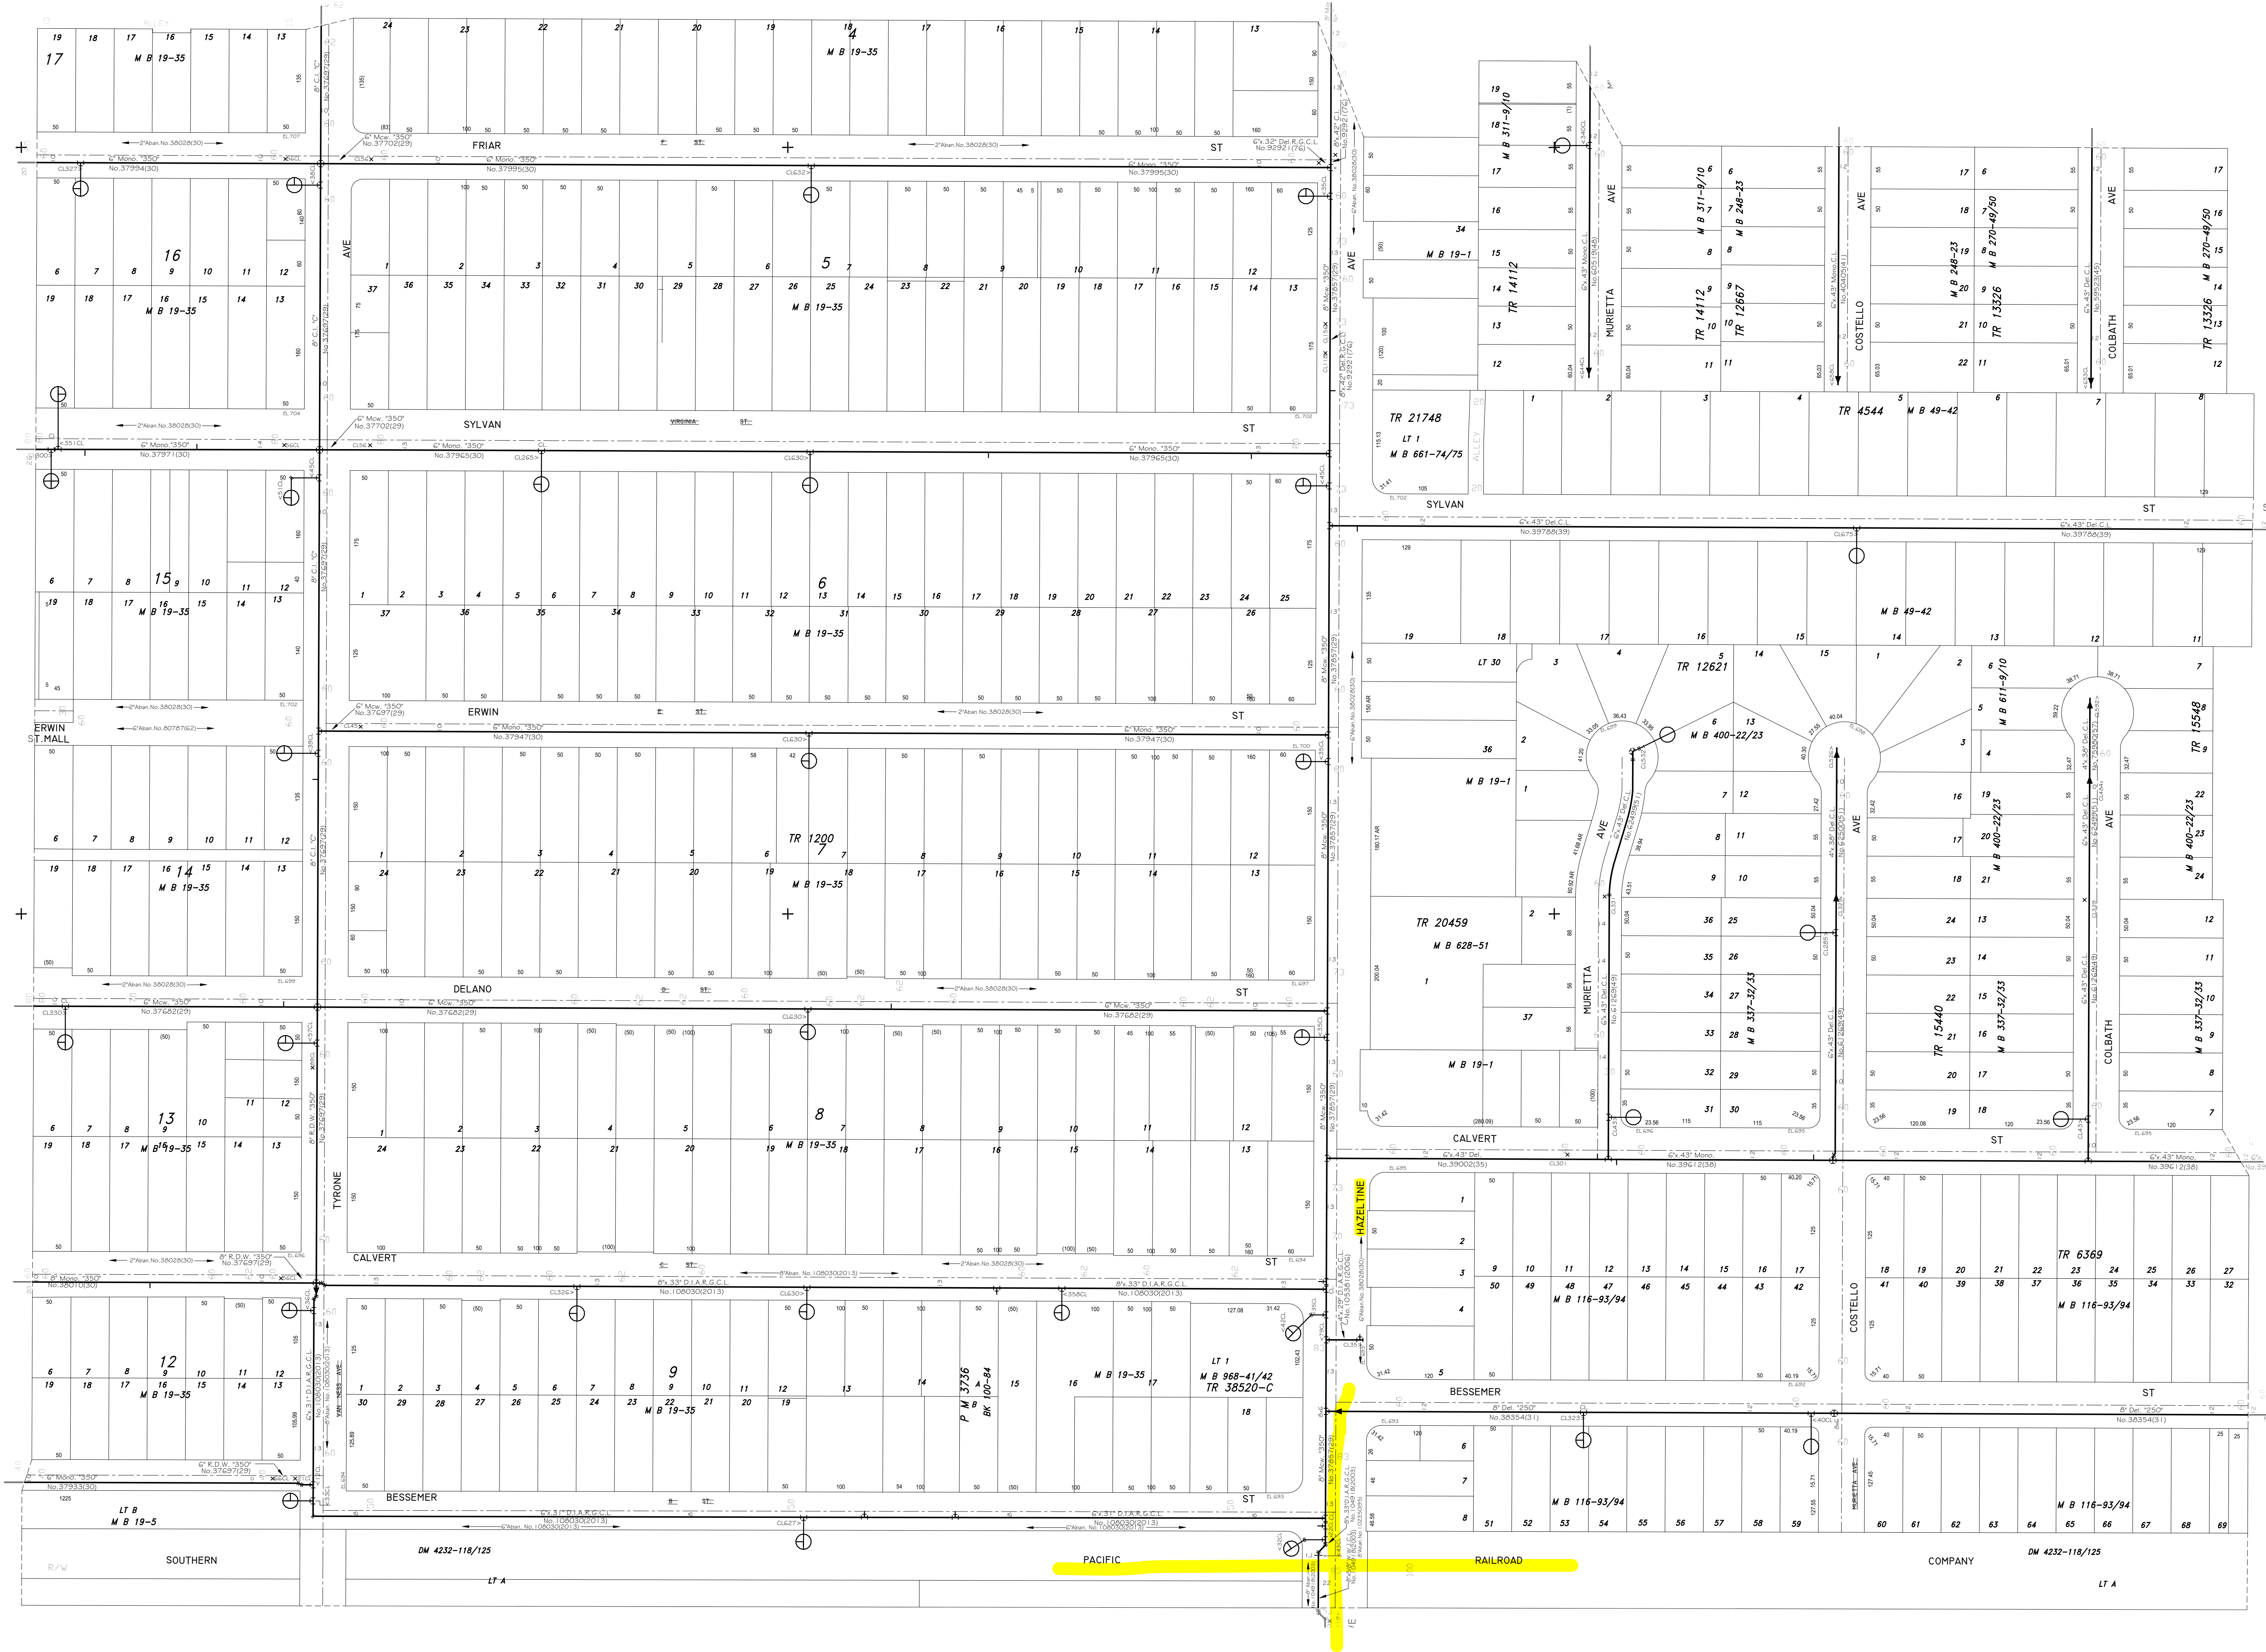

E.6.426.892

Questions or Comments, contact: WaterGIS Group, Rm. 1439, JFB

The Los Angeles Department of Water and Power (LADWP) assumes no responsibility for the accuracy of the substructure information herein provided. The user assumes responsibility for verifying substructure locations before excavation and assumes all liabilities for damage to LADWP facilities as a result of such excavation. Call Underground Service alert on 1-800-227-2600 two (2) days before excavating.

WATER SERVICE MAP	
DISTRICT: EAST VALLEY	
178-153	

LEGEND MAP SCALE 1" = 1500'		SYMBOLS AND NOTATIONS		SCALE: 1" = 100'		PLOTTED DATE		CHKD. DATE		FIRE HYDRANTS		REFERENCES	
AS SHOWN		MAP		NAME		NAME		NAME		2 1/2" SINGLE		MAPS REPLACED	
		CONVERTED MAINS		T-CHEN		06-10-2002		06-15-2009		2 1/2" S. BUILT UP		970 NS, 934 OS	
		CONVERTED SERVICES		D-LEE		02-02-2006		06-15-2009		2 1/2" DOUBLE		2023 NS, 927 OS	
		MISC		NAME		NAME		NAME		4" SINGLE			
										4" S. BUILT UP			
										4" DOUBLE		LANDBASE:	
										2 1/2" x 4" DOUBLE		177B153	