


MATCH LINE - SEE SHEET UE-5 - STA 315+00

MATCH LINE - SEE ABOVE RIGHT - STA 330+00

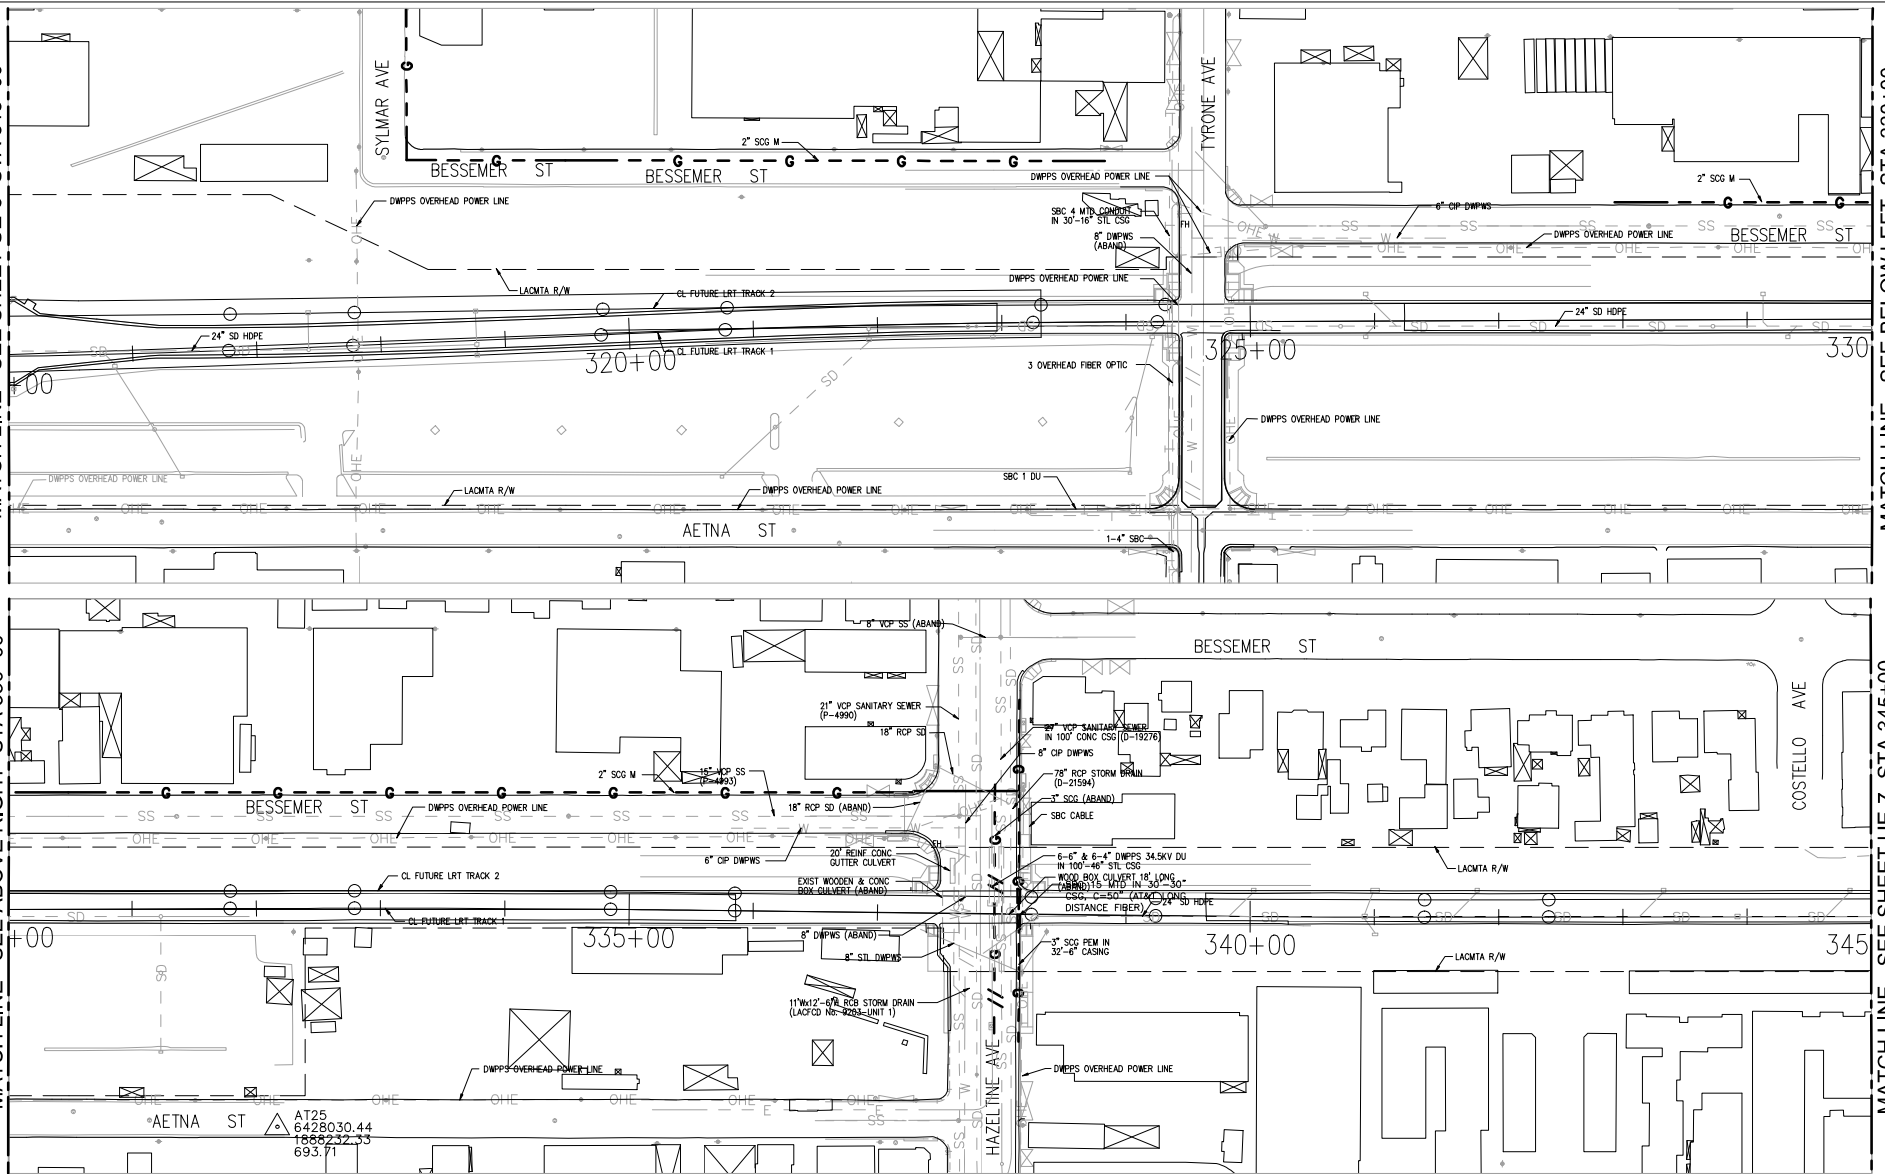

MATCH LINE - SEE BELOW LEFT - STA 330+00

MATCH LINE - SEE SHEET UE-7 - STA 345+00



|            |            |
|------------|------------|
| SCALE      | 1" = 50'   |
| REPORT NO. | UE-6       |
| DATE       | 03/22/2018 |

|         |                              |
|---------|------------------------------|
| LEGEND  |                              |
| ---     | EXISTING GAS                 |
| - - - - | LACMTA R/W                   |
| - - - - | LACMTA ORANGE LINE ALIGNMENT |

|                    |                                       |
|--------------------|---------------------------------------|
|                    | Metro                                 |
| LOS ANGELES COUNTY | METROPOLITAN TRANSPORTATION AUTHORITY |

|           |   |
|-----------|---|
| MOTT      | M |
| MACDONALD | M |



|                                             |
|---------------------------------------------|
| METRO ORANGE LINE GRADE SEPARATIONS PROJECT |
| EXISTING GAS EXHIBIT                        |
| SO CAL GAS                                  |
| STA 315+00 TO 345+00                        |

|               |
|---------------|
| GRAPHIC SCALE |
| 0 25 50 100   |
| SCALE: 1"=50' |