


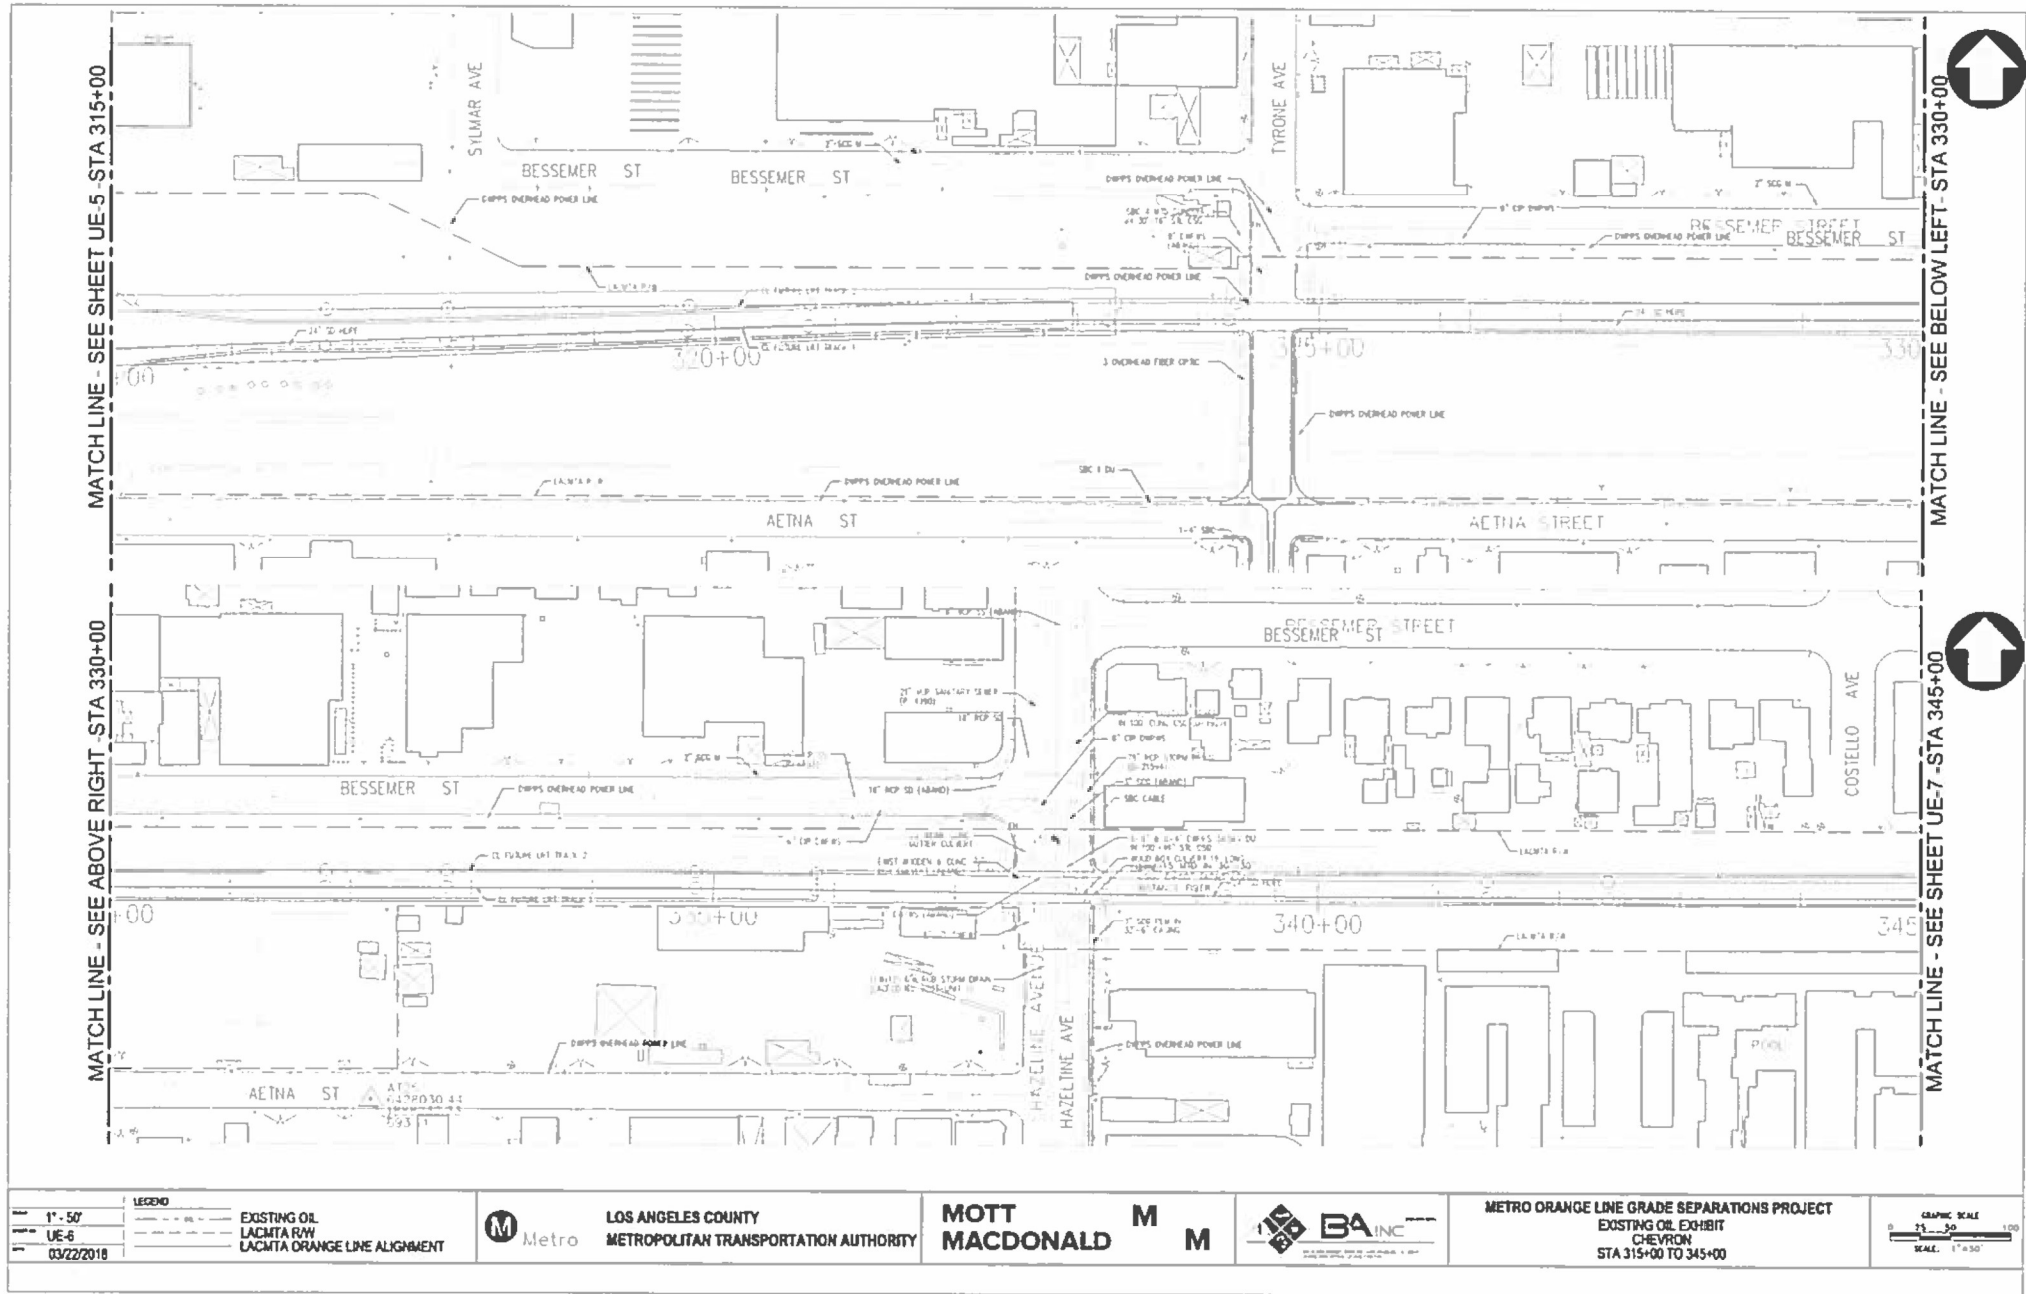

1" = 50' UE-6 03/22/2018 LEGEND --- EXISTING OIL LACMTA R/W --- LACMTA ORANGE LINE ALIGNMENT	M Metro LOS ANGELES COUNTY METROPOLITAN TRANSPORTATION AUTHORITY	MOTT MACDONALD M M	BA INC	METRO ORANGE LINE GRADE SEPARATIONS PROJECT EXISTING OIL EXHIBIT CHEVRON STA 315+00 TO 345+00	GRAPHIC SCALE 0 25 50 100 SCALE: 1" = 50'
---	---	----------------------------------	----------------------	--	--