


MATCH LINE - SEE SHEET UE-5 - STA 315+00

MATCH LINE - SEE ABOVE RIGHT - STA 330+00

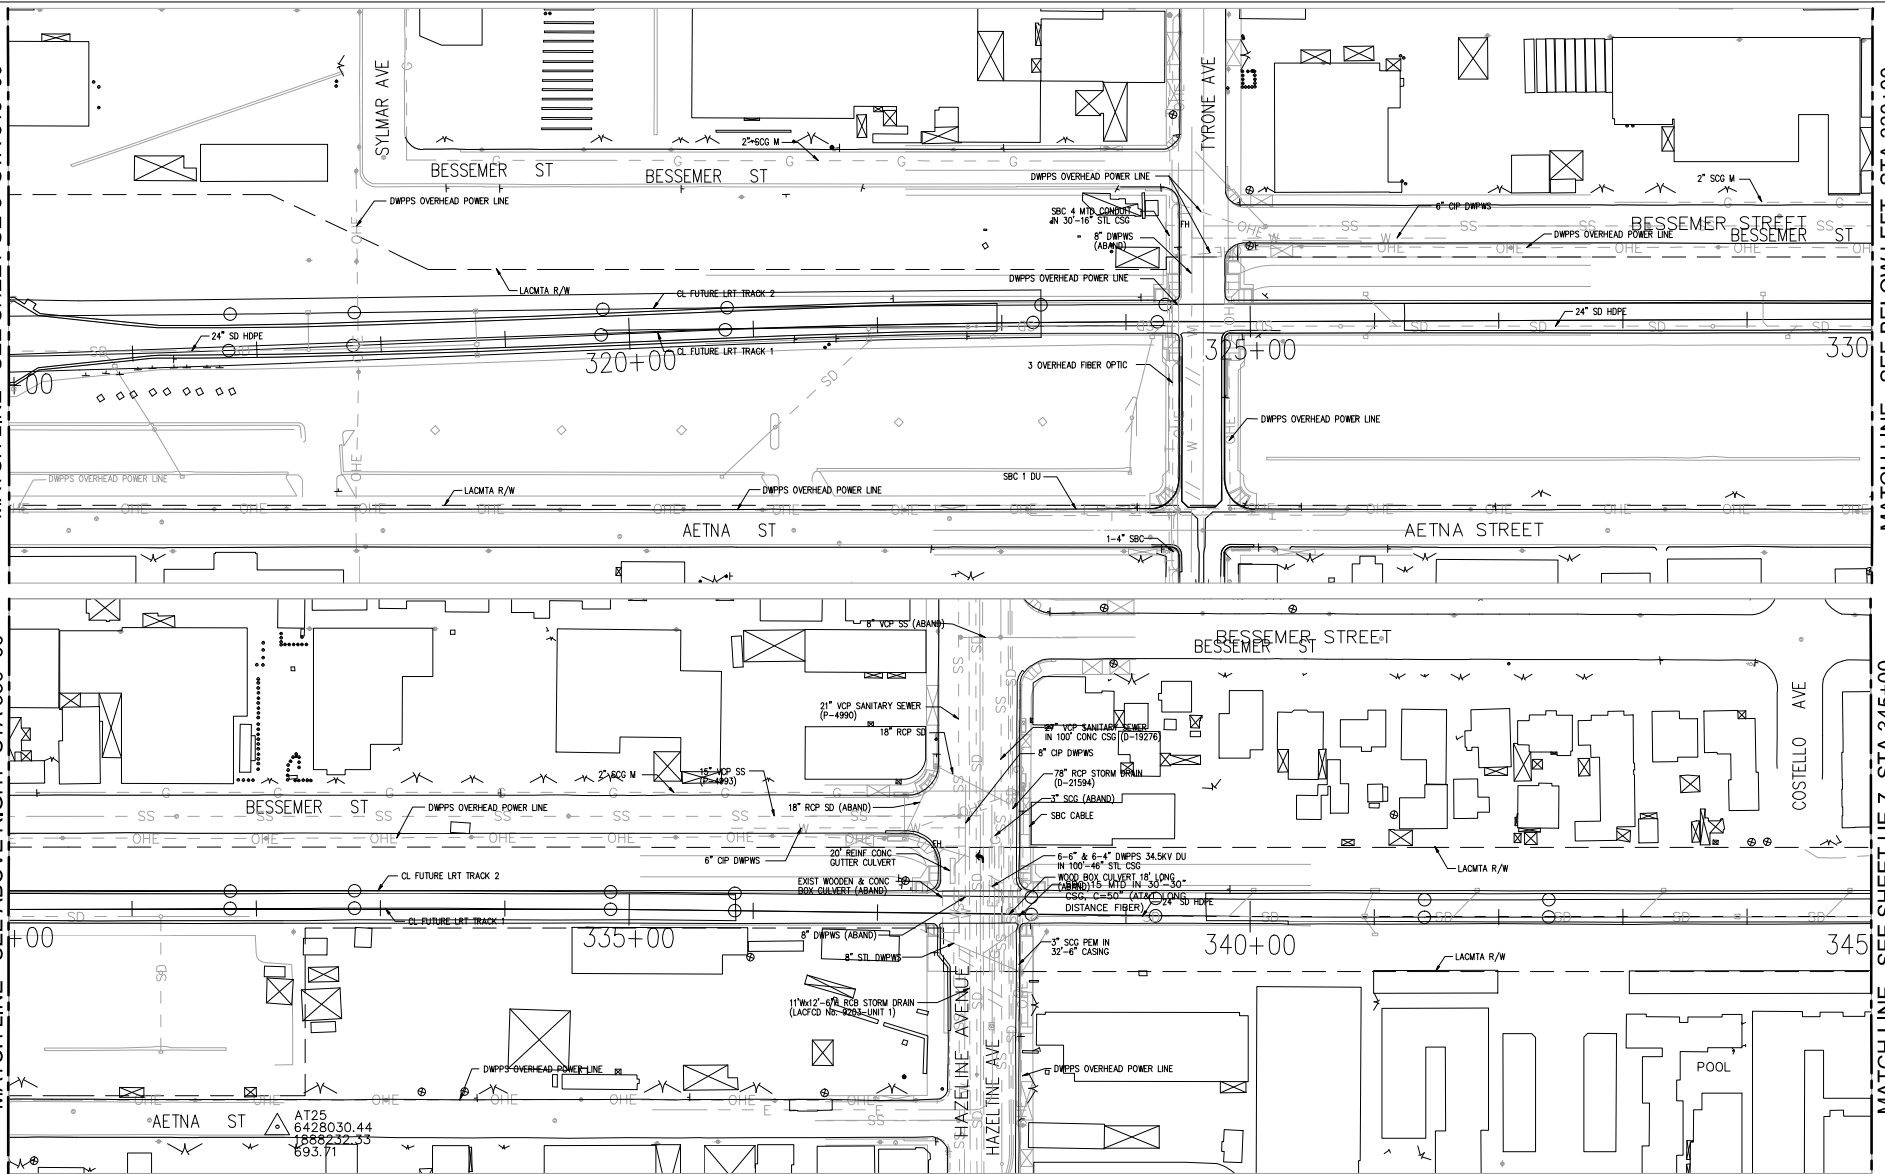

MATCH LINE - SEE BELOW LEFT - STA 330+00

MATCH LINE - SEE SHEET UE-7 - STA 345+00



SCALE	1" = 50'
REPORT NO.	UE-6
DATE	03/22/2018

LEGEND	
	EXISTING OIL
	LACMTA R/W
	LACMTA ORANGE LINE ALIGNMENT



LOS ANGELES COUNTY
METROPOLITAN TRANSPORTATION AUTHORITY

MOTT
MACDONALD



METRO ORANGE LINE GRADE SEPARATIONS PROJECT
EXISTING OIL EXHIBIT
SHELL OIL
STA 315+00 TO 345+00

