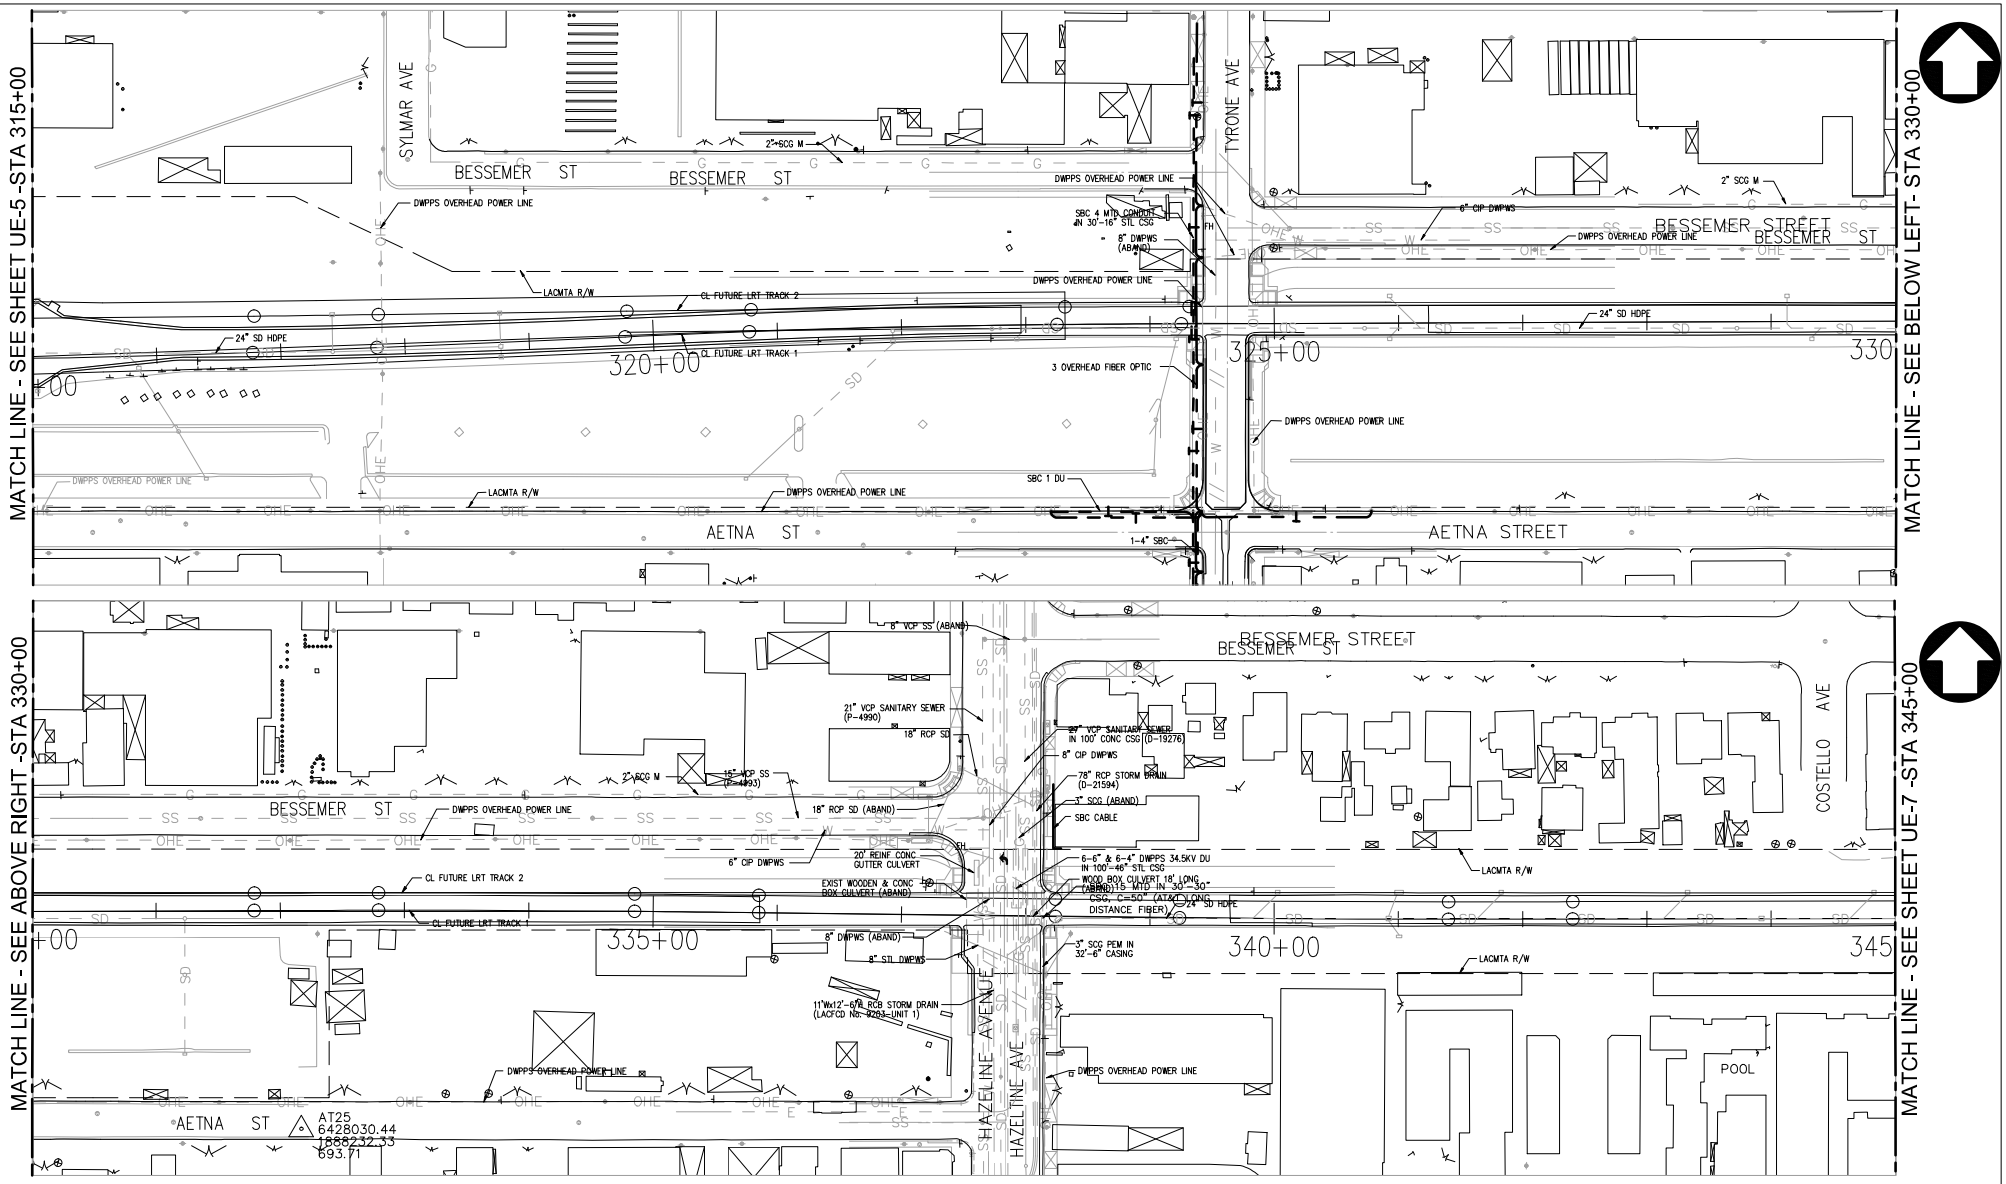

SCALE: 1" - 50' SHEET NO: UE-6 DATE: 03/22/2018	LEGEND EXISTING TELECOMMUNICATION LACMTA R/W LACMTA ORANGE LINE ALIGNMENT	Metro LOS ANGELES COUNTY METROPOLITAN TRANSPORTATION AUTHORITY	MOTT MACDONALD	BA INC	METRO ORANGE LINE GRADE SEPARATIONS PROJECT EXISTING TELECOMMUNICATION EXHIBIT WILCON-CROWN CASTLE FIBER STA 315+00 TO 345+00	GRAPHIC SCALE 0 25 50 100 SCALE: 1"=50'