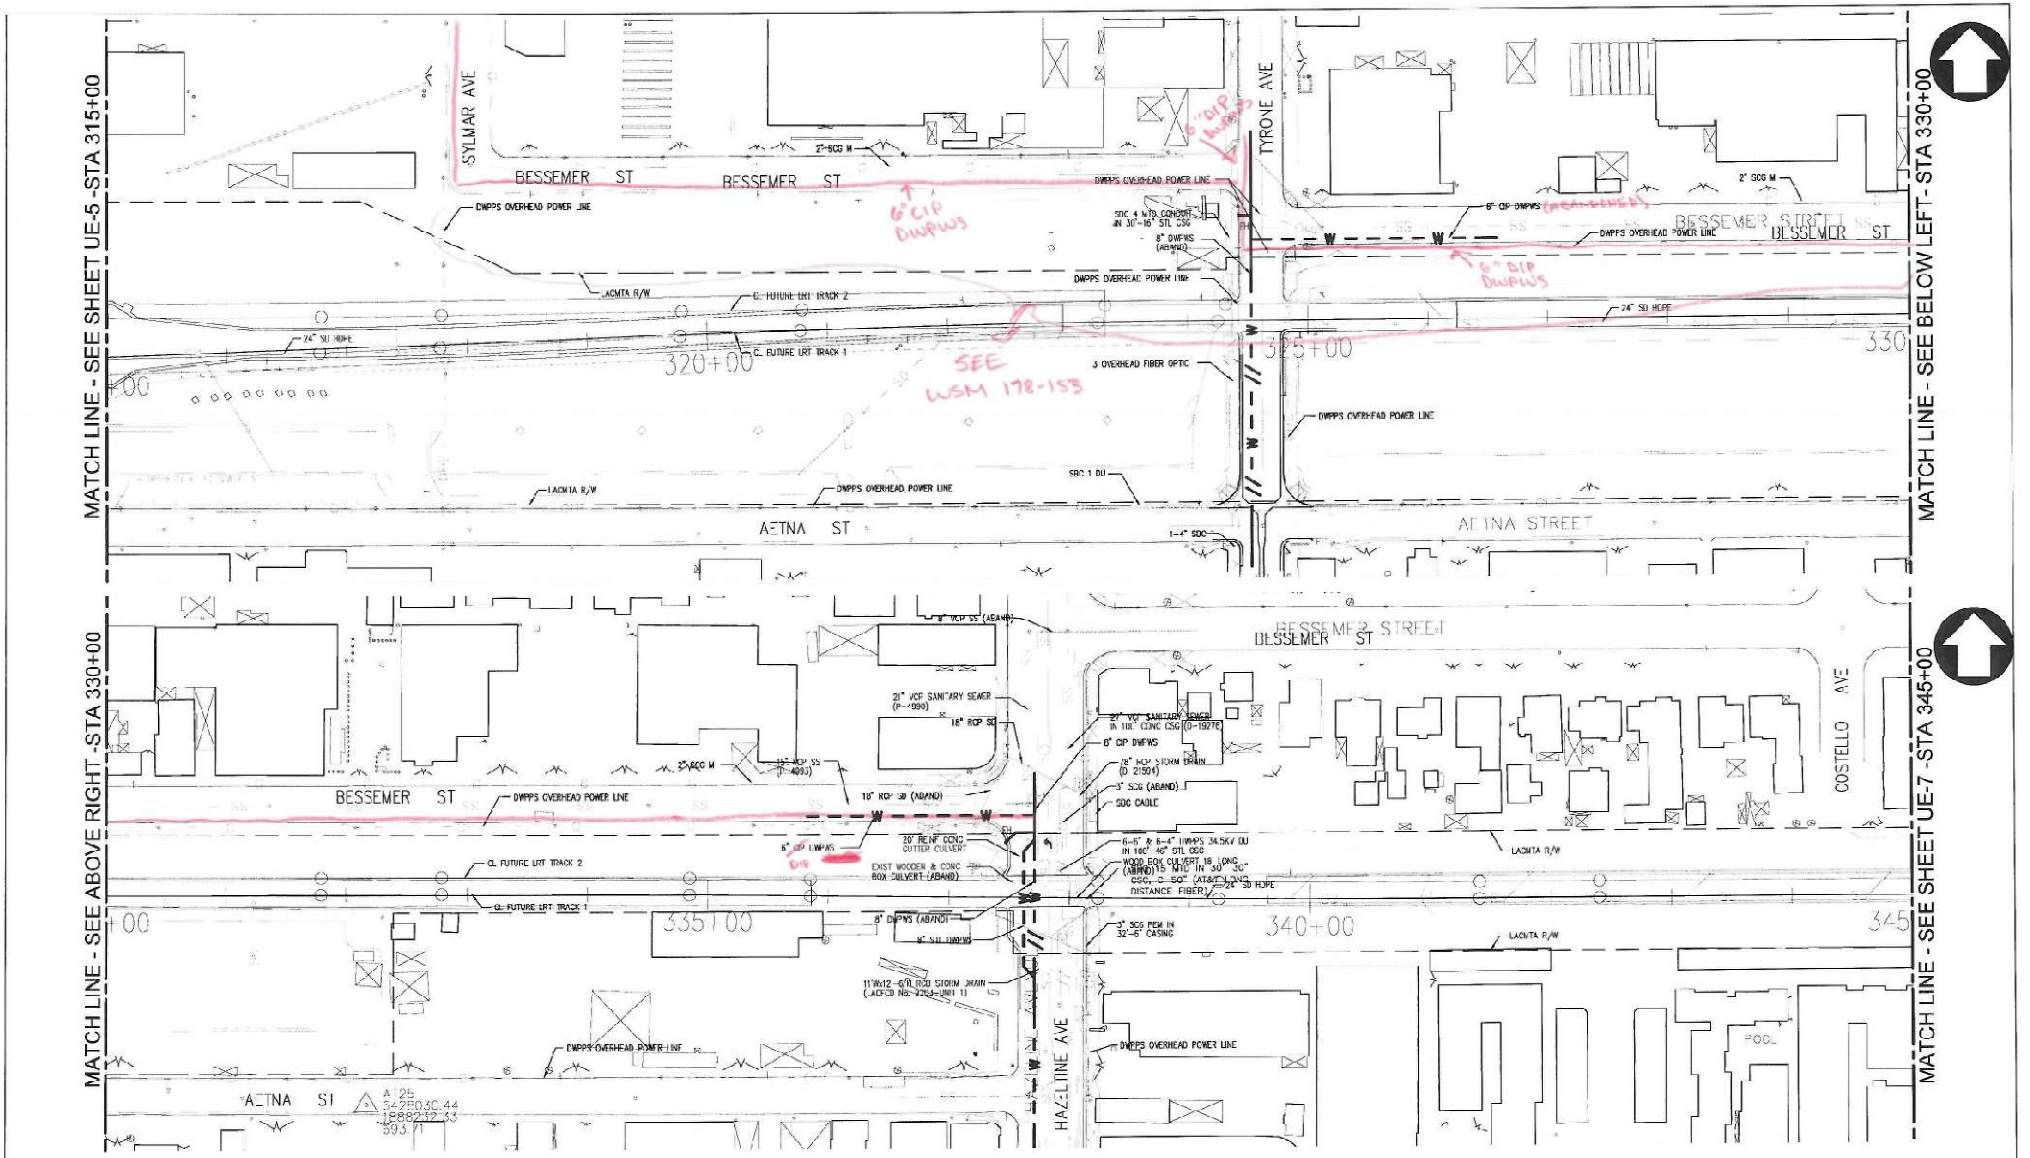

SCALE: 1" - 50'	LEGEND	Metro	LOS ANGELES COUNTY METROPOLITAN TRANSPORTATION AUTHORITY	MOTT MACDONALD	BA INC	METRO ORANGE LINE GRADE SEPARATIONS PROJECT
SHEET #: UE-6	EXISTING WATER					EXISTING WATER EXHIBIT
DATE: 03/22/2018	LACMTA R/W					LADWP-WS
	LACMTA ORANGE LINE ALIGNMENT					STA 315+00 TO 345+00

GRAPHIC SCALE 0 25 50 100 SCALE: 1"=50'