
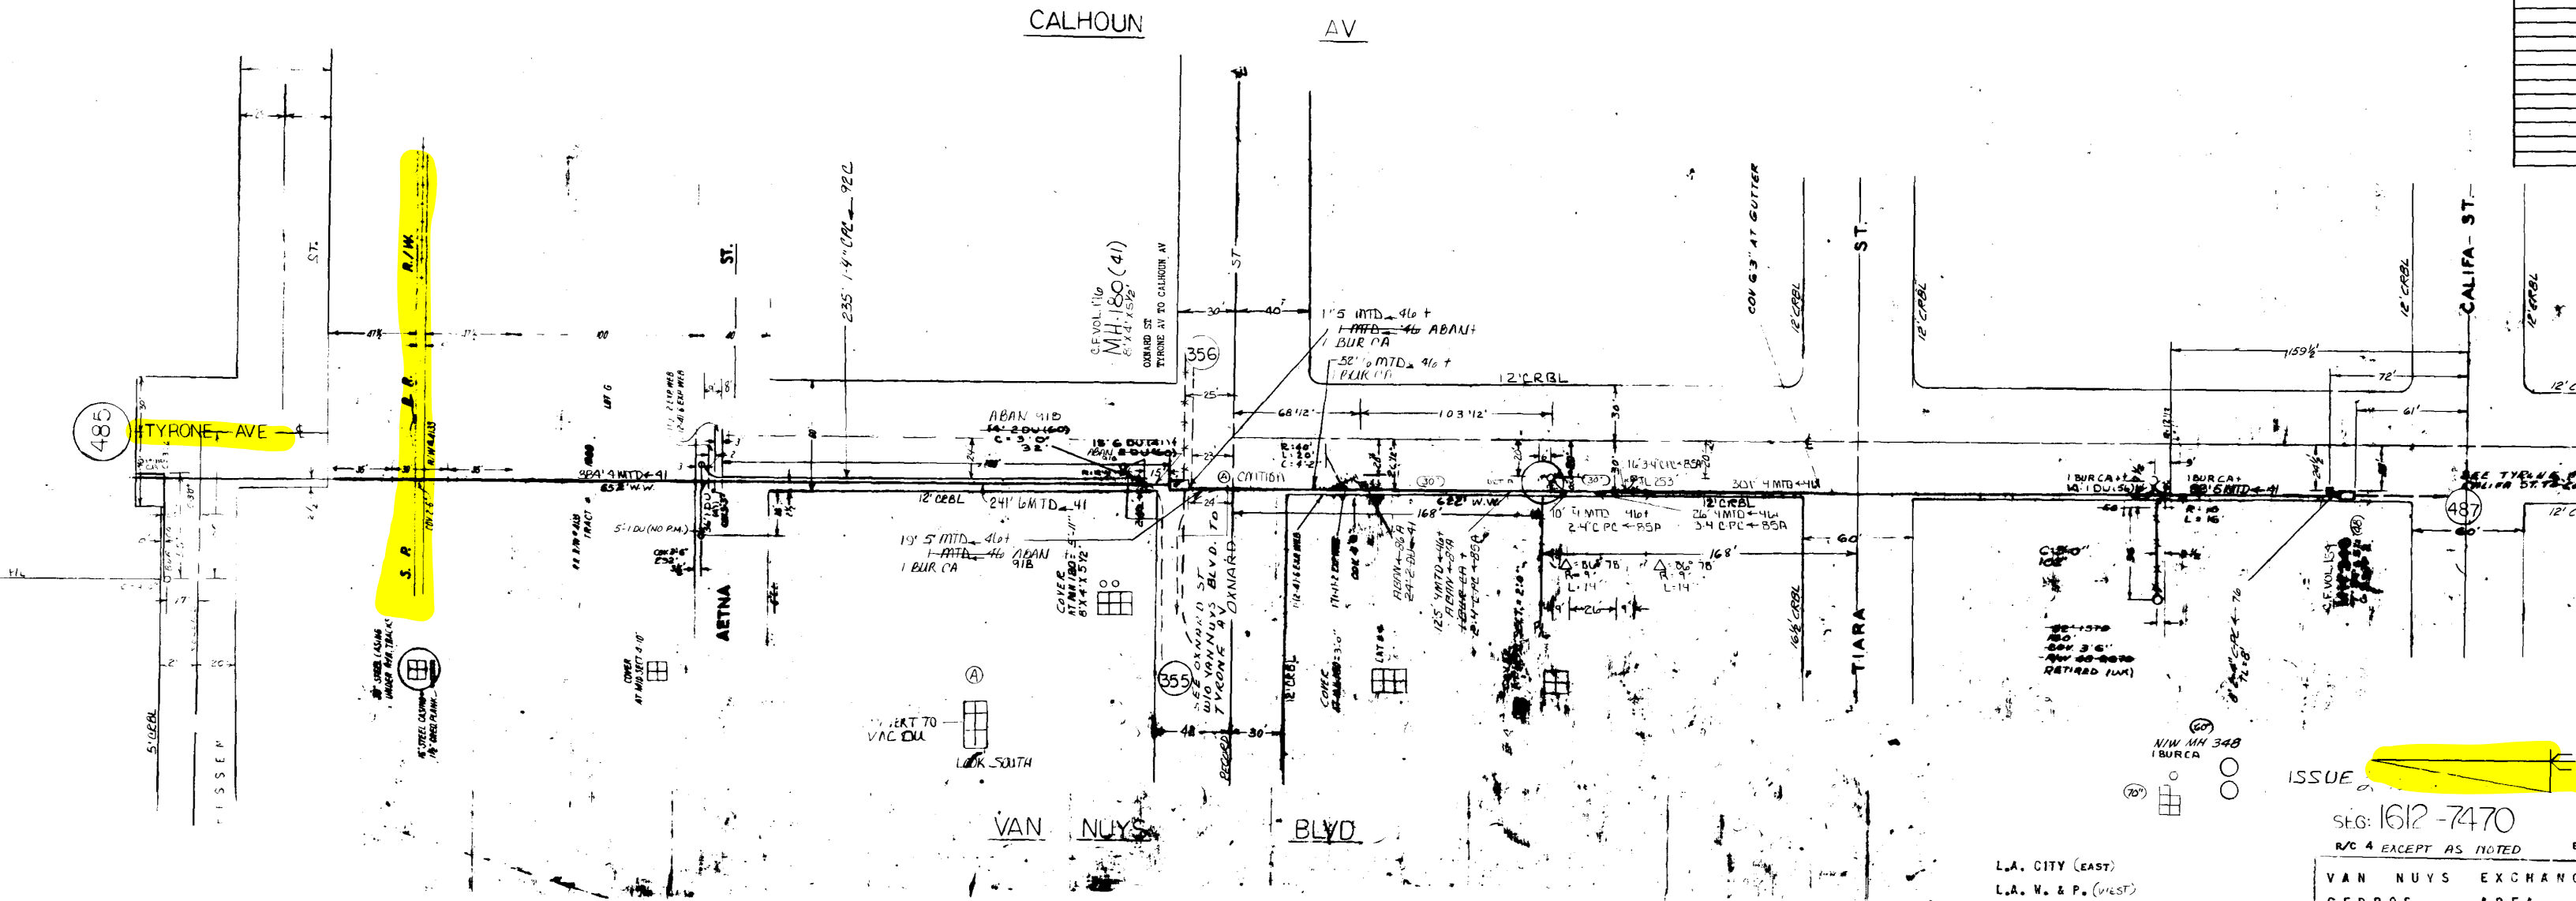


IN EFFECT	
REV	AUTHOR
CF0068	4-AUTHOR
(REF: B5P 928)	11/10/00
SUPERSEDES	
REVISED	
YR AUTH	

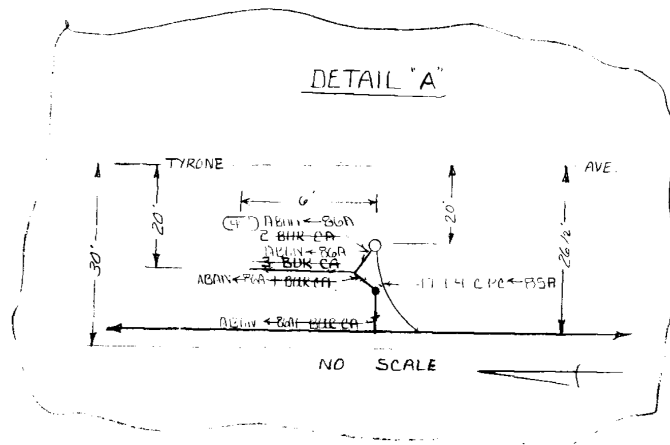

L.A. CITY (EAST)
L.A. W. & P. (WEST)

SEG: 1612-7470
R/C 4 EXCEPT AS NOTED
VAN NUYS EXCHANGE
CEDROS AREA
TYRONE AVENUE
BESSEMER ST. TO CALIFA ST.
SCALE 1" = 50'
THE PACIFIC TEL. AND TEL. CO.
CONDUIT
SUPERSEDES TYRONE AVE BESSEMER
CALIFA ST. (1-0-0)

CONDUIT CURVE DATA

$\Delta = 34^\circ$
 $R = 12'12"$
 $L = 7'16"$

$\Delta = 22^\circ 19' 54"$
 $R = 20'$
 $L = 8'$

PF 1982 (PR)

IN EFFECT

REVISION

AUTHORITY

CF006 (RE: 06001) (REF: BSP 9-8-80521 (1))


IN EFFECT

SUPERSEDES

REVISION

YR | AUTH

ACT

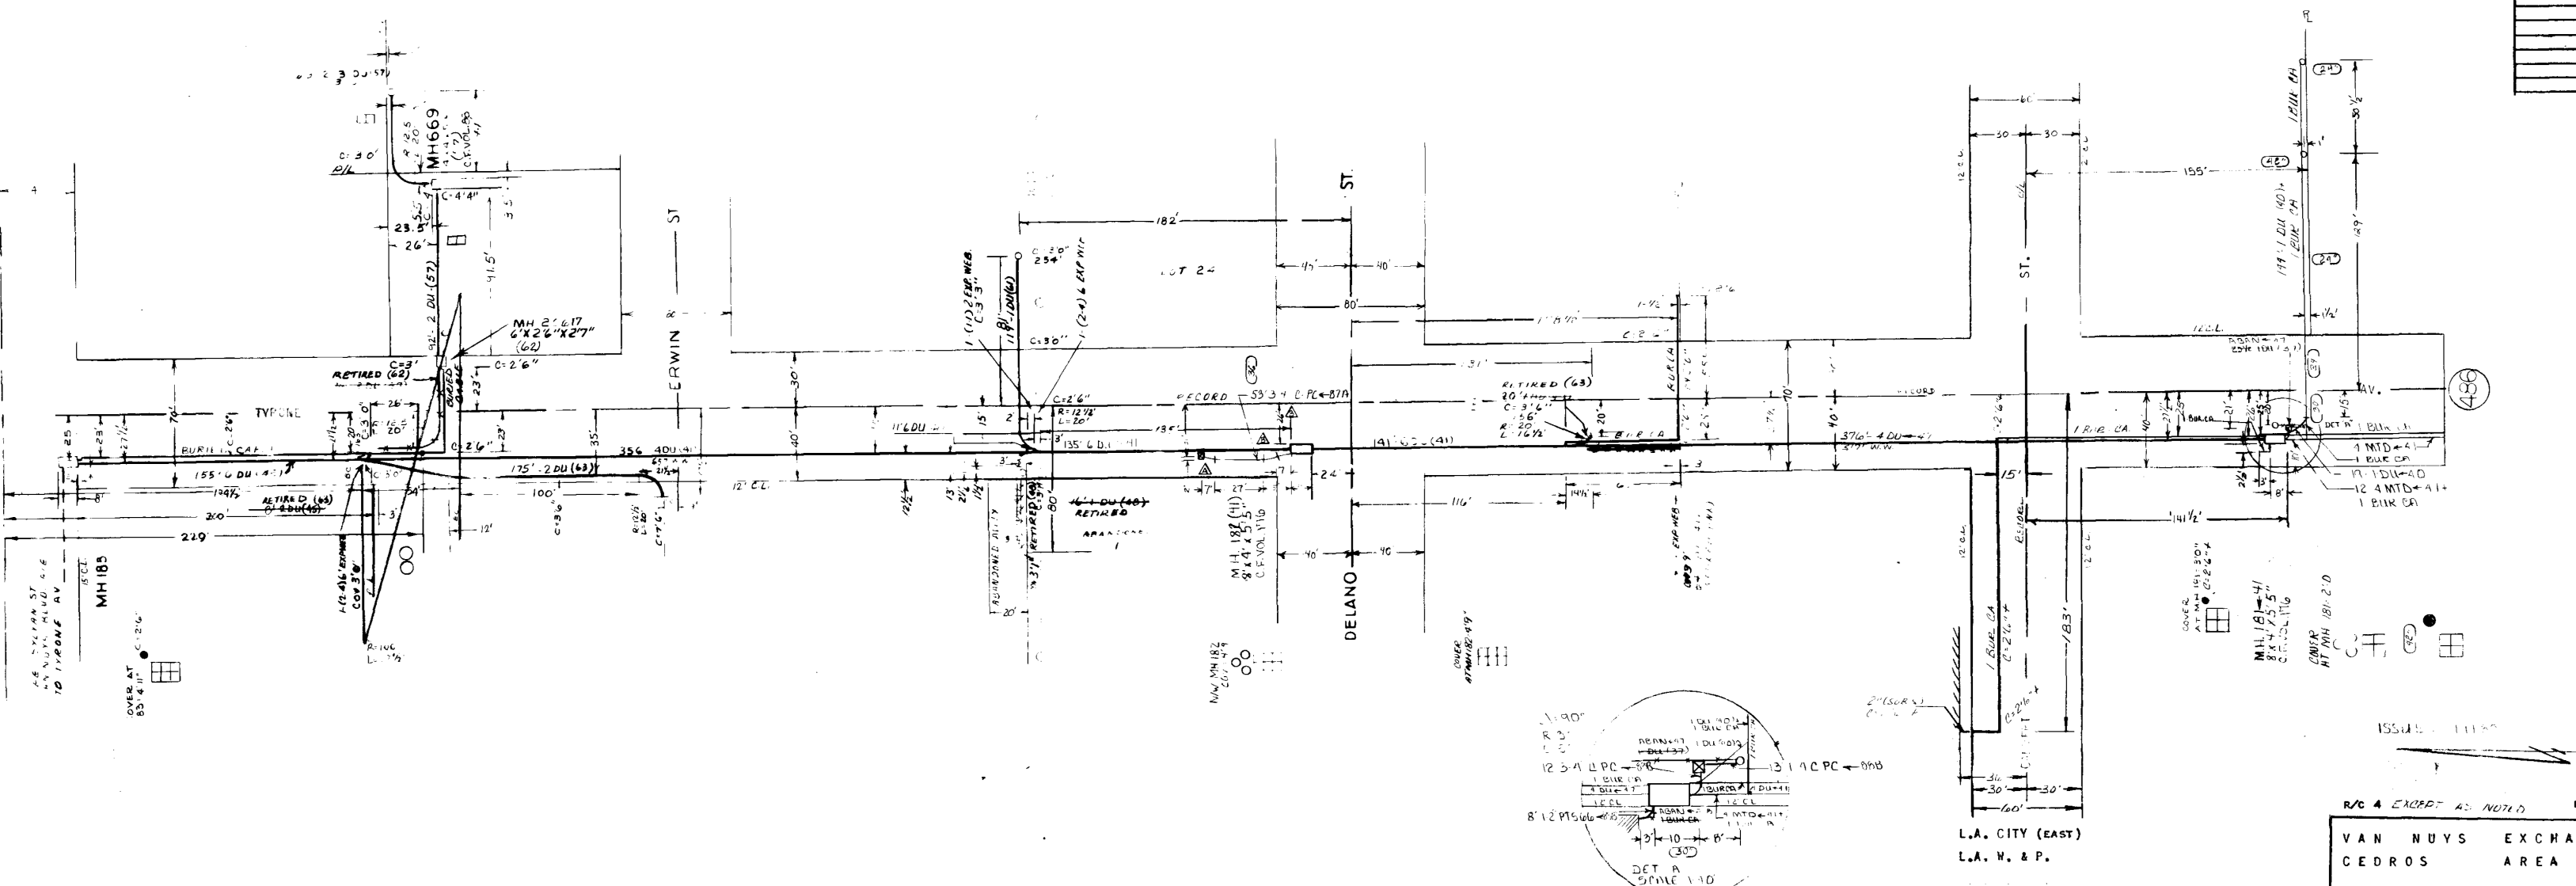

L.A. CITY (EAST)
 L.A. W. & P.

VITRIFIED CLAY DUCT
 BURIED CABLE

R/C 4 EXCEPT AS NOTED

VAN NUYS EXCHANGE
 CEDROS AREA

TYRONE AVENUE
 SYLVAN ST. TO BESSEMER ST.

SCALE 1" = 50'

THE PACIFIC TEL. AND TEL. CO.
 CONDUIT
 SUPERSEDES 108 (9-41)