


MATCH LINE - SEE SHEET UE-5 - STA 315+00

MATCH LINE - SEE ABOVE RIGHT - STA 330+00

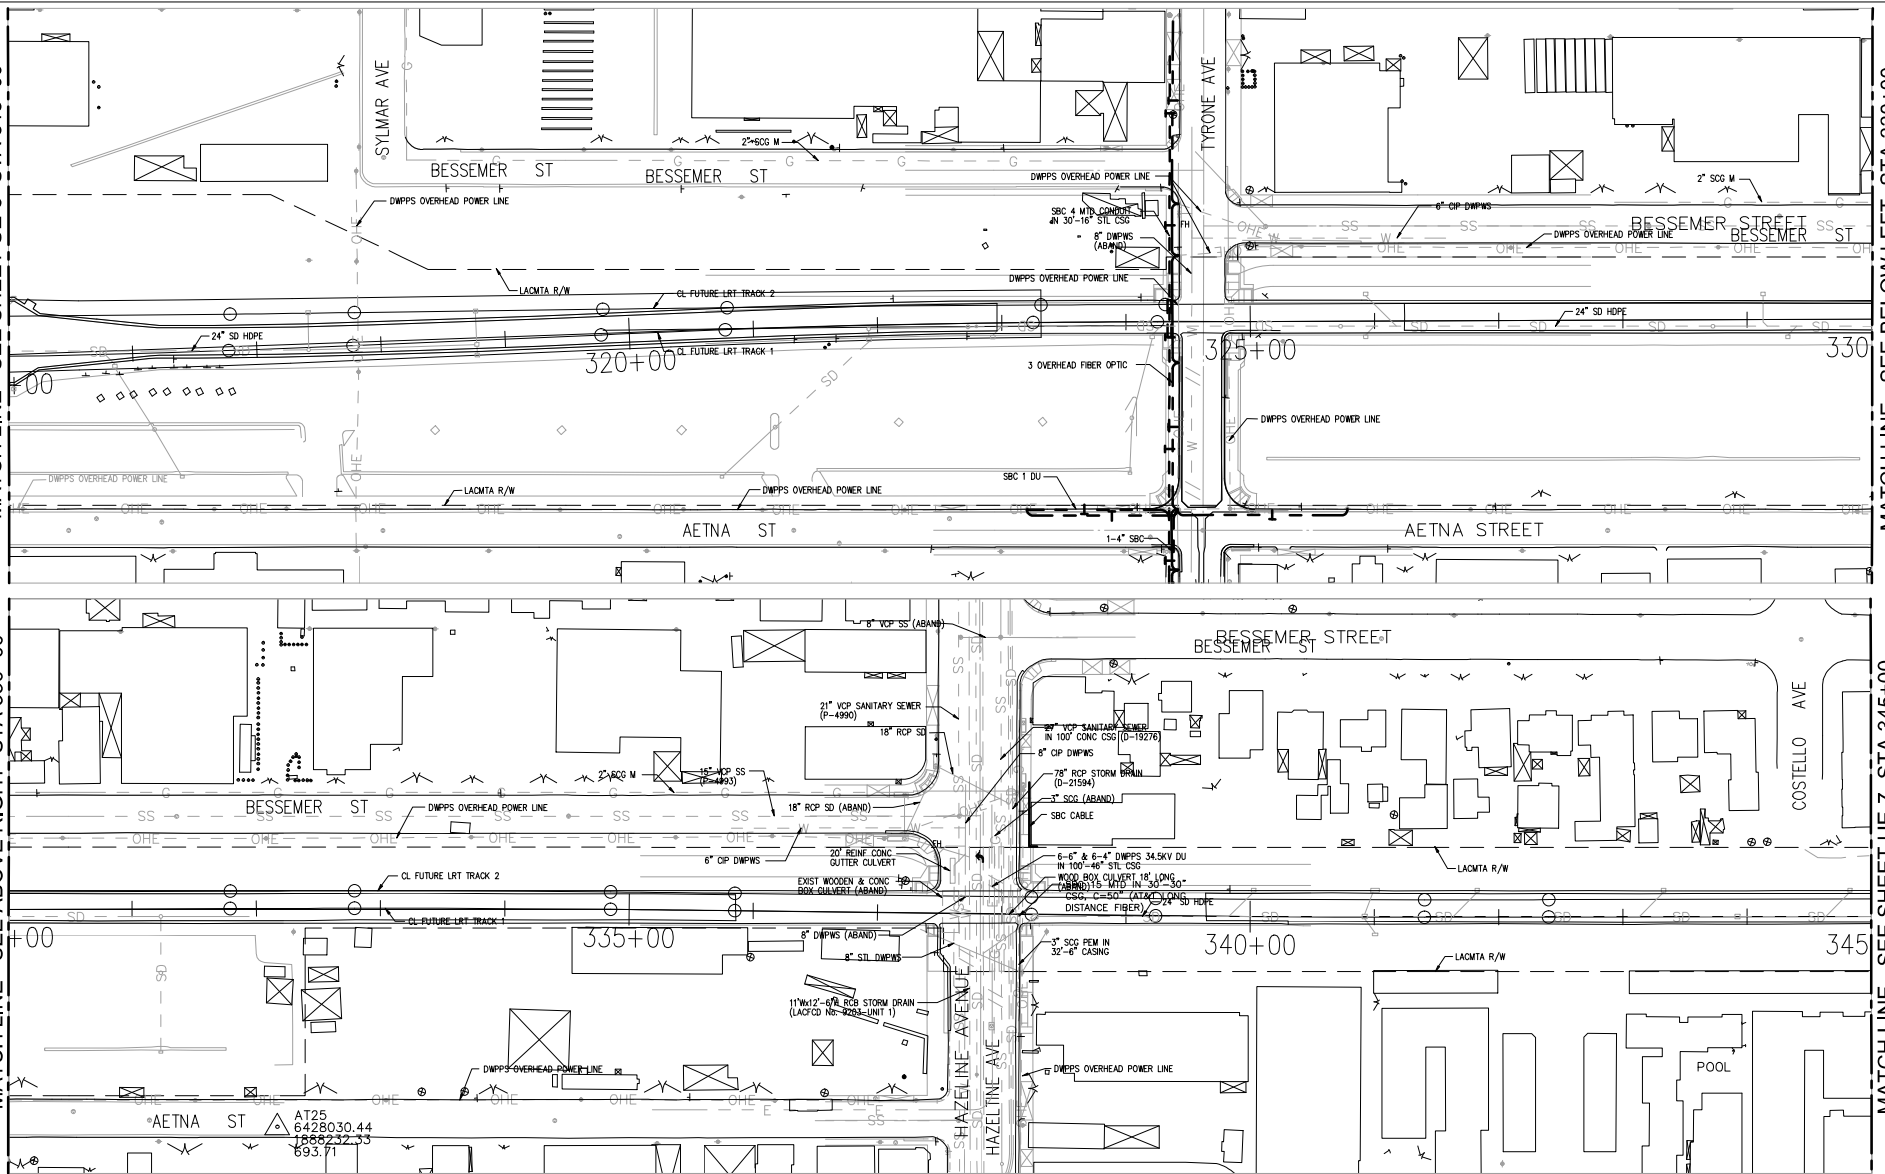

MATCH LINE - SEE BELOW LEFT - STA 330+00

MATCH LINE - SEE SHEET UE-7 - STA 345+00



SCALE	1" = 50'
DATE	03/22/2018
PROJECT	UE-6
LEGEND	
---	EXISTING TELECOMMUNICATION
---	LACMTA R/W
---	LACMTA ORANGE LINE ALIGNMENT

	LOS ANGELES COUNTY METROPOLITAN TRANSPORTATION AUTHORITY
--	---

	M M
--	--------

	BA INC
--	--------

METRO ORANGE LINE GRADE SEPARATIONS PROJECT EXISTING TELECOMMUNICATION EXHIBIT NEXT GLAVEN (CROWN CASTLE) STA 315+00 TO 345+00

GRAPHIC SCALE 0 25 50 100 SCALE: 1"=50'
