



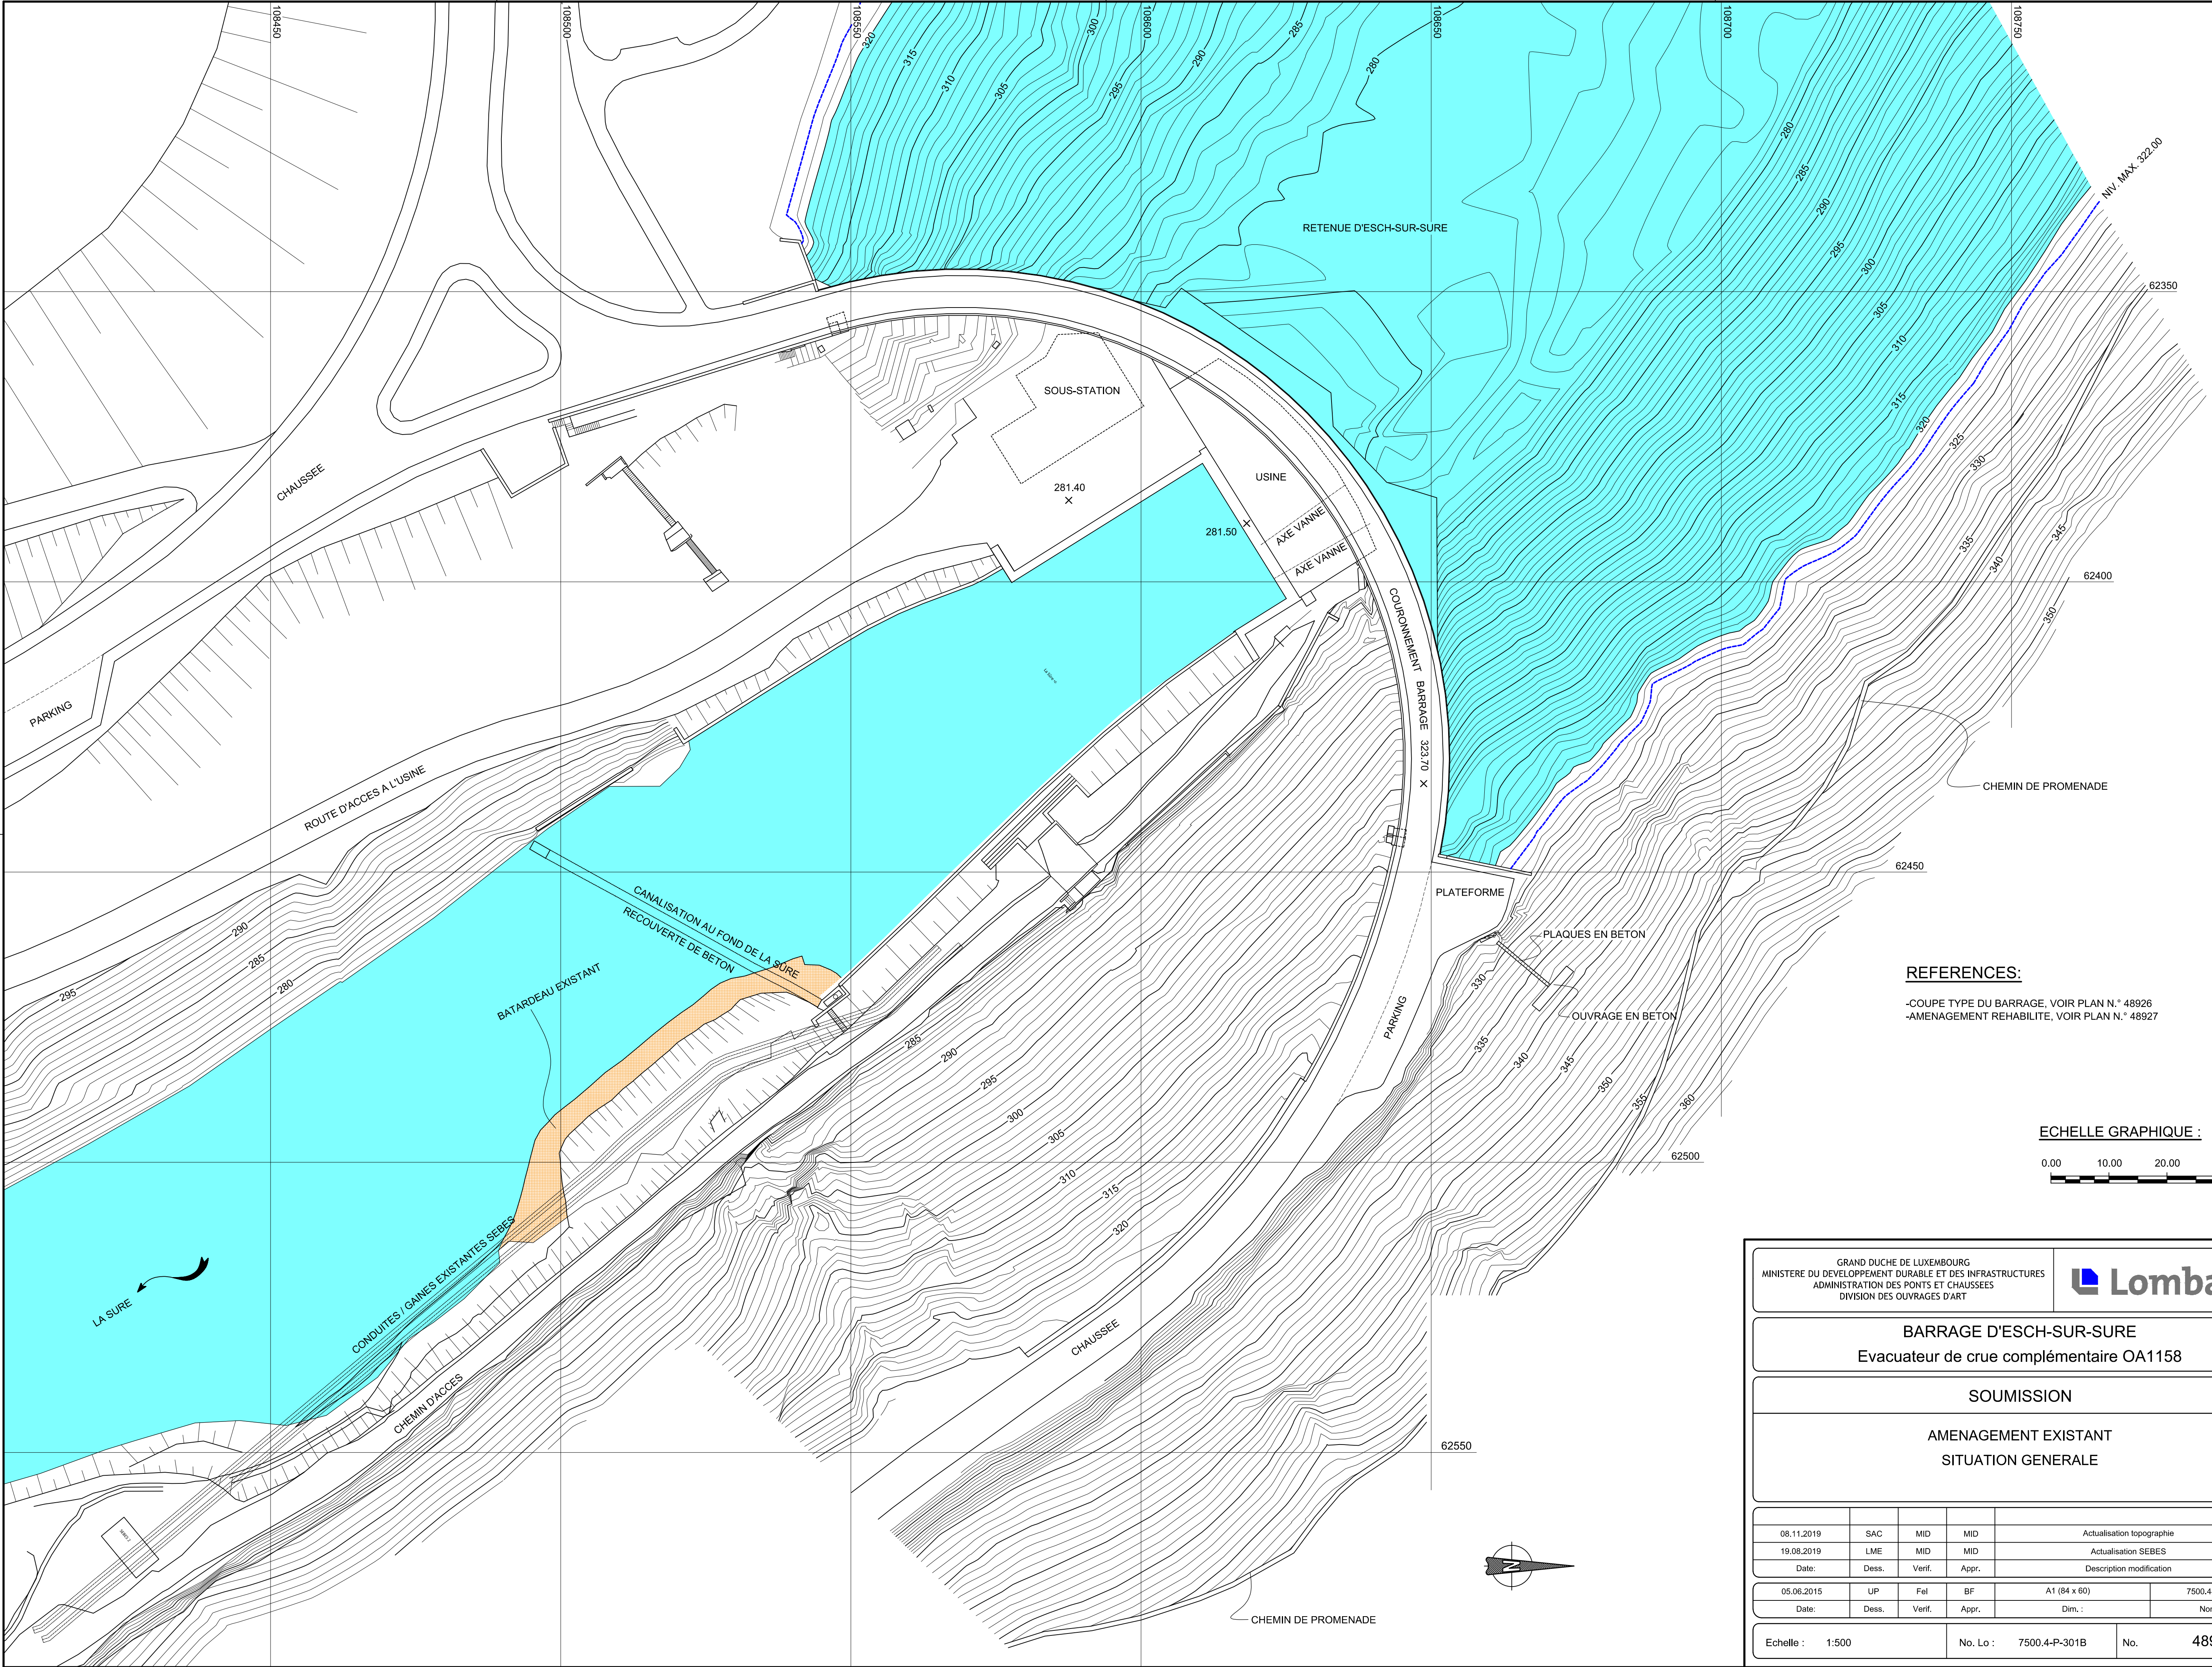

REFERENCES:
-COUPE TYPE DU BARRAGE, VOIR PLAN N.° 48926
-AMENAGEMENT REHABILE, VOIR PLAN N.° 48927

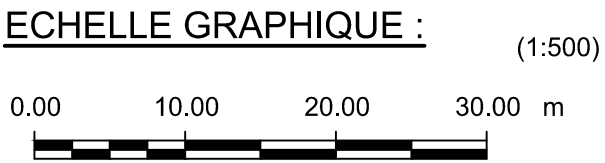

GRAND DUCHE DE LUXEMBOURG
MINISTRE DU DEVELOPPEMENT DURABLE ET DES INFRASTRUCTURES
ADMINISTRATION DES PONTS ET CHAUSSEES
DIVISION DES OUVRAGES D'ART

BARRAGE D'ESCH-SUR-SURE
Evacuateur de crue complémentaire OA1158

SOUMISSION

AMENAGEMENT EXISTANT
SITUATION GENERALE

08.11.2019	SAC	MID	MID	Actualisation topographie	C
19.08.2019	LME	MID	MID	Actualisation SEBES	B
Date:	Dess.	Verif.	Appr.	Description modification	A
05.06.2015	UP	Fel	BF	A1 (84 x 60)	7500.4-P-301B
Date:	Dess.	Verif.	Appr.	Dim. :	Nom fichier

Echelle : 1:500

No. Lo : 7500.4-P-301B

No. 48925

B