


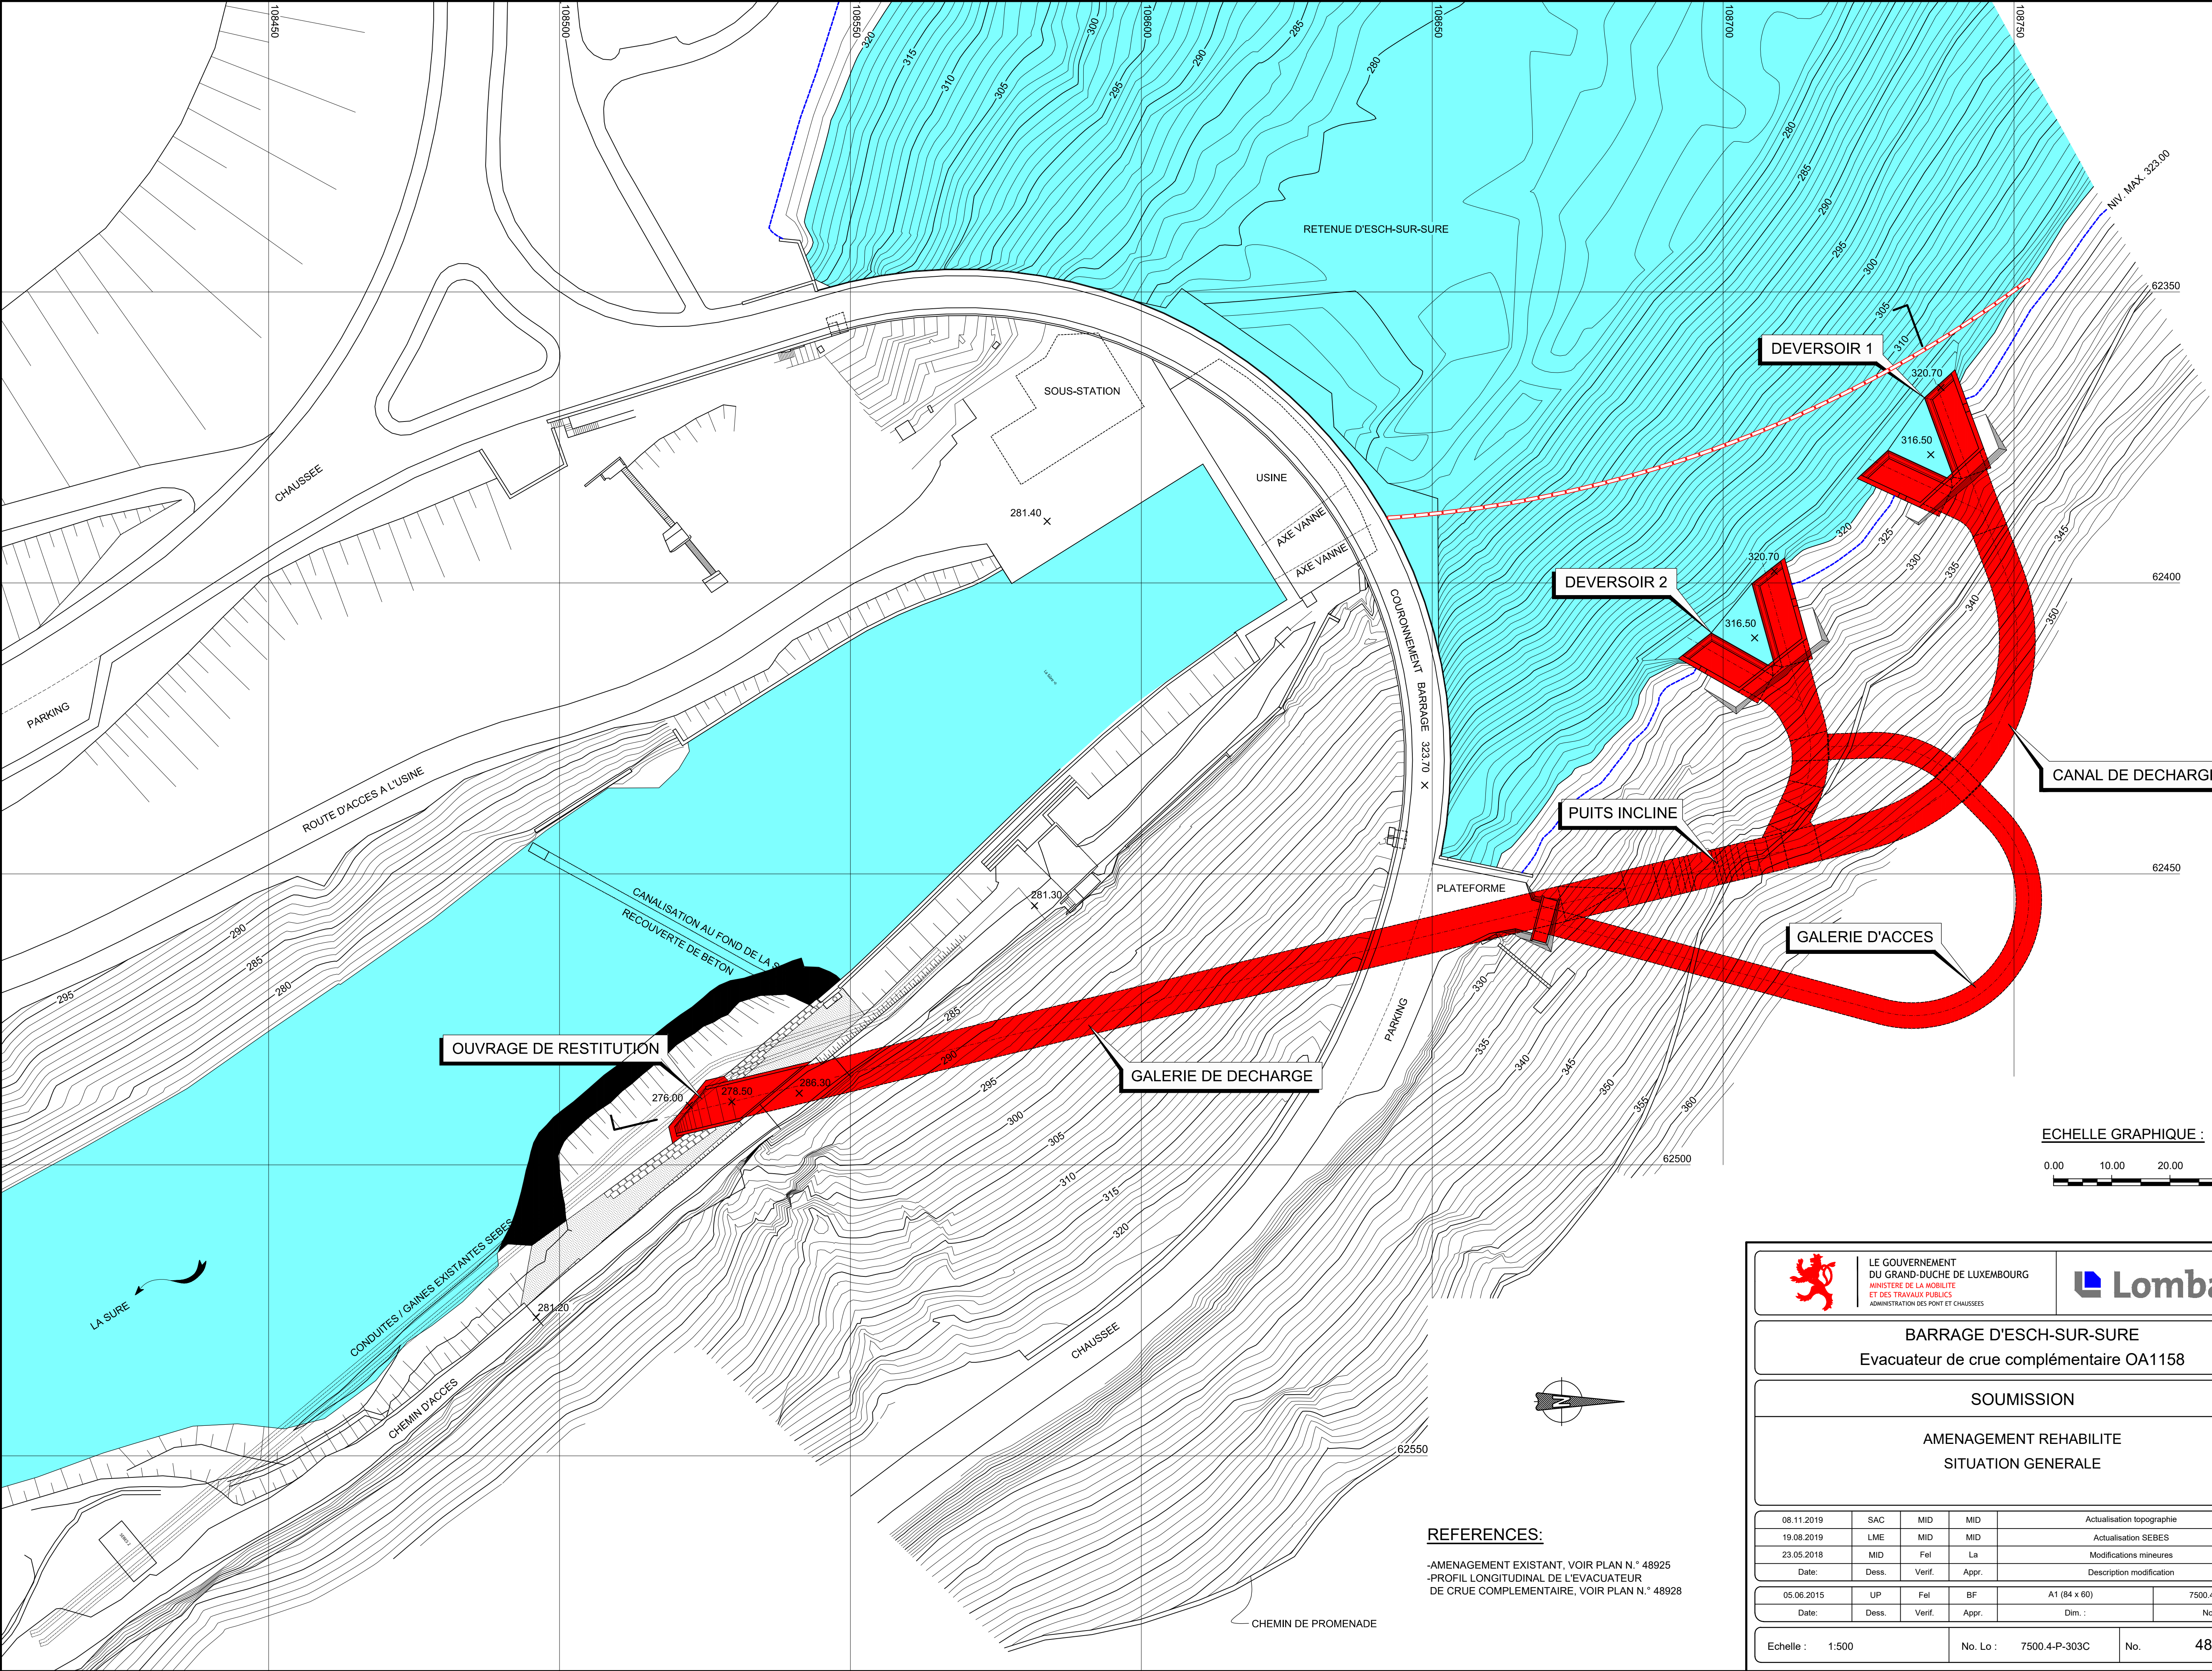

REFERENCES:

-AMENAGEMENT EXISTANT, VOIR PLAN N.° 48925
-PROFIL LONGITUDINAL DE L'EVACUATEUR
DE CRUE COMPLEMENTAIRE, VOIR PLAN N.° 48928



LE GOUVERNEMENT
DU GRAND-DUCHÉ DE LUXEMBOURG
MINISTÈRE DE LA MOBILITÉ
ET DES TRAVAUX PUBLICS
ADMINISTRATION DES PONTS ET CHAUSSEES



BARRAGE D'ESCH-SUR-SURE
Evacuateur de crue complémentaire OA1158

SOUSSION

AMENAGEMENT REHABILE
SITUATION GENERALE

08.11.2019	SAC	MID	MID	Actualisation topographie	C
19.08.2019	LME	MID	MID	Actualisation SEBES	B
23.05.2018	MID	Fel	La	Modifications mineures	A
Date:	Dess.	Verif.	Appr.	Description modification	
05.06.2015	UP	Fel	BF	A1 (84 x 60)	7500.4-P-303C
Date:	Dess.	Verif.	Appr.	Dim. :	Nom fichier

Echelle : 1:500

No. Lo : 7500.4-P-303C

No. 48927

C