



COMPORTEMENT DE LA RETENUE DE BAVIGNE DANS
LES CONFIGURATIONS ACTUELLE ET REHABILITEE
DU BARRAGE D'ESCH-SUR-SÛRE

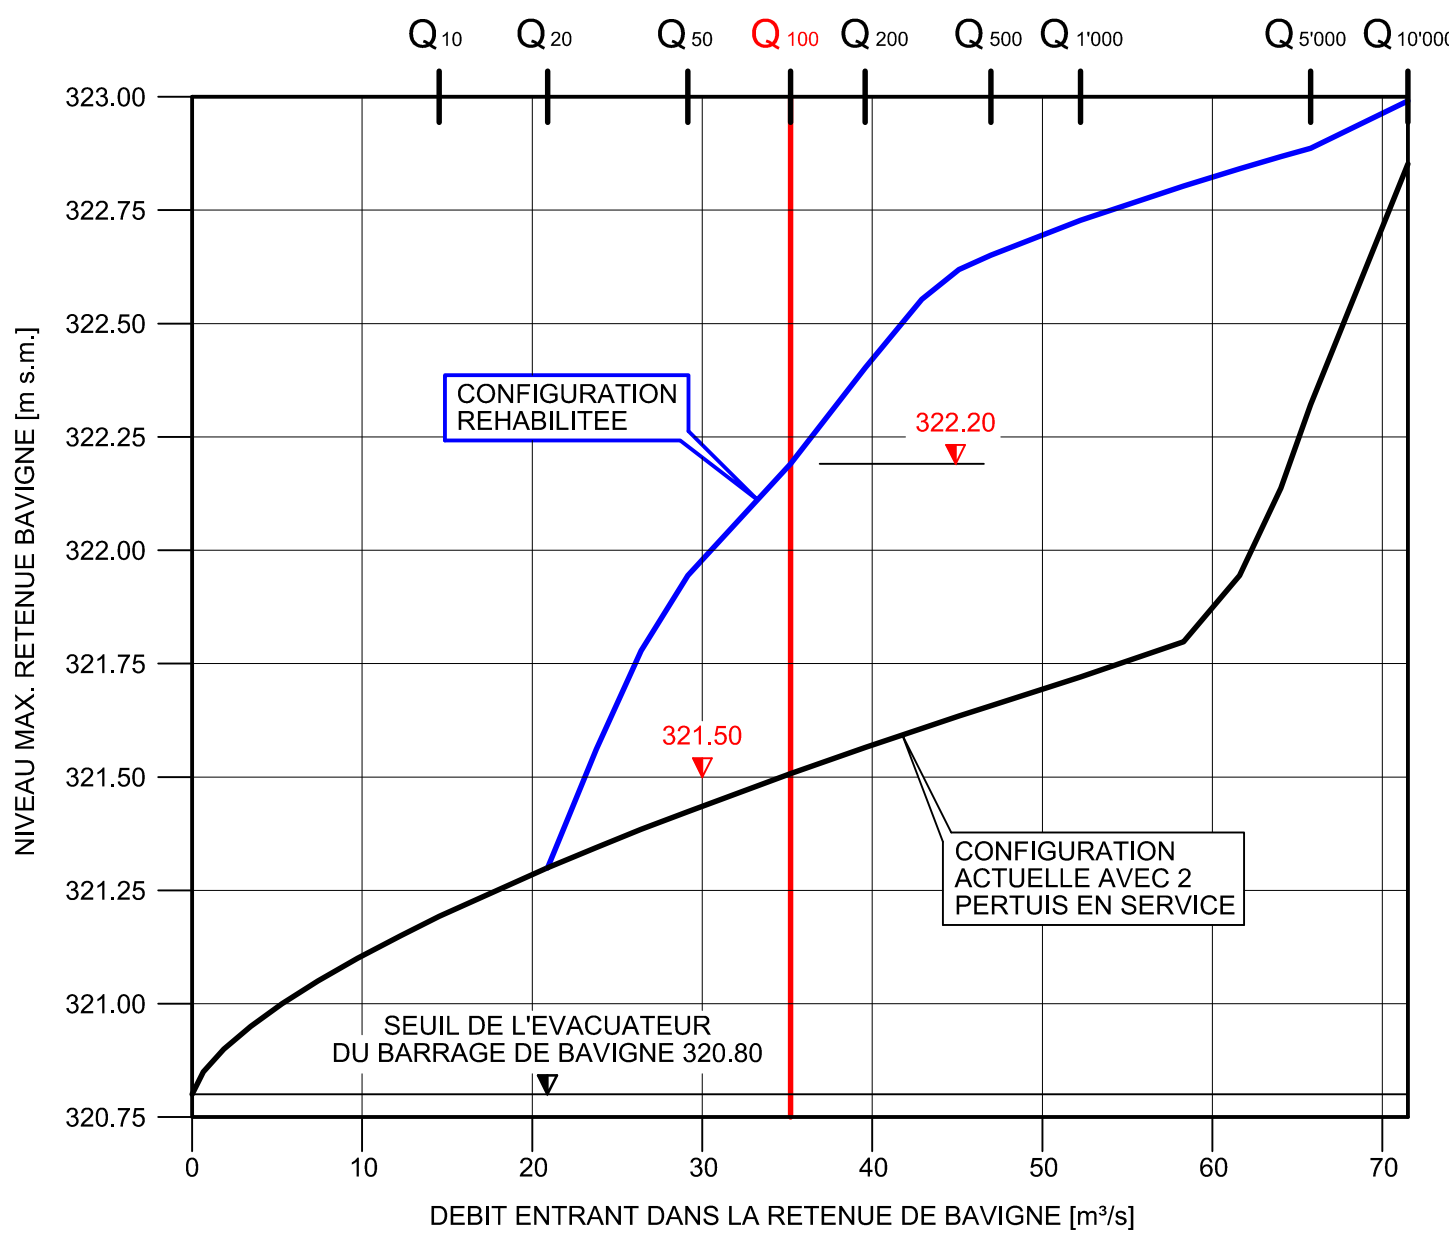


SITUATION BAVIGNE

(1:750)

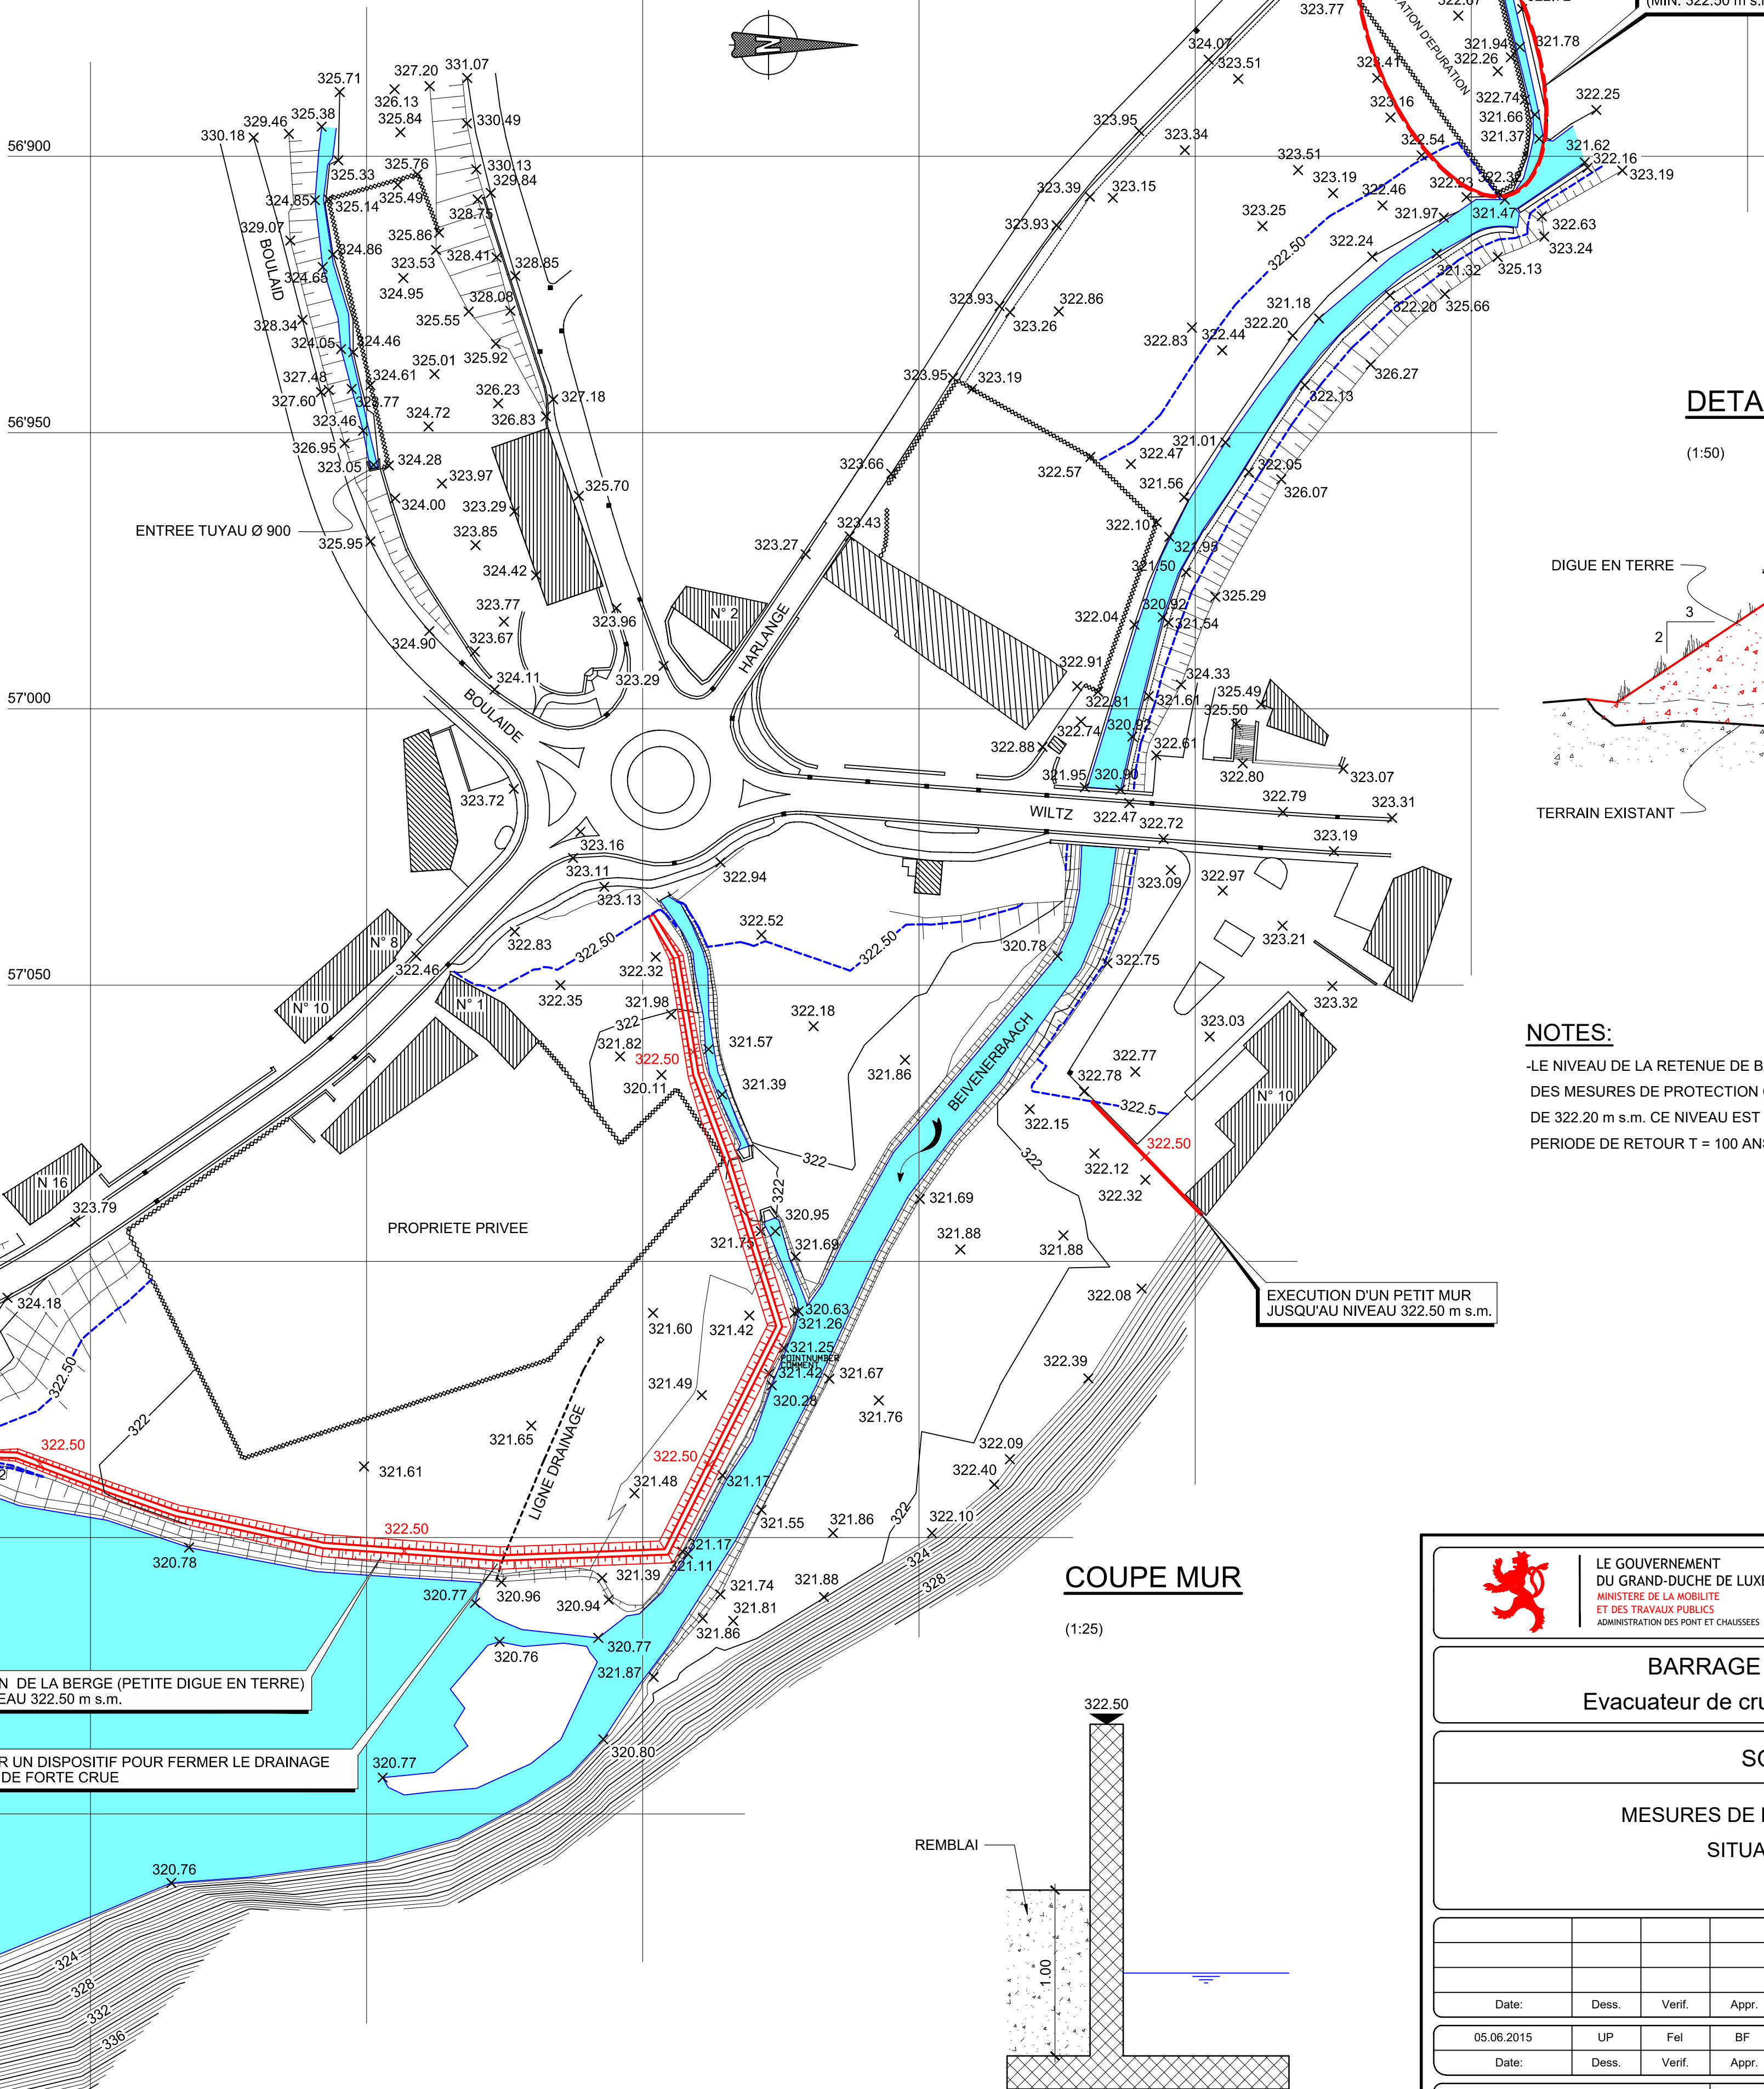

DETAIL DE LA DIGUE


(1:50)

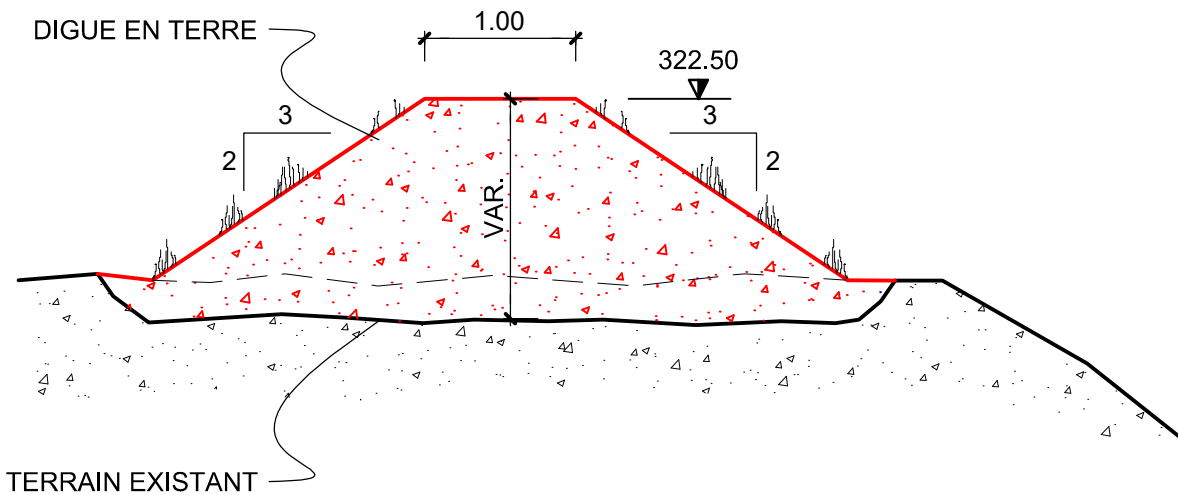

NOTES:


-LE NIVEAU DE LA RETENUE DE BAVIGNE RETENU POUR LE DIMENSIONNEMENT
DES MESURES DE PROTECTION CONTRE LES INONDATIONS EST
DE 322.20 m s.m. CE NIVEAU EST ASSOCIE A UN EVENEMENT DE CRUE AVEC UNE
PERIODE DE RETOUR T = 100 ANS

ECHELLES GRAPHIQUES :

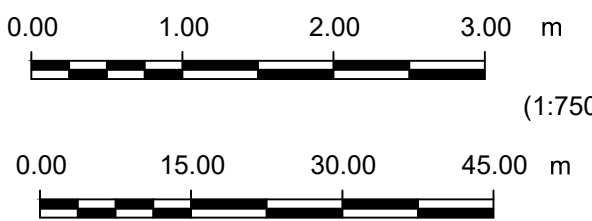

COUPE MUR

(1:25)

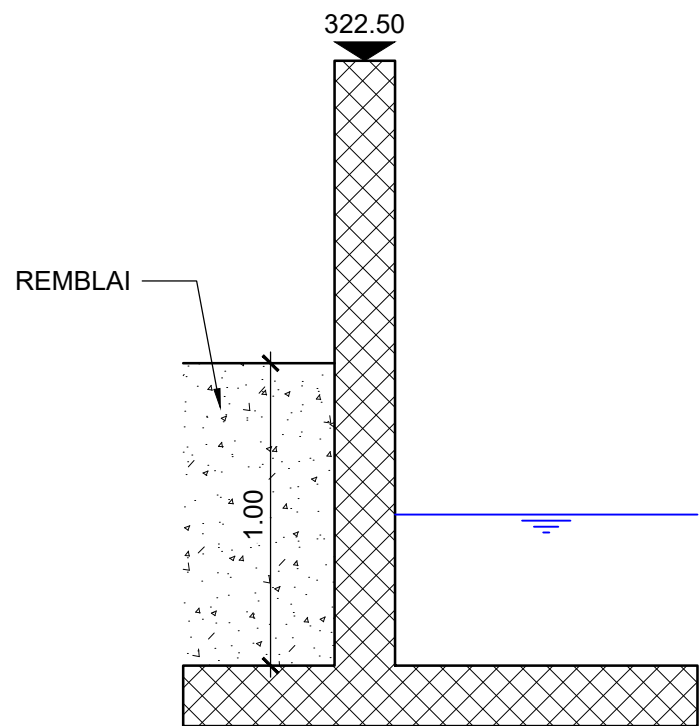

		LE GOUVERNEMENT DU GRAND-DUCHÉ DE LUXEMBOURG MINISTÈRE DE LA MOBILITÉ ET DES TRAVAUX PUBLICS ADMINISTRATION DES PONTS ET CHAUSSEES																					
BARRAGE D'ESCH-SUR-SÛRE Evacuateur de crue complémentaire OA1158																							
SOUSSION																							
MESURES DE PROTECTION A BAVIGNE SITUATION ET DETAIL																							
<table><tr><td></td><td></td><td></td><td></td><td></td><td>C</td></tr><tr><td></td><td></td><td></td><td></td><td></td><td>B</td></tr><tr><td></td><td></td><td></td><td></td><td></td><td>A</td></tr></table>											C						B						A
					C																		
					B																		
					A																		
Date:		Dess.	Verif.	Appr.	Description modification																		
05.06.2015		UP	Fel	BF	A1 (84 x 60) 7500.4-P-307																		
Date:		Dess.	Verif.	Appr.	Dim. : Nom fichier																		
Echelle : 1:750, 1:50		No. Lo : 7500.4-P-307		No.	48929																		