



ROCHE BONNE

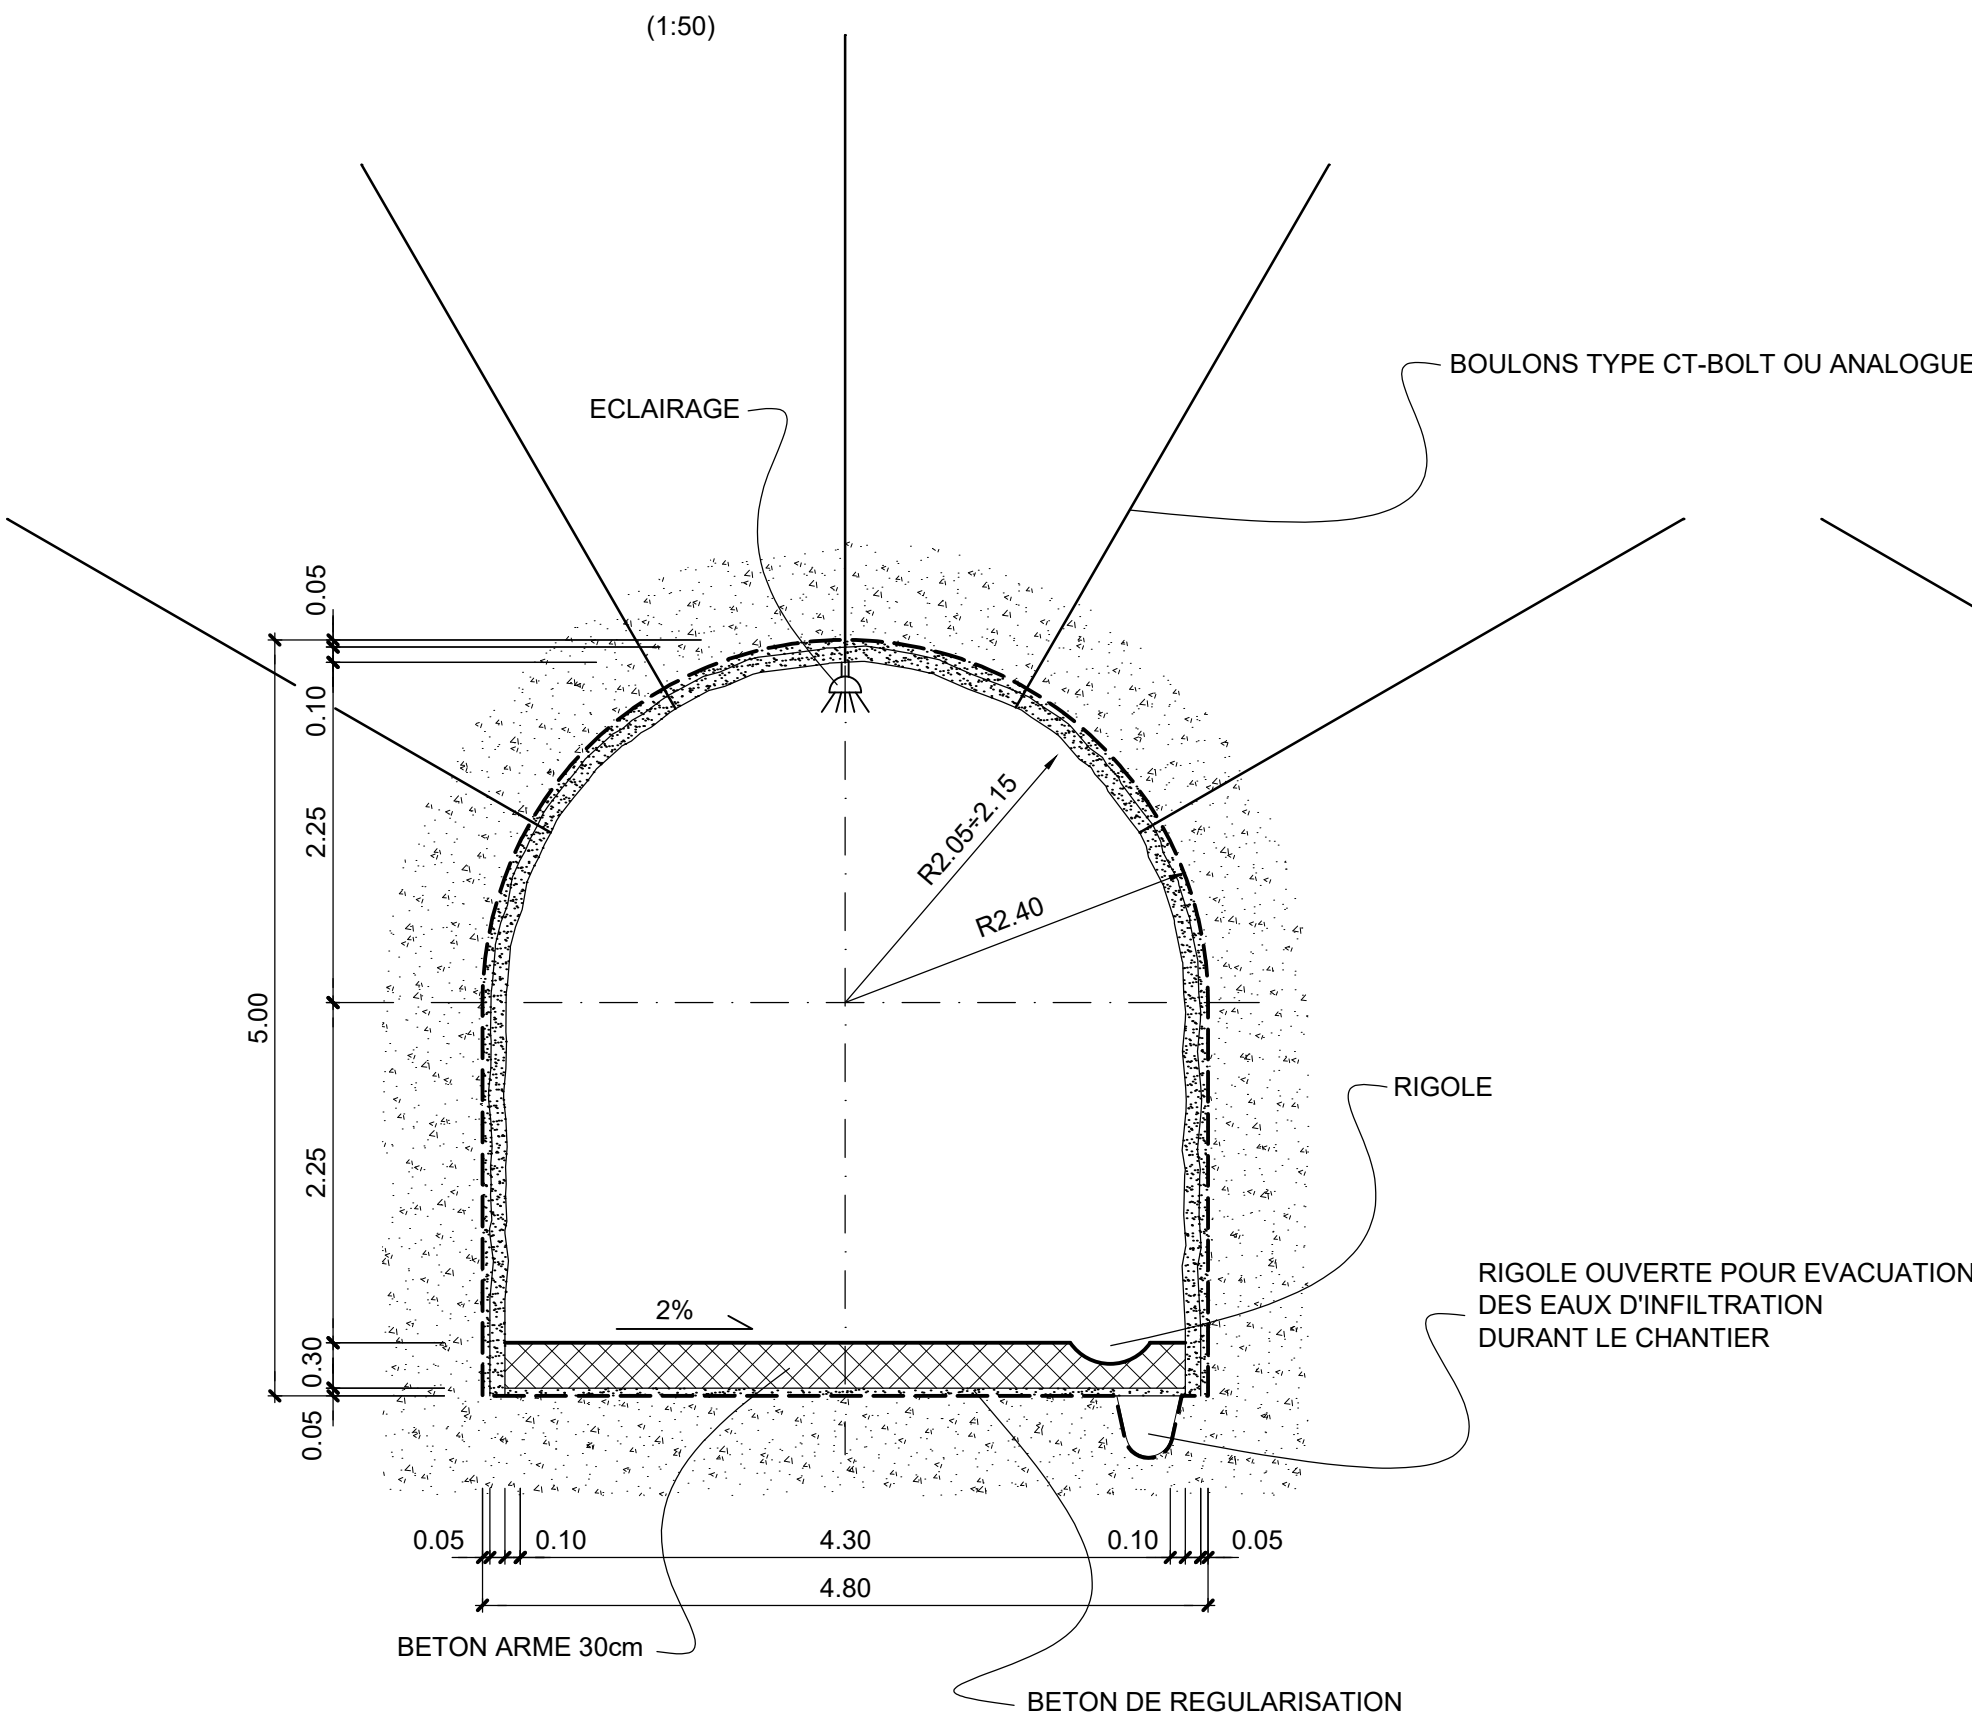


- SOUTÈNEMENT (PAR MÈTRE LINÉAIRE)**
- 5 cm BÉTON PROJETÉ AVEC FIBRES D'ACIER
 - 5/4 BOULONS CT BOLT OU ANALOGUE
- REVÈTEMENT DÉFINITIF**
- 30 cm DE BÉTON ARME
 - 10 cm BÉTON PROJETÉ:
 - 7 cm AVEC FIBRES
 - 3 cm SANS FIBRES

ROCHE MOYENNE

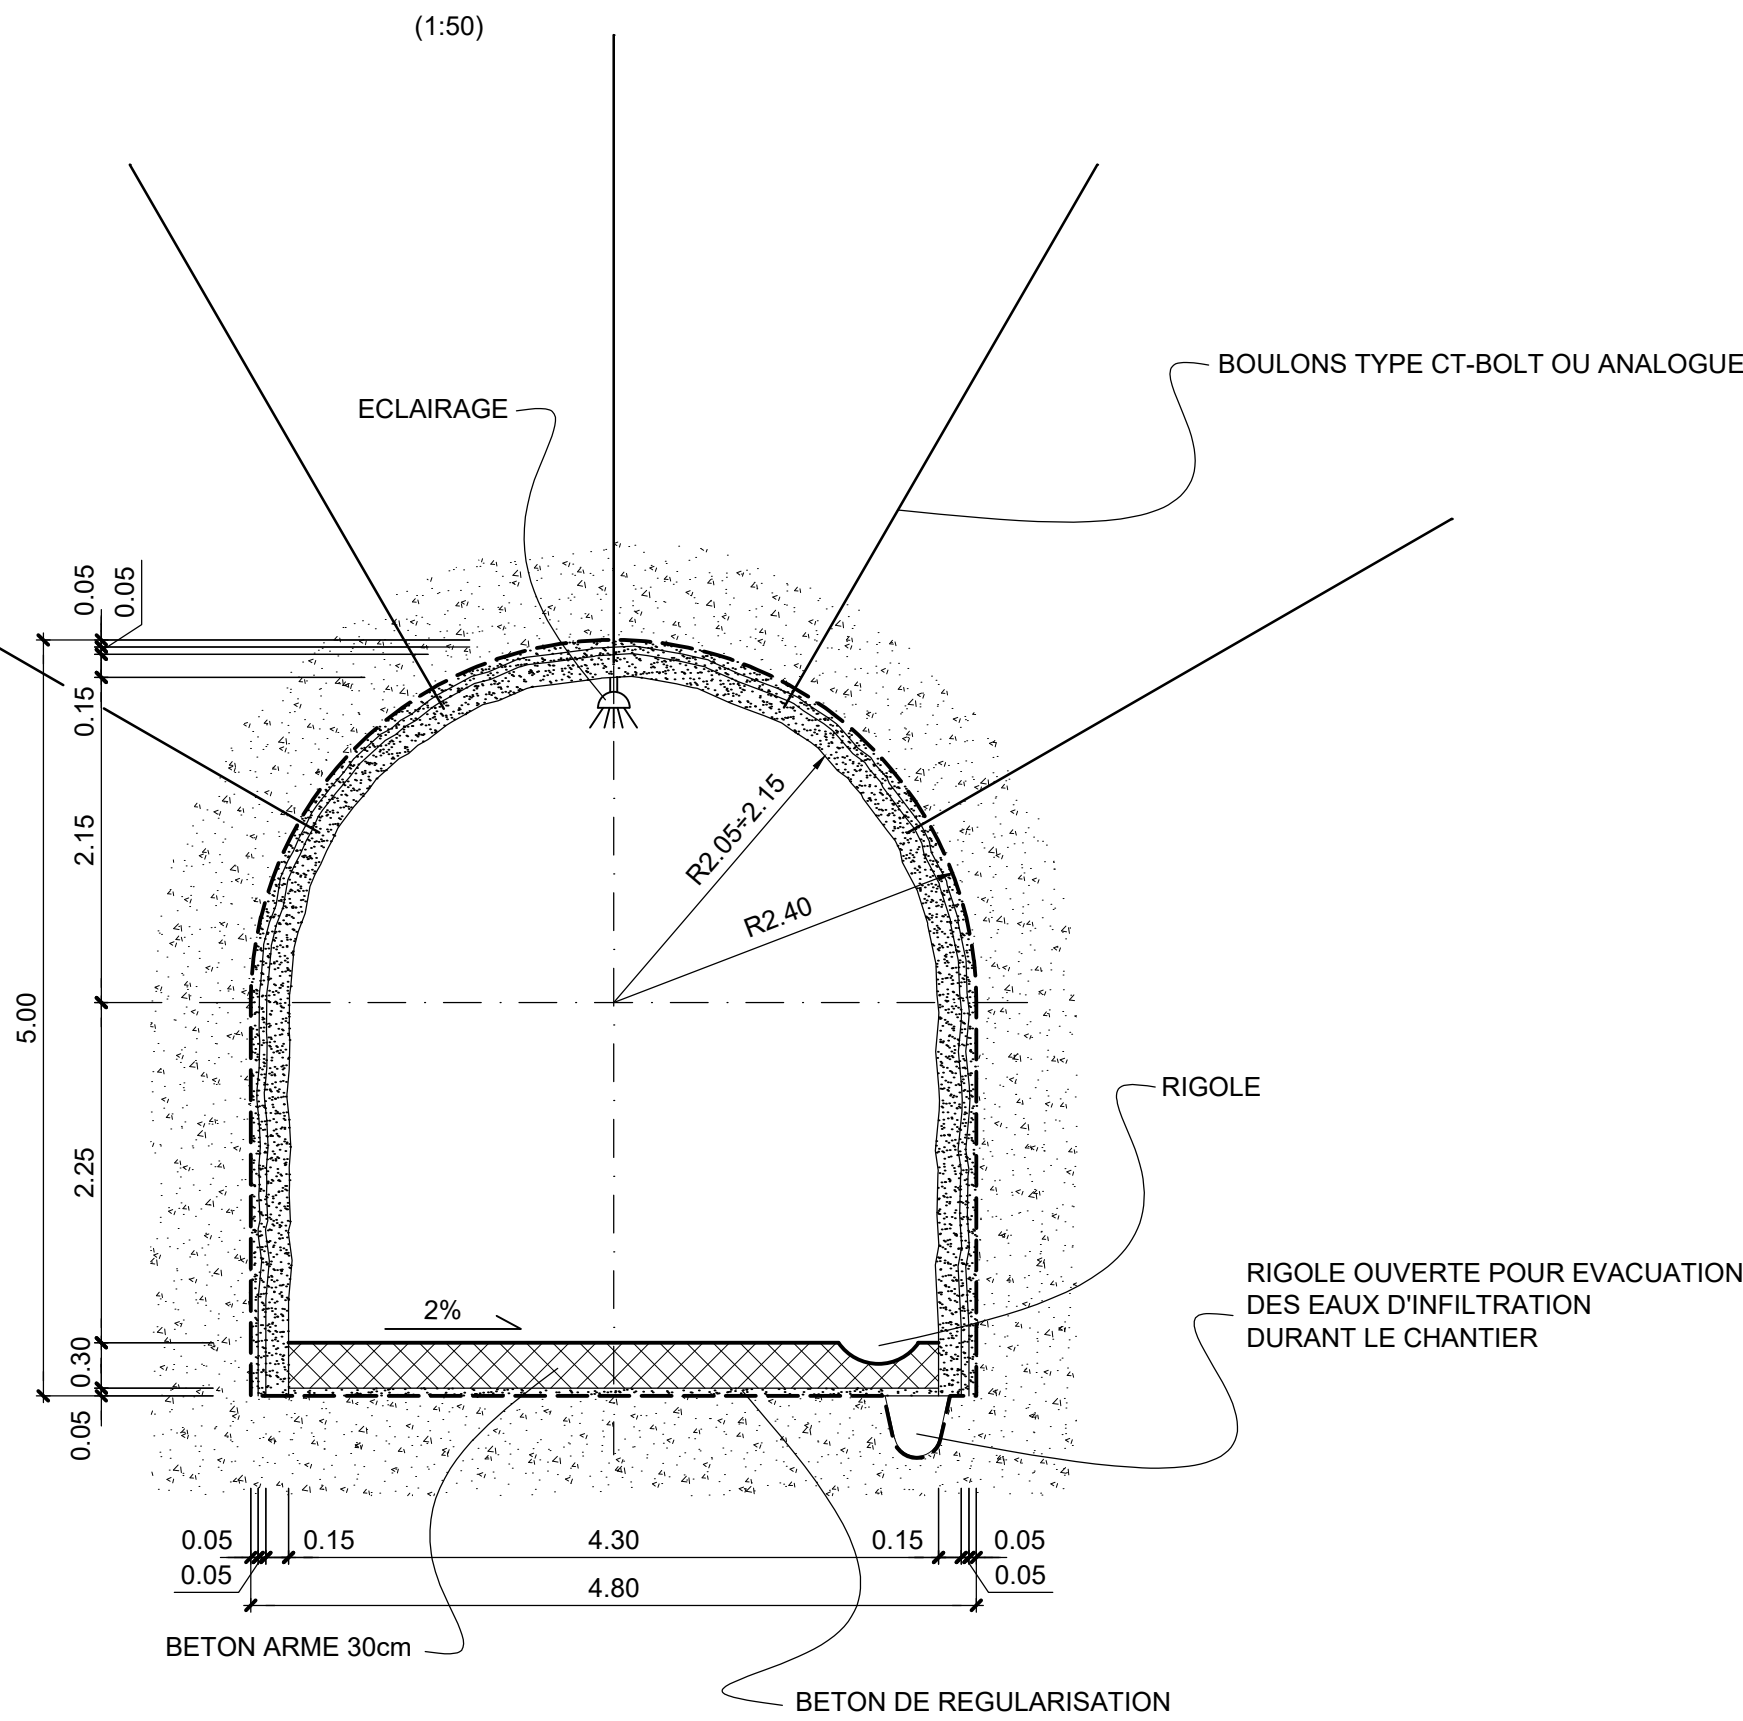


- SOUTÈNEMENT (PAR MÈTRE LINÉAIRE)**
- 5 cm BÉTON PROJETÉ AVEC FIBRES D'ACIER
 - 5/4 BOULONS CT BOLT OU ANALOGUE
 - 5 cm BÉTON PROJETÉ AVEC FIBRES
- REVÈTEMENT DÉFINITIF**
- 30 cm DE BÉTON ARME
 - 15 cm BÉTON PROJETÉ:
 - 12 cm AVEC FIBRES
 - 3 cm SANS FIBRES

ROCHE BROYÉE

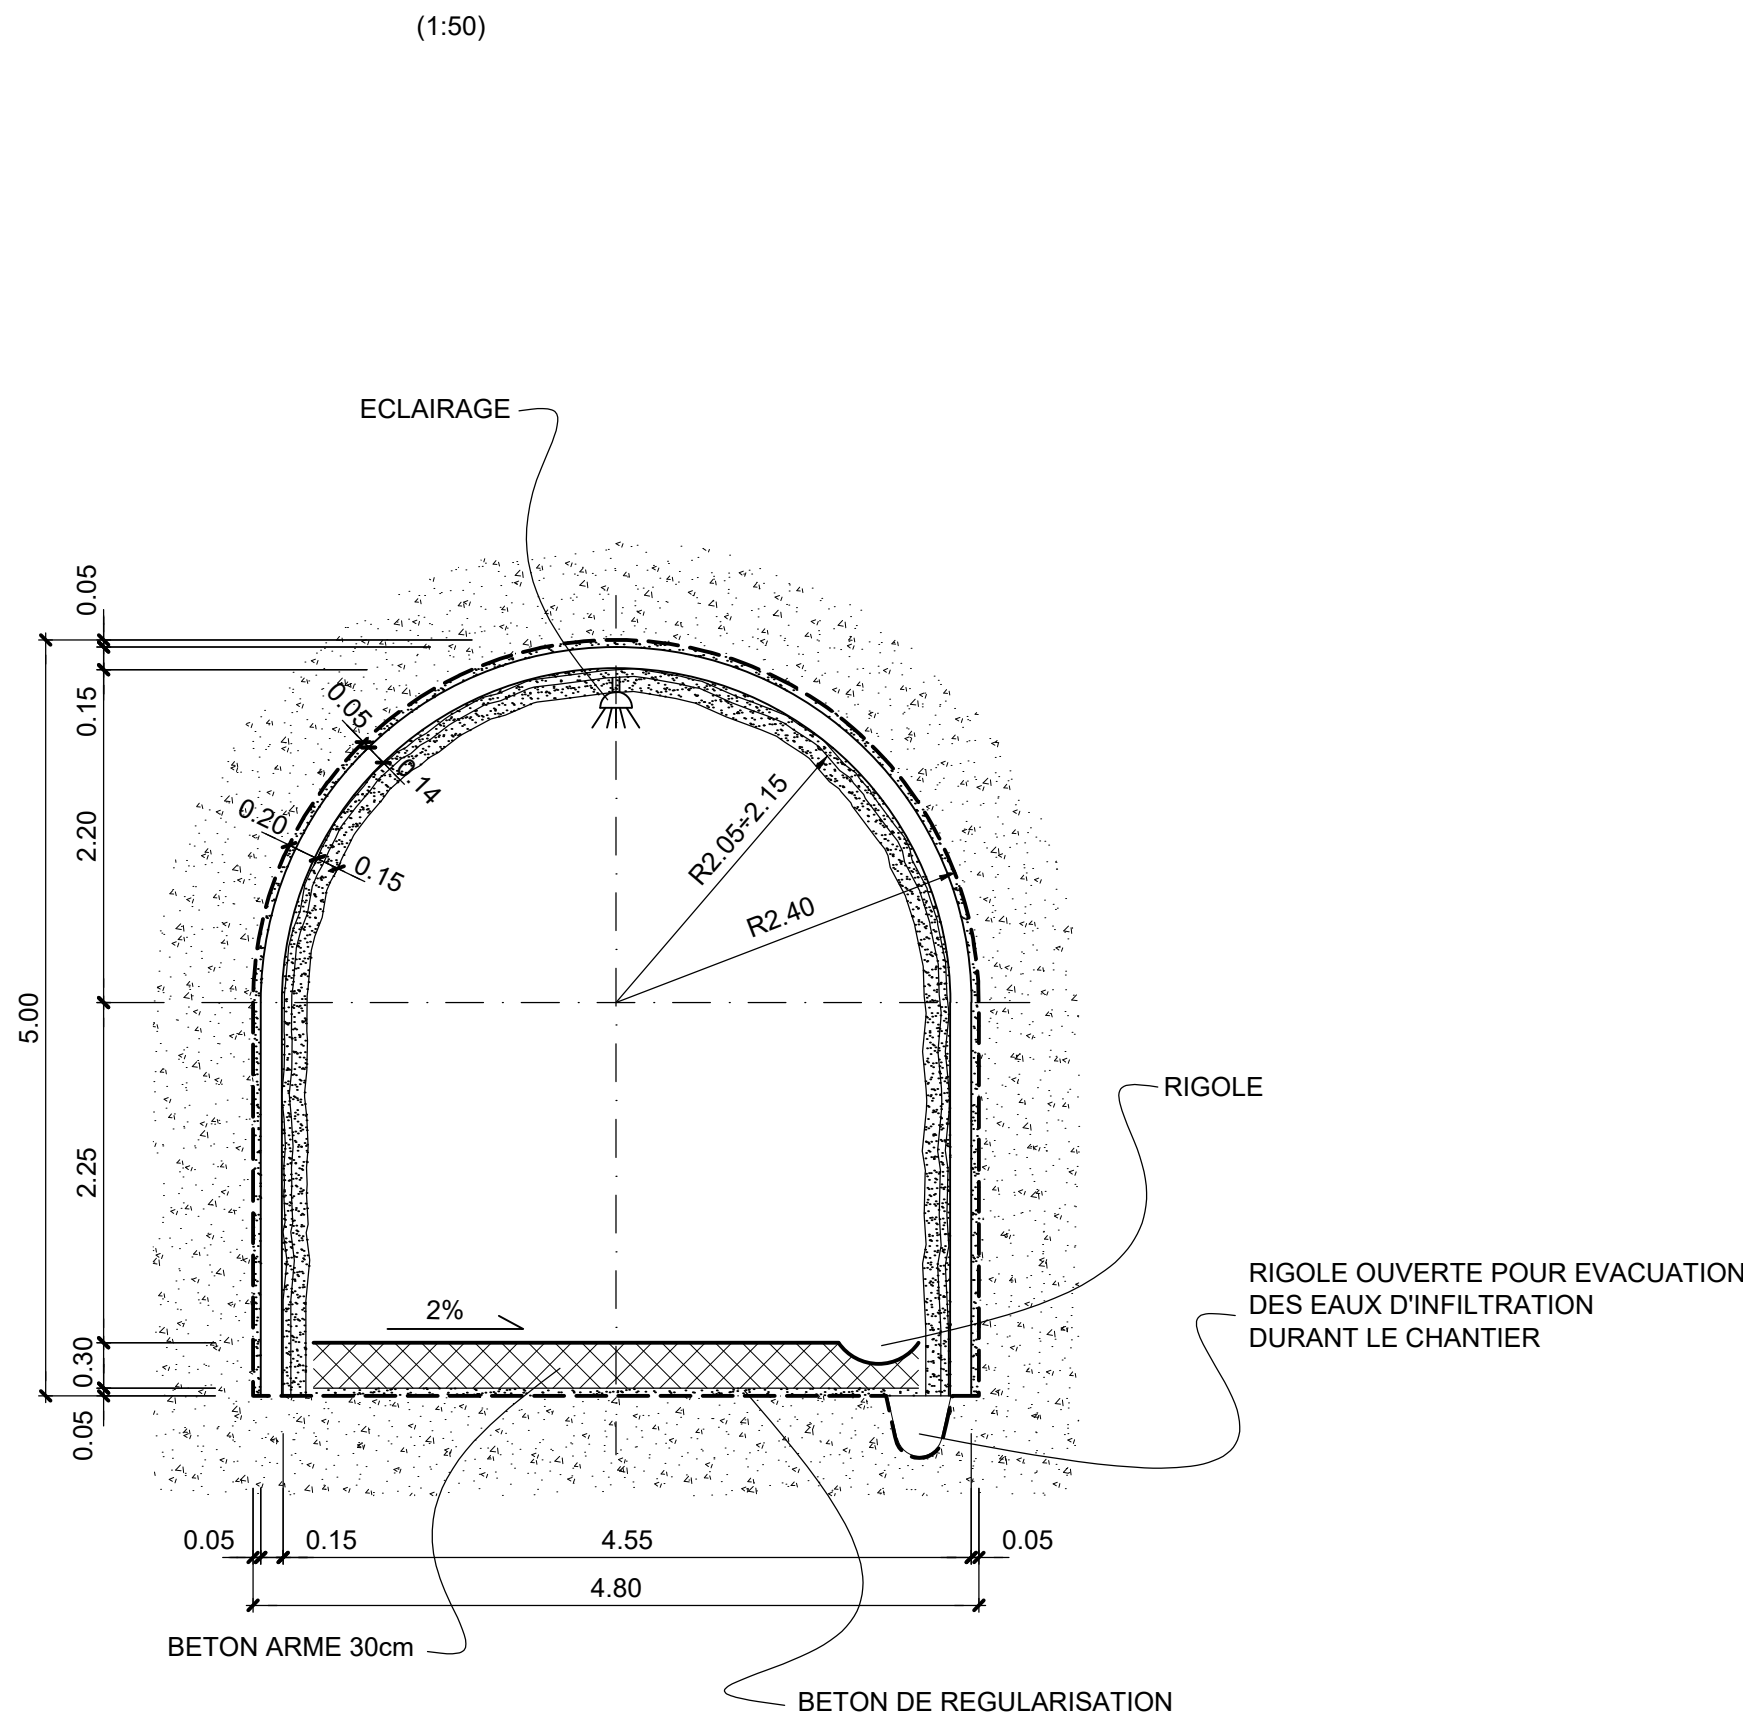

- SOUTÈNEMENT (PAR MÈTRE LINÉAIRE)**
- 5 cm BÉTON PROJETÉ AVEC FIBRES D'ACIER
 - CINTRE TYPE JB-4G-140/22 OU ANALOGUE
 - 15 cm BÉTON PROJETÉ AVEC FIBRES
- REVÈTEMENT DÉFINITIF**
- 30 cm DE BÉTON ARME
 - 15 cm BÉTON PROJETÉ:
 - 12 cm AVEC FIBRES
 - 3 cm SANS FIBRES

SITUATION

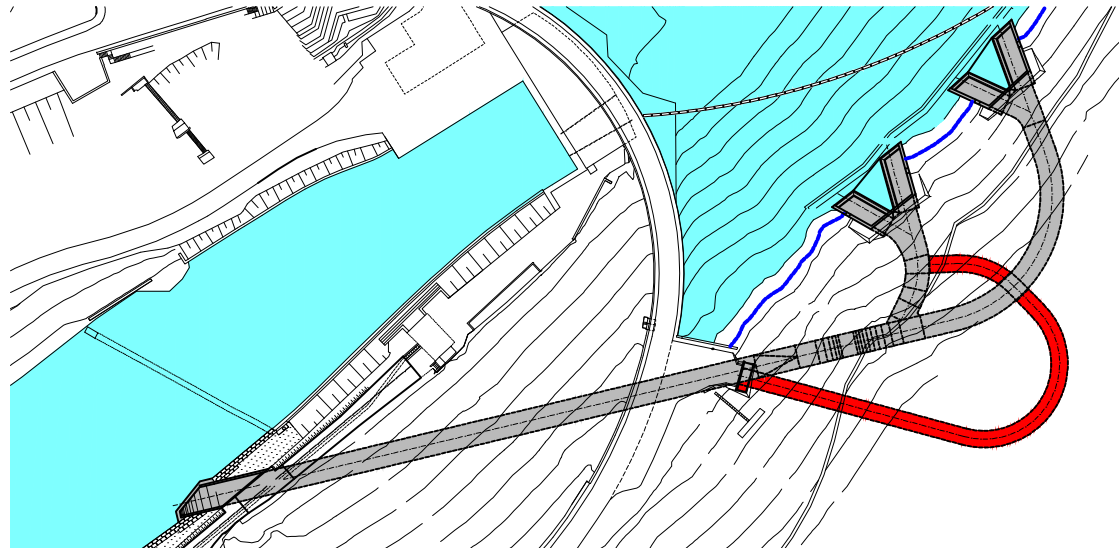


REFERENCE:

-TRONCON AMONT - SITUATION GÉNÉRALE, VOIR PLAN N.° 48930

NOTE:

- BÉTON DE REGULARISATION:
- BÉTON ARME: C30/37
- BOULONS: CT BOLT 168 KN
- LA RIGOLE SERA COMBLÉE À LA FIN DES TRAVAUX
- LE BOULONNAGE POURRA ÊTRE ADAPTÉ AU FUR ET À MESURE DU COMPORTEMENT DU ROCHER

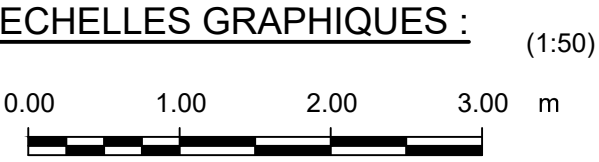

	LE GOUVERNEMENT DU GRAND-DUCHÉ DE LUXEMBOURG MINISTÈRE DE LA MOBILITÉ ET DES TRAVAUX PUBLICS ADMINISTRATION DES PONTS ET CHAUSSEES				
BARRAGE D'ESCH-SUR-SURE Evacuateur de crue complémentaire OA1158					
SOUSSION					
GALERIE D'ACCES TYPES DE SOUTÈNEMENT ET REVÈTEMENT DÉFINITIF					
Date:	Dess.	Verif.	Appr.	Description modification	C
					B
					A
07.07.2015	UP	Fel	BF	A1 (84 x 60)	7500.4-P-311-1
Date:	Dess.	Verif.	Appr.	Dim. :	Nom fichier
Echelle :	1:50	No. Lo :	7500.4-P-311-1	No.	48932

NOTE:

- LE TYPE DE SOUTÈNEMENT SERA DÉFINI EN FONCTION DE LA QUALITÉ DE LA ROCHE
- DISTRIBUTION ADMISE: 35% ROCHE BONNE / 50% ROCHE MOYENNE / 15% ROCHE BROYÉE
- LE BOULONNAGE POURRA ÊTRE ADAPTÉ AU FUR ET À MESURE DU COMPORTEMENT DU ROCHER