



PROFIL LONGITUDINAL

(1:200)

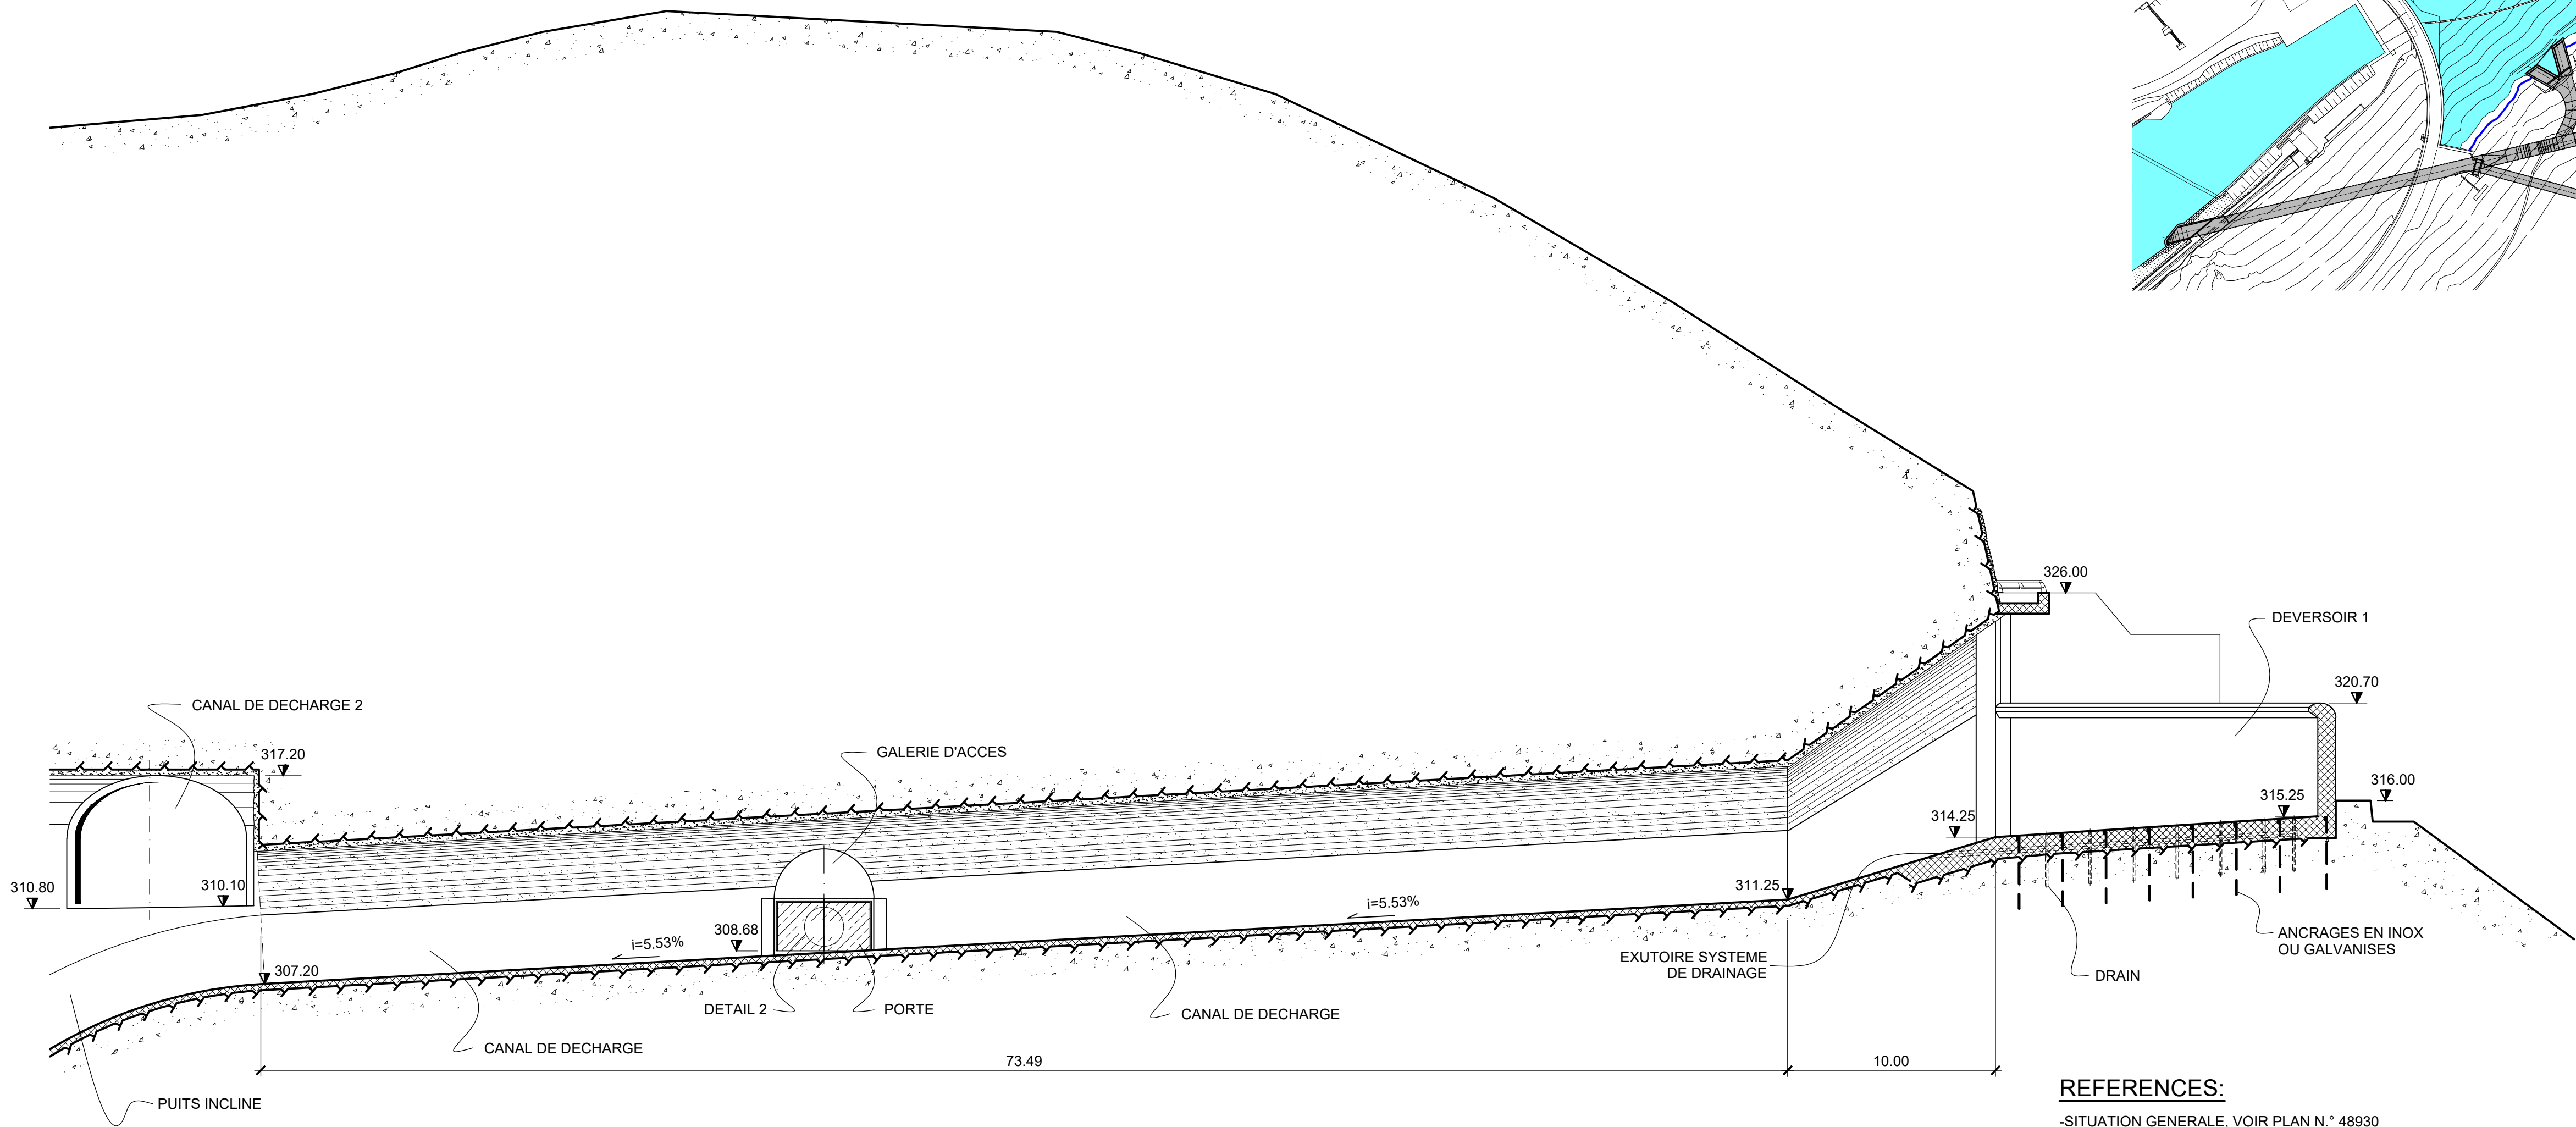

SITUATION

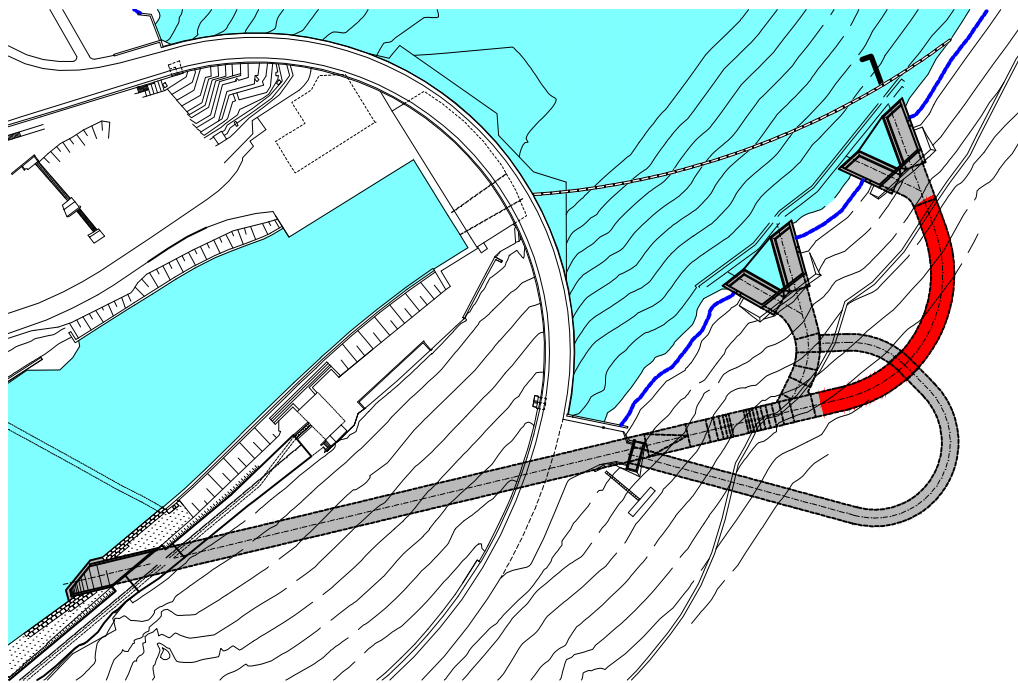

REFERENCES:


- SITUATION GENERALE, VOIR PLAN N.° 48930
- DEVERSOIR LABYRINTHE, VOIR PLAN N.° 48937 A 48940
- DEVERSOIR LABYRINTHE, DETAILS SOUTÈNEMENT DE L'ENTONNEMENT, VOIR PLAN N.° 48950
- CANAL DE DECHARGE, TYPES DE SOUTÈNEMENT ET REVÈTEMENT DÉFINITIF, VOIR PLAN N.° 48936

NOTE:

-LE DETAIL DU SOUTÈNEMENT DE L'ENTONNEMENT EST INDIQUE SUR LE PLAN 48950 ET PAS REPRIS ICI POUR DES RAISONS DE LISIBILITE

COUPE TYPE

(1:100)

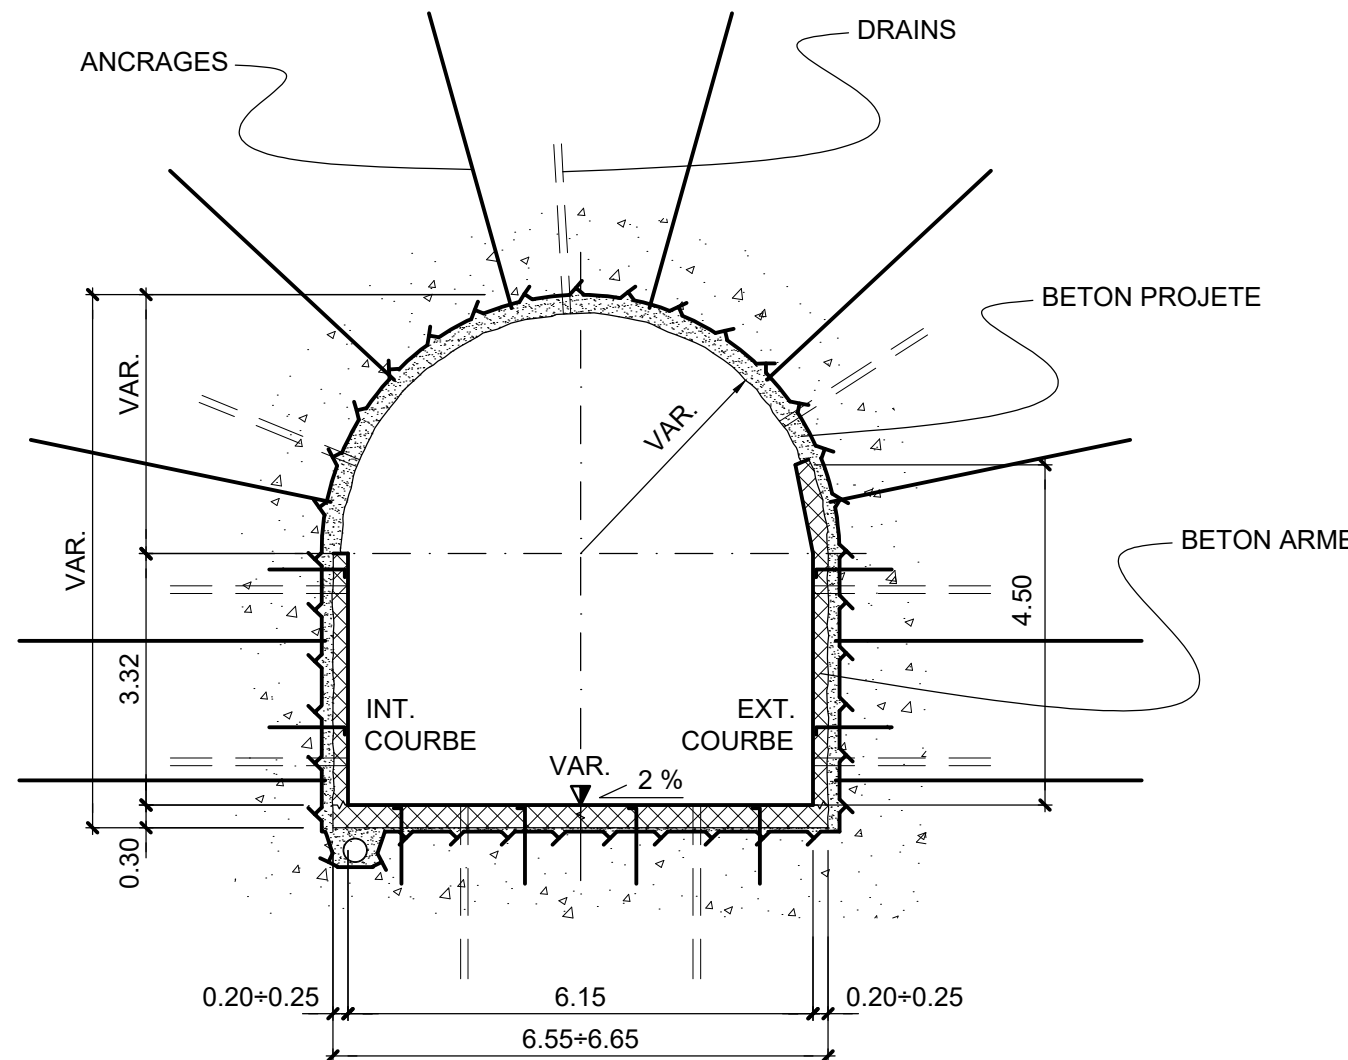

ECHELLES GRAPHIQUES :

(1:200)

0.00 4.00 8.00 12.00 m

(1:100)

0.00 2.00 4.00 6.00 m

		LE GOUVERNEMENT DU GRAND-DUCHÉ DE LUXEMBOURG MINISTÈRE DE LA MOBILITÉ ET DES TRAVAUX PUBLICS ADMINISTRATION DES PONTS ET CHAUSSEES			
BARRAGE D'ESCH-SUR-SURE Evacuateur de crue complémentaire OA1158					
SOUSSION					
CANAL DE DECHARGE 1 PROFIL LONGITUDINAL ET COUPE TYPE					
					C
23.05.18	MID	Fel	La	Modifications mineures	B
Date:	Dess.	Verif.	Appr.	Description modification	A
08.06.2015	UP	Fel	BF	A1 (84 x 60)	7500.4-P-312A
Date:	Dess.	Verif.	Appr.	Dim. :	Nom fichier
Echelle : 1:200, 1:100		No. Lo : 7500.4-P-312A		No. 48933	A