


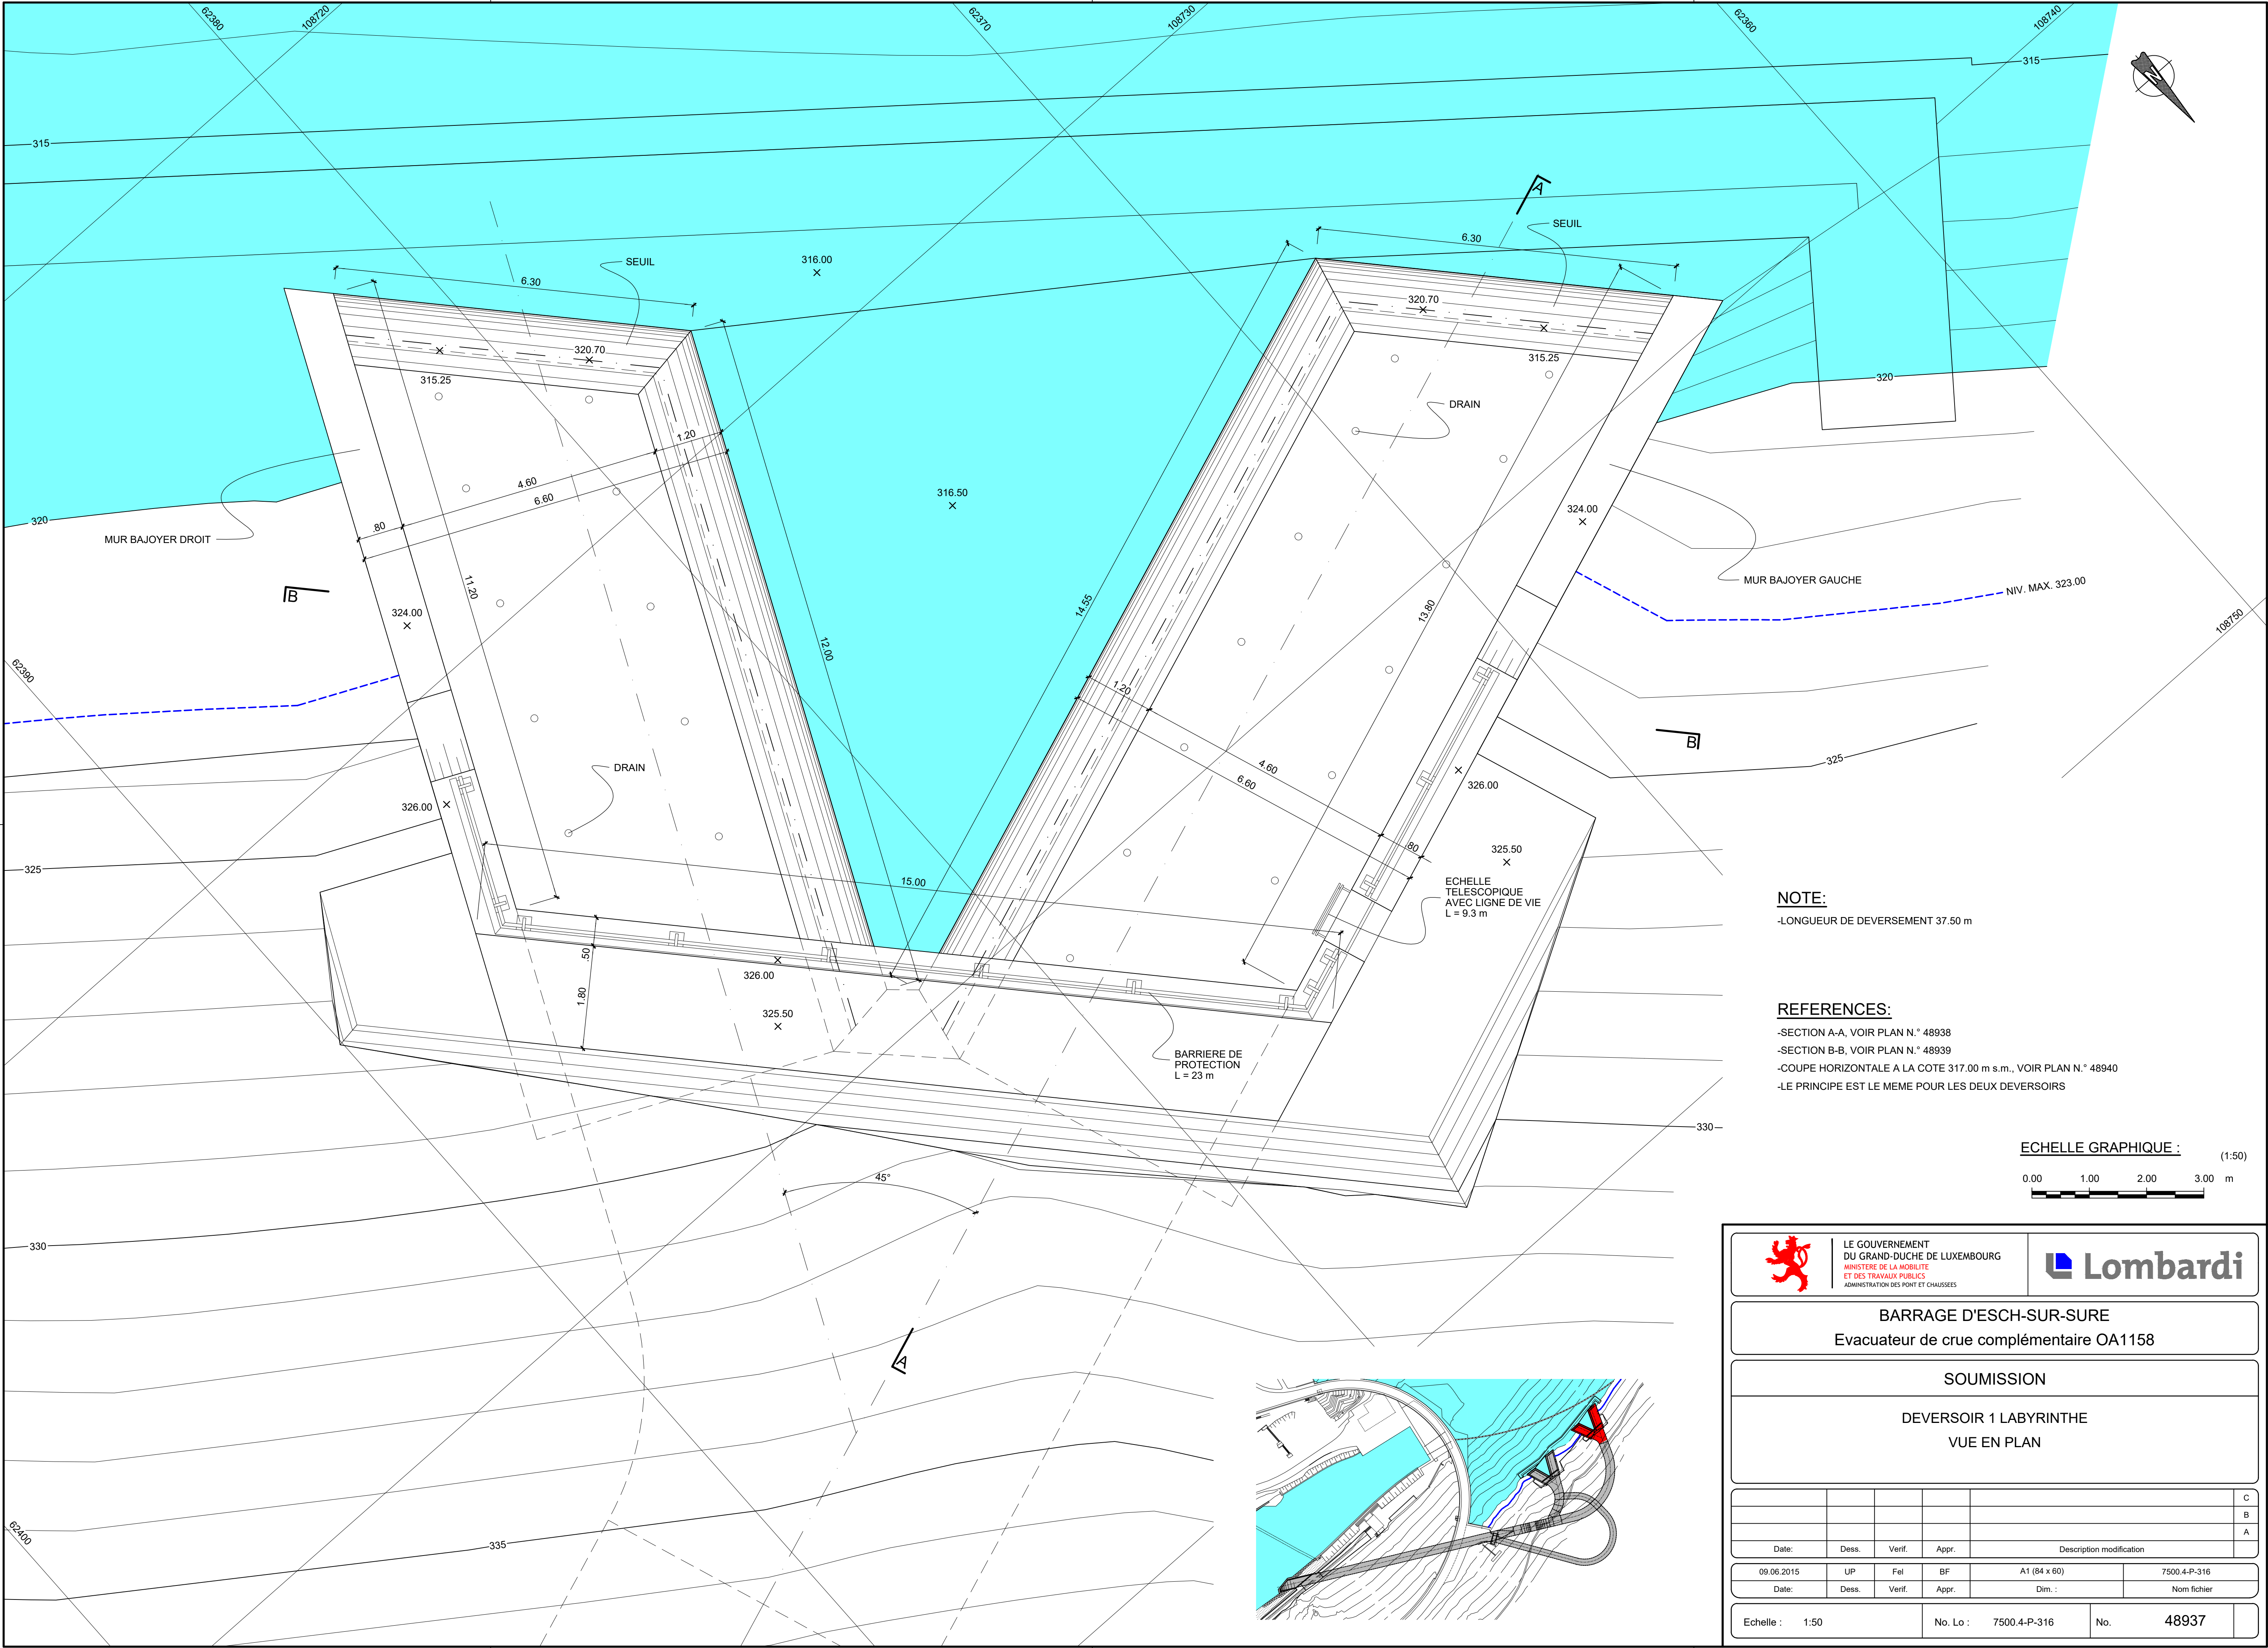

NOTE:

-LONGUEUR DE DEVERSEMENT 37.50 m

REFERENCES:

- SECTION A-A, VOIR PLAN N.° 48938
- SECTION B-B, VOIR PLAN N.° 48939
- COUPE HORIZONTALE A LA COTE 317.00 m s.m., VOIR PLAN N.° 48940
- LE PRINCIPE EST LE MEME POUR LES DEUX DEVERSOIRS

ECHELLE GRAPHIQUE :



		LE GOUVERNEMENT DU GRAND-DUCHÉ DE LUXEMBOURG MINISTÈRE DE LA MOBILITÉ ET DES TRAVAUX PUBLICS ADMINISTRATION DES PONTS ET CHAUSSEES			
BARRAGE D'ESCH-SUR-SURE Evacuateur de crue complémentaire OA1158					
SOUSSION					
DEVERSOIR 1 LABYRINTHE VUE EN PLAN					
Date:	Dess.	Verif.	Appr.	Description modification	C
					B
					A
09.06.2015	UP	Fel	BF	A1 (84 x 60)	7500.4-P-316
Date:	Dess.	Verif.	Appr.	Dim. :	Nom fichier
Echelle : 1:50		No. Lo : 7500.4-P-316		No. 48937	